Regulated Design Record


Project Address:

Project Title:

Consent No: DA18/0471.03 | Body Corporate Reg No:

Drawing Title: COVER SHEET | Drawing No: 5187-26-A000

Rev	Date dd.mm.yy	Description	DEP Full Name	Reg No
CC-A	02/09/26	FOR CC SUBMISSION	ERICA MARSHALL-EVANS	DEP 0001207

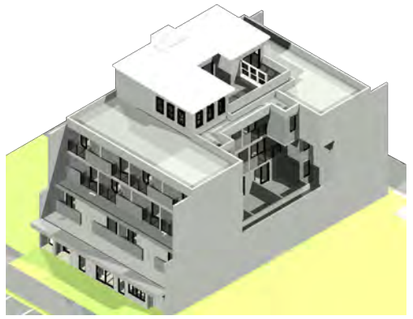

CERTIFICATE

DRAWING TITLE	DRAWING No.	SCALE	ISSUE	PAPER SIZE
COVER SHEET	5187-26-A000	NTS	CC-A	A3
SITE PLAN - 1:200	5187-26-A001	1:200	CC-A	A3
GROUND FLOOR PLAN - 1:200	5187-26-A100	1:200	CC-A	A3
LEVEL 1 PLAN - 1:200	5187-26-A101	1:200	CC-A	A3
LEVEL 2 PLAN - 1:200	5187-26-A102	1:200	CC-A	A3
LEVEL 3 PLAN - 1:200	5187-26-A103	1:200	CC-A	A3
LEVEL 4 PLAN - 1:200	5187-26-A104	1:200	CC-A	A3
ROOF PLAN - 1:200	5187-26-A105	1:200	CC-A	A3
CAFE LAYOUT	5187-26-A110	1:50	CC-A	A3
GROUND FLOOR - DISABLED TOILET LAYOUT	5187-26-A111	1:50	CC-A	A3
GROUND FLOOR REFLECTED CEILING PLAN	5187-26-A120	1:200	CC-A	A3
LEVEL 1 REFLECTED CEILING PLAN	5187-26-A121	1:200	CC-A	A3
LEVEL 2 REFLECTED CEILING PLAN	5187-26-A122	1:200	CC-A	A3
LEVEL 3 REFLECTED CEILING PLAN	5187-26-A123	1:200	CC-A	A3
LEVEL 4 REFLECTED CEILING PLAN	5187-26-A124	1:200	CC-A	A3
ELEVATIONS SHEET 1	5187-26-A200	1:200	CC-A	A3
ELEVATIONS SHEET 2	5187-26-A201	1:200	CC-A	A3
SECTIONS-SHEET 1	5187-26-A300	1:200	CC-A	A3
SECTIONS-SHEET 2	5187-26-A301	1:200	CC-A	A3
WALL SECTIONS	5187-26-A400	1:50	CC-A	A3
STAIR DETAILS	5187-26-A401	1:50	CC-A	A3
TYPICAL KITCHEN AND BATHROOM LAYOUT	5187-26-A402	1:50	CC-A	A3
TYPICAL BALCONY WATERPROOFING DETAILS	5187-26-A403	1:10	CC-A	A3
LETTER BOX AND EXTERNAL DETAILS	5187-26-A404	1:25	CC-A	A3
CAFE KITCHEN DETAILS & NOTES	5187-26-A405	NTS	CC-A	A3
WINDOW AND DOOR SCHEDULE	5187-26-A500	1:200	CC-A	A3
MATERIALS AND FINISHES SCHEDULE	5187-26-A501	1:200	CC-A	A3

CONSTRUCTION CERTIFICATE NOTES:

GENERAL

1.ALL WORK SHALL COMPLY WITH THE NCC (BCA VOL 1 2025 EDITION), CONDITIONS OF CONSENT, AND THE RELEVANT AUSTRALIAN STANDARDS AS LISTED BELOW.
2. FOR CONSTRUCTION CERTIFICATE ONLY NOT FOR CONSTRUCTION. ALL DIMENSIONS SHALL BE VERIFIED ON SITE PRIOR TO COMMENCEMENT OF WORK. DO NOT SCALE DRAWINGS.
3.BYDA BEFORE YOU DIG FOR ANY UNDERGROUND SERVICES.WWW.BYDA.COM.AU
4. ANY DISCREPANCIES BETWEEN DRAWINGS, SITE CONDITIONS, OR SPECIFICATIONS SHALL BE REFERRED TO THE ARCHITECT BEFORE PROCEEDING.
5. DRAWINGS ARE TO BE READ IN CONJUNCTION WITH THE ARCHITECTURAL SPECIFICATION AND ALL CONSULTANT DRAWINGS AND SPECIFICATIONS, INCLUDING STRUCTURAL, CIVIL, HYDRAULIC, MECHANICAL, ELECTRICAL, FIRE, LANDSCAPE AND SECTION J DOCUMENTATION.
6. THE BUILDER SHALL CARRY OUT ALL WORK IN ACCORDANCE WITH: NCC (BCA VOL 1 2025), CONDITIONS OF DEVELOPMENT CONSENT, WHS REGULATION (NSW), AND RELEVANT AUSTRALIAN STANDARDS.
7. PROVIDE ADEQUATE PROTECTION TO EXISTING STRUCTURES, PUBLIC SPACES AND SERVICES DURING CONSTRUCTION.
8. THE BUILDER SHALL COORDINATE ALL TRADES AND ENSURE PENETRATIONS, SET-OUTS AND SERVICE ROUTES ARE ACCURATELY LOCATED.
9. ALL DIMENSIONS TO BE CHECKED ON SITE AND SETOUT BY A SURVEYOR PRIOR TO COMMENCEMENT OF CONSTRUCTION.

2. BUILDING CLASSIFICATION & DESIGN CRITERIA:

10.BUILDING CLASSIFICATION: CLASS 3 AND CLASS 7A
11. TYPE OF CONSTRUCTION: TYPE A AS STATED IN BCA REPORT.
12. SITE WORKS AND STORMWATER TO COMPLY WITH AS 3500 SERIES AND COUNCIL DCP REQUIREMENTS.

3. STRUCTURAL & MATERIALS:

13.ALL STRUCTURAL COMPONENTS TO BE CONSTRUCTED IN ACCORDANCE WITH THE STRUCTURAL ENGINEERS DRAWINGS AND SPECIFICATIONS.

4. FIRE SAFETY & EGRESS

14. FIRE-RESISTING CONSTRUCTION TO COMPLY WITH NCC SECTIONS C1 TO C3 AND SPECIFICATION C1.1.
15. MINIMUM FIRE RESISTANCE LEVELS (FRLS) TO BE ACHIEVED AS PER BCA TABLE 3 OF SPEC C1.1.
16. FIRE-RATED SYSTEMS (WALLS, FLOORS, CEILINGS, PENETRATIONS) TO BE INSTALLED TO MANUFACTURER'S TESTED SYSTEMS (AS 1530.4 & AS 4072.1).

5. ACCESS & INCLUSION

17. COMPLY WITH NCC SECTION D4 AND SPEC D3.6, AS 1428.1 (2021), AS 1428.4.1, AND AS 1735.12 WHERE LIFTS ARE PROVIDED.
18. PROVIDE CONTINUOUS ACCESSIBLE PATHS FROM THE STREET AND ACCESSIBLE PARKING TO ENTRIES AND INTERNAL FACILITIES.
19. DOORS AND LIFTS OFF HINGES TO ALL TOILETS.
20. DISABLE TOILET TO COMPLY WITH AS 1428.1-2009

6. SERVICES & ENERGY EFFICIENCY

21.REFER TO FIRE ENGINEERS DRAWINGS AND SPECIFICATIONS
22.REFER TO ELECTRICAL ENGINEERS DRAWINGS AND SPECIFICATIONS
23.REFER TO MECHANICAL ENGINEERS DRAWINGS AND SPECIFICATIONS
24. ACOUSTIC TREATEMENS TO COMPLY WITH THE ACOUSTIC CONSULTANT'S RECOMMENDATIONS.

7. ENVIRONMENTAL & ACOUSTIC

25. EXTERNAL AIR CONDITIONING UNITS TO HAVE AN ACOUSTIC ENCLOSURE ON A UNIT WITH A NOISE LEVEL OF 70 DBA WITH A 25 DBA REDUCTION, RELEVANT NOISE GOALS AT THE RELEVANT PROPERTY BOUNDARIES WILL BE ACHIEVED.
26. BRICK WALLS MUST COMPLY WITH MASONRY AUSTRALIAN STANDARDS FOR BRICK TIES AND MASONRY STRUCTURES AS2699.1:2020 AND AS3700.
27. ALL EXTERNAL GLAZED DOORS INCLUDING FRAMES AND ASSOCIATED COMPONENTS SHALL COMPLY WITH AS2047.
28. ALL WATERPROOFING MEMBRANES TO COMPLY WITH THE REQUIREMENTS OF AS 3740 WATERPROOFING OF WET AREAS WITHIN RESIDENTIAL BUILDINGS INSTALLATION AS 4858 WATERPROOFING OF WET AREAS WITHIN RESIDENTIAL BUILDINGS MATERIALSAS 4654.1 WATERPROOFING OF EXTERNAL ABOVE GROUND AREAS MATERIALS AS 4654.2 WATERPROOFING OF EXTERNAL ABOVE GROUND AREAS - INSTALLATION
29. DAMP PROOF COURSE DCP MEMBRANE TO PROVIDE UNDER SUBFLOOR SLAB AND WALLS TO COMPLY WITH NCC FID6 AND FID7.
30. WHERE POSSIBLE, EXTERNAL SURFACES THAT ARE ACCESSIBLE TO THE PUBLIC ARE TO INCORPORATE AN APPROPRIATE ANTI-GRAFFITI RESISTANT COATING, INCLUDING SIGNAGE, STREET FURNITURE, PLANTER BOXES AND OTHER EXPOSED EXTERNAL SURFACES. THE COATING IS TO BE COMPATIBLE WITH THE NOMINATED SURFACE FINISH AND APPLIED IN ACCORDANCE WITH THE MANUFACTURER'S RECOMMENDATIONS.
31.OUTDOOR LIGHTING TO BE INSTALLED IN ACCORDANCE WITH AS1158.0 AND AS/NZS 4282-2023 CONTROL OF OBSTRUCTURE EFFECTS OF OUTDOOR LIGHTING.

DOOR LOCKS & HARDWARE

32.DOOR LOCKS AND WINDOW LOCKS TO BE INSTALLED IN ACCORDANCE WITH AS4145.2-2008 LOCKSETS AND HARDWARE FOR DOORS AND WINDOWS.
33. ALL DOOR LOCKSETS, LATCHES AND ASSOCIATED HARDWARE TO COMPLY WITH THE NCC 2022 AND RELEVANT AUSTRALIAN STANDARDS.
34. DOORS IN REQUIRED EXITS, FORMING PART OF A REQUIRED EXIT OR IN A PATH OF TRAVEL TO A REQUIRED EXIT SHALL BE FITTED WITH LATCHING DEVICES COMPLYING WITH NCC 2022 D3D26.
35. LATCHING DEVICES SHALL BE READILY OPERABLE FROM THE EGRESS SIDE WITHOUT A KEY AND OPERATED BY A SINGLE DOWNWARD ACTION OR PUSHING ACTION, AS REQUIRED BY NCC D3D26.
36. DOOR HARDWARE TO ACCESSIBLE DOORS SHALL COMPLY WITH AS 1428.1:2021.
37. WHERE FIRE DOORS ARE REQUIRED, DOOR LEAF, FRAME, CLOSER, LOCKSET AND ASSOCIATED HARDWARE SHALL BE COMPATIBLE WITH THE REQUIRED FIRE-RESISTANCE LEVEL AND TESTED/APPROVED AS PART OF THE FIRE DOOR ASSEMBLY.
38. ALL LOCKSETS AND HARDWARE SHALL BE SELECTED AND INSTALLED IN ACCORDANCE WITH THE MANUFACTURER'S REQUIREMENTS AND RELEVANT AUSTRALIAN STANDARDS.

FOR CC SUBMISSION

No.	Date	Issue Notes
CC-A	02-Sep-26	FOR CC SUBMISSION

Consultant / Notes:
Survey Prepared by Total Surveying Solutions
ARTARMON.CAMDEN, MANLYVALE

COPYRIGHT
THIS DRAWING IS THE PROPERTY OF LYLE MARSHALL AND PARTNERS P/L AND MAY ONL BE USED FOR THE PURPOSE FOR WHICH IT WAS COMMISSIONED & IN ACCORDANCE WIT THE TERMS OF ENGAGEMENT FOR THAT COMMISSION. UNAUTHORISED USE OF THIS DRAWING IS PROHIBITED.


Design By		Job No.	5187-26
Drawn By	EMMC	Scale	NTS
Reviewed By		Date	02-Sep-26
Passed By		Date of Issue	
Sheet No.	A000	Issue	CC-A
of			

TEST PROJECT ONLY

Regulated Design Record

Project Address:			
Project Title:			
Consent No:	DA18/0471.03	Body Corporate Reg No:	
Drawing Title:	SITE PLAN - 1:200	Drawing No:	5187-26-A001

Rev	Date dd.mm.yy	Description	DEP Full Name	Reg No
CC-A	02/09/26	FOR CC SUBMISSION	ERICA MARSHALL-EVANS	DEP 0001207

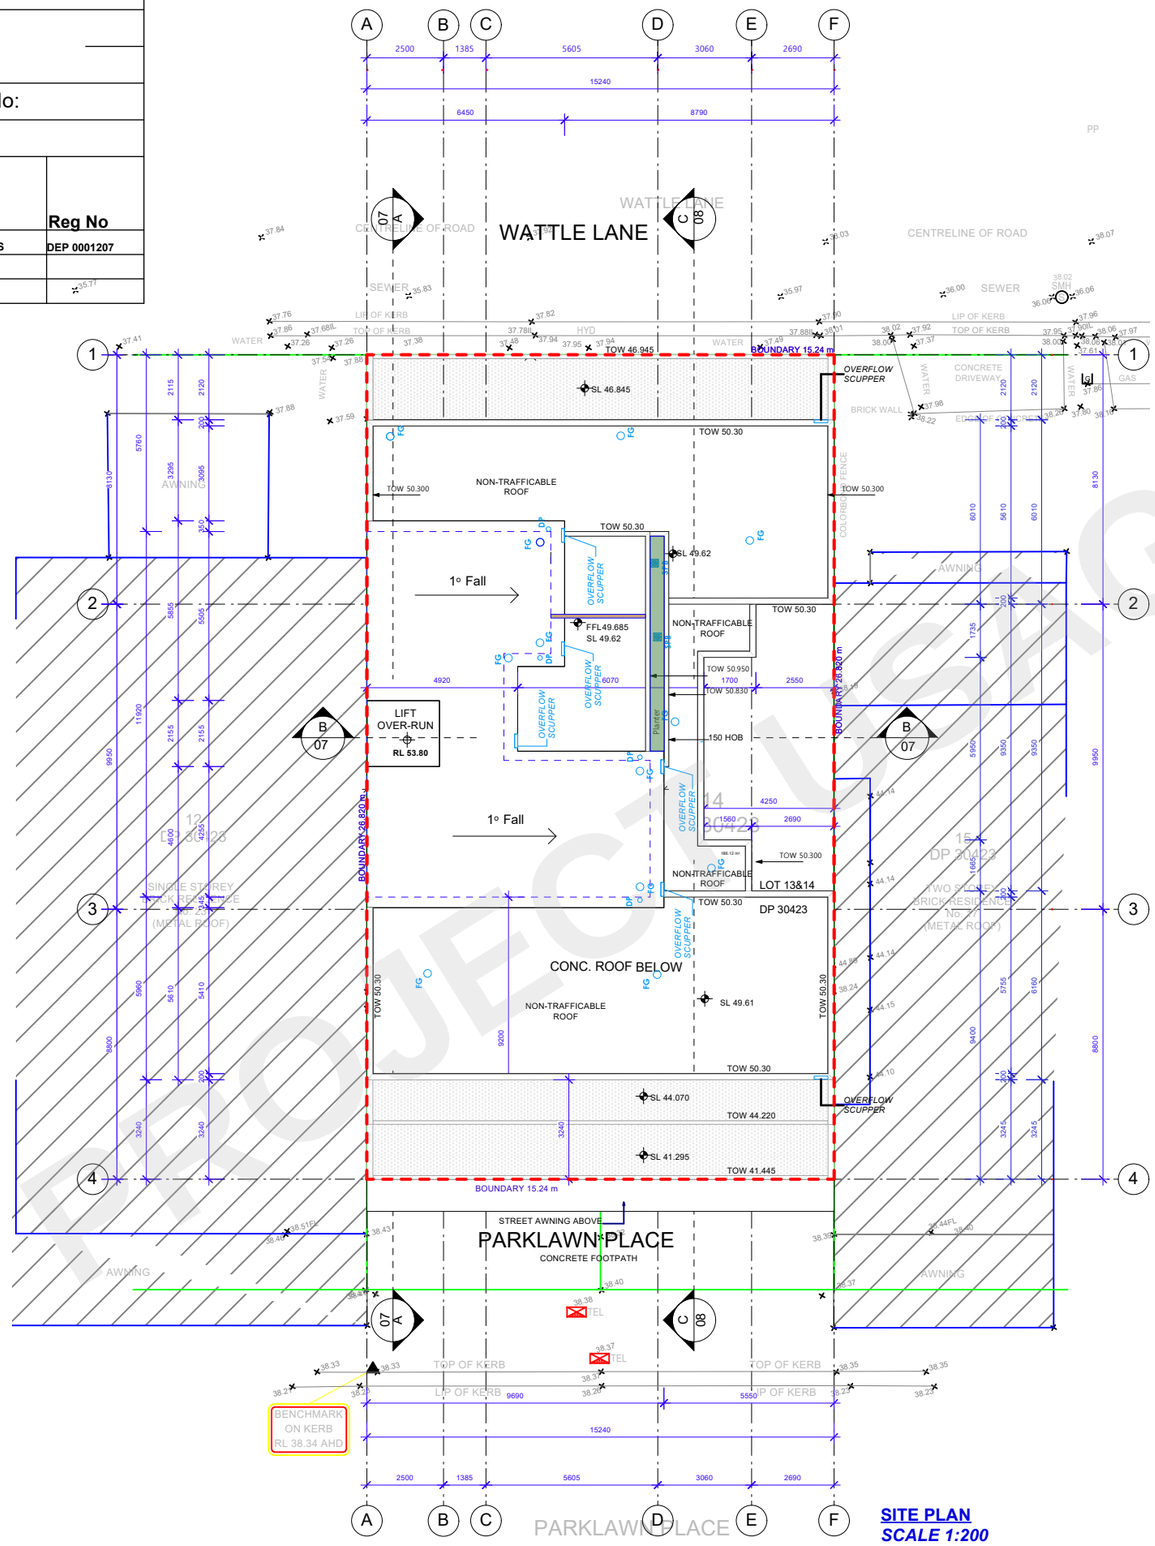

SITE PLAN
SCALE 1:200

CONSTRUCTION CERTIFICATE NOTES:

GENERAL

1.ALL WORK SHALL COMPLY WITH THE NCC (BCA VOL 1 2025 EDITION), CONDITIONS OF CONSENT, AND THE RELEVANT AUSTRALIAN STANDARDS AS LISTED BELOW.
2. FOR CONSTRUCTION CERTIFICATE ONLY NOT FOR CONSTRUCTION. ALL DIMENSIONS SHALL BE VERIFIED ON SITE PRIOR TO COMMENCEMENT OF WORK. DO NOT SCALE DRAWINGS.
3.BYDA BEFORE YOU DIG FOR ANY UNDERGROUND SERVICES.WWW.BYDA.COM.AU
4. ANY DISCREPANCIES BETWEEN DRAWINGS, SITE CONDITIONS, OR SPECIFICATIONS SHALL BE REFERRED TO THE ARCHITECT BEFORE PROCEEDING.
5. DRAWINGS ARE TO BE READ IN CONJUNCTION WITH THE ARCHITECTURAL SPECIFICATION AND ALL CONSULTANT DRAWINGS AND SPECIFICATIONS, INCLUDING STRUCTURAL, CIVIL, HYDRAULIC, MECHANICAL, ELECTRICAL, FIRE, LANDSCAPE AND SECTION J DOCUMENTATION.
6. THE BUILDER SHALL CARRY OUT ALL WORK IN ACCORDANCE WITH: NCC (BCA VOL 1 2025), CONDITIONS OF DEVELOPMENT CONSENT, WHS REGULATION (NSW), AND RELEVANT AUSTRALIAN STANDARDS.
7. PROVIDE ADEQUATE PROTECTION TO EXISTING STRUCTURES, PUBLIC SPACES AND SERVICES DURING CONSTRUCTION.
8. THE BUILDER SHALL COORDINATE ALL TRADES AND ENSURE PENETRATIONS, SET-OUTS AND SERVICE ROUTES ARE ACCURATELY LOCATED.
9. ALL DIMENSIONS TO BE CHECKED ON SITE AND SETOUT BY A SURVEYOR PRIOR TO COMMENCEMENT OF CONSTRUCTION.

0 2 3 5 m

LEGEND

BOUNDARY LINE

TEST PROJECT
STORAGE ONLY

No.	Date	Issue Notes
CC-A	02-Sep-26	FOR CC SUBMISSION

Consultant / Notes:
Survey Prepared by Total Surveying Solutions
ARTARMON.CAMDEN, MANLYVALE

COPYRIGHT
THIS DRAWING IS THE PROPERTY OF LYLE MARSHALL AND PARTNERS P/L AND MAY ONLY BE USED FOR THE PURPOSE FOR WHICH IT WAS COMMISSIONED & IN ACCORDANCE WITH THE TERMS OF ENGAGEMENT FOR THAT COMMISSION. UNAUTHORISED USE OF THIS DRAWING IS PROHIBITED.


FOR CC SUBMISSION

Design By	Job No. 5187-26		
Drawn By EMMC	Scale 1:200		
Reviewed By	Date 02-Sep-26	Sheet No. A001 of	Issue CC-A
Passed By	Date of Issue		

Regulated Design Record

Project Address:			
Project Title:			
Consent No:	DA18/0471.03	Body Corporate Reg No:	
Drawing Title:	GROUND FLOOR PLAN - 1:200	Drawing No:	5187-26-A100

Rev	Date dd.mm.yy	Description	DEP Full Name	Reg No
CC-A	02/09/26	FOR CC SUBMISSION	ERICA MARSHALL-EVANS	DEP 0001207

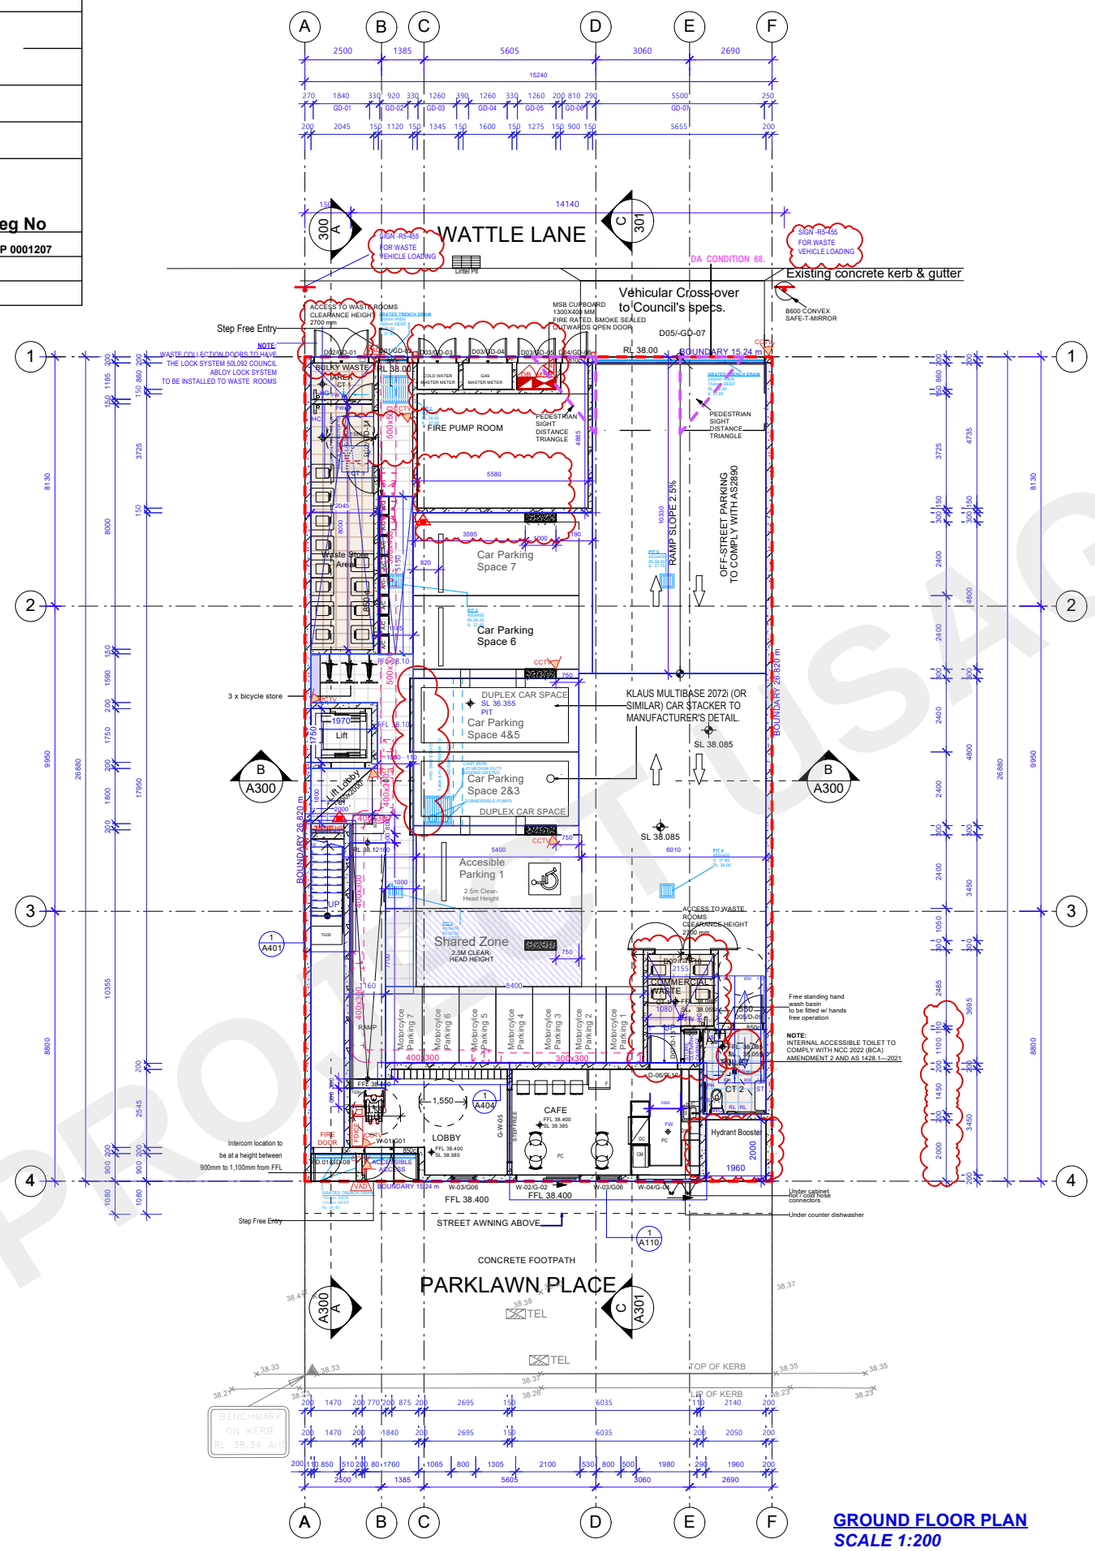

GROUND FLOOR PLAN
SCALE 1:200

LEGEND

CT 1 TILED FLOOR
CT2 NON SLIP TILE
BS BASIN
PH TOILET PAPER HOLDER
GR GRABRAIL
FW FLOOR WASTE
HC HOSE COCK/ WATER
SH SHOWER
WC WATER CLOSET
ST SHOWER SEAT
BOUNDARY LINE
GRATED DRAIN
PIT
DP DOWNPIPE
VD VERTICAL DROP

LEGEND

FDICE — FIRE DETECTION CONTROL AND INDICATING EQUIPMENT (FDCIE) CONFORMING TO AS 1670.1:2018 AND AS 7240.2:2018

VAD — VISUAL ALARM DEVICE (VAD) IN ACCORDANCE WITH AS 1670.1:2018 AND AS ISO 7240.23:2014

MANUAL CALL POINT (MCP) COMPLYING WITH AS 1670.1:2018 AND AS ISO 7240.11:2018

FHR — FIRE HOSE REEL

2.5 KG ABE POWDER TYPE FIRE EXTINGUISHER TO COMPLY WITH AS 2444-2001. MIN. RATING 2A:40B:E OR EQUIVALENT

5 KG CARBON DIOXIDE (C02) TYPE FIRE EXTINGUISHER TO CONFORM WITH AS 2444-2001

DB — DISTRIBUTION BOARD

MSB — MAIN SWITCH BOARD

CCTV — CCTV CAMERA

INTERCOM

NOTES:

ACCESS PATHWAYS TO ACHIEVE 2700 mm CLEARANCE HEIGHT TO ALL THE WASTE ROOMS.

FIRST FLOOR SLAB: FRL 120/120/120

OTHER FLOORS : 90/90/90
REFER TO STRUCTURAL ENG'S DETAILS

WALL TYPES

115 mm INTERNAL STEEL STUD WALL
13 mm PLASTERBOARD
90 mm STEEL STUD
13 mm PLASTERBOARD

CONCRETE COLUMN

270 mm CAVITY BRICK WALL
FRL 90/90/90
110 mm BRICK
90 50 AIR GAP
110 mm BRICK

FRL 240/240/240
Ritek XL - 200A EXTERNAL CONCRETE WALL

FRL 240/240/240
Ritek XL - 165A INTERNAL CONCRETE WALL

FRL 240/240/240
Ritek XL - 150A INTERNAL CONCRETE WALL

FRL 240/240/240
Ritek XL - 165-C INTERTENANCY WALLS
13 mm PLASTERBOARD
165 mm Ritek XL WALL
13 mm PLASTERBOARD
ALLOW 190mm

FRL 240/240/240
Ritek XL - 150-C DISCONTINUOUS WALLS
13 mm PLASTERBOARD
64 mm STEEL STUD WITH GLASS FIBRE INSULATION
20 mm GAP
150 mm XL WALL
13 mm PLASTERBOARD

NOTE: CONDITION 33
ACCESS TO WASTE ROOMS CLEARANCE HEIGHT 2700 mm

0 2 3 5 m

CONSTRUCTION CERTIFICATE NOTES:

GENERAL
1.ALL WORK SHALL COMPLY WITH THE NCC (BCA VOL 1 2025 EDITION), CONDITIONS OF CONSENT, AND THE RELEVANT AUSTRALIAN STANDARDS AS LISTED BELOW.
2. FOR CONSTRUCTION CERTIFICATE ONLY NOT FOR CONSTRUCTION. ALL DIMENSIONS SHALL BE VERIFIED ON SITE PRIOR TO COMMENCEMENT OF WORK. DO NOT SCALE DRAWINGS.
3.BYDA BEFORE YOU DIG FOR ANY UNDERGROUND SERVICES.WWW.BYDA.COM.AU
4. ANY DISCREPANCIES BETWEEN DRAWINGS, SITE CONDITIONS, OR SPECIFICATIONS SHALL BE REFERRED TO THE ARCHITECT BEFORE PROCEEDING.
5. DRAWINGS ARE TO BE READ IN CONJUNCTION WITH THE ARCHITECTURAL SPECIFICATION AND ALL CONSULTANT DRAWINGS AND SPECIFICATIONS, INCLUDING STRUCTURAL, CIVIL, HYDRAULIC, MECHANICAL, ELECTRICAL, FIRE, LANDSCAPE AND SECTION J DOCUMENTATION.
6. THE BUILDER SHALL CARRY OUT ALL WORK IN ACCORDANCE WITH: NCC (BCA VOL 1 2025), CONDITIONS OF DEVELOPMENT CONSENT, WHS REGULATION (NSW), AND RELEVANT AUSTRALIAN STANDARDS.
7. PROVIDE ADEQUATE PROTECTION TO EXISTING STRUCTURES, PUBLIC SPACES AND SERVICES DURING CONSTRUCTION.
8. THE BUILDER SHALL COORDINATE ALL TRADES AND ENSURE PENETRATIONS, SET-OUTS AND SERVICE ROUTES ARE ACCURATELY LOCATED.
9. ALL DIMENSIONS TO BE CHECKED ON SITE AND SETOUT BY A SURVEYOR PRIOR TO COMMENCEMENT OF CONSTRUCTION.

4. FIRE SAFETY & EGRESS
14. FIRE-RESISTING CONSTRUCTION TO COMPLY WITH NCC SECTIONS C1 TO C3 AND SPECIFICATION C1.1.

NOTE:

CCTV CAMERAS TO BE INSTALLED TO SATISFY CONDITION 20 OF DA

INTERCOM TO BE INSTALLED TO ENTRY DOORS AND CARPARK.

REFER TO STAMPED DA No. **DA18/0471.03**
DRAWING No. MOD101

FOR CC SUBMISSION

No.	Date	Issue Notes
CC-A	02-Sep-26	FOR CC SUBMISSION

Consultant / Notes:
Survey Prepared by Total Surveying Solutions
ARTARMON.CAMDEN, MANLYVALE

COPYRIGHT
THIS DRAWING IS THE PROPERTY OF LYLE MARSHALL AND PARTNERS P/L AND MAY ONLY BE USED FOR THE PURPOSE FOR WHICH IT WAS COMMISSIONED & IN ACCORDANCE WITH THE TERMS OF ENGAGEMENT FOR THAT COMMISSION. UNAUTHORISED USE OF THIS DRAWING IS PROHIBITED.


Design By		Job No.	5187-26
Drawn By	EMMC	Scale	1:200
Reviewed By		Date	02-Sep-26
Passed By		Date of Issue	
Sheet No.	A100 of	Issue	CC-A

TEST PROJECT

Regulated Design Record

Project Address:			
Project Title:			
Consent No:	DA18/0471.03	Body Corporate Reg No:	
Drawing Title:	LEVEL 1 FLOOR PLAN - 1:200	Drawing No:	5187-26-A101

Rev	Date dd.mm.yy	Description	DEP Full Name	Reg No
CC-A	02/09/26	FOR CC SUBMISSION	ERICA MARSHALL-EVANS	DEP 0001207

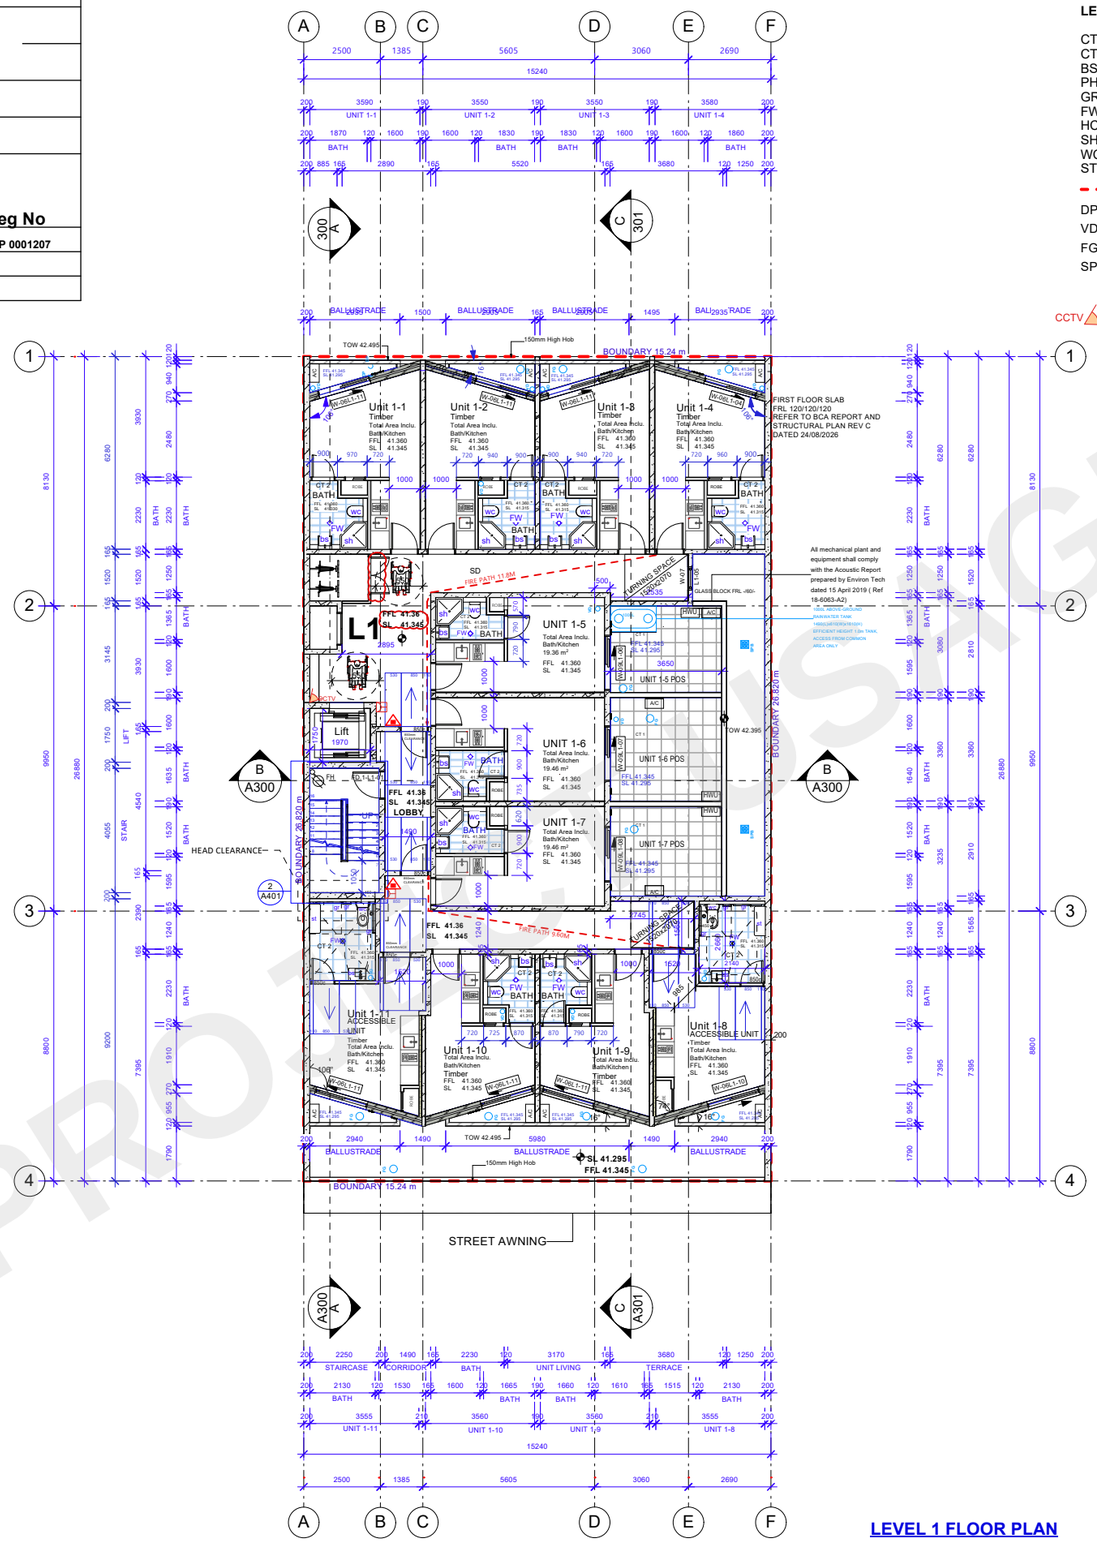

LEGEND

CT 1	TILED FLOOR
CT2	NON SLIP TILE
BS	BASIN
PH	TOILET PAPER HOLDER
GR	GRABRAIL
FW	FLOOR WASTE
HC	HOSE COCK/ WATER
SH	SHOWER
WC	WATER CLOSET
ST	SHOWER SEAT
	BOUNDARY LINE
DP	DOWNPIPE
VD	VERTICAL DROP
FG	FLOOR GRATE
SPB	SUSPENDED PLANTER BOX
	RAINWATER OUTLET
CCTV	CCTV CAMERA

WALL TYPES

115 mm INTERNAL STEEL STUD WALL
13 mm PLASTERBOARD
90 mm STEEL STUD
13 mm PLASTERBOARD

270 mm CAVITY BRICK WALL
FRL 90/90/90
110 mm BRICK
90 50 AIR GAP
110 mm BRICK

FRL 240/240/240 — **Ritek XL - 200A EXTERNAL CONCRETE WALL**

FRL 240/240/240 — **Ritek XL - 165A INTERNAL CONCRETE WALL**

FRL 240/240/240 — **Ritek XL - 150A INTERNAL CONCRETE WALL**

FRL 240/240/240 — **Ritek XL - 165-C INTERTENANCY WALLS**
13 mm PLASTERBOARD
165 mm Ritek XL WALL
13 mm PLASTERBOARD
ALLOW 190mm

FRL 240/240/240 — **Ritek XL - 150-C DISCONTINUOUS WALLS**
13 mm PLASTERBOARD
64 mm STEEL STUD WITH
GLASS FIBRE INSULATION
20 mm GAP
150 mm XL WALL
13 mm PLASTERBOARD

MANUAL CALL POINT (MCP) COMPLYING WITH AS 1670.1:2018 AND AS ISO 7240.11:2018

5 KG CARBON DIOXIDE (C02) TYPE FIRE EXTINGUISHER TO CONFORM WITH AS 2444-2001

0 2 3 5 m

CONSTRUCTION CERTIFICATE NOTES:

GENERAL

1.ALL WORK SHALL COMPLY WITH THE NCC (BCA VOL 1 2025 EDITION), CONDITIONS OF CONSENT, AND THE RELEVANT AUSTRALIAN STANDARDS AS LISTED BELOW.
2. FOR CONSTRUCTION CERTIFICATE ONLY NOT FOR CONSTRUCTION. ALL DIMENSIONS SHALL BE VERIFIED ON SITE PRIOR TO COMMENCEMENT OF WORK. DO NOT SCALE DRAWINGS.
3.BYDA BEFORE YOU DIG FOR ANY UNDERGROUND SERVICES.WWW.BYDA.COM.AU
4. ANY DISCREPANCIES BETWEEN DRAWINGS, SITE CONDITIONS, OR SPECIFICATIONS SHALL BE REFERRED TO THE ARCHITECT BEFORE PROCEEDING.
5. DRAWINGS ARE TO BE READ IN CONJUNCTION WITH THE ARCHITECTURAL SPECIFICATION AND ALL CONSULTANT DRAWINGS AND SPECIFICATIONS, INCLUDING STRUCTURAL, CIVIL, HYDRAULIC, MECHANICAL, ELECTRICAL, FIRE, LANDSCAPE AND SECTION J DOCUMENTATION.
6. THE BUILDER SHALL CARRY OUT ALL WORK IN ACCORDANCE WITH: NCC (BCA VOL 1 2025), CONDITIONS OF DEVELOPMENT CONSENT, WHS REGULATION (NSW), AND RELEVANT AUSTRALIAN STANDARDS.
7. PROVIDE ADEQUATE PROTECTION TO EXISTING STRUCTURES, PUBLIC SPACES AND SERVICES DURING CONSTRUCTION.
8. THE BUILDER SHALL COORDINATE ALL TRADES AND ENSURE PENETRATIONS, SET-OUTS AND SERVICE ROUTES ARE ACCURATELY LOCATED.
9. ALL DIMENSIONS TO BE CHECKED ON SITE AND SETOUT BY A SURVEYOR PRIOR TO COMMENCEMENT OF CONSTRUCTION.

4. FIRE SAFETY & EGRESS

14. FIRE-RESISTING CONSTRUCTION TO COMPLY WITH NCC SECTIONS C1 TO C3 AND SPECIFICATION C1.1.

7. ENVIRONMENTAL & ACOUSTIC

25. EXTERNAL AIR CONDITIONING UNITS TO HAVE AN ACOUSTIC ENCLOSURE ON A UNIT WITH A NOISE LEVEL OF 70 DBA WITH A 25 DBA REDUCTION, RELEVANT NOISE GOALS AT THE RELEVANT PROPERTY BOUNDARIES WILL BE ACHIEVED.

LEVEL 1 FLOOR PLAN

REFER TO STAMPED DA No. **DA18/0471.03**
DRAWING No. MOD103

FOR CC SUBMISSION

No.	Date	Issue Notes
CC-A	02-Sep-26	FOR CC CONSTRUCTION

Consultant / Notes:
Survey Prepared by Total Surveying Solutions
ARTARMON.CAMDEN, MANLYVALE

COPYRIGHT
THIS DRAWING IS THE PROPERTY OF LYLE MARSHALL AND PARTNERS P/L AND MAY O BE USED FOR THE PURPOSE FOR WHICH IT WAS COMMISSIONED & IN ACCORDANCE THE TERMS OF ENGAGEMENT FOR THAT COMMISSION. UNAUTHORISED USE OF THIS DRAWING IS PROHIBITED.

Design By	Job No. 5187-26
Drawn By EMMC	Scale 1:200
Reviewed By	Date 02-Sep-26
Passed By	Date of Issue
	Sheet No. A101 of
	Issue CC-A


TEST PROJECT ONLY

SAMPLE PROJECT A - ARCHITECTURAL - RECRUITMENT ASSESSMENT ONLY

Regulated Design Record

Project Address:			
Project Title:			
Consent No:	DA18/0471.03	Body Corporate Reg No:	
Drawing Title:	LEVEL 2 FLOOR PLAN - 1:200	Drawing No:	5187-26-A102


Rev	Date dd.mm.yy	Description	DEP Full Name	Reg No
CC-A	02/09/26	FOR CC SUBMISSION	ERICA MARSHALL-EVANS	DEP 0001207

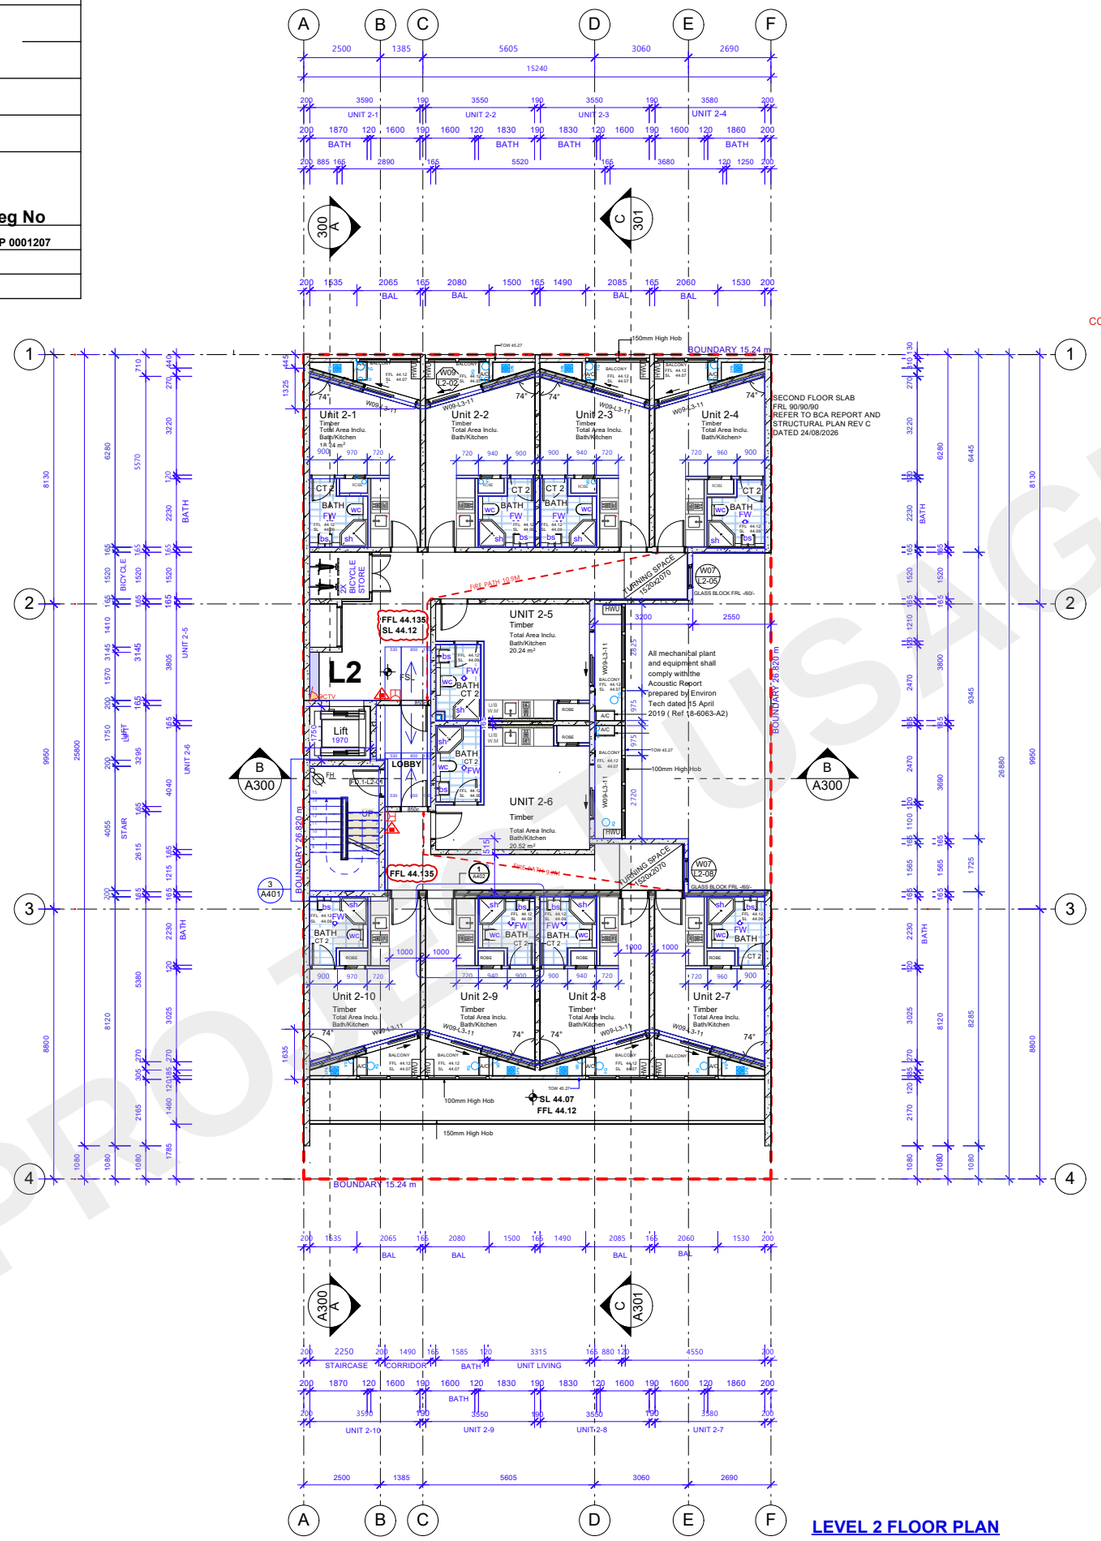
A B C D E F
1 2 3 4
2500 1385 5605 3060 2690
15240
UNIT 2-1 UNIT 2-2 UNIT 2-3 UNIT 2-4
BATH
BOUNDARY 15.24 m
BOUNDARY 26.820 m
150mm High Hob
100mm High Hob
SECOND FLOOR SLAB FRL 90/90/90 REFER TO BCA REPORT AND STRUCTURAL PLAN REV C DATED 24/08/2026
Unit 2-1 Timber Total Area Inclu. Bath/Kitchen 18.04 m²
Unit 2-2 Timber Total Area Inclu. Bath/Kitchen
Unit 2-3 Timber Total Area Inclu. Bath/Kitchen
Unit 2-4 Timber Total Area Inclu. Bath/Kitchen
UNIT 2-5 Timber Total Area Inclu. Bath/Kitchen 20.24 m²
UNIT 2-6 Timber Total Area Inclu. Bath/Kitchen 20.52 m²
Unit 2-10 Timber Total Area Inclu. Bath/Kitchen
Unit 2-9 Timber Total Area Inclu. Bath/Kitchen
Unit 2-8 Timber Total Area Inclu. Bath/Kitchen
Unit 2-7 Timber Total Area Inclu. Bath/Kitchen
L2
FFL 44.135 SL 44.12
FFL 44.135
SL 44.07 FFL 44.12
LOBBY
Lift 1970
BICYCLE STORE
STAIR
LIFT
UNIT 2-5
UNIT 2-6
UNIT 2-10
UNIT 2-9
UNIT 2-8
UNIT 2-7
STAIRCASE
CORRIDOR
UNIT LIVING
All mechanical plant and equipment shall comply with the Acoustic Report prepared by Environ Tech dated 15 April 2019 (Ref 18-6063-A2)
TURNING SPACE 1200X2070
W07 2-08
GLASS BLOCK FRL -/60/-
W09-L3-11
W09-L3-1
W09-L3-2
Regulated Design Record

Project Address:			
Project Title:			
Consent No:	DA18/0471.03	Body Corporate Reg No:	
Drawing Title:	LEVEL 3 FLOOR PLAN - 1:200	Drawing No:	5187-26-A103

Rev	Date dd.mm.yy	Description	DEP Full Name	Reg No
CC-A	02/09/26	FOR CC SUBMISSION	ERICA MARSHALL-EVANS	DEP 0001207

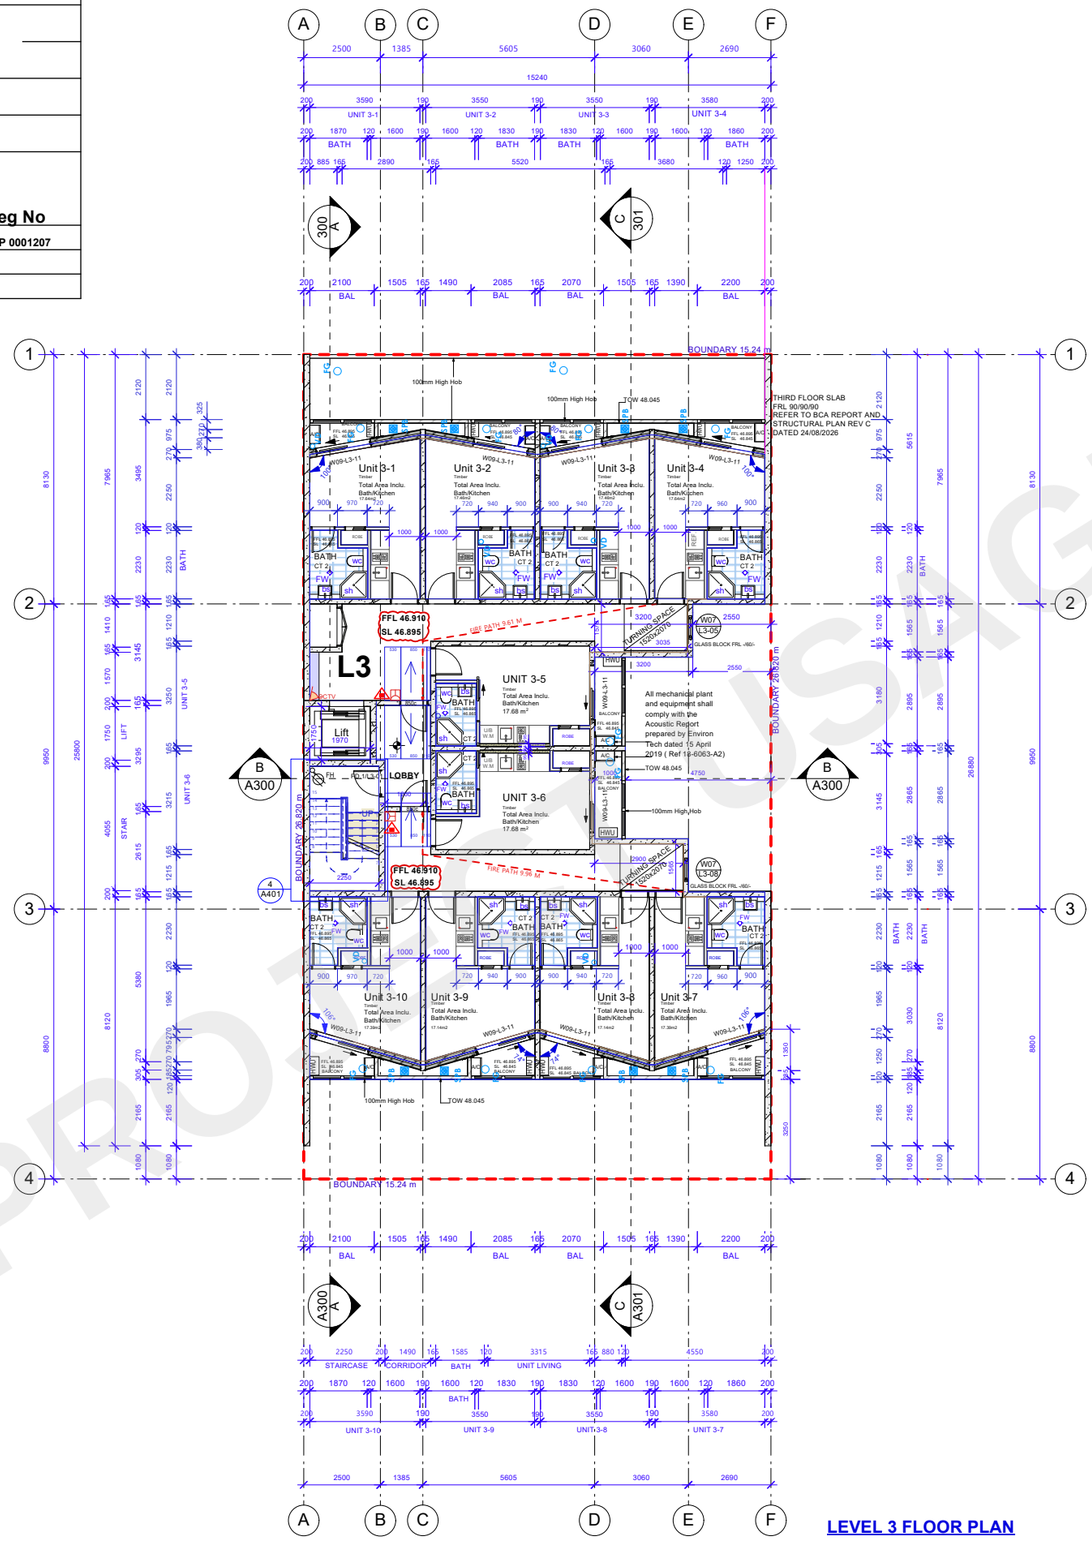

LEGEND

CT 1	TILED FLOOR
CT2	NON SLIP TILE
BS	BASIN
PH	TOILET PAPER HOLDER
GR	GRABRAIL
FW	FLOOR WASTE
HC	HOSE COCK/ WATER
SH	SHOWER
WC	WATER CLOSET
ST	SHOWER SEAT
	BOUNDARY LINE
DP	DOWNPIPE
VD	VERTICAL DROP
FG	FLOOR GRATE
SPB	SUSPENDED PLANTER BOX
	RAINWATER OUTLET
CCTV	CCTV CAMERA

WALL TYPES

115 mm INTERNAL STEEL STUD WALL
13 mm PLASTERBOARD
90 mm STEEL STUD
13 mm PLASTERBOARD

CONCRETE COLUMN

FRL 90/90/90
270 mm CAVITY BRICK WALL
110 mm BRICK
90 50 AIR GAP
110 mm BRICK

FRL 240/240/240
Ritek XL - 200A EXTERNAL CONCRETE WALL

FRL 240/240/240
Ritek XL - 165A INTERNAL CONCRETE WALL

FRL 240/240/240
Ritek XL - 150A INTERNAL CONCRETE WALL

FRL 240/240/240
Ritek XL - 165-C INTERTENANCY WALLS
13 mm PLASTERBOARD
165 mm Ritek XL WALL
13 mm PLASTERBOARD
ALLOW 190mm

FRL 240/240/240
Ritek XL - 150-C DISCONTINUOUS WALLS
13 mm PLASTERBOARD
64 mm STEEL STUD WITH
GLASS FIBRE INSULATION
20 mm GAP
150 mm XL WALL
13 mm PLASTERBOARD

MANUAL CALL POINT (MCP) COMPLYING WITH AS 1670.1:2018 AND AS ISO 7240.11:2018

5 KG CARBON DIOXIDE (C02) TYPE FIRE EXTINGUISHER TO CONFORM WITH AS 2444-2001

N

0 2 3 5 m

CONSTRUCTION CERTIFICATE NOTES:

GENERAL
1.ALL WORK SHALL COMPLY WITH THE NCC (BCA VOL 1 2025 EDITION), CONDITIONS OF CONSENT, AND THE RELEVANT AUSTRALIAN STANDARDS AS LISTED BELOW.
2. FOR CONSTRUCTION CERTIFICATE ONLY NOT FOR CONSTRUCTION. ALL DIMENSIONS SHALL BE VERIFIED ON SITE PRIOR TO COMMENCEMENT OF WORK. DO NOT SCALE DRAWINGS.
3.BYDA BEFORE YOU DIG FOR ANY UNDERGROUND SERVICES.WWW.BYDA.COM.AU
4. ANY DISCREPANCIES BETWEEN DRAWINGS, SITE CONDITIONS, OR SPECIFICATIONS SHALL BE REFERRED TO THE ARCHITECT BEFORE PROCEEDING.
5. DRAWINGS ARE TO BE READ IN CONJUNCTION WITH THE ARCHITECTURAL SPECIFICATION AND ALL CONSULTANT DRAWINGS AND SPECIFICATIONS, INCLUDING STRUCTURAL, CIVIL, HYDRAULIC, MECHANICAL, ELECTRICAL, FIRE, LANDSCAPE AND SECTION J DOCUMENTATION.
6. THE BUILDER SHALL CARRY OUT ALL WORK IN ACCORDANCE WITH: NCC (BCA VOL 1 2025), CONDITIONS OF DEVELOPMENT CONSENT, WHS REGULATION (NSW), AND RELEVANT AUSTRALIAN STANDARDS.
7. PROVIDE ADEQUATE PROTECTION TO EXISTING STRUCTURES, PUBLIC SPACES AND SERVICES DURING CONSTRUCTION.
8. THE BUILDER SHALL COORDINATE ALL TRADES AND ENSURE PENETRATIONS, SET-OUTS AND SERVICE ROUTES ARE ACCURATELY LOCATED.
9. ALL DIMENSIONS TO BE CHECKED ON SITE AND SETOUT BY A SURVEYOR PRIOR TO COMMENCEMENT OF CONSTRUCTION.

4. FIRE SAFETY & EGRESS
14. FIRE-RESISTING CONSTRUCTION TO COMPLY WITH NCC SECTIONS C1 TO C3 AND SPECIFICATION C1.1.

7. ENVIRONMENTAL & ACOUSTIC
25. EXTERNAL AIR CONDITIONING UNITS TO HAVE AN ACOUSTIC ENCLOSURE ON A UNIT WITH A NOISE LEVEL OF 70 DBA WITH A 25 DBA REDUCTION, RELEVANT NOISE GOALS AT THE RELEVANT PROPERTY BOUNDARIES WILL BE ACHIEVED.

LEVEL 3 FLOOR PLAN

REFER TO STAMPED DA No. **DA18/0471.03**
DRAWING No. MOD103

FOR CC SUBMISSION

No.	Date	Issue Notes
CC-A	02-Sep-26	FOR CC SUBMISSION

Consultant / Notes:
Survey Prepared by Total Surveying Solutions
ARTARMON.CAMDEN, MANLYVALE

COPYRIGHT
THIS DRAWING IS THE PROPERTY OF LYLE MARSHALL AND PARTNERS P/L AND MAY O BE USED FOR THE PURPOSE FOR WHICH IT WAS COMMISSIONED & IN ACCORDANCE THE TERMS OF ENGAGEMENT FOR THAT COMMISSION. UNAUTHORISED USE OF THIS DRAWING IS PROHIBITED.


Design By		Job No.	5187-26
Drawn By	EMMC	Scale	1:200
Reviewed By		Date	02-Sep-26
Passed By		Date of Issue	
		Sheet No.	A103 of
		Issue	CC-A

TEST PROJECT - USAGE ONLY

Regulated Design Record

Project Address:	
Project Title:	
Consent No: DA18/0471.03	Body Corporate Reg No:
Drawing Title: LEVEL 4 FLOOR PLAN - 1:200	Drawing No: 5187-26-A104

Rev	Date dd.mm.yy	Description	DEP Full Name	Reg No
CC-A	02/09/26	FOR CC SUBMISSION	ERICA MARSHALL-EVANS	DEP 0001207

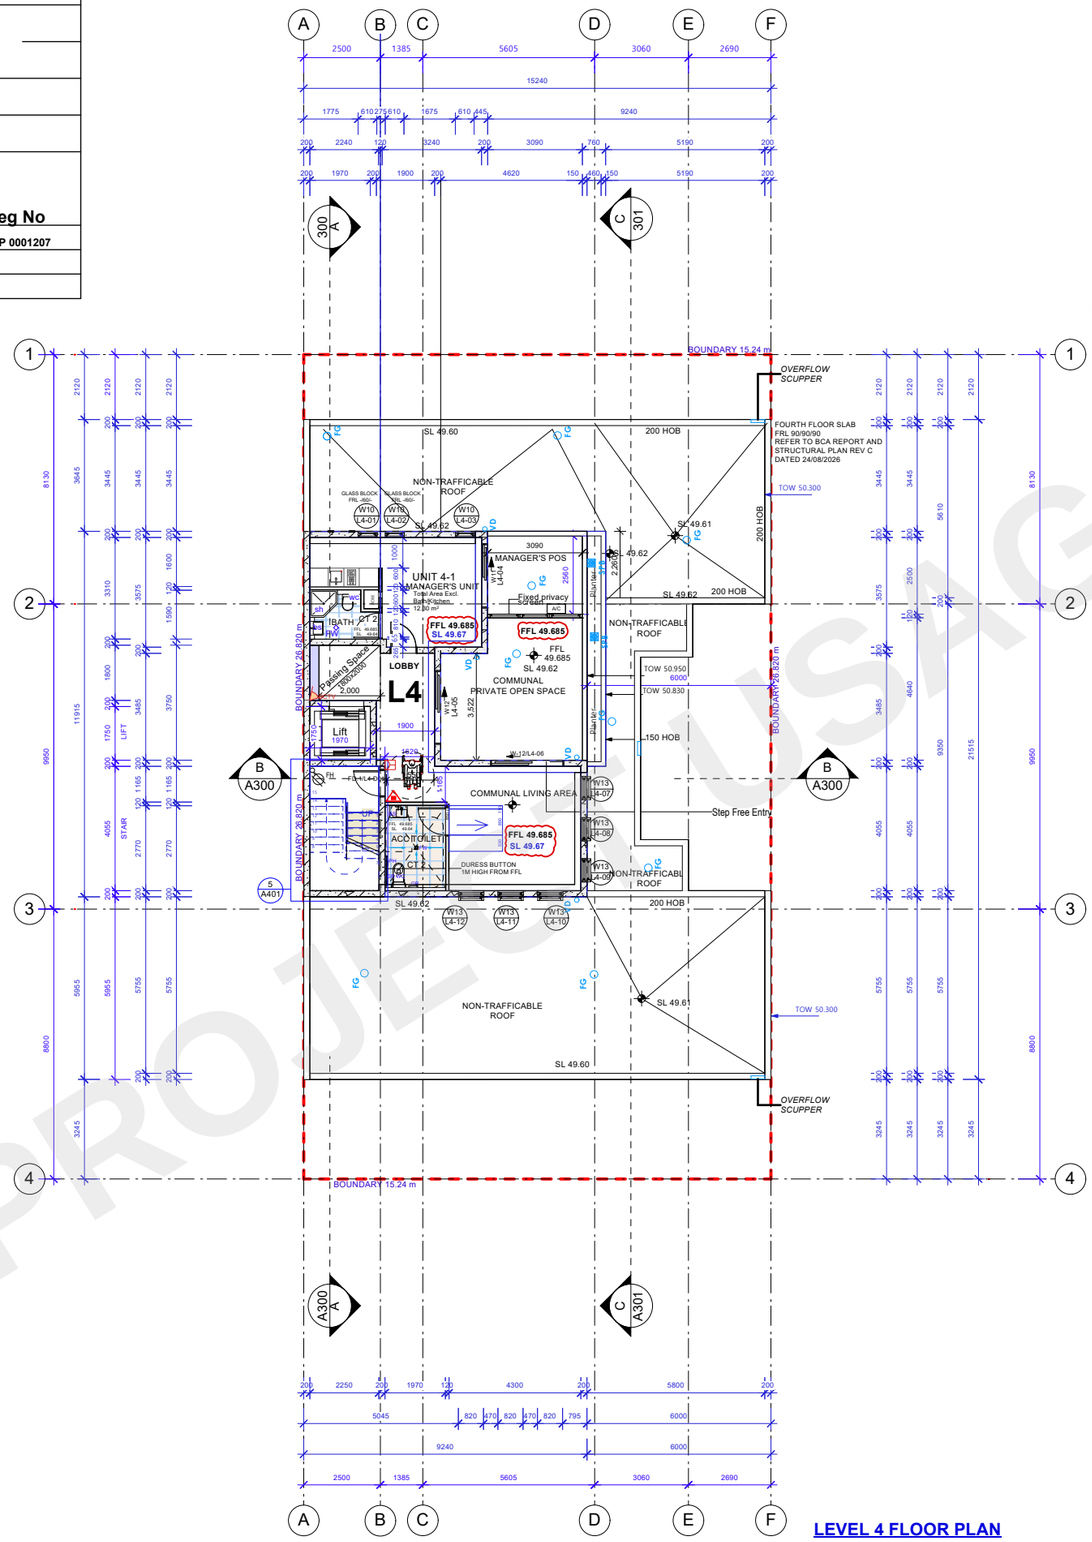

LEVEL 4 FLOOR PLAN

LEGEND

CT 1	TILED FLOOR
CT2	NON SLIP TILE
BS	BASIN
PH	TOILET PAPER HOLDER
GR	GRABRAIL
FW	FLOOR WASTE
HC	HOSE COCK/ WATER
SH	SHOWER
WC	WATER CLOSET
ST	SHOWER SEAT
	BOUNDARY LINE
DP	DOWNPIPE
VD	VERTICAL DROP
FG	FLOOR GRATE
SPB	SUSPENDED PLANTER BOX
	RAINWATER OUTLET
CCTV	CCTV CAMERA

WALL TYPES

115 mm INTERNAL STEEL STUD WALL
13 mm PLASTERBOARD
90 mm STEEL STUD
13 mm PLASTERBOARD

FRL 240/240/240 — Ritek XL - 200A EXTERNAL CONCRETE WALL

MANUAL CALL POINT (MCP) COMPLYING WITH AS 1670.1:2018 AND AS ISO 7240.11:2018

5 KG CARBON DIOXIDE (C02) TYPE FIRE EXTINGUISHER TO CONFORM WITH AS 2444-2001

0 2 3 5 m

CONSTRUCTION CERTIFICATE NOTES:

GENERAL

1.ALL WORK SHALL COMPLY WITH THE NCC (BCA VOL 1 2025 EDITION), CONDITIONS OF CONSENT, AND THE RELEVANT AUSTRALIAN STANDARDS AS LISTED BELOW.
2. FOR CONSTRUCTION CERTIFICATE ONLY NOT FOR CONSTRUCTION. ALL DIMENSIONS SHALL BE VERIFIED ON SITE PRIOR TO COMMENCEMENT OF WORK. DO NOT SCALE DRAWINGS.
3.BYDA BEFORE YOU DIG FOR ANY UNDERGROUND SERVICES.WWW.BYDA.COM.AU
4. ANY DISCREPANCIES BETWEEN DRAWINGS, SITE CONDITIONS, OR SPECIFICATIONS SHALL BE REFERRED TO THE ARCHITECT BEFORE PROCEEDING.
5. DRAWINGS ARE TO BE READ IN CONJUNCTION WITH THE ARCHITECTURAL SPECIFICATION AND ALL CONSULTANT DRAWINGS AND SPECIFICATIONS, INCLUDING STRUCTURAL, CIVIL, HYDRAULIC, MECHANICAL, ELECTRICAL, FIRE, LANDSCAPE AND SECTION J DOCUMENTATION.
6. THE BUILDER SHALL CARRY OUT ALL WORK IN ACCORDANCE WITH: NCC (BCA VOL 1 2025), CONDITIONS OF DEVELOPMENT CONSENT, WHS REGULATION (NSW), AND RELEVANT AUSTRALIAN STANDARDS.
7. PROVIDE ADEQUATE PROTECTION TO EXISTING STRUCTURES, PUBLIC SPACES AND SERVICES DURING CONSTRUCTION.
8. THE BUILDER SHALL COORDINATE ALL TRADES AND ENSURE PENETRATIONS, SET-OUTS AND SERVICE ROUTES ARE ACCURATELY LOCATED.
9. ALL DIMENSIONS TO BE CHECKED ON SITE AND SETOUT BY A SURVEYOR PRIOR TO COMMENCEMENT OF CONSTRUCTION.

4. FIRE SAFETY & EGRESS

14. FIRE-RESISTING CONSTRUCTION TO COMPLY WITH NCC SECTIONS C1 TO C3 AND SPECIFICATION C1.1.

7. ENVIRONMENTAL & ACOUSTIC

25. EXTERNAL AIR CONDITIONING UNITS TO HAVE AN ACOUSTIC ENCLOSURE ON A UNIT WITH A NOISE LEVEL OF 70 DBA WITH A 25 DBA REDUCTION, RELEVANT NOISE GOALS AT THE RELEVANT PROPERTY BOUNDARIES WILL BE ACHIEVED.

REFER TO STAMPED DA No. **DA18/0471.03**
DRAWING No. MOD103

FOR CC SUBMISSION

No.	Date	Issue Notes
CC-A	02-Sep-26	FOR CC SUBMISSION

Consultant / Notes:
Survey Prepared by Total Surveying Solutions
ARTARMON.CAMDEN, MANLYVALE

COPYRIGHT
THIS DRAWING IS THE PROPERTY OF LYLE MARSHALL AND PARTNERS P/L AND MAY ON BE USED FOR THE PURPOSE FOR WHICH IT WAS COMMISSIONED & IN ACCORDANCE WI THE TERMS OF ENGAGEMENT FOR THAT COMMISSION. UNAUTHORISED USE OF THIS DRAWING IS PROHIBITED.


Design By		Job No.	5187-26
Drawn By	EMMC	Scale	1:200
Reviewed By		Date	02-Sep-26
Passed By		Date of Issue	
Sheet No.	A104 of	Issue	CC-A

TEST PROJECT
NOT FOR USAGE ONLY

Regulated Design Record

Project Address:	
Project Title:	
Consent No: DA18/0471.03	Body Corporate Reg No:
Drawing Title: ROOF PLAN - 1:200	Drawing No: 5187-26-A105

Rev	Date dd.mm.yy	Description	DEP Full Name	Reg No
CC-A	02/09/26	FOR CC SUBMISSION	ERICA MARSHALL-EVANS	DEP 0001207

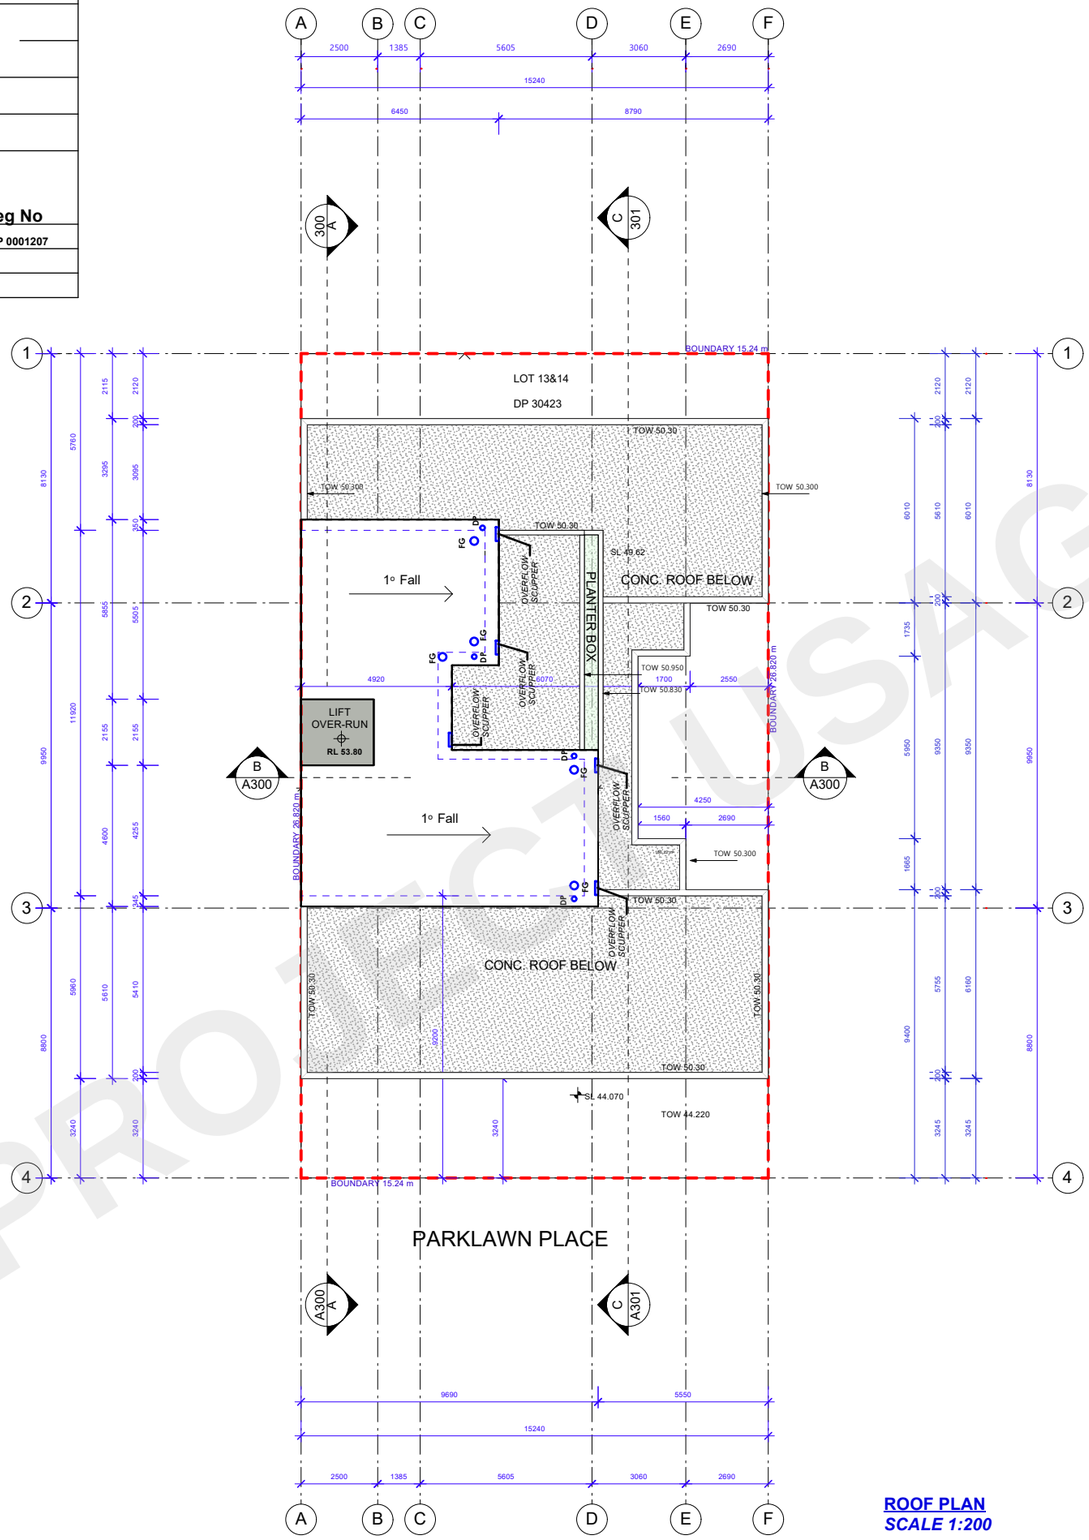

LEGEND

CT 1	TILED FLOOR
CT2	NON SLIP TILE
BS	BASIN
PH	TOILET PAPER HOLDER
GR	GRABRAIL
FW	FLOOR WASTE
HC	HOSE COCK/ WATER
SH	SHOWER
WC	WATER CLOSET
ST	SHOWER SEAT
- -	BOUNDARY LINE
DP	DOWNPIPE
VD	VERTICAL DROP

N

0 2 3 5 m

CONSTRUCTION CERTIFICATE NOTES:

GENERAL

1.ALL WORK SHALL COMPLY WITH THE NCC (BCA VOL 1 2025 EDITION), CONDITIONS OF CONSENT, AND THE RELEVANT AUSTRALIAN STANDARDS AS LISTED BELOW.
2. FOR CONSTRUCTION CERTIFICATE ONLY NOT FOR CONSTRUCTION. ALL DIMENSIONS SHALL BE VERIFIED ON SITE PRIOR TO COMMENCEMENT OF WORK. DO NOT SCALE DRAWINGS.
3.BYDA BEFORE YOU DIG FOR ANY UNDERGROUND SERVICES.WWW.BYDA.COM.AU
4. ANY DISCREPANCIES BETWEEN DRAWINGS, SITE CONDITIONS, OR SPECIFICATIONS SHALL BE REFERRED TO THE ARCHITECT BEFORE PROCEEDING.
5. DRAWINGS ARE TO BE READ IN CONJUNCTION WITH THE ARCHITECTURAL SPECIFICATION AND ALL CONSULTANT DRAWINGS AND SPECIFICATIONS, INCLUDING STRUCTURAL, CIVIL, HYDRAULIC, MECHANICAL, ELECTRICAL, FIRE, LANDSCAPE AND SECTION J DOCUMENTATION.
6. THE BUILDER SHALL CARRY OUT ALL WORK IN ACCORDANCE WITH: NCC (BCA VOL 1 2025), CONDITIONS OF DEVELOPMENT CONSENT, WHS REGULATION (NSW), AND RELEVANT AUSTRALIAN STANDARDS.
7. PROVIDE ADEQUATE PROTECTION TO EXISTING STRUCTURES, PUBLIC SPACES AND SERVICES DURING CONSTRUCTION.
8. THE BUILDER SHALL COORDINATE ALL TRADES AND ENSURE PENETRATIONS, SET-OUTS AND SERVICE ROUTES ARE ACCURATELY LOCATED.
9. ALL DIMENSIONS TO BE CHECKED ON SITE AND SETOUT BY A SURVEYOR PRIOR TO COMMENCEMENT OF CONSTRUCTION.

4. FIRE SAFETY & EGRESS

14. FIRE-RESISTING CONSTRUCTION TO COMPLY WITH NCC SECTIONS C1 TO C3 AND SPECIFICATION C1.1.

ROOF PLAN
SCALE 1:200

REFER TO STAMPED DA No. **DA18/0471.03**
DRAWING No. MOD103

FOR CC SUBMISSION

No.	Date	Issue Notes
CC-A	02-Sep-26	FOR CC SUBMISSION

Consultant / Notes:

Survey Prepared by Total Surveying Solutions
ARTARMON.CAMDEN, MANLYVALE

COPYRIGHT
THIS DRAWING IS THE PROPERTY OF LYLE MARSHALL AND PARTNERS P/L AND MAY ONL BE USED FOR THE PURPOSE FOR WHICH IT WAS COMMISSIONED & IN ACCORDANCE WIT THE TERMS OF ENGAGEMENT FOR THAT COMMISSION. UNAUTHORISED USE OF THIS DRAWING IS PROHIBITED.
date: 4-9-26
File name:


Design By	Job No. 5187-26
Drawn By EMMC	Scale 1:200
Reviewed By	Date 02-Sep-26
Passed By	Date of Issue
	Sheet No. A105 of
	Issue CC-A

TEST PROJECT USAGE ONLY


Regulated Design Record

Project Address:			
Project Title:			
Consent No:	DA18/0471.03	Body Corporate Reg No:	
Drawing Title:	CAFE LAYOUT	Drawing No:	5187-26-A110

Rev	Date dd.mm.yy	Description	DEP Full Name	Reg No
CC-A	02/09/26	FOR CC SUBMISSION	ERICA MARSHALL-EVANS	DEP 0001207

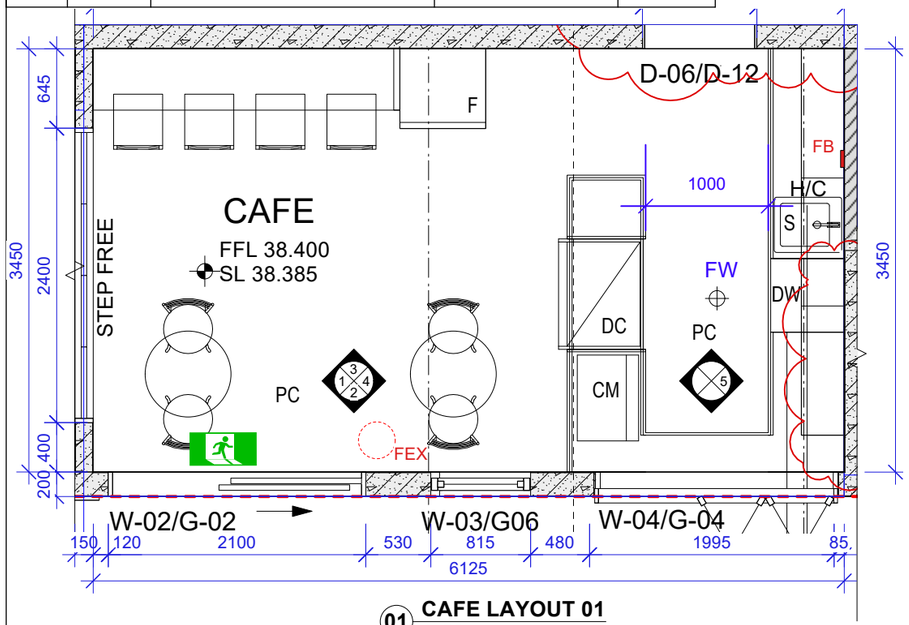

01 CAFE LAYOUT 01
1:50

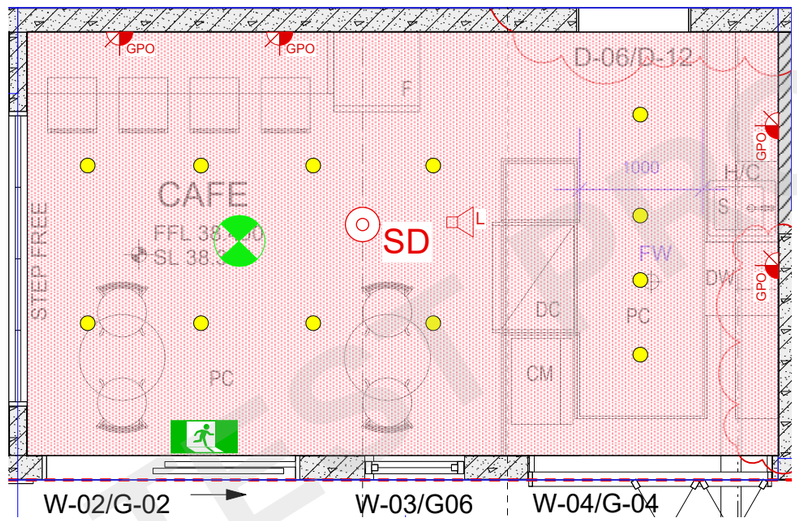

06 CAFE ELECTRICAL LAYOUT 01
1:50

FIRE SERVICES

- L — CELING MOUNTED SPEAKER
- SD — SMOKE DETECTOR
- FEX — FIRE EXTINGUISHER
- FB — FIRE BLANKET
- FIRE EGRESS SIGNS
- EMERGENCY LIGHT TO COMPLY WITH AS/NZS 2293.1:2018. CLASS E32 OR EQUIVALENT


LEGEND

- CH — CEILING HEIGHT ABOVE FINISHED FLOOR LEVEL
- SWITCH
- GPO
- SURFACE MOUNTED LED DOWNLIGHT
- PLASTERBOARD CEILING - FOR WET AREAS (GYPROCK AQUACHECK)
- FIRE RESISTANT PLASTERBOARD CEILING (GYPROCK FYRECHECK 16 MM)


NOTE: KITCHEN TO AS4674 AND FOOD SAFETY AUSTRALIAN STANDARD 3.2.3

LEGEND


PC	POLISHED CONCRETE FLOOR (NON-ABSORBENT)
CT	GLAZED CERAMIC TILE
WP	WALL PAINTED FINISH DULUX WHISPER WHITE (WASHABLE)
S	STAINLESS STEEL SINGLE BOWL SINK
DW	DISH WASHER
CM	COFFEE MACHINE
F	REFRIDGERATOR
DC	REF. GLASS COUNTER TOP DISPLAY
H/C	HOT/COLD HOSE CONNECTOR
WC	WATER CLOSET
B	FREE STANDING BASIN
FW	FLOOR WASTE

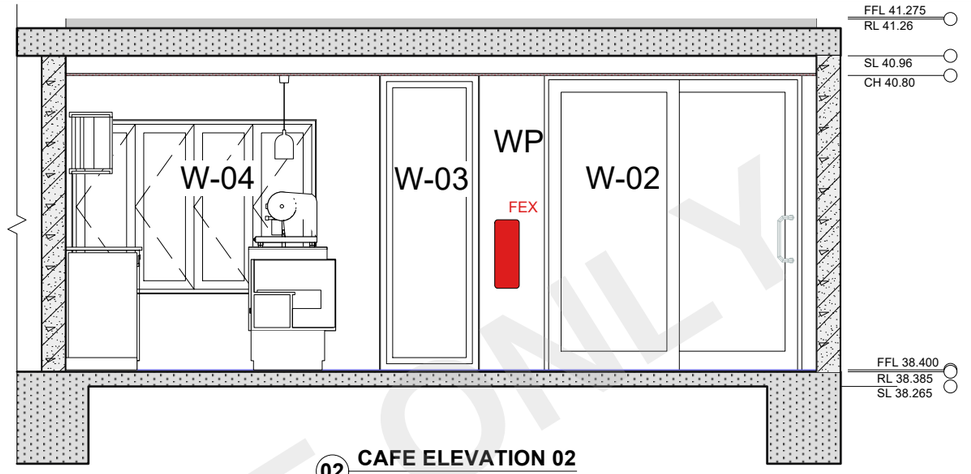


02 CAFE ELEVATION 02
1:50

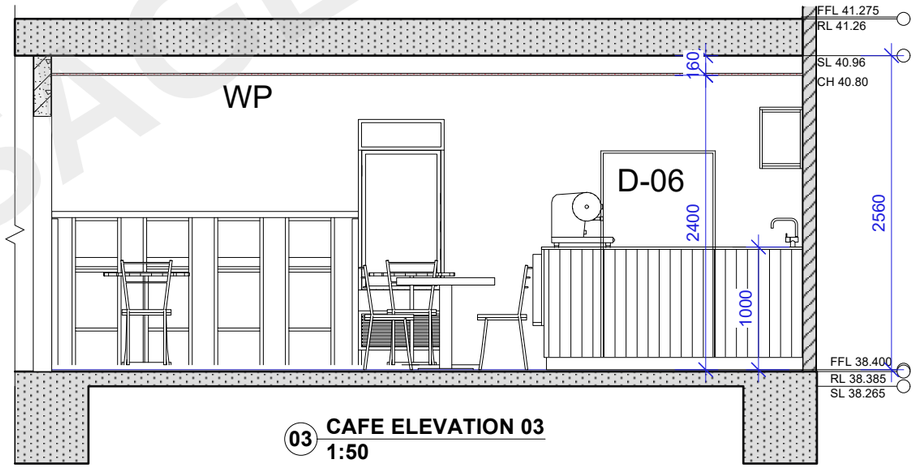

03 CAFE ELEVATION 03
1:50

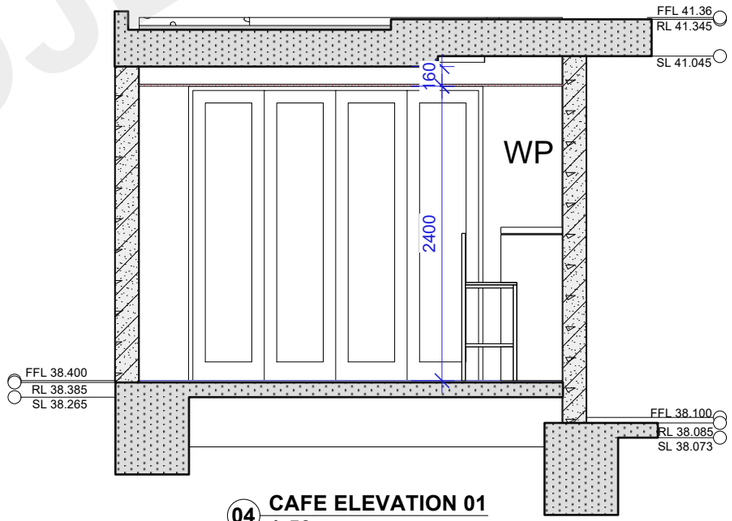

04 CAFE ELEVATION 01
1:50

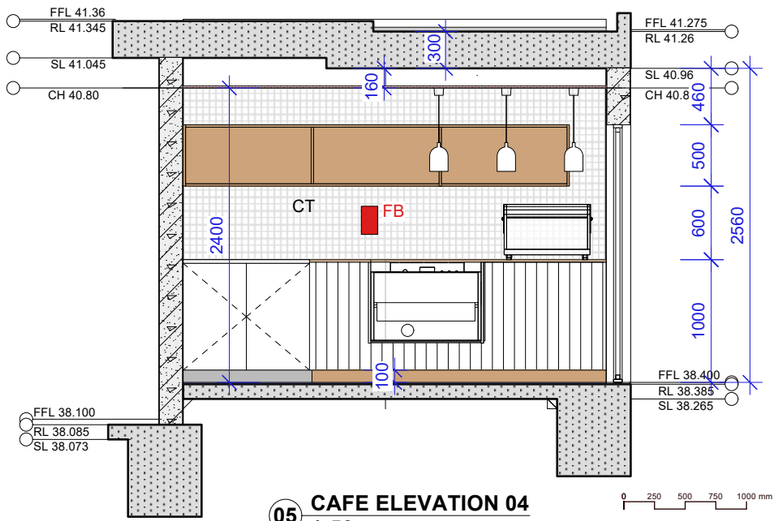

05 CAFE ELEVATION 04
1:50

0 250 500 750 1000 mm

FOR CC SUBMISSION

No.	Date	Issue Notes
CC-A	02-Sep-26	FOR CC SUBMISSION

Consultant / Notes:
Survey Prepared by Total Surveying Solutions
ARTARMON.CAMDEN, MANLYVALE


COPYRIGHT
THIS DRAWING IS THE PROPERTY OF LYLE MARSHALL AND PARTNERS P/L AND MAY ONL BE USED FOR THE PURPOSE FOR WHICH IT WAS COMMISSIONED & IN ACCORDANCE WIT THE TERMS OF ENGAGEMENT FOR THAT COMMISSION. UNAUTHORISED USE OF THIS DRAWING IS PROHIBITED.

Design By		Job No.	5187-26
Drawn By	EMMC	Scale	1:50
Reviewed By		Date	02-Sep-26
Passed By		Date of Issue	
Sheet No.	A110	of	
Issue	CC-A		

TEMPLATE PROJECT NOT FOR USE

Regulated Design Record			
Project Address:			
Project Title:			
Consent No:	DA18/0471.03	Body Corporate Reg No:	
Drawing Title:	DISABLED BATHROOM LAYOUT	Drawing No:	5187-26-A111

Rev	Date dd.mm.yy	Description	DEP Full Name	Reg No
CC-A	02/09/26	FOR CC SUBMISSION	ERICA MARSHALL-EVANS	DEP 0001207

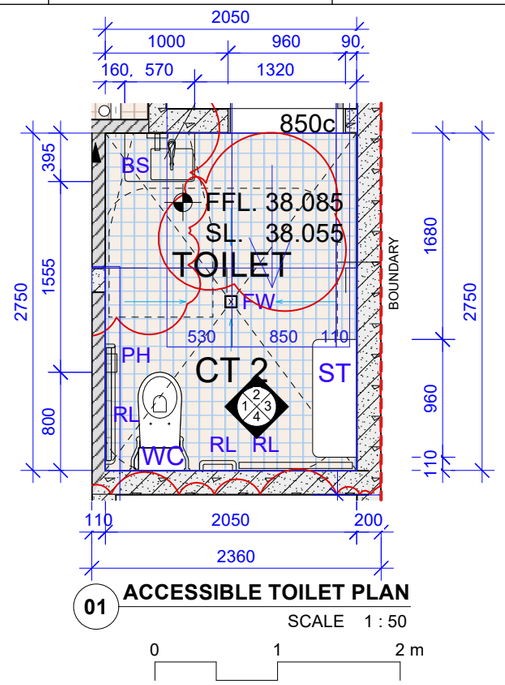

01 **ACCESSIBLE TOILET PLAN**
SCALE 1 : 50

0 1 2 m


LEGEND

BR	BACK REST
CT 2	CERAMIC TILES/ NON SLIP (600X600 TBA)
CLH	CLOTHES HOOK
FW	FLOOR WASTE
GR	GRABRAIL
	GENERAL WASTE
	SHARPS BIN STORAGE
IT	INTERNCON
HR	HANDRAIL MOUNTED AT 900 mm AFFL
HD	HAND DRYER / PAPER TOWEL
MR	MIRROR
EF	EXHAUST FAN
P1	PAINT FINISH
TPH	TOILET PAPER HOLDER
TR	TOWEL RAIL
VB	BASIN - COLOUR-WHITE
WC	WATER CLOSET - CAROMA, WHITE
WT1	CERAMIC WALL TILES (TILES 300X100)
WT2	CERAMIC SKIRTING TILES 100X100
WT3	CERAMIC WALL TILES (TILES 200X100)


BOUNDARY LINE

WALL TYPES


FRL 240/240/240 — 290 — **Ritek XL - 200A EXTERNAL CONCRETE WALL**

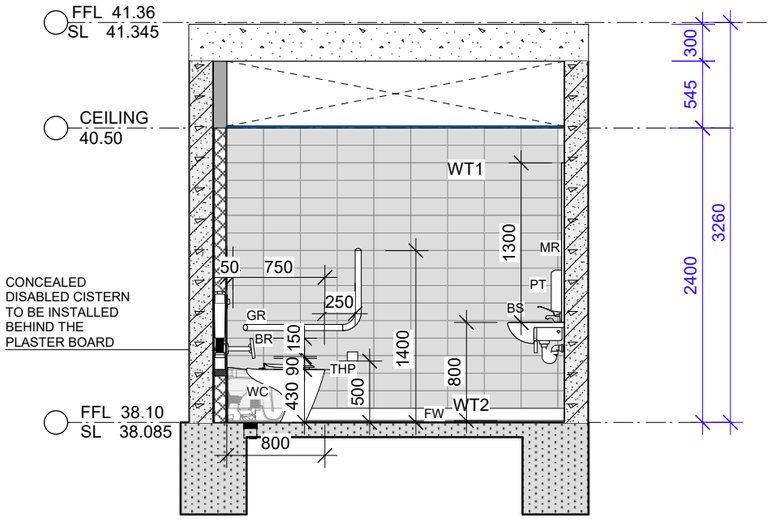


02 **ELEVATION 01**
SCALE 1 : 50

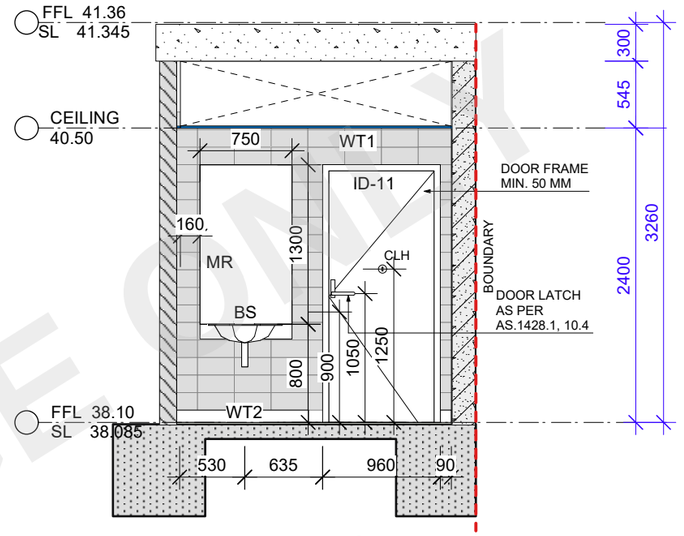

03 **ELEVATION 02**
SCALE 1 : 50

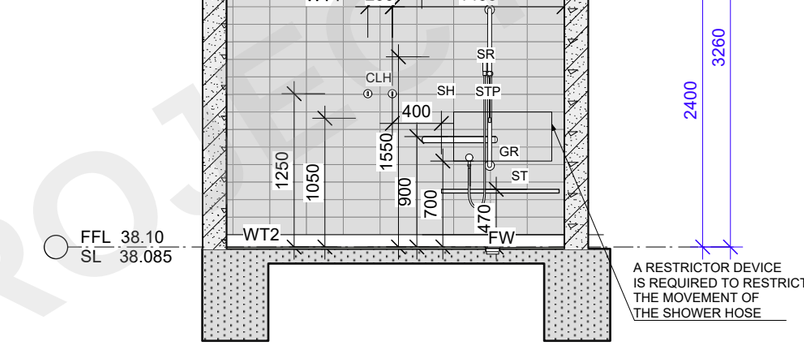

04 **ELEVATION 3**
SCALE 1 : 50

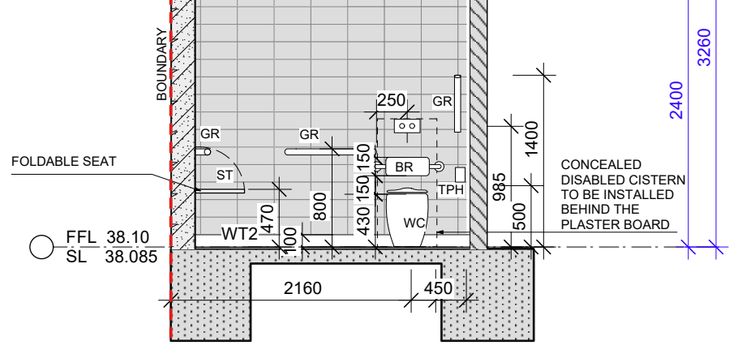

05 **ELEVATION 4**
SCALE 1 : 50

CONSTRUCTION CERTIFICATE NOTES:

GENERAL

1.ALL WORK SHALL COMPLY WITH THE NCC (BCA VOL 1 2025 EDITION), CONDITIONS OF CONSENT, AND THE RELEVANT AUSTRALIAN STANDARDS AS LISTED BELOW.
2. FOR CONSTRUCTION CERTIFICATE ONLY NOT FOR CONSTRUCTION. ALL DIMENSIONS SHALL BE VERIFIED ON SITE PRIOR TO COMMENCEMENT OF WORK. DO NOT SCALE DRAWINGS.
3.BYDA BEFORE YOU DIG FOR ANY UNDERGROUND SERVICES.WWW.BYDA.COM.AU
4. ANY DISCREPANCIES BETWEEN DRAWINGS, SITE CONDITIONS, OR SPECIFICATIONS SHALL BE REFERRED TO THE ARCHITECT BEFORE PROCEEDING.
5. DRAWINGS ARE TO BE READ IN CONJUNCTION WITH THE ARCHITECTURAL SPECIFICATION AND ALL CONSULTANT DRAWINGS AND SPECIFICATIONS, INCLUDING STRUCTURAL, CIVIL, HYDRAULIC, MECHANICAL, ELECTRICAL, FIRE, LANDSCAPE AND SECTION J DOCUMENTATION.
6. THE BUILDER SHALL CARRY OUT ALL WORK IN ACCORDANCE WITH: NCC (BCA VOL 1 2025), CONDITIONS OF DEVELOPMENT CONSENT, WHS REGULATION (NSW), AND RELEVANT AUSTRALIAN STANDARDS.
7. PROVIDE ADEQUATE PROTECTION TO EXISTING STRUCTURES, PUBLIC SPACES AND SERVICES DURING CONSTRUCTION.
8. THE BUILDER SHALL COORDINATE ALL TRADES AND ENSURE PENETRATIONS, SET-OUTS AND SERVICE ROUTES ARE ACCURATELY LOCATED.
9. ALL DIMENSIONS TO BE CHECKED ON SITE AND SETOUT BY A SURVEYOR PRIOR TO COMMENCEMENT OF CONSTRUCTION.
19. DOORS AND LIFTS OFF HINGES TO ALL TOILETS.
20. DISABLE TOILET TO COMPLY WITH AS 1428.1-2009

TEST PROJECT USAGE ONLY

No.	Date	Issue Notes
CC-A	02-Sep-26	FOR CC SUBMISSION

Consultant / Notes:
SURVEY BY
REGISTERED SURVEYORS
PO BOX

COPYRIGHT
THIS DRAWING IS THE PROPERTY OF LYLE MARSHALL AND PARTNERS P/L AND MAY ONLY BE USED FOR THE PURPOSE FOR WHICH IT WAS COMMISSIONED & IN ACCORDANCE WITH THE TERMS OF ENGAGEMENT FOR THAT COMMISSION. UNAUTHORISED USE OF THIS DRAWING IS PROHIBITED.

FOR CC SUBMISSION


T LAYOUT

Design By: EMMC	Job No.: 5187-26		
Drawn By: EMMC	Scale: 1:50		
Reviewed By: EMMC	Date: 02-Sep-26	Sheet No.: A111 of	Issue: CC-A
Passed By: EMMC	Date of Issue:		

Regulated Design Record

Project Address:			
Project Title:			
Consent No:	DA18/0471.03	Body Corporate Reg No:	
Drawing Title:	GROUND FLOOR REFLECTED CEILING PLAN	Drawing No:	5187-26-A120

Rev	Date dd.mm.yy	Description	DEP Full Name	Reg No
CC-A	02/09/26	FOR CC SUBMISSION	ERICA MARSHALL-EVANS	DEP 0001207

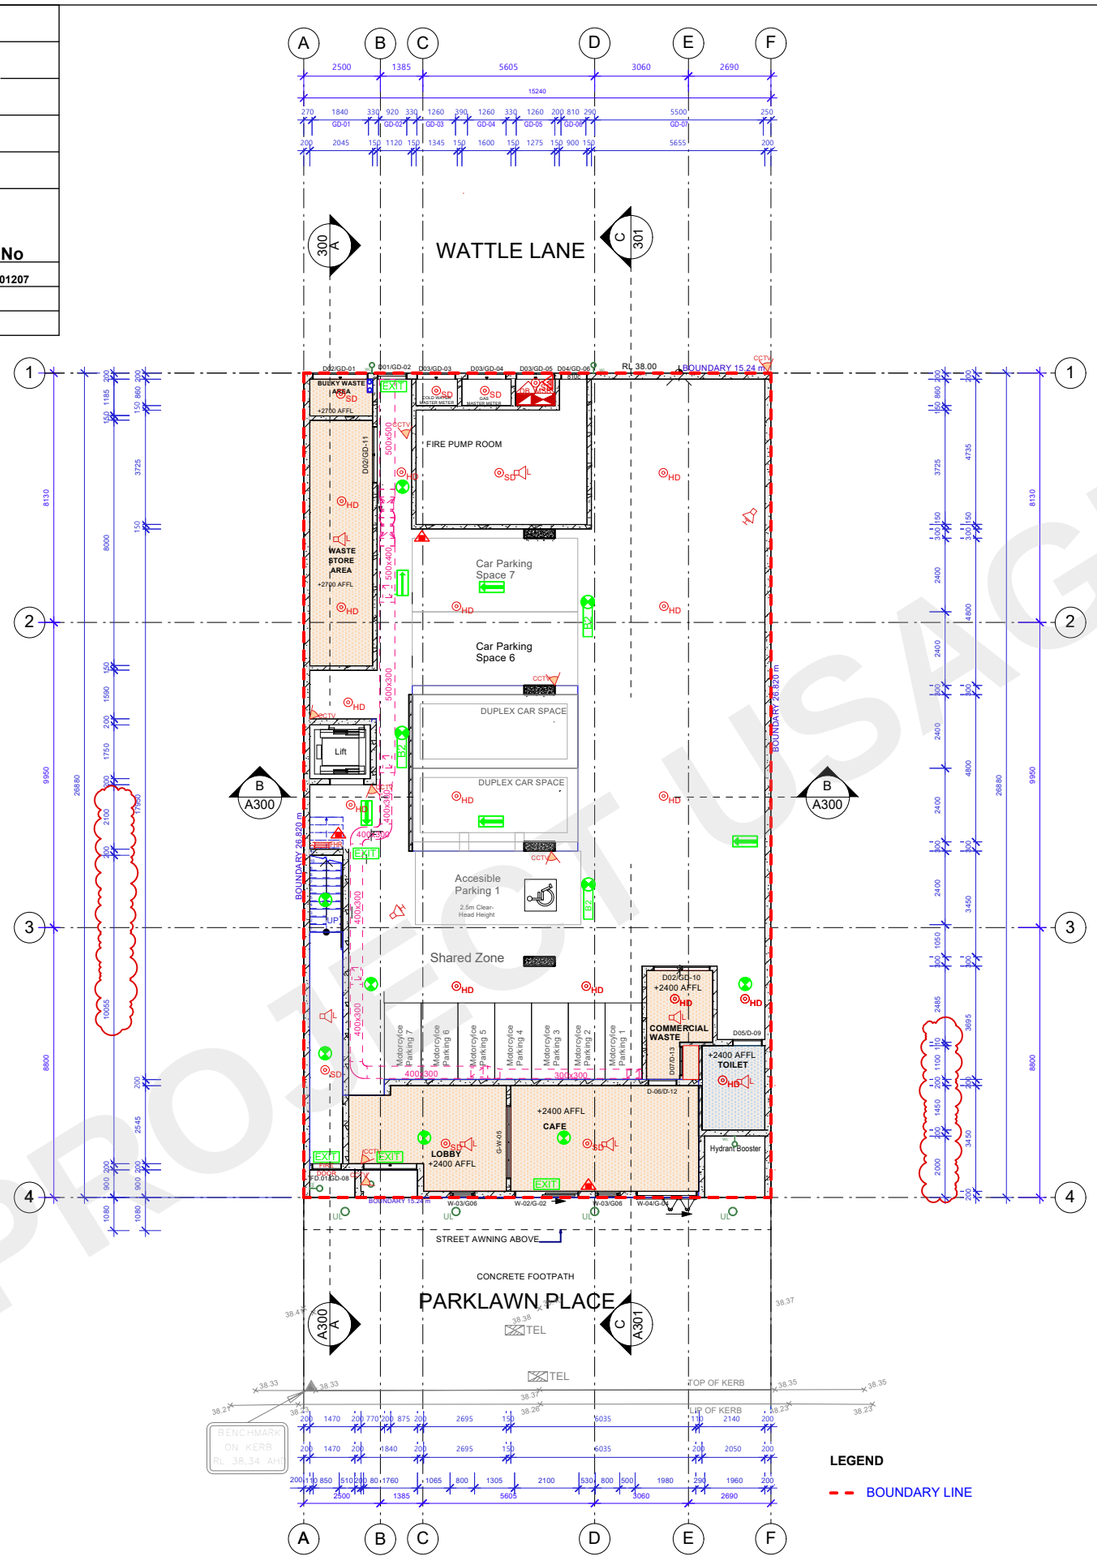

LEGEND

- SD — POINT-TYPE SMOKE DETECTOR TO COMPLY WITH AS 1670.1:2018 AND AS 7240.7:2018
- HD — POINT-TYPE HEAT DETECTOR IN ACCORDANCE WITH AS 1670.1:2018 AND AS 7240.5:2018
- SA — SMOKE ALARM TO COMPLY WITH AS 3786:2014 AND AS 1670.1:2018
- B2 — COMBINED, SUSTAINED EMERGENCY LUMINAIRE TO COMPLY WITH AS/NZS 2293.1:2018. CLASS B2 OR EQUIVALENT
- EMERGENCY LIGHT TO COMPLY WITH AS/NZS 2293.1:2018. CLASS E32 OR EQUIVALENT
- DIRECTION SIGN (DOUBLE SIDED) IN LINE WITH AS/NZS 2293.1:2018
- EXIT — EXIT SIGN IN ACCORDANCE WITH AS/NZS 2293.1:2018
- 2.5 KG ABE POWDER TYPE FIRE EXTINGUISHER TO COMPLY WITH AS 2444-2001. MIN. RATING 2A:40B:E OR EQUIVALENT
- 5 KG CARBON DIOXIDE (C02) TYPE FIRE EXTINGUISHER TO CONFORM WITH AS 2444-2001
- H — HORN SPEAKER IN LINE WITH AS 7240.24:2018
- L — 100 MM 5W 100V CELING MOUNTED SPEAKERS TO COMPLY WITH AS 1670.1:2018 AND AS 7240.24:2018
- MANUAL CALL POINT (MCP) COMPLYING WITH AS 1670.1:2018 AND AS ISO 7240.11:2018
- DB — DISTRIBUTION BOARD
- MSB — MAIN SWITCH BOARD
- +2700 AFFL — PROPOSED CEILING HEIGHT ABOVE FINISHED FLOOR LEVEL
- FIRE RESISTANT PLASTERBOARD CEILING - GYPROCK FYRCHEK 16 MM
- PLASTERBOARD CEILING FOR WET AREAS - GYPROCK AQUACHECK
- WL / UL — WALL LIGHTS - TO LIGHT EXTERNAL SPACES LIGHTING UNDER AWNING
- FHR — FIRE HOSE REEL
- CCTV — CCTV CAMERA

N

0 2 3 5 m

CONSTRUCTION CERTIFICATE NOTES:

GENERAL

1.ALL WORK SHALL COMPLY WITH THE NCC (BCA VOL 1 2025 EDITION), CONDITIONS OF CONSENT, AND THE RELEVANT AUSTRALIAN STANDARDS AS LISTED BELOW.
2. FOR CONSTRUCTION CERTIFICATE ONLY NOT FOR CONSTRUCTION. ALL DIMENSIONS SHALL BE VERIFIED ON SITE PRIOR TO COMMENCEMENT OF WORK. DO NOT SCALE DRAWINGS.
3.BYDA BEFORE YOU DIG FOR ANY UNDERGROUND SERVICES.WWW.BYDA.COM.AU
4. ANY DISCREPANCIES BETWEEN DRAWINGS, SITE CONDITIONS, OR SPECIFICATIONS SHALL BE REFERRED TO THE ARCHITECT BEFORE PROCEEDING.
5. DRAWINGS ARE TO BE READ IN CONJUNCTION WITH THE ARCHITECTURAL SPECIFICATION AND ALL CONSULTANT DRAWINGS AND SPECIFICATIONS, INCLUDING STRUCTURAL, CIVIL, HYDRAULIC, MECHANICAL, ELECTRICAL, FIRE, LANDSCAPE AND SECTION J DOCUMENTATION.
6. THE BUILDER SHALL CARRY OUT ALL WORK IN ACCORDANCE WITH: NCC (BCA VOL 1 2025), CONDITIONS OF DEVELOPMENT CONSENT, WHS REGULATION (NSW), AND RELEVANT AUSTRALIAN STANDARDS.
7. PROVIDE ADEQUATE PROTECTION TO EXISTING STRUCTURES, PUBLIC SPACES AND SERVICES DURING CONSTRUCTION.
8. THE BUILDER SHALL COORDINATE ALL TRADES AND ENSURE PENETRATIONS, SET-OUTS AND SERVICE ROUTES ARE ACCURATELY LOCATED.
9. ALL DIMENSIONS TO BE CHECKED ON SITE AND SETOUT BY A SURVEYOR PRIOR TO COMMENCEMENT OF CONSTRUCTION.

31.OUTDOOR LIGHTING TO BE INSTALLED IN ACCORDANCE WITH AS1158.0 AND AS/NZS 4282-2023

CONTROL OF OBSTRUCTURE EFFECTS OF OUTDOOR LIGHTING.

TEST PROJECT USAGE ONLY

No.	Date	Issue Notes
CC-A	02-Sep-26	FOR CC SUBMISSION

Consultant / Notes:
SURVEY BY
REGISTERED SURVEYORS
PO BOX

COPYRIGHT
THIS DRAWING IS THE PROPERTY OF LYLE MARSHALL AND PARTNERS P/L AND MAY ONLY BE USED FOR THE PURPOSE FOR WHICH IT WAS COMMISSIONED & IN ACCORDANCE WITH THE TERMS OF ENGAGEMENT FOR THAT COMMISSION. UNAUTHORISED USE OF THIS DRAWING IS PROHIBITED.

FOR CC SUBMISSION


NG PLAN

Design By: EMMC	Job No.: 5187-26		
Drawn By: EMMC	Scale: 1:200		
Reviewed By: EMMC	Date: 02-Sep-26	Sheet No.: A120 of	Issue: CC-A
Passed By: EMMC	Date of Issue:		

Regulated Design Record

Project Address:			
Project Title:			
Consent No:	DA18/0471.03	Body Corporate Reg No:	
Drawing Title:	LEVEL 1 REFLECTED CEILING PLAN	Drawing No:	5187-26-A121

Rev	Date dd.mm.yy	Description	DEP Full Name	Reg No
CC-A	02/09/26	FOR CC SUBMISSION	ERICA MARSHALL-EVANS	DEP 0001207

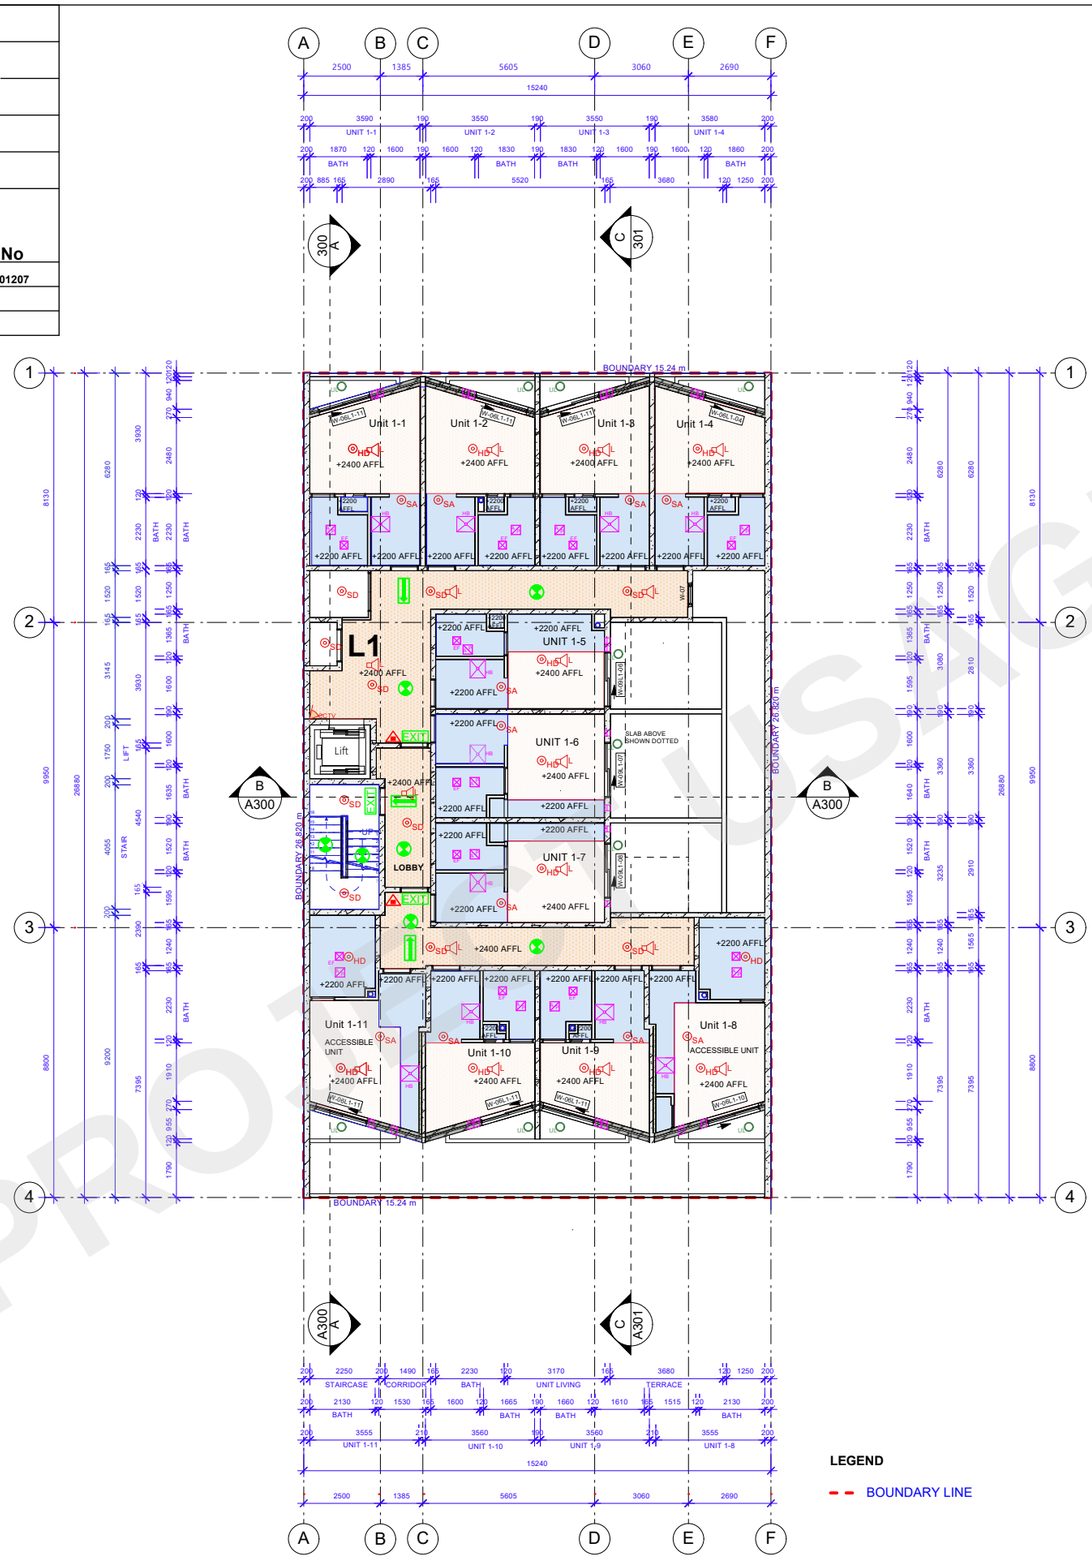

LEGEND

- SD — POINT-TYPE SMOKE DETECTOR TO COMPLY WITH AS 1670.1:2018 AND AS 7240.7:2018
- HD — POINT-TYPE HEAT DETECTOR IN ACCORDANCE WITH AS 1670.1:2018 AND AS 7240.5:2018
- SA — SMOKE ALARM TO COMPLY WITH AS 3786:2014 AND AS 1670.1:2018
- B2 — COMBINED, SUSTAINED EMERGENCY LUMINAIRE TO COMPLY WITH AS/NZS 2293.1:2018. CLASS B2 OR EQUIVALENT
- E32 — EMERGENCY LIGHT TO COMPLY WITH AS/NZS 2293.1:2018. CLASS E32 OR EQUIVALENT
- DIRECTION SIGN (DOUBLE SIDED) IN LINE WITH AS/NZS 2293.1:2018
- EXIT — EXIT SIGN IN ACCORDANCE WITH AS/NZS 2293.1:2018
- 2.5 KG ABE POWDER TYPE FIRE EXTINGUISHER TO COMPLY WITH AS 2444-2001. MIN. RATING 2A:40B:E OR EQUIVALENT
- 100 MM 5W 100V CELING MOUNTED SPEAKERS TO COMPLY WITH AS 1670.1:2018 AND AS 7240.24:2018
- AIR LOUVRE WITH INSECT SCREEN. DISCHARGE TO OUTSIDE THROUGH CEILING SPACE. REFER TO LOUVRE SCHEDULE
- KR — KITCHEN EXHAUST HOOD WITH NON- RETURN DAMPER, MINIMUM 40 L/S REFER TO KITCHEN EXHAUST HOOD SCHEDULE
- ACCESS PANEL
- TF — TOILET EXHAUST FAN WITH NON-RETURN DAMPER, MINIMUM 25 L/S REFER TO TOILET EXHAUST FAN SCHEDULE
- +2700 AFFL — PROPOSED CEILING HEIGHT ABOVE FINISHED FLOOR LEVEL
- FIRE RESISTANT PLASTERBOARD CEILING - GYPROCK FYRCHEK 16 MM
- PLASTERBOARD CEILING FOR WET AREAS - GYPROCK AQUACHECK
- UC — EXTERNAL SOFFIT LIGHTING
- CCTV — CCTV CAMERA

N

0 2 3 5 m

LEGEND

BOUNDARY LINE

CONSTRUCTION CERTIFICATE NOTES:

GENERAL

1.ALL WORK SHALL COMPLY WITH THE NCC (BCA VOL 1 2025 EDITION), CONDITIONS OF CONSENT, AND THE RELEVANT AUSTRALIAN STANDARDS AS LISTED BELOW.
2. FOR CONSTRUCTION CERTIFICATE ONLY NOT FOR CONSTRUCTION. ALL DIMENSIONS SHALL BE VERIFIED ON SITE PRIOR TO COMMENCEMENT OF WORK. DO NOT SCALE DRAWINGS.
3.BYDA BEFORE YOU DIG FOR ANY UNDERGROUND SERVICES.WWW.BYDA.COM.AU
4. ANY DISCREPANCIES BETWEEN DRAWINGS, SITE CONDITIONS, OR SPECIFICATIONS SHALL BE REFERRED TO THE ARCHITECT BEFORE PROCEEDING.
5. DRAWINGS ARE TO BE READ IN CONJUNCTION WITH THE ARCHITECTURAL SPECIFICATION AND ALL CONSULTANT DRAWINGS AND SPECIFICATIONS, INCLUDING STRUCTURAL, CIVIL, HYDRAULIC, MECHANICAL, ELECTRICAL, FIRE, LANDSCAPE AND SECTION J DOCUMENTATION.
6. THE BUILDER SHALL CARRY OUT ALL WORK IN ACCORDANCE WITH: NCC (BCA VOL 1 2025), CONDITIONS OF DEVELOPMENT CONSENT, WHS REGULATION (NSW), AND RELEVANT AUSTRALIAN STANDARDS.
7. PROVIDE ADEQUATE PROTECTION TO EXISTING STRUCTURES, PUBLIC SPACES AND SERVICES DURING CONSTRUCTION.
8. THE BUILDER SHALL COORDINATE ALL TRADES AND ENSURE PENETRATIONS, SET-OUTS AND SERVICE ROUTES ARE ACCURATELY LOCATED.
9. ALL DIMENSIONS TO BE CHECKED ON SITE AND SETOUT BY A SURVEYOR PRIOR TO COMMENCEMENT OF CONSTRUCTION.

31.OUTDOOR LIGHTING TO BE INSTALLED IN ACCORDANCE WITH AS1158.0 AND AS/NZS 4282-2023

CONTROL OF OBSTRUCTURE EFFECTS OF OUTDOOR LIGHTING.

TEST PROJECT
FOR USAGE ONLY

No.	Date	Issue Notes
CC-A	02-Sep-26	FOR CC SUBMISSION

Consultant / Notes:
SURVEY BY
REGISTERED SURVEYORS
PO BOX

COPYRIGHT
THIS DRAWING IS THE PROPERTY OF LYLE MARSHALL AND PARTNERS P/L AND MAY ONLY BE USED FOR THE PURPOSE FOR WHICH IT WAS COMMISSIONED & IN ACCORDANCE WITH THE TERMS OF ENGAGEMENT FOR THAT COMMISSION. UNAUTHORISED USE OF THIS DRAWING IS PROHIBITED.

Date 4-9-26
File name


FOR CC SUBMISSION

Design By: EMMC	Job No. 5187-26		
Drawn By: EMMC	Scale 1:200		
Reviewed By: EMMC	Date 02-Sep-26	Sheet No. A121 of	Issue CC-A
Passed By: EMMC	Date of Issue		

Regulated Design Record

Project Address:			
Project Title:			
Consent No:	DA18/0471.03	Body Corporate Reg No:	
Drawing Title:	LEVEL 2 REFLECTED CEILING PLAN	Drawing No:	5187-26-A122

Rev	Date dd.mm.yy	Description	DEP Full Name	Reg No
CC-A	02/09/26	FOR CC SUBMISSION	ERICA MARSHALL-EVANS	DEP 0001207

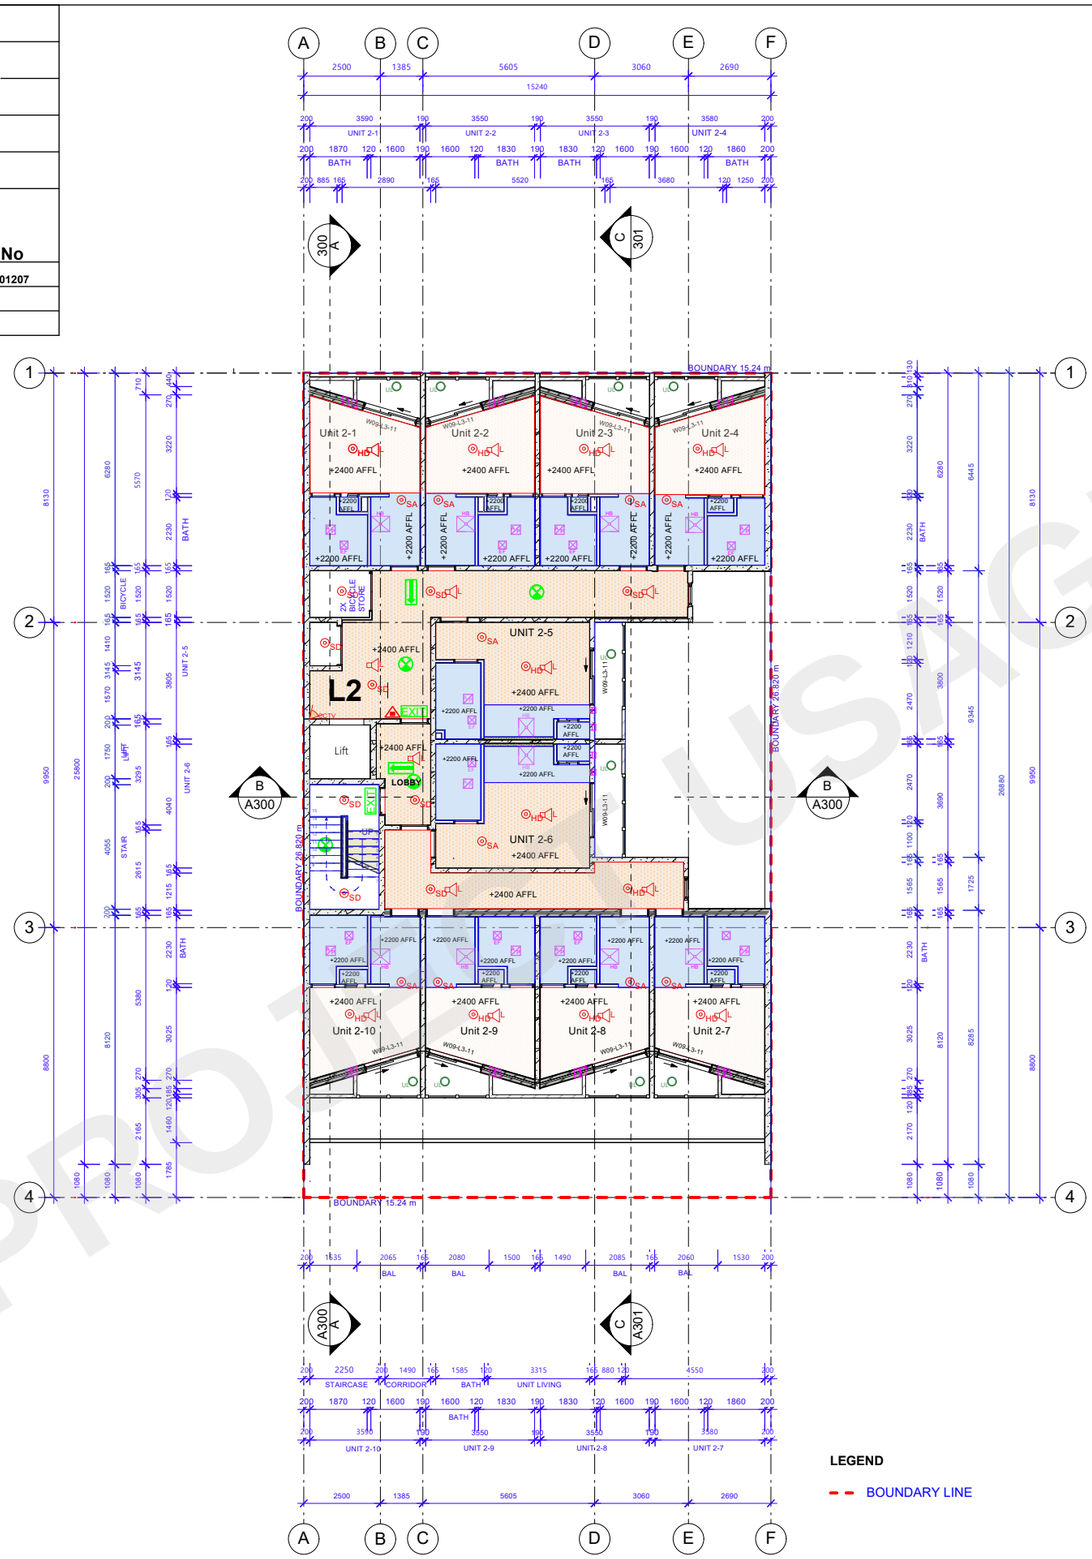

LEGEND

- SD — POINT-TYPE SMOKE DETECTOR TO COMPLY WITH AS 1670.1:2018 AND AS 7240.7:2018
- HD — POINT-TYPE HEAT DETECTOR IN ACCORDANCE WITH AS 1670.1:2018 AND AS 7240.5:2018
- SA — SMOKE ALARM TO COMPLY WITH AS 3786:2014 AND AS 1670.1:2018
- B2 — COMBINED, SUSTAINED EMERGENCY LUMINAIRE TO COMPLY WITH AS/NZS 2293.1:2018. CLASS B2 OR EQUIVALENT
- EMERGENCY LIGHT TO COMPLY WITH AS/NZS 2293.1:2018. CLASS E32 OR EQUIVALENT
- DIRECTION SIGN (DOUBLE SIDED) IN LINE WITH AS/NZS 2293.1:2018
- EXIT — EXIT SIGN IN ACCORDANCE WITH AS/NZS 2293.1:2018
- 2.5 KG ABE POWDER TYPE FIRE EXTINGUISHER TO COMPLY WITH AS 2444-2001. MIN. RATING 2A:40B:E OR EQUIVALENT
- 100 MM 5W 100V CELING MOUNTED SPEAKERS TO COMPLY WITH AS 1670.1:2018 AND AS 7240.24:2018
- AIR LOUVRE WITH INSECT SCREEN. DISCHARGE TO OUTSIDE THROUGH CEILING SPACE. REFER TO LOUVRE SCHEDULE
- KITCHEN EXHAUST HOOD WITH NON- RETURN DAMPER, MINIMUM 40 L/S REFER TO KITCHEN EXHAUST HOOD SCHEDULE
- ACCESS PANEL
- TOILET EXHAUST FAN WITH NON-RETURN DAMPER, MINIMUM 25 L/S REFER TO TOILET EXHAUST FAN SCHEDULE
- +2700 AFFL — PROPOSED CEILING HEIGHT ABOVE FINISHED FLOOR LEVEL
- FIRE RESISTANT PLASTERBOARD CEILING - GYPROCK FYRCHEK 16 MM
- PLASTERBOARD CEILING FOR WET AREAS - GYPROCK AQUACHECK
- UO — EXTERNAL SOFFIT LIGHTING
- CCTV — CCTV CAMERA

N

0 2 3 5 m

LEGEND

- BOUNDARY LINE

CONSTRUCTION CERTIFICATE NOTES:

GENERAL

1.ALL WORK SHALL COMPLY WITH THE NCC (BCA VOL 1 2025 EDITION), CONDITIONS OF CONSENT, AND THE RELEVANT AUSTRALIAN STANDARDS AS LISTED BELOW.
2. FOR CONSTRUCTION CERTIFICATE ONLY NOT FOR CONSTRUCTION. ALL DIMENSIONS SHALL BE VERIFIED ON SITE PRIOR TO COMMENCEMENT OF WORK. DO NOT SCALE DRAWINGS.
3.BYDA BEFORE YOU DIG FOR ANY UNDERGROUND SERVICES.WWW.BYDA.COM.AU
4. ANY DISCREPANCIES BETWEEN DRAWINGS, SITE CONDITIONS, OR SPECIFICATIONS SHALL BE REFERRED TO THE ARCHITECT BEFORE PROCEEDING.
5. DRAWINGS ARE TO BE READ IN CONJUNCTION WITH THE ARCHITECTURAL SPECIFICATION AND ALL CONSULTANT DRAWINGS AND SPECIFICATIONS, INCLUDING STRUCTURAL, CIVIL, HYDRAULIC, MECHANICAL, ELECTRICAL, FIRE, LANDSCAPE AND SECTION J DOCUMENTATION.
6. THE BUILDER SHALL CARRY OUT ALL WORK IN ACCORDANCE WITH: NCC (BCA VOL 1 2025), CONDITIONS OF DEVELOPMENT CONSENT, WHS REGULATION (NSW), AND RELEVANT AUSTRALIAN STANDARDS.
7. PROVIDE ADEQUATE PROTECTION TO EXISTING STRUCTURES, PUBLIC SPACES AND SERVICES DURING CONSTRUCTION.
8. THE BUILDER SHALL COORDINATE ALL TRADES AND ENSURE PENETRATIONS, SET-OUTS AND SERVICE ROUTES ARE ACCURATELY LOCATED.
9. ALL DIMENSIONS TO BE CHECKED ON SITE AND SETOUT BY A SURVEYOR PRIOR TO COMMENCEMENT OF CONSTRUCTION.

31.OUTDOOR LIGHTING TO BE INSTALLED IN ACCORDANCE WITH AS1158.0 AND AS/NZS 4282-2023 CONTROL OF OBSTRUCTURE EFFECTS OF OUTDOOR LIGHTING.

TEST PROJECT USAGE ONLY

No.	Date	Issue Notes
CC-A	02-Sep-26	FOR CC SUBMISSION

Consultant / Notes:
SURVEY BY
REGISTERED SURVEYORS
PO BOX

COPYRIGHT
THIS DRAWING IS THE PROPERTY OF LYLE MARSHALL AND PARTNERS P/L AND MAY ONLY BE USED FOR THE PURPOSE FOR WHICH IT WAS COMMISSIONED & IN ACCORDANCE WITH THE TERMS OF ENGAGEMENT FOR THAT COMMISSION. UNAUTHORISED USE OF THIS DRAWING IS PROHIBITED.

Date: 4-9-26
File name:


FOR CC SUBMISSION

Design By: EMMC	Job No.: 5187-26		
Drawn By: EMMC	Scale: 1:200		
Reviewed By: EMMC	Date: 02-Sep-26	Sheet No.: A122 of	Issue: CC-A
Passed By: EMMC	Date of Issue		

Regulated Design Record

Project Address:			
Project Title:			
Consent No:	DA18/0471.03	Body Corporate Reg No:	
Drawing Title:	LEVEL 3 REFLECTED CEILING PLAN	Drawing No:	5187-26-A123

Rev	Date dd.mm.yy	Description	DEP Full Name	Reg No
CC-A	02/09/26	FOR CC SUBMISSION	ERICA MARSHALL-EVANS	DEP 0001207

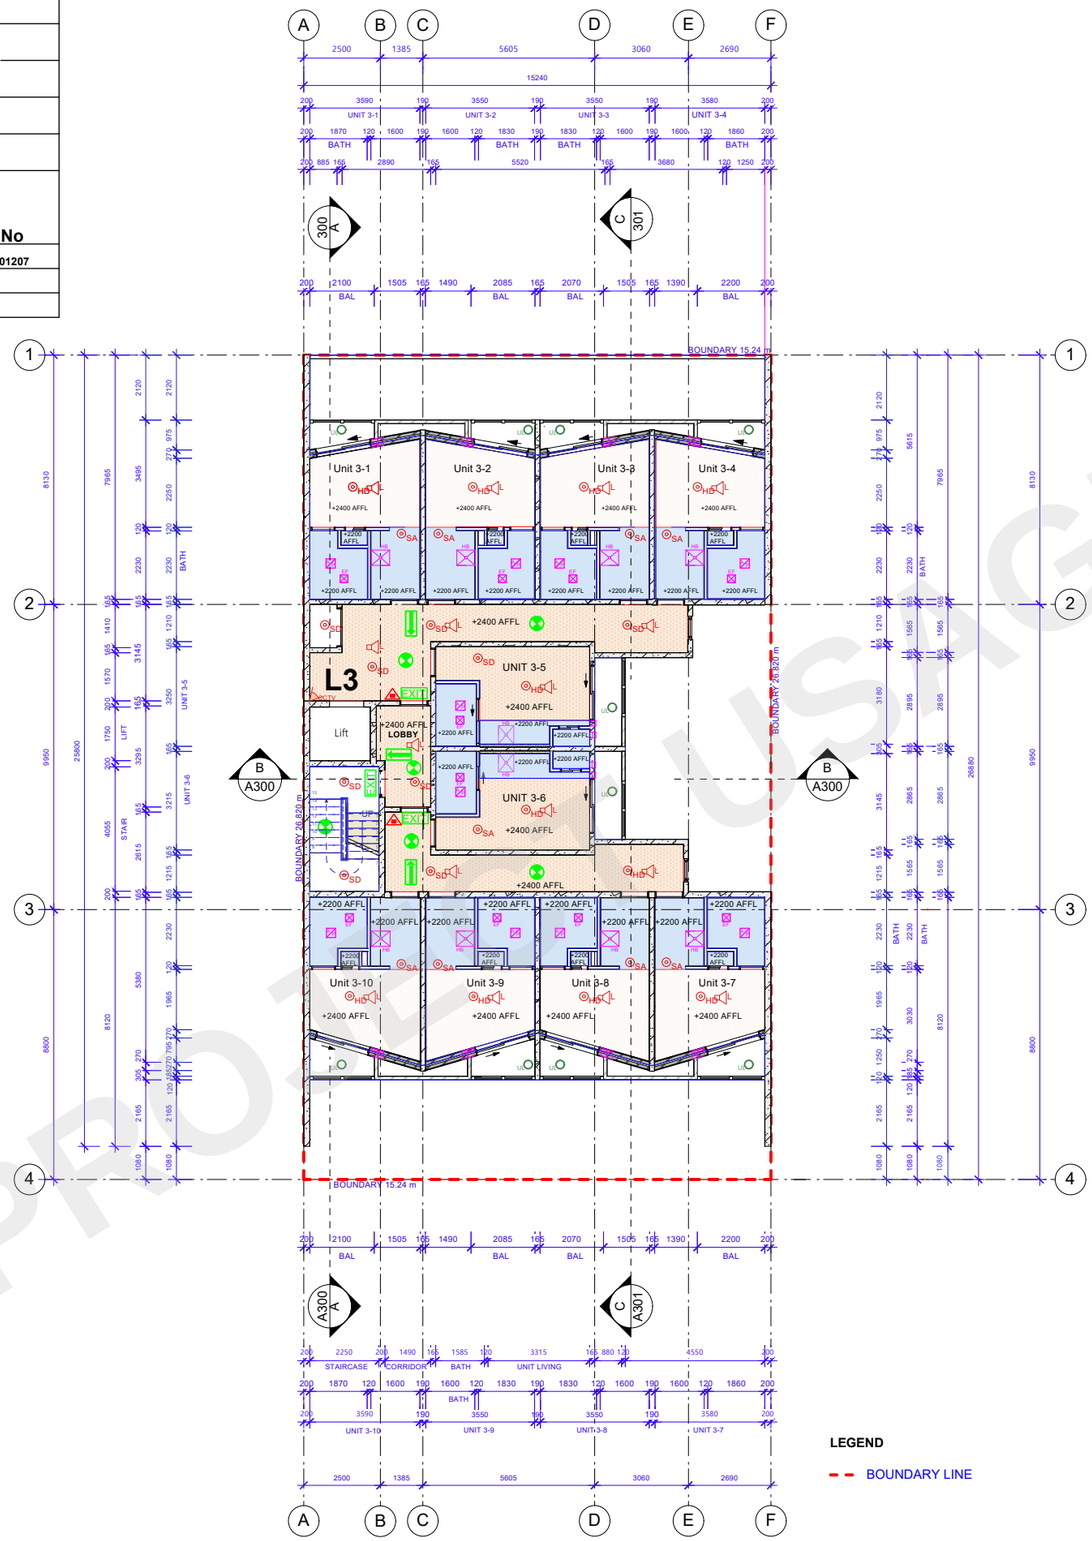

LEGEND

- SD — POINT-TYPE SMOKE DETECTOR TO COMPLY WITH AS 1670.1:2018 AND AS 7240.7:2018
- HD — POINT-TYPE HEAT DETECTOR IN ACCORDANCE WITH AS 1670.1:2018 AND AS 7240.5:2018
- SA — SMOKE ALARM TO COMPLY WITH AS 3786:2014 AND AS 1670.1:2018
- B2 — COMBINED, SUSTAINED EMERGENCY LUMINAIRE TO COMPLY WITH AS/NZS 2293.1:2018. CLASS B2 OR EQUIVALENT
- EMERGENCY LIGHT TO COMPLY WITH AS/NZS 2293.1:2018. CLASS E32 OR EQUIVALENT
- DIRECTION SIGN (DOUBLE SIDED) IN LINE WITH AS/NZS 2293.1:2018
- EXIT — EXIT SIGN IN ACCORDANCE WITH AS/NZS 2293.1:2018
- 2.5 KG ABE POWDER TYPE FIRE EXTINGUISHER TO COMPLY WITH AS 2444-2001. MIN. RATING 2A:40B:E OR EQUIVALENT
- L — 100 MM 5W 100V CELING MOUNTED SPEAKERS TO COMPLY WITH AS 1670.1:2018 AND AS 7240.24:2018
- AIR LOUVRE WITH INSECT SCREEN. DISCHARGE TO OUTSIDE THROUGH CEILING SPACE. REFER TO LOUVRE SCHEDULE
- HR — KITCHEN EXHAUST HOOD WITH NON- RETURN DAMPER, MINIMUM 40 L/S REFER TO KITCHEN EXHAUST HOOD SCHEDULE
- ACCESS PANEL
- EF — TOILET EXHAUST FAN WITH NON-RETURN DAMPER, MINIMUM 25 L/S REFER TO TOILET EXHAUST FAN SCHEDULE
- +2400 AFFL — PROPOSED CEILING HEIGHT ABOVE FINISHED FLOOR LEVEL
- FIRE RESISTANT PLASTERBOARD CEILING - GYPROCK FYRCHEK 16 MM
- PLASTERBOARD CEILING FOR WET AREAS - GYPROCK AQUACHECK
- UL — EXTERNAL SOFFIT LIGHTING
- CCTV — CCTV CAMERA

N

0 2 3 5 m

CONSTRUCTION CERTIFICATE NOTES:

GENERAL

1.ALL WORK SHALL COMPLY WITH THE NCC (BCA VOL 1 2025 EDITION), CONDITIONS OF CONSENT, AND THE RELEVANT AUSTRALIAN STANDARDS AS LISTED BELOW.
2. FOR CONSTRUCTION CERTIFICATE ONLY NOT FOR CONSTRUCTION. ALL DIMENSIONS SHALL BE VERIFIED ON SITE PRIOR TO COMMENCEMENT OF WORK. DO NOT SCALE DRAWINGS.
3.BYDA BEFORE YOU DIG FOR ANY UNDERGROUND SERVICES.WWW.BYDA.COM.AU
4. ANY DISCREPANCIES BETWEEN DRAWINGS, SITE CONDITIONS, OR SPECIFICATIONS SHALL BE REFERRED TO THE ARCHITECT BEFORE PROCEEDING.
5. DRAWINGS ARE TO BE READ IN CONJUNCTION WITH THE ARCHITECTURAL SPECIFICATION AND ALL CONSULTANT DRAWINGS AND SPECIFICATIONS, INCLUDING STRUCTURAL, CIVIL, HYDRAULIC, MECHANICAL, ELECTRICAL, FIRE, LANDSCAPE AND SECTION J DOCUMENTATION.
6. THE BUILDER SHALL CARRY OUT ALL WORK IN ACCORDANCE WITH: NCC (BCA VOL 1 2025), CONDITIONS OF DEVELOPMENT CONSENT, WHS REGULATION (NSW), AND RELEVANT AUSTRALIAN STANDARDS.
7. PROVIDE ADEQUATE PROTECTION TO EXISTING STRUCTURES, PUBLIC SPACES AND SERVICES DURING CONSTRUCTION.
8. THE BUILDER SHALL COORDINATE ALL TRADES AND ENSURE PENETRATIONS, SET-OUTS AND SERVICE ROUTES ARE ACCURATELY LOCATED.
9. ALL DIMENSIONS TO BE CHECKED ON SITE AND SETOUT BY A SURVEYOR PRIOR TO COMMENCEMENT OF CONSTRUCTION.

31.OUTDOOR LIGHTING TO BE INSTALLED IN ACCORDANCE WITH AS1158.0 AND AS/NZS 4282-2023

CONTROL OF OBSTRUCTURE EFFECTS OF OUTDOOR LIGHTING.

TEST PROJECT
NOT FOR USAGE ONLY

No.	Date	Issue Notes
CC-A	02-Sep-26	FOR CC SUBMISSION

Consultant / Notes:
SURVEY BY
REGISTERED SURVEYORS
PO BOX

COPYRIGHT
THIS DRAWING IS THE PROPERTY OF LYLE MARSHALL AND PARTNERS P/L AND MAY ONLY BE USED FOR THE PURPOSE FOR WHICH IT WAS COMMISSIONED & IN ACCORDANCE WITH THE TERMS OF ENGAGEMENT FOR THAT COMMISSION. UNAUTHORISED USE OF THIS DRAWING IS PROHIBITED.


FOR CC SUBMISSION

Design By: EMMC	Job No.: 5187-26		
Drawn By: EMMC	Scale: 1:200		
Reviewed By: EMMC	Date: 02-Sep-26	Sheet No.: A123 of	Issue: CC-A
Passed By: EMMC	Date of Issue:		

Regulated Design Record

Project Address:	
Project Title:	
Consent No: DA18/0471.03	Body Corporate Reg No:
Drawing Title: LEVEL 4 REFLECTED CEILING PLAN	Drawing No: 5187-26-A124

Rev	Date dd.mm.yy	Description	DEP Full Name	Reg No
CC-A	02/09/26	FOR CC SUBMISSION	ERICA MARSHALL-EVANS	DEP 0001207

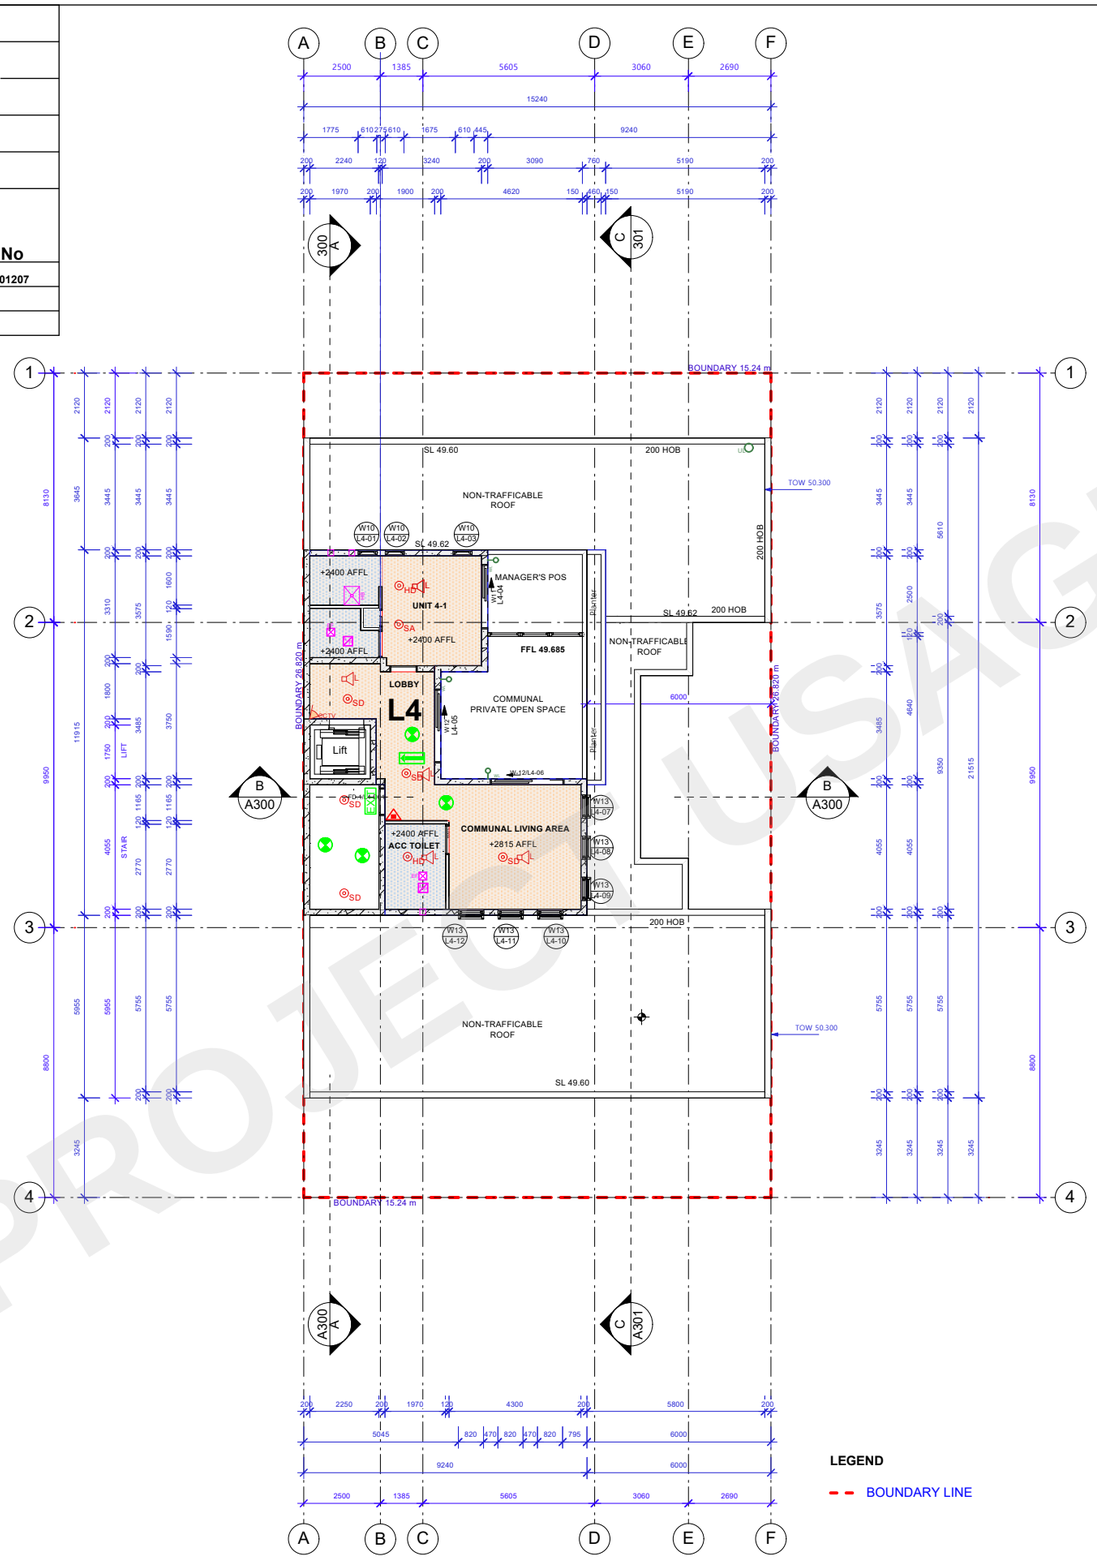

LEGEND

- BOUNDARY LINE

LEGEND

- SD — POINT-TYPE SMOKE DETECTOR TO COMPLY WITH AS 1670.1:2018 AND AS 7240.7:2018
- HD — POINT-TYPE HEAT DETECTOR IN ACCORDANCE WITH AS 1670.1:2018 AND AS 7240.5:2018
- SA — SMOKE ALARM TO COMPLY WITH AS 3786:2014 AND AS 1670.1:2018
- B2 — COMBINED, SUSTAINED EMERGENCY LUMINAIRE TO COMPLY WITH AS/NZS 2293.1:2018. CLASS B2 OR EQUIVALENT
- EMERGENCY LIGHT TO COMPLY WITH AS/NZS 2293.1:2018. CLASS E32 OR EQUIVALENT
- DIRECTION SIGN (DOUBLE SIDED) IN LINE WITH AS/NZS 2293.1:2018
- EXIT — EXIT SIGN IN ACCORDANCE WITH AS/NZS 2293.1:2018
- 2.5 KG ABE POWDER TYPE FIRE EXTINGUISHER TO COMPLY WITH AS 2444-2001. MIN. RATING 2A:40B:E OR EQUIVALENT
- 100 MM 5W 100V CELING MOUNTED SPEAKERS TO COMPLY WITH AS 1670.1:2018 AND AS 7240.24:2018
- AIR LOUVRE WITH INSECT SCREEN. DISCHARGE TO OUTSIDE THROUGH CEILING SPACE. REFER TO LOUVRE SCHEDULE
- KITCHEN EXHAUST HOOD WITH NON- RETURN DAMPER, MINIMUM 40 L/S REFER TO KITCHEN EXHAUST HOOD SCHEDULE
- ACCESS PANEL
- TOILET EXHAUST FAN WITH NON-RETURN DAMPER, MINIMUM 25 L/S REFER TO TOILET EXHAUST FAN SCHEDULE
- +2700 AFFL — PROPOSED CEILING HEIGHT ABOVE FINISHED FLOOR LEVEL
- FIRE RESISTANT PLASTERBOARD CEILING - GYPROCK FYRCHEK 16 MM
- PLASTERBOARD CEILING FOR WET AREAS - GYPROCK AQUACHECK
- WL — WALL LIGHTS - TO LIGHT EXTERNAL SPACES
- CCTV — CCTV CAMERA

N

0 2 3 5 m

CONSTRUCTION CERTIFICATE NOTES:

GENERAL

1.ALL WORK SHALL COMPLY WITH THE NCC (BCA VOL 1 2025 EDITION), CONDITIONS OF CONSENT, AND THE RELEVANT AUSTRALIAN STANDARDS AS LISTED BELOW.
2. FOR CONSTRUCTION CERTIFICATE ONLY NOT FOR CONSTRUCTION. ALL DIMENSIONS SHALL BE VERIFIED ON SITE PRIOR TO COMMENCEMENT OF WORK. DO NOT SCALE DRAWINGS.
3.BYDA BEFORE YOU DIG FOR ANY UNDERGROUND SERVICES.WWW.BYDA.COM.AU
4. ANY DISCREPANCIES BETWEEN DRAWINGS, SITE CONDITIONS, OR SPECIFICATIONS SHALL BE REFERRED TO THE ARCHITECT BEFORE PROCEEDING.
5. DRAWINGS ARE TO BE READ IN CONJUNCTION WITH THE ARCHITECTURAL SPECIFICATION AND ALL CONSULTANT DRAWINGS AND SPECIFICATIONS, INCLUDING STRUCTURAL, CIVIL, HYDRAULIC, MECHANICAL, ELECTRICAL, FIRE, LANDSCAPE AND SECTION J DOCUMENTATION.
6. THE BUILDER SHALL CARRY OUT ALL WORK IN ACCORDANCE WITH: NCC (BCA VOL 1 2025), CONDITIONS OF DEVELOPMENT CONSENT, WHS REGULATION (NSW), AND RELEVANT AUSTRALIAN STANDARDS.
7. PROVIDE ADEQUATE PROTECTION TO EXISTING STRUCTURES, PUBLIC SPACES AND SERVICES DURING CONSTRUCTION.
8. THE BUILDER SHALL COORDINATE ALL TRADES AND ENSURE PENETRATIONS, SET-OUTS AND SERVICE ROUTES ARE ACCURATELY LOCATED.
9. ALL DIMENSIONS TO BE CHECKED ON SITE AND SETOUT BY A SURVEYOR PRIOR TO COMMENCEMENT OF CONSTRUCTION.

31.OUTDOOR LIGHTING TO BE INSTALLED IN ACCORDANCE WITH AS1158.0 AND AS/NZS 4282-2023

CONTROL OF OBSTRUCTURE EFFECTS OF OUTDOOR LIGHTING.

TEST PROJECT USAGE ONLY

FOR CC SUBMISSION

No.	Date	Issue Notes
CC-A	02-Sep-26	FOR CC SUBMISSION

Consultant / Notes:
SURVEY BY
REGISTERED SURVEYORS
PO BOX

COPYRIGHT
THIS DRAWING IS THE PROPERTY OF LYLE MARSHALL AND PARTNERS P/L AND MAY ONLY BE USED FOR THE PURPOSE FOR WHICH IT WAS COMMISSIONED & IN ACCORDANCE WITH THE TERMS OF ENGAGEMENT FOR THAT COMMISSION. UNAUTHORISED USE OF THIS DRAWING IS PROHIBITED.


Design By: EMMC	Job No.: 5187-26		
Drawn By: EMMC	Scale: 1:200		
Reviewed By: EMMC	Date: 02-Sep-26	Sheet No.: A124 of	Issue: CC-A
Passed By: EMMC	Date of Issue:		

SAMPLE PROJECT A - ARCHITECTURAL - RECRUITMENT ASSESSMENT ONLY


Regulated Design Record

Project Address:			
Project Title:			
Consent No: DA18/0471.03		Body Corporate Reg No:	
Drawing Title: ELEVATIONS - SHEET 1		Drawing No: 5187-26-A200	

Rev	Date dd.mm.yy	Description	DEP Full Name	Reg No
CC-A	02/09/26	FOR CC SUBMISSION	ERICA MARSHALL-EVANS	DEP 0001207

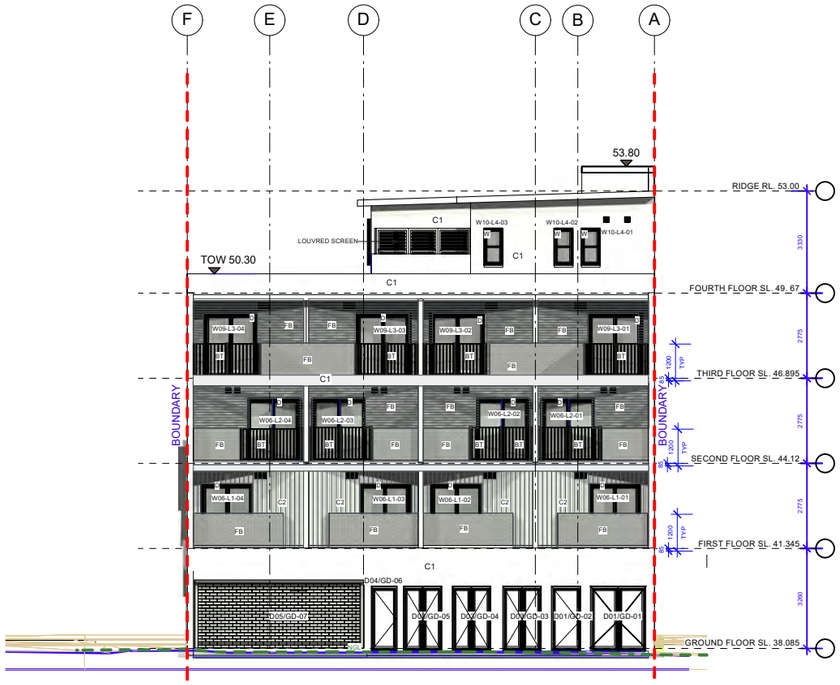

NORTH FACING ELEVATION
scale 1:200

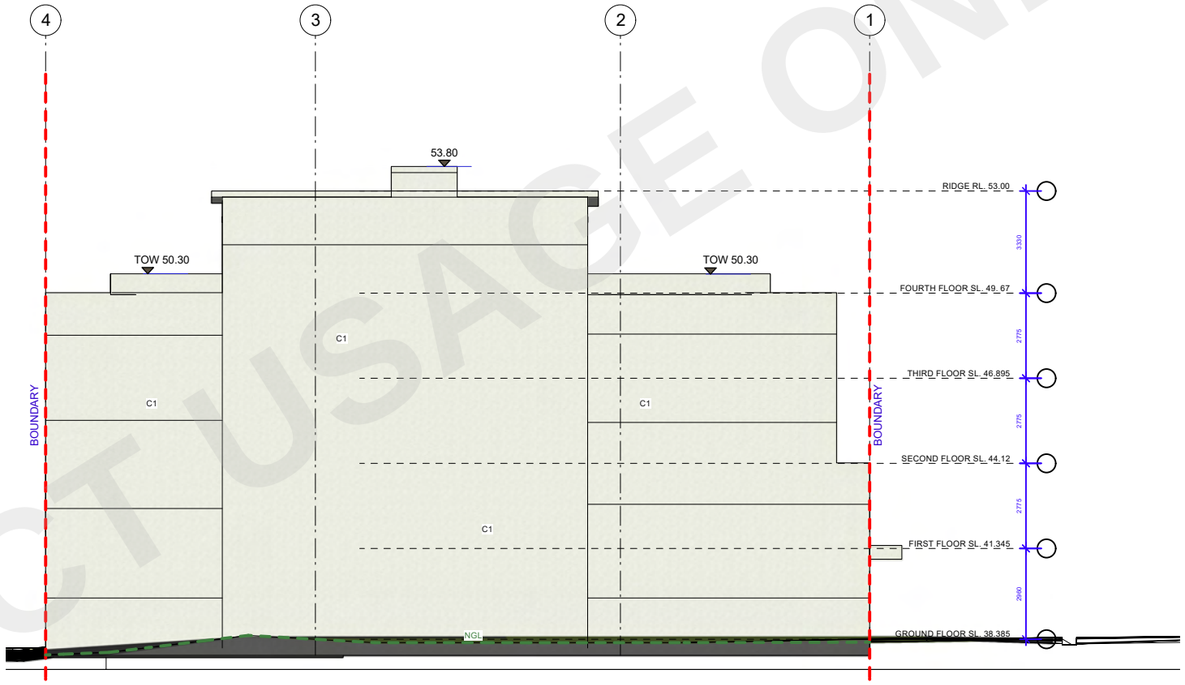

WEST FACING ELEVATION
scale 1:200

CONSTRUCTION CERTIFICATE NOTES:

GENERAL

1.ALL WORK SHALL COMPLY WITH THE NCC (BCA VOL 1 2025 EDITION), CONDITIONS OF CONSENT, AND THE RELEVANT AUSTRALIAN STANDARDS AS LISTED BELOW.
2. FOR CONSTRUCTION CERTIFICATE ONLY NOT FOR CONSTRUCTION. ALL DIMENSIONS SHALL BE VERIFIED ON SITE PRIOR TO COMMENCEMENT OF WORK. DO NOT SCALE DRAWINGS.
3.BYDA BEFORE YOU DIG FOR ANY UNDERGROUND SERVICES.WWW.BYDA.COM.AU
4. ANY DISCREPANCIES BETWEEN DRAWINGS, SITE CONDITIONS, OR SPECIFICATIONS SHALL BE REFERRED TO THE ARCHITECT BEFORE PROCEEDING.
5. DRAWINGS ARE TO BE READ IN CONJUNCTION WITH THE ARCHITECTURAL SPECIFICATION AND ALL CONSULTANT DRAWINGS AND SPECIFICATIONS, INCLUDING STRUCTURAL, CIVIL, HYDRAULIC, MECHANICAL, ELECTRICAL, FIRE, LANDSCAPE AND SECTION J DOCUMENTATION.
6. THE BUILDER SHALL CARRY OUT ALL WORK IN ACCORDANCE WITH: NCC (BCA VOL 1 2025), CONDITIONS OF DEVELOPMENT CONSENT, WHS REGULATION (NSW), AND RELEVANT AUSTRALIAN STANDARDS.
7. PROVIDE ADEQUATE PROTECTION TO EXISTING STRUCTURES, PUBLIC SPACES AND SERVICES DURING CONSTRUCTION.
8. THE BUILDER SHALL COORDINATE ALL TRADES AND ENSURE PENETRATIONS, SET-OUTS AND SERVICE ROUTES ARE ACCURATELY LOCATED.
9. ALL DIMENSIONS TO BE CHECKED ON SITE AND SETOUT BY A SURVEYOR PRIOR TO COMMENCEMENT OF CONSTRUCTION.

LEGEND

GD-06	DOOR NUMBERS
W06	WINDOW NUMBERS
W	BLACK ALUMINIUM FRAMED WINDOW
D	BLACK ALUMINIUM FRAMED DOOR
FB	DARK GREY FACE BRICK
C2	PAINTED V-GROOVE PANELS
C1	PAINTED CONCRETE PANELS
BT	BLACK POWDERCOATED BALUSTRADE
L	BLACK ALUMINIUM FRAMED LOUVRES
	AMENDMENTS FOR CC BY LMP
	BOUNDARY LINE
NGL	NATURAL GROUND LEVEL

0 2 3 5 m

TEST PROJECT USAGE ONLY

No.	Date	Issue Notes
CC-A	02-Sep-26	FOR CC SUBMISSION

Consultant / Notes:
Survey Prepared by Total Surveying Solutions
ARTARMON.CAMDEN, MANLYVALE


COPYRIGHT
THIS DRAWING IS THE PROPERTY OF LYLE MARSHALL AND PARTNERS P/L AND MAY O BE USED FOR THE PURPOSE FOR WHICH IT WAS COMMISSIONED & IN ACCORDANCE THE TERMS OF ENGAGEMENT FOR THAT COMMISSION. UNAUTHORISED USE OF THIS DRAWING IS PROHIBITED.

FOR CC SUBMISSION


Design By	Job No. 5187-26		
Drawn By EMMC	Scale 1:200		
Reviewed By	Date 02-Sep-26	Sheet No. A200 of	Issue CC-A
Passed By	Date of Issue		

Regulated Design Record			
Project Address:			
Project Title:			
Consent No: DA18/0471.03		Body Corporate Reg No:	
Drawing Title: ELEVATIONS - SHEET 2		Drawing No: 5187-26-A201	

Rev	Date dd.mm.yy	Description	DEP Full Name	Reg No
CC-A	02/09/26	FOR CC SUBMISSION	ERICA MARSHALL-EVANS	DEP 0001207

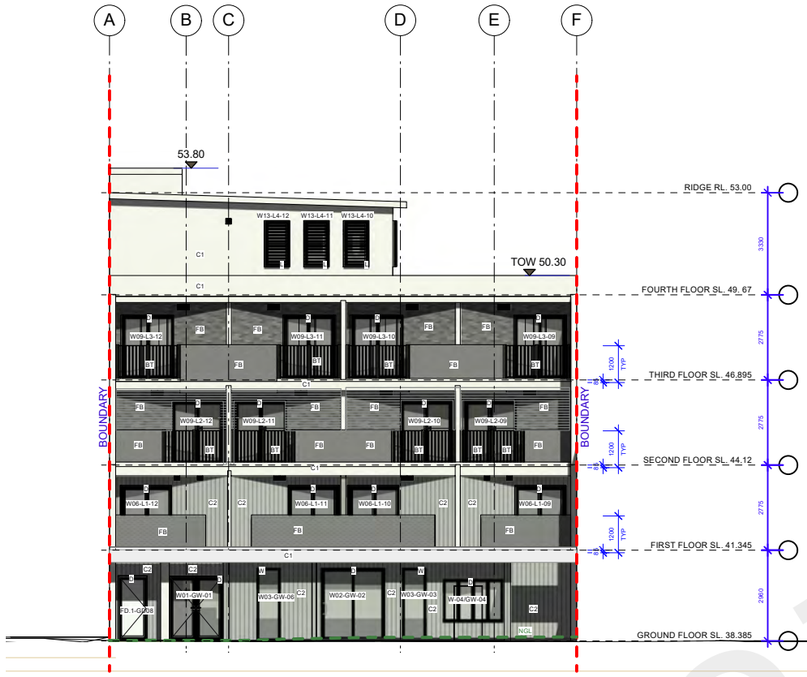

SOUTH FACING ELEVATION
scale 1:200

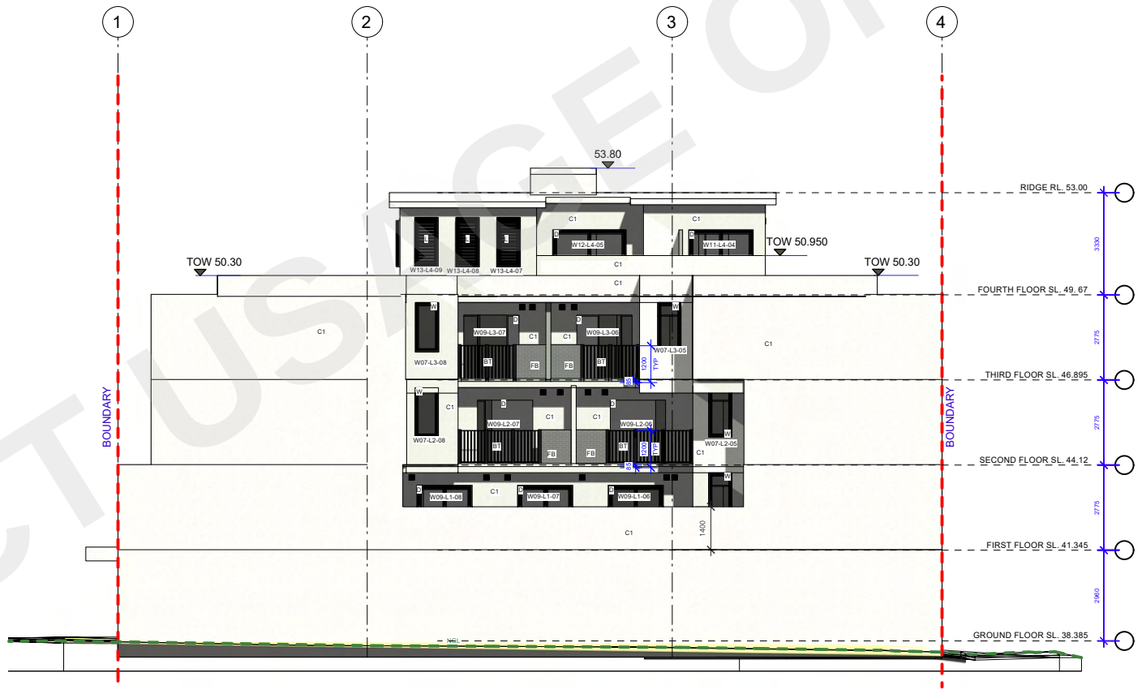

EAST FACING ELEVATION
scale 1:200

CONSTRUCTION CERTIFICATE NOTES:

GENERAL

1.ALL WORK SHALL COMPLY WITH THE NCC (BCA VOL 1 2025 EDITION), CONDITIONS OF CONSENT, AND THE RELEVANT AUSTRALIAN STANDARDS AS LISTED BELOW.
2. FOR CONSTRUCTION CERTIFICATE ONLY NOT FOR CONSTRUCTION. ALL DIMENSIONS SHALL BE VERIFIED ON SITE PRIOR TO COMMENCEMENT OF WORK. DO NOT SCALE DRAWINGS.
3.BYDA BEFORE YOU DIG FOR ANY UNDERGROUND SERVICES.WWW.BYDA.COM.AU
4. ANY DISCREPANCIES BETWEEN DRAWINGS, SITE CONDITIONS, OR SPECIFICATIONS SHALL BE REFERRED TO THE ARCHITECT BEFORE PROCEEDING.
5. DRAWINGS ARE TO BE READ IN CONJUNCTION WITH THE ARCHITECTURAL SPECIFICATION AND ALL CONSULTANT DRAWINGS AND SPECIFICATIONS, INCLUDING STRUCTURAL, CIVIL, HYDRAULIC, MECHANICAL, ELECTRICAL, FIRE, LANDSCAPE AND SECTION J DOCUMENTATION.
6. THE BUILDER SHALL CARRY OUT ALL WORK IN ACCORDANCE WITH: NCC (BCA VOL 1 2025), CONDITIONS OF DEVELOPMENT CONSENT, WHS REGULATION (NSW), AND RELEVANT AUSTRALIAN STANDARDS.
7. PROVIDE ADEQUATE PROTECTION TO EXISTING STRUCTURES, PUBLIC SPACES AND SERVICES DURING CONSTRUCTION.
8. THE BUILDER SHALL COORDINATE ALL TRADES AND ENSURE PENETRATIONS, SET-OUTS AND SERVICE ROUTES ARE ACCURATELY LOCATED.
9. ALL DIMENSIONS TO BE CHECKED ON SITE AND SETOUT BY A SURVEYOR PRIOR TO COMMENCEMENT OF CONSTRUCTION.

LEGEND

SD-06	DOOR NUMBERS
W09	WINDOW NUMBERS
W	BLACK ALUMINIUM FRAMED WINDOW
D	BLACK ALUMINIUM FRAMED DOOR
FB	DARK GREY FACE BRICK
C2	PAINTED V-GROOVE PANELS
C1	PAINTED CONCRETE PANELS
BT	BLACK POWDERCOATED BALUSTRADE
L	BLACK ALUMINIUM FRAMED LOUVRES
	AMENDMENTS FOR CC BY LMP
	BOUNDARY LINE
NGL	NATURAL GROUND LEVEL

0 2 3 5 m

No.	Date	Issue Notes
CC-A	02-Sep-26	FOR CC SUBMISSION

Consultant / Notes:
Survey Prepared by Total Surveying Solutions
ARTARMON.CAMDEN, MANLYVALE

COPYRIGHT
THIS DRAWING IS THE PROPERTY OF LYLE MARSHALL AND PARTNERS P/L AND MAY O BE USED FOR THE PURPOSE FOR WHICH IT WAS COMMISSIONED & IN ACCORDANCE THE TERMS OF ENGAGEMENT FOR THAT COMMISSION. UNAUTHORISED USE OF THIS DRAWING IS PROHIBITED.

FOR CC SUBMISSION

Design By	Job No. 5187-26		
Drawn By EMMC	Scale 1:200		
Reviewed By	Date 02-Sep-26	Sheet No. A201 of	Issue CC-A
Passed By	Date of Issue		

TEST PROJECT USE ONLY

Regulated Design Record

Project Address:			
Project Title:			
Consent No:	DA18/0471.03	Body Corporate Reg No:	
Drawing Title:	BUILDING SECTIONS - SHEET 1	Drawing No:	5187-26-A300

Rev	Date dd.mm.yy	Description	DEP Full Name	Reg No
CC-A	02/09/26	FOR CC SUBMISSION	ERICA MARSHALL-EVANS	DEP 0001207


CONSTRUCTION CERTIFICATE NOTES:

GENERAL

1.ALL WORK SHALL COMPLY WITH THE NCC (BCA VOL 1 2025 EDITION), CONDITIONS OF CONSENT, AND THE RELEVANT AUSTRALIAN STANDARDS AS LISTED BELOW.
2. FOR CONSTRUCTION CERTIFICATE ONLY NOT FOR CONSTRUCTION. ALL DIMENSIONS SHALL BE VERIFIED ON SITE PRIOR TO COMMENCEMENT OF WORK. DO NOT SCALE DRAWINGS.
3.BYDA BEFORE YOU DIG FOR ANY UNDERGROUND SERVICES.WWW.BYDA.COM.AU
4. ANY DISCREPANCIES BETWEEN DRAWINGS, SITE CONDITIONS, OR SPECIFICATIONS SHALL BE REFERRED TO THE ARCHITECT BEFORE PROCEEDING.
5. DRAWINGS ARE TO BE READ IN CONJUNCTION WITH THE ARCHITECTURAL SPECIFICATION AND ALL CONSULTANT DRAWINGS AND SPECIFICATIONS, INCLUDING STRUCTURAL, CIVIL, HYDRAULIC, MECHANICAL, ELECTRICAL, FIRE, LANDSCAPE AND SECTION J DOCUMENTATION.
6. THE BUILDER SHALL CARRY OUT ALL WORK IN ACCORDANCE WITH: NCC (BCA VOL 1 2025), CONDITIONS OF DEVELOPMENT CONSENT, WHS REGULATION (NSW), AND RELEVANT AUSTRALIAN STANDARDS.
7. PROVIDE ADEQUATE PROTECTION TO EXISTING STRUCTURES, PUBLIC SPACES AND SERVICES DURING CONSTRUCTION.
8. THE BUILDER SHALL COORDINATE ALL TRADES AND ENSURE PENETRATIONS, SET-OUTS AND SERVICE ROUTES ARE ACCURATELY LOCATED.
9. ALL DIMENSIONS TO BE CHECKED ON SITE AND SETOUT BY A SURVEYOR PRIOR TO COMMENCEMENT OF CONSTRUCTION.



SECTION A-A
SCALE 1:200@A3

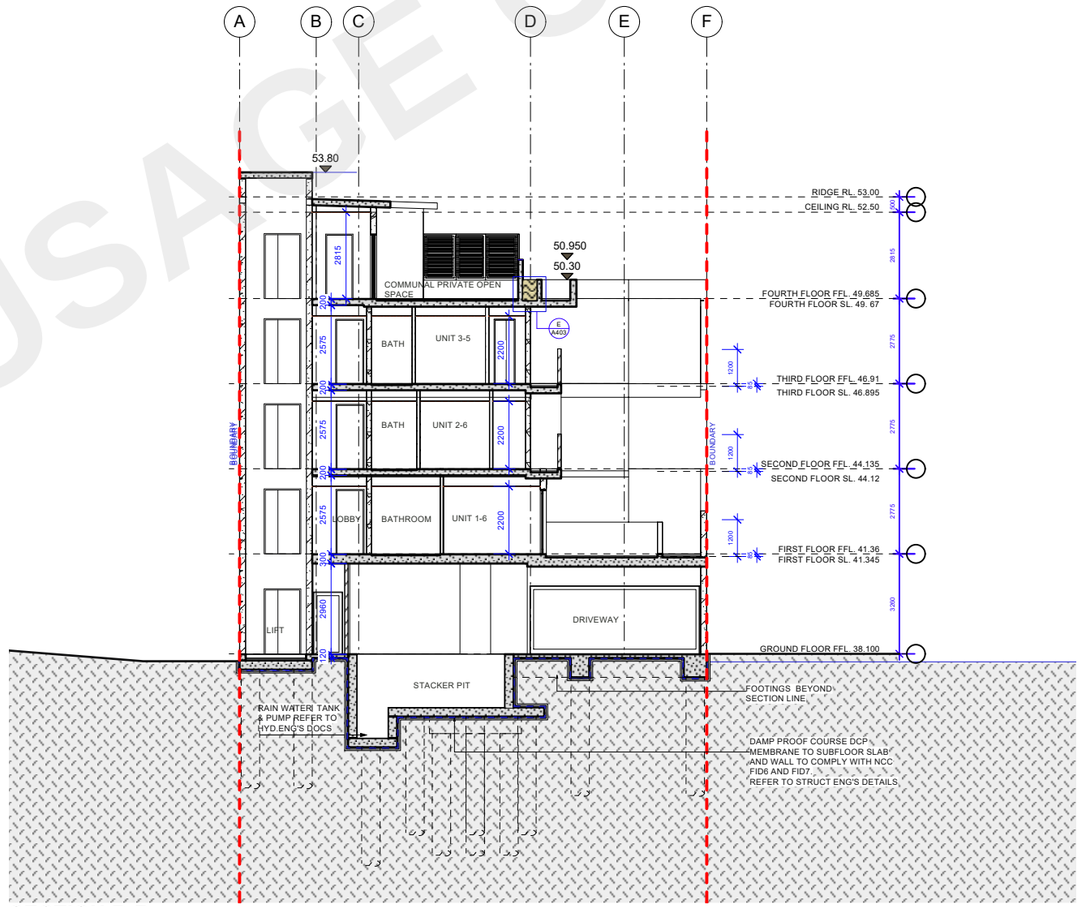

SECTION B-B
SCALE 1:200@A3

LEGEND

BOUNDARY LINE

NGL NATURAL GROUND LEVEL

0 2 3 5 m

FOR CC SUBMISSION

No.	Date	Issue Notes
CC-A	02-Sep-26	FOR CC SUBMISSION

Consultant / Notes:

Survey Prepared by Total Surveying Solutions
ARTARMON.CAMDEN, MANLYVALE

COPYRIGHT
THIS DRAWING IS THE PROPERTY OF LYLE MARSHALL AND PARTNERS P/L AND MAY O BE USED FOR THE PURPOSE FOR WHICH IT WAS COMMISSIONED & IN ACCORDANCE THE TERMS OF ENGAGEMENT FOR THAT COMMISSION. UNAUTHORISED USE OF THIS DRAWING IS PROHIBITED.


Design By		Job No.	5187-26
Drawn By	EMMC	Scale	1:200
Reviewed By		Date	02-Sep-26
Passed By		Date of Issue	
Sheet No.	A300 of	Issue	CC-A

TEST USAGE ONLY

Regulated Design Record

Project Address:	
Project Title:	
Consent No: DA18/0471.03	Body Corporate Reg No:
Drawing Title: BUILDING SECTIONS - SHEET 2	Drawing No: 5187-26-A301

Rev	Date dd.mm.yy	Description	DEP Full Name	Reg No
CC-A	02/09/26	FOR CC SUBMISSION	ERICA MARSHALL-EVANS	DEP 0001207

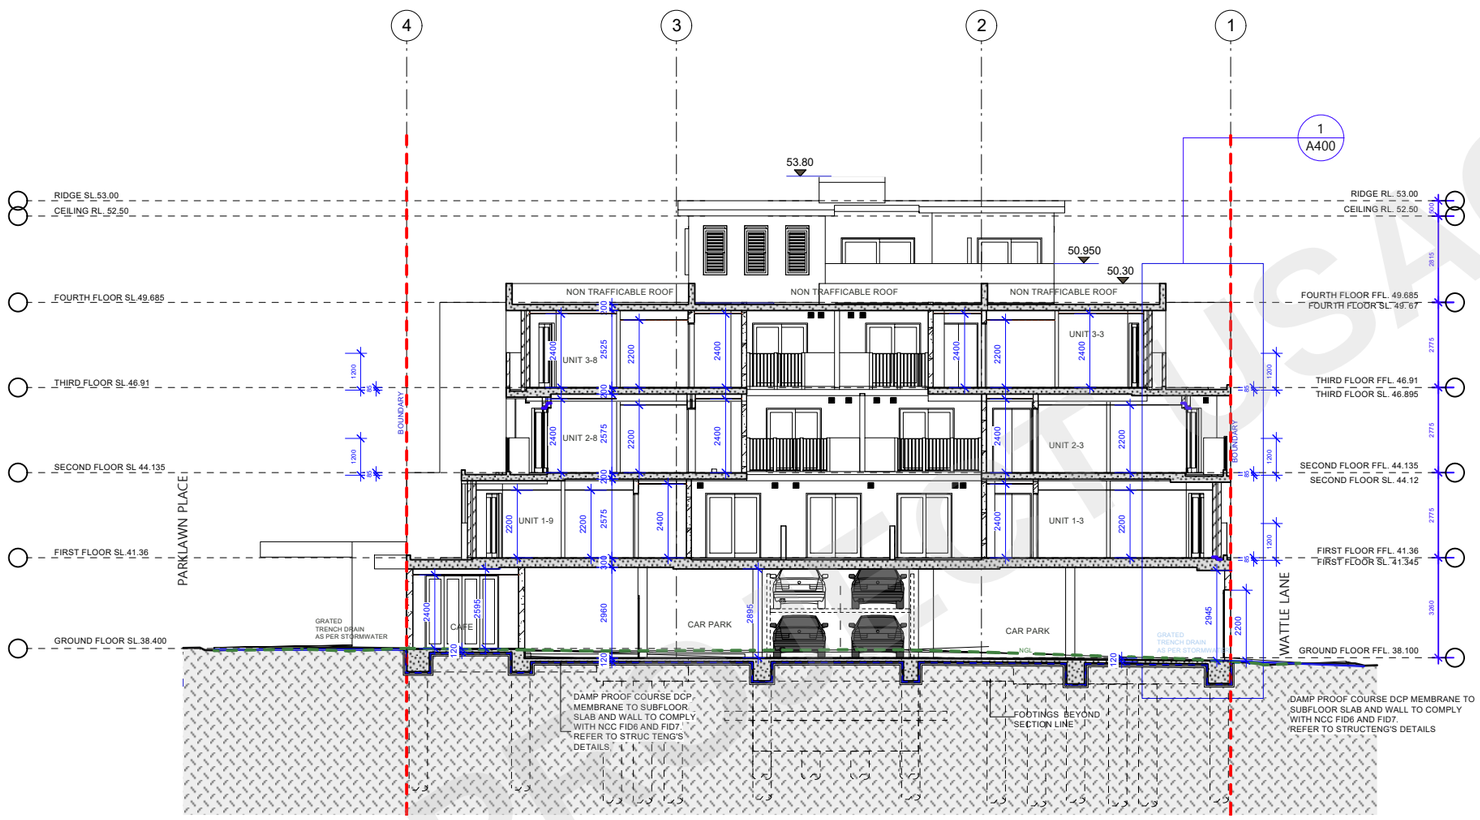

SECTION C-C
SCALE 1:200@A3

CONSTRUCTION CERTIFICATE NOTES:

GENERAL
1.ALL WORK SHALL COMPLY WITH THE NCC (BCA VOL 1 2025 EDITION), CONDITIONS OF CONSENT, AND THE RELEVANT AUSTRALIAN STANDARDS AS LISTED BELOW.
2. FOR CONSTRUCTION CERTIFICATE ONLY NOT FOR CONSTRUCTION. ALL DIMENSIONS SHALL BE VERIFIED ON SITE PRIOR TO COMMENCEMENT OF WORK. DO NOT SCALE DRAWINGS.
3.BYDA BEFORE YOU DIG FOR ANY UNDERGROUND SERVICES.WWW.BYDA.COM.AU
4. ANY DISCREPANCIES BETWEEN DRAWINGS, SITE CONDITIONS, OR SPECIFICATIONS SHALL BE REFERRED TO THE ARCHITECT BEFORE PROCEEDING.
5. DRAWINGS ARE TO BE READ IN CONJUNCTION WITH THE ARCHITECTURAL SPECIFICATION AND ALL CONSULTANT DRAWINGS AND SPECIFICATIONS, INCLUDING STRUCTURAL, CIVIL, HYDRAULIC, MECHANICAL, ELECTRICAL, FIRE, LANDSCAPE AND SECTION J DOCUMENTATION.
6. THE BUILDER SHALL CARRY OUT ALL WORK IN ACCORDANCE WITH: NCC (BCA VOL 1 2025), CONDITIONS OF DEVELOPMENT CONSENT, WHS REGULATION (NSW), AND RELEVANT AUSTRALIAN STANDARDS.
7. PROVIDE ADEQUATE PROTECTION TO EXISTING STRUCTURES, PUBLIC SPACES AND SERVICES DURING CONSTRUCTION.
8. THE BUILDER SHALL COORDINATE ALL TRADES AND ENSURE PENETRATIONS, SET-OUTS AND SERVICE ROUTES ARE ACCURATELY LOCATED.
9. ALL DIMENSIONS TO BE CHECKED ON SITE AND SETOUT BY A SURVEYOR PRIOR TO COMMENCEMENT OF CONSTRUCTION.

LEGEND
BOUNDARY LINE
NGL NATURAL GROUND LEVEL

0 2 3 5 m

FOR CC SUBMISSION

No.	Date	Issue Notes
CC-A	02-Sep-26	FOR CC SUBMISSION

Consultant / Notes:
Survey Prepared by Total Surveying Solutions
ARTARMON.CAMDEN, MANLYVALE

COPYRIGHT
THIS DRAWING IS THE PROPERTY OF LYLE MARSHALL AND PARTNERS P/L AND MAY O BE USED FOR THE PURPOSE FOR WHICH IT WAS COMMISSIONED & IN ACCORDANCE THE TERMS OF ENGAGEMENT FOR THAT COMMISSION. UNAUTHORISED USE OF THIS DRAWING IS PROHIBITED.

Design By		Job No.	5187-26
Drawn By	EMMC	Scale	1:200
Reviewed By		Date	02-Sep-26
Passed By		Date of Issue	
Sheet No.	A301 of	Issue	CC-A

TEST PROJECT
USAGE ONLY

SAMPLE PROJECT A - ARCHITECTURAL - RECRUITMENT ASSESSMENT ONLY


Regulated Design Record

Project Address:	
Project Title:	
Consent No: DA18/0471.03	Body Corporate Reg No:
Drawing Title: WALL SECTIONS	Drawing No: 5187-26-A400

Rev	Date dd.mm.yy	Description	DEP Full Name	Reg No
CC-A	02/09/26	FOR CC SUBMISSION	ERICA MARSHALL-EVANS	DEP 0001207


NOTE:

DAMP PROOF COURSE DCP MEMBRANE TO SUBFLOOR SLAB AND WALL TO CPMPLY WITH NCC FID6 AND FID7.

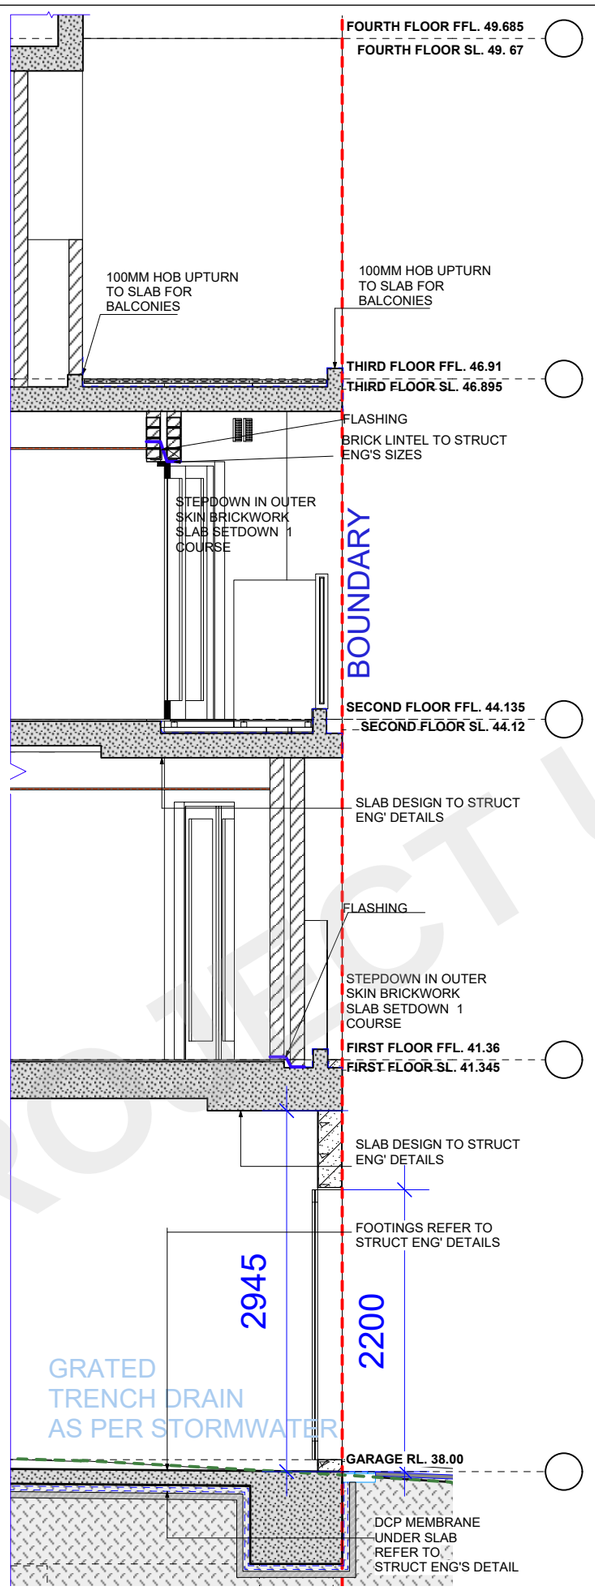

1 WALL DETAIL 1
SCALE 1:50

0 250 500 750 1000 mm

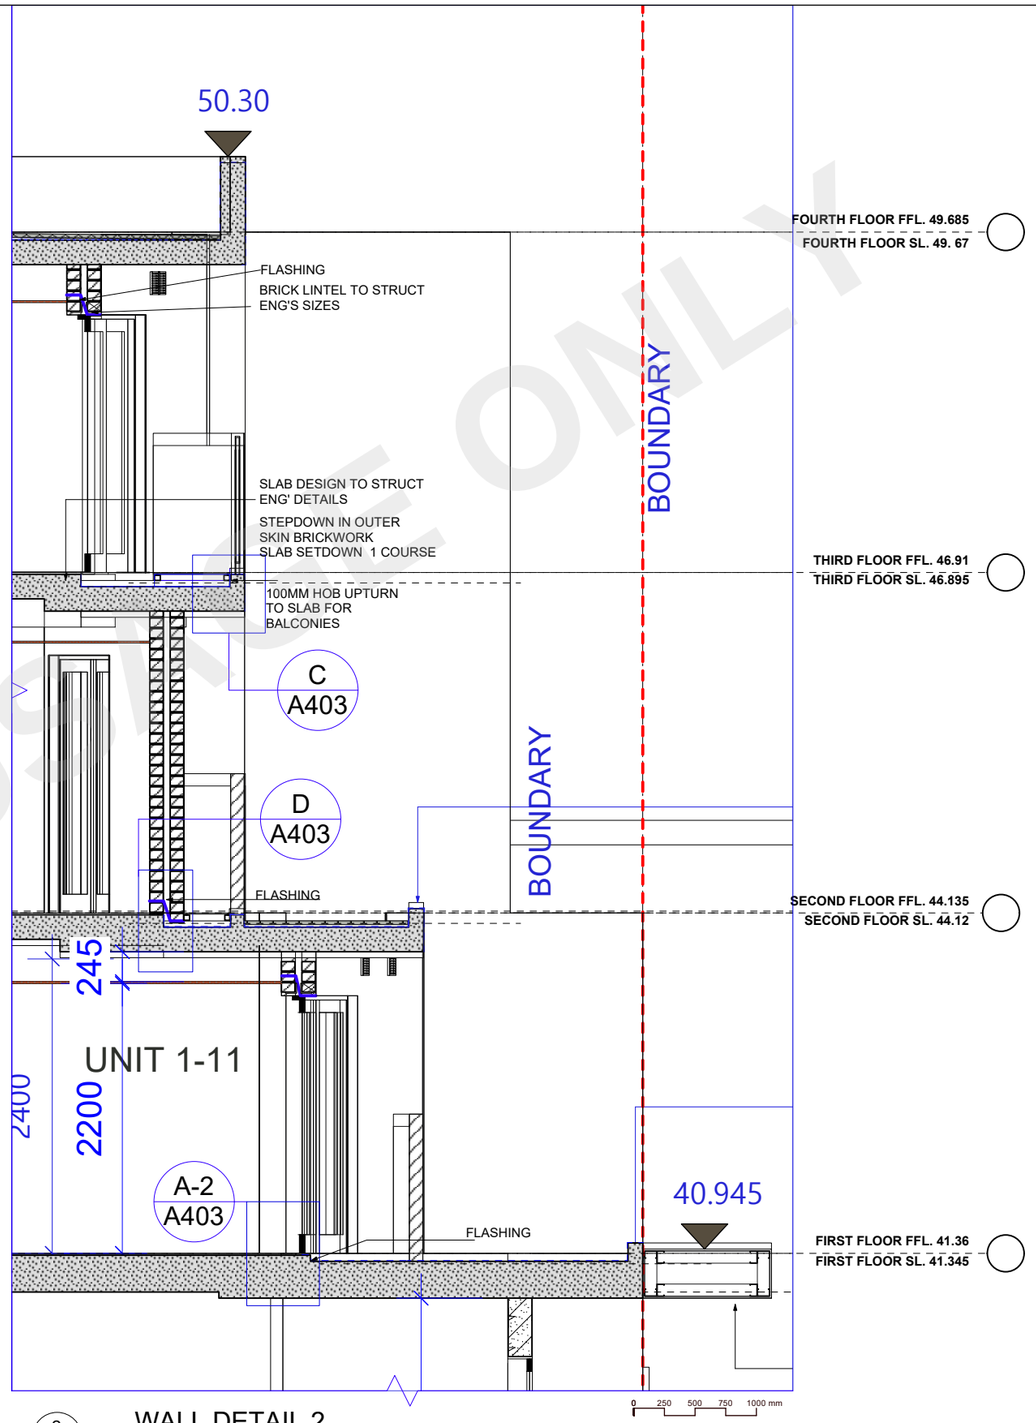

2 WALL DETAIL 2
SCALE 1:50

0 250 500 750 1000 mm

LEGEND

BOUNDARY LINE

NOTE:
FOR GENERAL CONSTRUCTION NOTES REFER TO COVER SHEET A000

FOR CC SUBMISSION

No.	Date	Issue Notes
CC-A	02-Sep-26	FOR CC SUBMISSION

Consultant / Notes:

Survey Prepared by Total Surveying Solutions
ARTARMON.CAMDEN, MANLYVALE

COPYRIGHT
THIS DRAWING IS THE PROPERTY OF LYLE MARSHALL AND PARTNERS P/L AND MAY O BE USED FOR THE PURPOSE FOR WHICH IT WAS COMMISSIONED & IN ACCORDANCE THE TERMS OF ENGAGEMENT FOR THAT COMMISSION. UNAUTHORISED USE OF THIS DRAWING IS PROHIBITED.

Design By		Job No.	5187-26		
Drawn By	EMMC	Scale	1:50		
Reviewed By		Date	02-Sep-26	Sheet No.	A400 of
Passed By		Date of Issue		Issue	CC-A

TEST PROJECT USAGE ONLY

SAMPLE PROJECT A - ARCHITECTURAL - RECRUITMENT ASSESSMENT ONLY

Regulated Design Record

Project Address:			
Project Title:			
Consent No:	DA18/0471.03	Body Corporate Reg No:	
Drawing Title:	STAIR DETAILS	Drawing No:	5187-26-A401

Rev	Date dd.mm.yy	Description	DEP Full Name	Reg No
CC-A	02/09/26	FOR CC SUBMISSION	ERICA MARSHALL-EVANS	DEP 0001207

WALL TYPES

FRL 240/240/240 — 200 — **Ritek XL - 200A EXTERNAL CONCRETE WALL**

FRL 240/240/240 — 165 — **Ritek XL - 165A INTERNAL CONCRETE WALL**

FRL 240/240/240 — 150 — **Ritek XL - 150A INTERNAL CONCRETE WALL**


LEGEND

BOUNDARY LINE


NOTE:
FOR GENERAL CONSTRUCTION NOTES
REFER TO COVER SHEET A000

NOTE:


LIFT IS STRETCHER-COMPLIANT WITH NCC CLAUSE E3D3. (ALPINE SHOTTON LIFT MODEL)

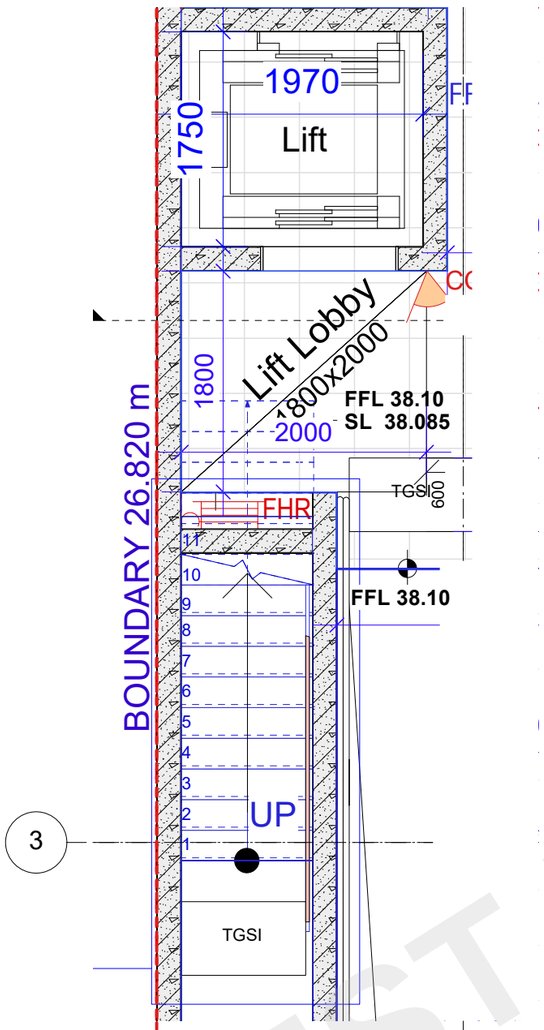


1 401 STAIR GF DETAIL 1
SCALE 1:50

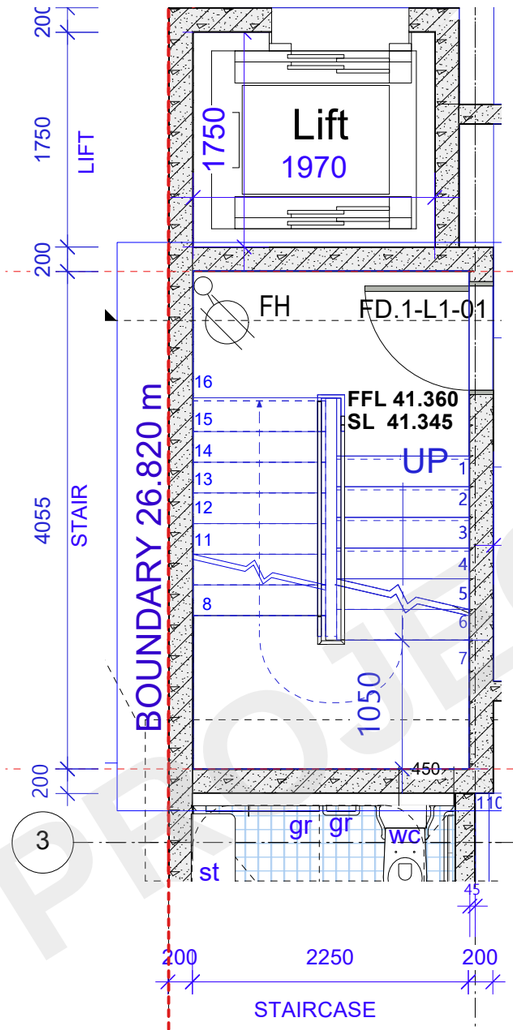


2 401 STAIR L1 DETAIL 2
SCALE 1:50

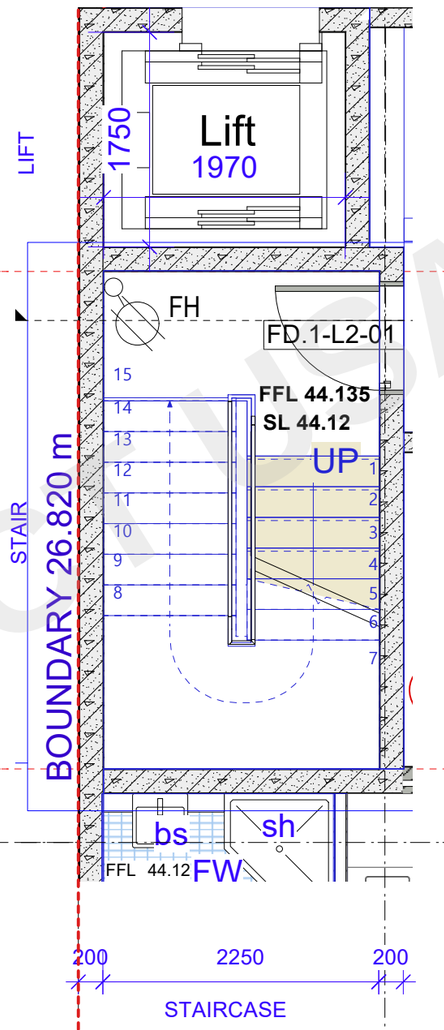

3 401 STAIR L2 DETAIL 3
SCALE 1:50

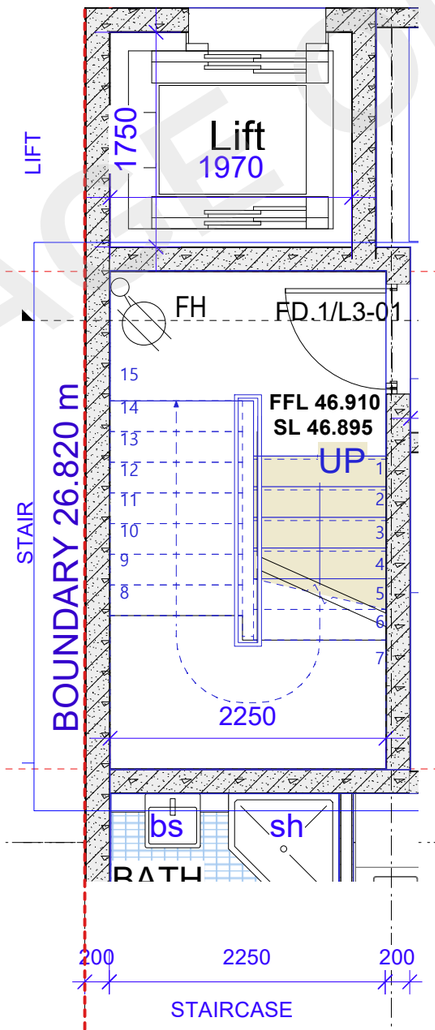

4 401 STAIR L3 DETAIL 4
SCALE 1:50

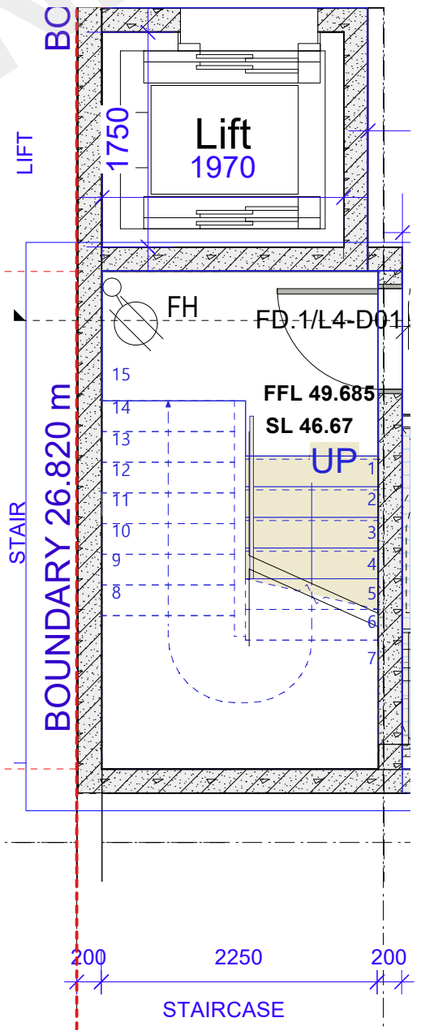

5 401 STAIR L4 DETAIL 5
SCALE 1:50

TEST PROJECT ONLY

No.	Date	Issue Notes
CC-A	02-Sep-26	FOR CC SUBMISSION

Consultant / Notes:

Survey Prepared by Total Surveying Solutions
ARTARMON.CAMDEN, MANLYVALE

COPYRIGHT
THIS DRAWING IS THE PROPERTY OF LYLE MARSHALL AND PARTNERS P/L AND MAY O BE USED FOR THE PURPOSE FOR WHICH IT WAS COMMISSIONED & IN ACCORDANCE THE TERMS OF ENGAGEMENT FOR THAT COMMISSION. UNAUTHORISED USE OF THIS DRAWING IS PROHIBITED.

0 250 500 750 1000 mm


FOR CC SUBMISSION

Design By		Job No.	5187-26
Drawn By	EMMC	Scale	1:50
Reviewed By		Date	02-Sep-26
Passed By		Date of Issue	
Sheet No.	A401 of	Issue	CC-A


Regulated Design Record

Project Address:	
Project Title:	
Consent No: DA18/0471.03	Body Corporate Reg No:
Drawing Title: TYPICAL KITCHEN AND BATHROOM LAYOUT	Drawing No: 5187-26-A402


Rev	Date dd.mm.yy	Description	DEP Full Name	Reg No
CC-A	02/09/26	FOR CC SUBMISSION	ERICA MARSHALL-EVANS	DEP 0001207

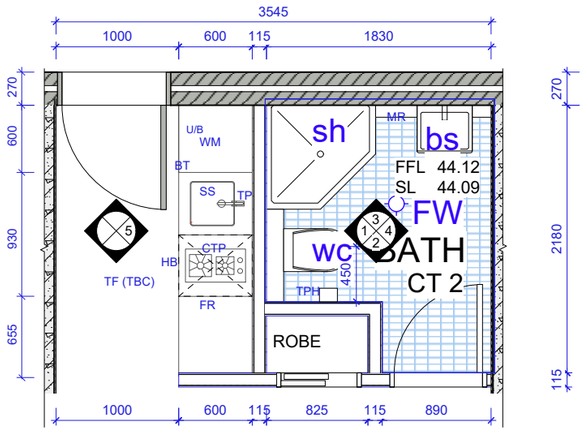


01 KITCHEN AND BATHROOM LAYOUT 01
1:50

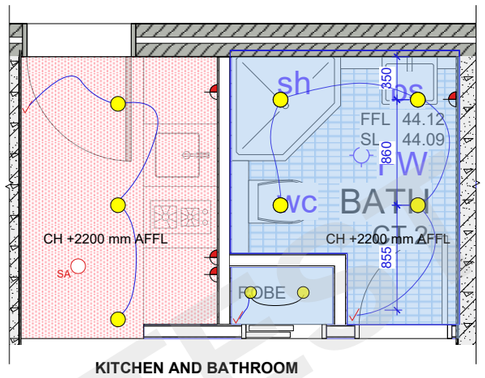


KITCHEN AND BATHROOM RCP AND ELECTRICAL LAYOUT
02 1:50

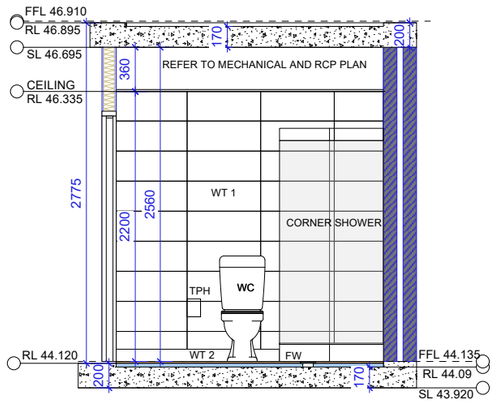


03 BATHROOM ELEVATION 01
1:50

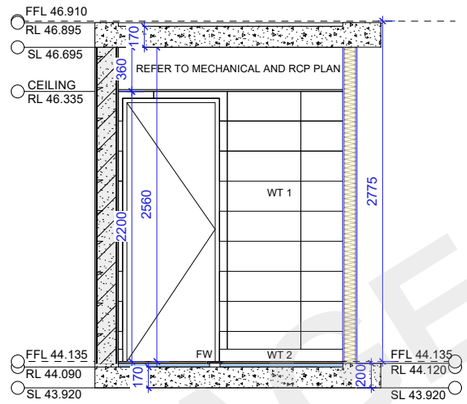


04 BATHROOM ELEVATION 02
1:50

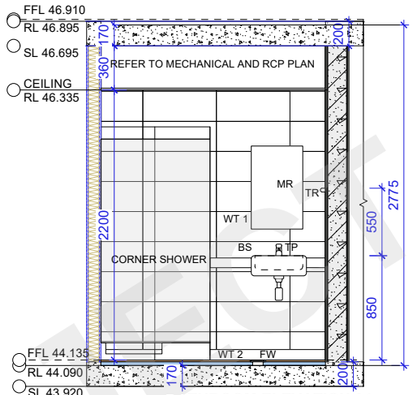

05 BATHROOM ELEVATION 04
1:50

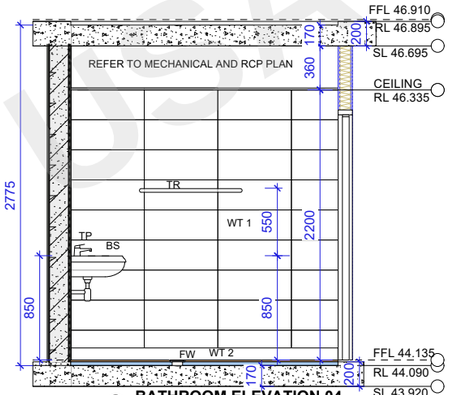

06 BATHROOM ELEVATION 04
1:50

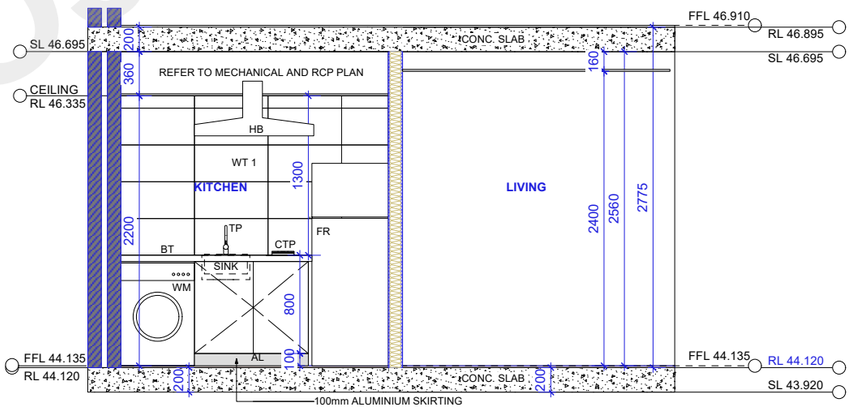


07 KITCHEN ELEVATION
1:50


WALL TYPES



115 mm INTERNAL STEEL STUD WALL
13 mm PLASTERBOARD
90 mm STEEL STUD
13 mm PLASTERBOARD

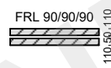

270 mm CAVITY BRICK WALL
110 mm BRICK
90 50 AIR GAP
110 mm BRICK

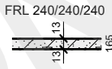

Ritek XL - 165-C INTERTENANCY WALLS
13 mm PLASTERBOARD
165 mm Ritek XL WALL
13 mm PLASTERBOARD
ALLOW 190mm

LEGEND

AL	100 MM ALUMINIUM KICKER
BT	BENCHTOP
BS	BASIN
CA	CABINET
CT2	NON-SLIP CERAMIC TILE(BATHROOM)
CTP	COOKTOP
MR	MIRROR
FR	REFRIGERATOR
FP	FLUSH PLATE
HB	HOB
SS	STAINLESS STEEL SINK
TP	TAP
TPH	TOILET PAPER HOLDER
TR	TOWEL RAIL
TF	TIMBER FLOOR (TO BE CONFIRMED)
WC	WATER CLOSET
WM	WASHMACHINE
WT1	WALL TILE 1
WT2	WALL TILE 2
FFL	FINISH FLOOR LEVEL
SL	CONCRETE SLAB LEVEL

LEGEND

CH	CEILING HEIGHT ABOVE FINISHED FLOOR LEVEL
✓	SWITCH
	GPO
	SURFACE MOUNTED LED DOWNLIGHT
SA	SMOKE ALARM
	PLASTERBOARD CEILING - FOR WET AREAS (GYPROCK AQUACHECK)
	FIRE RESISTANT PLASTERBOARD CEILING (GYPROCK FYRECHECK 16 MM)

CONSTRUCTION CERTIFICATE NOTES:

GENERAL

1.ALL WORK SHALL COMPLY WITH THE NCC (BCA VOL 1 2025 EDITION), CONDITIONS OF CONSENT, AND THE RELEVANT AUSTRALIAN STANDARDS AS LISTED BELOW.
2. FOR CONSTRUCTION CERTIFICATE ONLY NOT FOR CONSTRUCTION. ALL DIMENSIONS SHALL BE VERIFIED ON SITE PRIOR TO COMMENCEMENT OF WORK. DO NOT SCALE DRAWINGS.
3.BYDA BEFORE YOU DIG FOR ANY UNDERGROUND SERVICES.WWW.BYDA.COM.AU
4. ANY DISCREPANCIES BETWEEN DRAWINGS, SITE CONDITIONS, OR SPECIFICATIONS SHALL BE REFERRED TO THE ARCHITECT BEFORE PROCEEDING.
5. DRAWINGS ARE TO BE READ IN CONJUNCTION WITH THE ARCHITECTURAL SPECIFICATION AND ALL CONSULTANT DRAWINGS AND SPECIFICATIONS, INCLUDING STRUCTURAL, CIVIL, HYDRAULIC, MECHANICAL, ELECTRICAL, FIRE, LANDSCAPE AND SECTION J DOCUMENTATION.
6. THE BUILDER SHALL CARRY OUT ALL WORK IN ACCORDANCE WITH: NCC (BCA VOL 1 2025), CONDITIONS OF DEVELOPMENT CONSENT, WHS REGULATION (NSW), AND RELEVANT AUSTRALIAN STANDARDS.
7. PROVIDE ADEQUATE PROTECTION TO EXISTING STRUCTURES, PUBLIC SPACES AND SERVICES DURING CONSTRUCTION.
8. THE BUILDER SHALL COORDINATE ALL TRADES AND ENSURE PENETRATIONS, SET-OUTS AND SERVICE ROUTES ARE ACCURATELY LOCATED.
9. ALL DIMENSIONS TO BE CHECKED ON SITE AND SETOUT BY A SURVEYOR PRIOR TO COMMENCEMENT OF CONSTRUCTION.
21.REFER TO FIRE ENGINEERS DRAWINGS AND SPECIFICATIONS
22.REFER TO ELECTRICAL ENGINEERS DRAWINGS AND SPECIFICATIONS
23.REFER TO MECHANICAL ENGINEERS DRAWINGS AND SPECIFICATIONS
24. ACOUSTIC TREATEMENS TO COMPLY WITH THE ACOUSTIC CONSULTANT'S RECOMMENDATIONS.

0 250 500 750 1000 mm

FOR CC SUBMISSION

No.	Date	Issue Notes
CC-A	02-Sep-26	FOR CC SUBMISSION

Consultant / Notes:
Survey Prepared by Total Surveying Solutions
ARTARMON.CAMDEN, MANLYVALE

COPYRIGHT
THIS DRAWING IS THE PROPERTY OF LYLE MARSHALL AND PARTNERS P/L AND MAY ONL BE USED FOR THE PURPOSE FOR WHICH IT WAS COMMISSIONED & IN ACCORDANCE WIT THE TERMS OF ENGAGEMENT FOR THAT COMMISSION. UNAUTHORISED USE OF THIS DRAWING IS PROHIBITED.

LAYOUT

Design By	Job No. 5187-26		
Drawn By EMMC	Scale 1:50		
Reviewed By	Date 02-Sep-26	Sheet No. A402	Issue CC-A
Passed By	Date of Issue	of	

TEST PROJECT ONLY

Regulated Design Record


Project Address:

Project Title:

Consent No: DA18/0471.03 | Body Corporate Reg No:


Drawing Title: TYPICAL BALCONY WATERPROOFING DETAIL | Drawing No: 5187-26-A403

Rev	Date dd.mm.yy	Description	DEP Full Name	Reg No
CC-A	02/09/26	FOR CC SUBMISSION	ERICA MARSHALL-EVANS	DEP 0001207

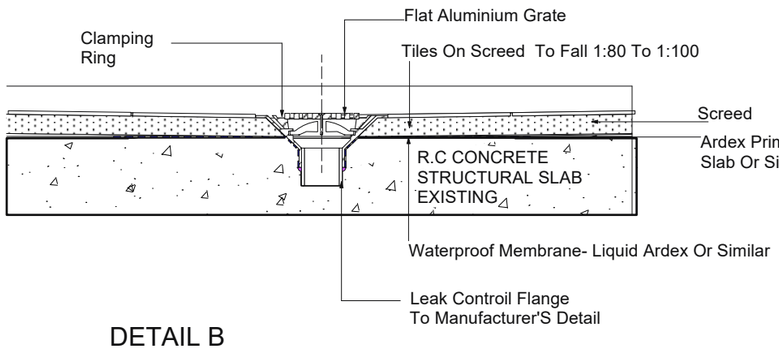


DETAIL B
WATERPROOFNG DETAIL TO DRAINAGE OUTLET

SCALE 1:10

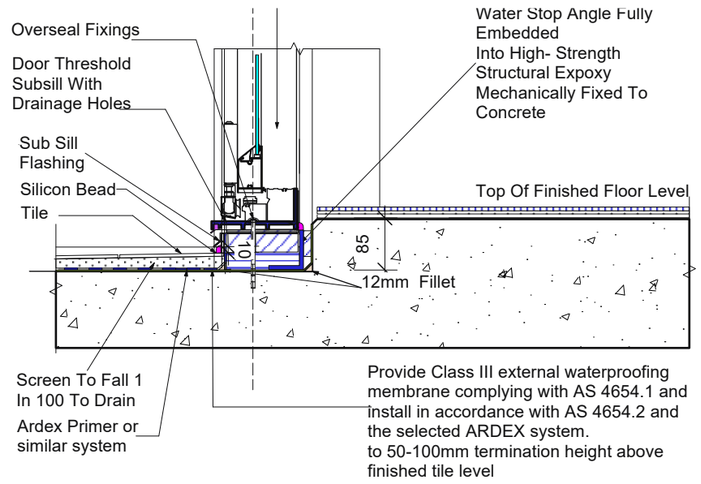


DETAIL A
SILL WATERPROOFING DETAIL TYPE A

SCALE 1:10

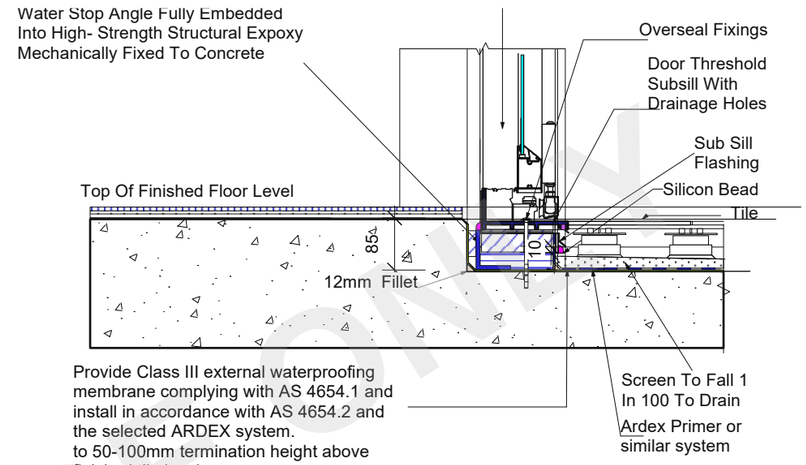


DETAIL A-2
SILL WATERPROOFING DETAIL ACCESSIBLE THRESHOLD
SCALE 1:10

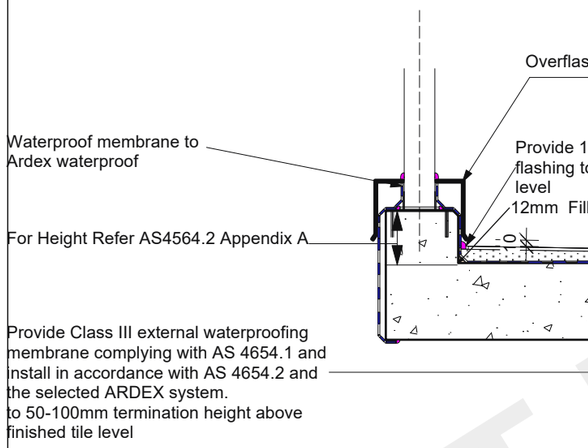

DETAIL D
WATERPROOFNG DETAIL TO BALUSTRADE HOB


SCALE 1:10

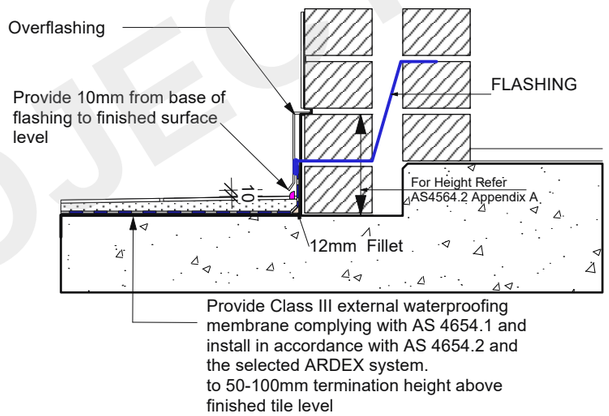

DETAIL C
TYPICAL UPWARD TERMINATION OF LIQUID MEMBRANE DETAIL TYPE A

SCALE 1:10

0 250 500 mm

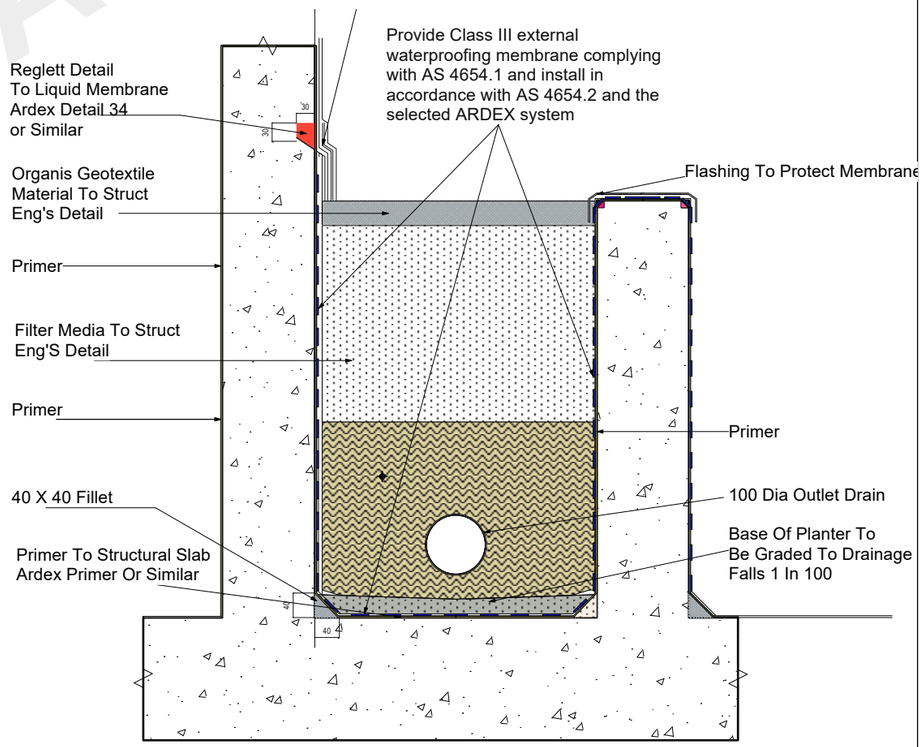

DETAIL E
PLANTER BOX DETAIL

SCALE 1:10

NOTE:
FOR GENERAL CONSTRUCTION NOTES REFER TO COVER SHEET A000

FOR CC SUBMISSION

No.	Date	Issue Notes
CC-A	02-Sep-26	FOR CC SUBMISSION

Consultant / Notes:
Survey Prepared by Total Surveying Solutions
ARTARMON.CAMDEN, MANLYVALE

COPYRIGHT
THIS DRAWING IS THE PROPERTY OF LYLE MARSHALL AND PARTNERS P/L AND MAY ONL BE USED FOR THE PURPOSE FOR WHICH IT WAS COMMISSIONED & IN ACCORDANCE WIT THE TERMS OF ENGAGEMENT FOR THAT COMMISSION. UNAUTHORISED USE OF THIS DRAWING IS PROHIBITED.

G DETAILS


Design By	Job No. 5187-26
Drawn By EMMC	Scale 1:10
Reviewed By	Date 02-Sep-26 / Sheet No. A403 / Issue CC-A
Passed By	Date of Issue / of

TEST PROJECT USAGE ONLY


Regulated Design Record

Project Address:	
Project Title:	
Consent No: DA18/0471.03	Body Corporate Reg No:
Drawing Title: LETTERBOX AND EXTERNAL DETAILS	Drawing No: 5187-26-A404

Rev	Date dd.mm.yy	Description	DEP Full Name	Reg No
CC-A	28/08/26	DRAFT FOR CC SUBMISSION	ERICA MARSHALL-EVANS	DEP 0001207

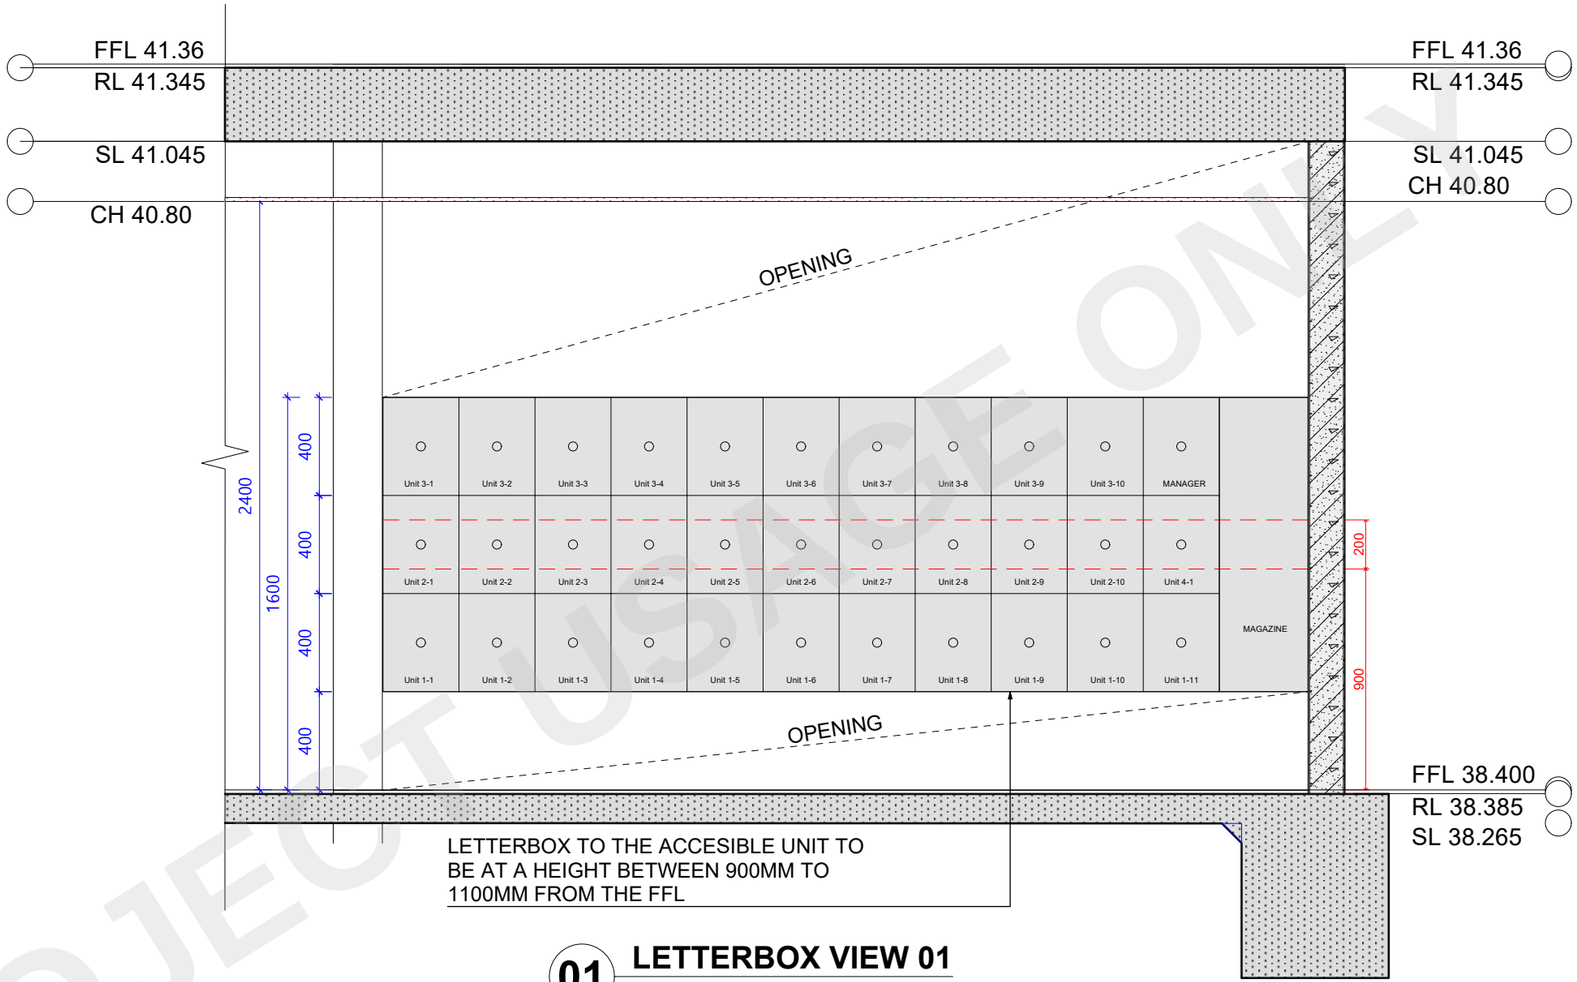

01 LETTERBOX VIEW 01
1:25

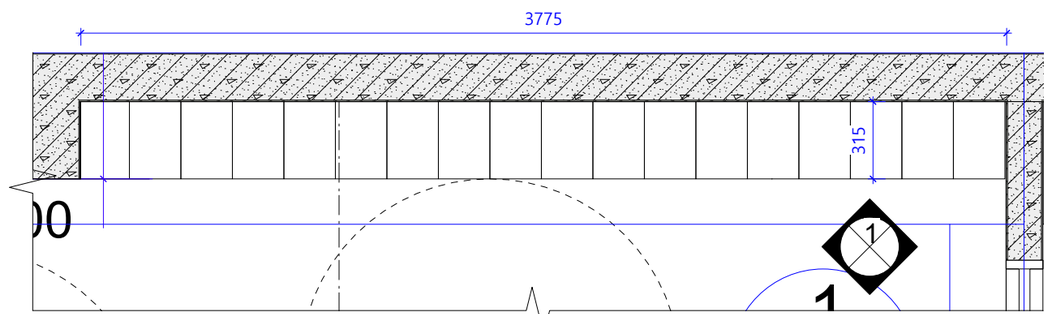

02 LETTERBOX LAYOUT
1:25

CONSTRUCTION CERTIFICATE NOTES:

GENERAL

1.ALL WORK SHALL COMPLY WITH THE NCC (BCA VOL 1 2025 EDITION), CONDITIONS OF CONSENT, AND THE RELEVANT AUSTRALIAN STANDARDS AS LISTED BELOW.
2. FOR CONSTRUCTION CERTIFICATE ONLY NOT FOR CONSTRUCTION. ALL DIMENSIONS SHALL BE VERIFIED ON SITE PRIOR TO COMMENCEMENT OF WORK. DO NOT SCALE DRAWINGS.
3.BYDA BEFORE YOU DIG FOR ANY UNDERGROUND SERVICES.WWW.BYDA.COM.AU
4. ANY DISCREPANCIES BETWEEN DRAWINGS, SITE CONDITIONS, OR SPECIFICATIONS SHALL BE REFERRED TO THE ARCHITECT BEFORE PROCEEDING.
5. DRAWINGS ARE TO BE READ IN CONJUNCTION WITH THE ARCHITECTURAL SPECIFICATION AND ALL CONSULTANT DRAWINGS AND SPECIFICATIONS, INCLUDING STRUCTURAL, CIVIL, HYDRAULIC, MECHANICAL, ELECTRICAL, FIRE, LANDSCAPE AND SECTION J DOCUMENTATION.
6. THE BUILDER SHALL CARRY OUT ALL WORK IN ACCORDANCE WITH: NCC (BCA VOL 1 2025), CONDITIONS OF DEVELOPMENT CONSENT, WHS REGULATION (NSW), AND RELEVANT AUSTRALIAN STANDARDS.
7. PROVIDE ADEQUATE PROTECTION TO EXISTING STRUCTURES, PUBLIC SPACES AND SERVICES DURING CONSTRUCTION.
8. THE BUILDER SHALL COORDINATE ALL TRADES AND ENSURE PENETRATIONS, SET-OUTS AND SERVICE ROUTES ARE ACCURATELY LOCATED.
9. ALL DIMENSIONS TO BE CHECKED ON SITE AND SETOUT BY A SURVEYOR PRIOR TO COMMENCEMENT OF CONSTRUCTION.

TEST PROJECT

No.	Date	Issue Notes
CC-A	28-Aug-26	DRAFT FOR CC SUBMISSION
CC-B	0/03/2026	NOTES ADDED WET AREAS AND FOOD SAFETY
CC-A	8/12/25	AMENDED FOR CONSTRUCTION CERTIFICATE
CC-A	24/11/25	AMENDED FOR CONSTRUCTION CERTIFICATE
E	3/06/2025	AMENDMENTS TO ISSUE NUMBERS FOR RFI-3-6-25

Consultant / Notes:
Survey Prepared by Total Surveying Solutions
ARTARMON.CAMDEN, MANLYVALE

COPYRIGHT
THIS DRAWING IS THE PROPERTY OF LYLE MARSHALL AND PARTNERS P/L AND MAY ONL BE USED FOR THE PURPOSE FOR WHICH IT WAS COMMISSIONED & IN ACCORDANCE WIT THE TERMS OF ENGAGEMENT FOR THAT COMMISSION. UNAUTHORISED USE OF THIS DRAWING IS PROHIBITED.

FOR CC SUBMISSION

ILS

Design By	Job No. 5187-26		
Drawn By EMMC	Scale 1:25		
Reviewed By	Date 28-Aug-26	Sheet No. A404 of	Issue CC-A
Passed By	Date of Issue		

Regulated Design Record


Project Address:

Project Title:

Consent No: DA18/0471.03 | Body Corporate Reg No:


Drawing Title: CAFE KITCHEN DETAILS & NOTES | Drawing No: 5187-26-A405

Rev	Date dd.mm.yy	Description	DEP Full Name	Reg No
CC-A	02/09/26	FOR CC SUBMISSION	ERICA MARSHALL-EVANS	DEP 0001207

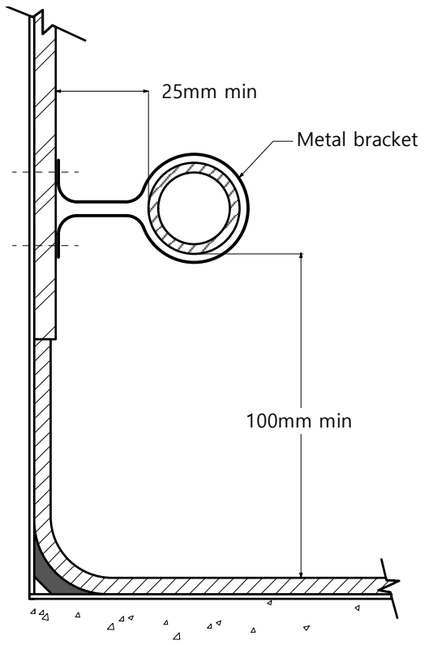

1 **TYPICAL CLEARANCES FOR SERVICE PIPES AND CONDUITS**

NTS

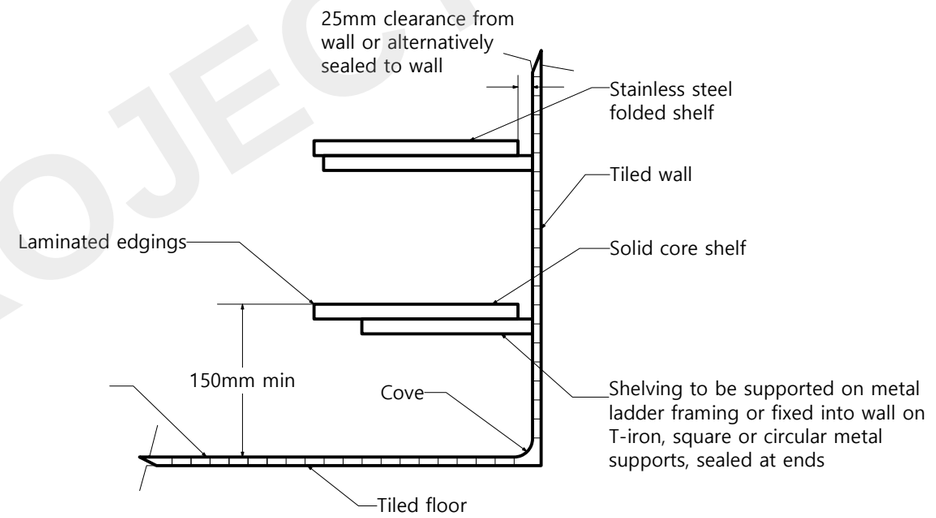

2 **TYPICAL ARRANGEMENT -SHELVING DETAIL**

NTS

KITCHEN GENERAL NOTES

0**KITCHEN GENERAL NOTES**

01 THE LAYOUT IS CONCEPT INTENT REFER TO DETAILED SPECIFICATION AND DRAWINGS PRODUCED AT CONSTRUCTION CERTIFICATE STAGE.
02 KITCHEN DESIGN CONSTRUCTION AND FITOUT FINISHES ARE TO COMPLY WITH THE NCC 2022, AS4674-2004.
03 INSTALL SMOKE DETECTION AND ALARM SYSTEMS IN ACCORDANCE WITH AS16700 AND NCC 2022.
04 PROVIDE PORTABLE FIRE EXTINGUISHERS COMPLYING WITH AS2444 AND NCC 2022.

KITCHEN CONSTRUCTION NOTES

01 PROVIDE COVING TO ALL FLOOR AND WALL JUNCTIONS\
02 INSTAL LIGHT COLOUR VINYL SLIP RESISTANT P5 VINYL SHEEING WITH WELDED JOINTS FALL TO FLOOR WASTE. TO COMPLY WITH AS 4586 SLIP RESISTANCE CLASSIFICATION OF NEW PEDESTRIAN SURFACE MATERIALS'.
03 PROVIDE SOLID PLINTHS UNDER HEAVY EQUIPMENT THAT CAN NOT BE MOVED FOR CLEANING PURPOSES
04 ALL KITCHEN AND PANTRY WALLS TO BE SOLID WITH NO VOIDS, CAVITIES AND FINISHED WITH LIGHT COLOURED FULL HEIGHT CEREAMIC TILES WITH EXPOXY GROUTING
05 CEILING TO BE RIGID, SMOOTH FINISH WITH MOISTURE RESISTANT PLASTERBOARD AND SEALED AND DUST PROOF AND FINISHED WITH SELECTED GLOSS FINISH.
06 THE WALL AND CEILING JUNCTIONS ARE TO BE TIGHT JOINTED, SEALED AND DUST PROOF.
07 SEAL BETWEEN ALL FITTINGS AND BETWEEN EQUIPMENT BASES THAT ARE FIXED.
08 SUPPLY AND INSTALL EXHAUST CANOPY HOOD WITH DUCTED FAN SYSTEM COMPLYING WITH MECHANICAL ENGINEER'S SPECIFICATIONS AND CODE REQUIREMENTS.
09 PROTECT ALL WINDOWS AND DOORS FROM THE ENTRY OF PESTS.
10 MORTAR FILLED PRESS METAL DOOR FRAMES.
11 CONCEAL ALL WATER AND DRAINAGE PIPES.
12 PROVIDE HOT AND COLD WATER MIXING SET TO HANDBASIN AND INSTALL LIQUID SOAP AND PAPER TOWEL DISPENSERS AND FIX "HAND WASH ONLY" SIGN ADJACENT TO SOAP DISPENSER.
13 RECESS ALL LIGHT FITTINGS INTO CEILINGS WITH APPROVED LIGHT DIFUSER COVER TO PREVENT FOOD CONTAMINATION AND DUST.
14 ENSURE NO GAPS OR VOIDS IN KITCHEN JOINERY.
15 PROVIDE ANY STAINLESS STEEL BENCHES WITH A 300MM MIN SPLASHBACK
16 ALLS WINDOWS TO BE 300MM ABOVE PREPARATION BENCHES.

TEST PROJECT USAGE ONLY

No.	Date	Issue Notes
CC-A	02-Sep-26	FOR CC SUBMISSION

Consultant / Notes:
SURVEY BY
REGISTERED SURVEYORS
PO BOX

COPYRIGHT
THIS DRAWING IS THE PROPERTY OF LYLE MARSHALL AND PARTNERS P/L AND MAY ONLY BE USED FOR THE PURPOSE FOR WHICH IT WAS COMMISSIONED & IN ACCORDANCE WITH THE TERMS OF ENGAGEMENT FOR THAT COMMISSION. UNAUTHORISED USE OF THIS DRAWING IS PROHIBITED.

FOR CC SUBMISSION

Design By: EMMC	Job No.: 5187-26		
Drawn By: EMMC	Scale: NTS		
Reviewed By: EMMC	Date: 02-Sep-26	Sheet No.: A405 of	Issue: CC-A
Passed By: EMMC	Date of Issue:		

Regulated Design Record

Project Address:

Project Title:

Consent No: DA18/0471.03

Body Corporate Reg No:

Drawing Title: EXTERNAL WINDOW AND DOOR SCHEDULE

Drawing No: 5187-26-A500

Rev	Date dd.mm.yy	Description	DEP Full Name	Reg No
CC-A	02/09/26	FOR CC SUBMISSION	ERICA MARSHALL-EVANS	DEP 0001207

External Doors Schedule

SW 2760

Refer to 'External Doors Schedule' & 'External Windows Schedule' drawings. 13-08-26

LEVEL	IMAGE	ID CC	ID DA	Width (mm)	Height (mm)	Configuration	Supplier	Additional Informations	Location	Comments
GROUND FLOOR	2100 / 1800	GD-01	D02	1800	2100	Hinged Left Door	TBA	D LEVER TYPE HANDLE	Bulky Waste Area	50L092 ABLOY LOCK SYSTEM TO BE INSTALLED TO WASTE ROOMS
	2100 / 920	GD-02	D-01	920	2100	Hinged Right Door-Outward Opening	TBA	D LEVER TYPE HANDLE	Exit door - Wattle Lane	ENTRY DOOR
	2100 / 1220	GD-03	D-03	1220	2100	DOUBLE DOOR - OUTWARD OPENING	TBA	D LEVER TYPE HANDLE	Water meter Room	
	2100 / 1220	GD-04	D-03	1220	2100	DOUBLE DOOR - OUTWARD OPENING	TBA	D LEVER TYPE HANDLE	Gas Meter Room	
	2100 / 1220	GD-05	D-03	1220	2100	DOUBLE DOOR - OUTWARD OPENING	TBA	D LEVER TYPE HANDLE	Electrical room	
	2100 / 810	GD-06	D-04	810	2100	Hinged Left Door-Outward Opening	TBA	D LEVER TYPE HANDLE	Fire Pump Room	Fire Exit Door FRL-/120/30
	2200 / 5500	GD-07	D-05	5500	2200	Garage Shutter Door	PaneLift -Grange - PFT3	B&D Sectional overhead door	Garage	Fire Exit Door FRL-/120/30
	2100 / 920	GD-08	FD-01	920	2100	Hinged Left Door	TBA	Outward Opening	Exit door - Parklawn Pl	Fire Exit Door FRL-/120/30

Internal Windows Schedule

NSW 2760

13-08-26

LEVEL	IMAGE	ID	Qty (pc)	Size Width (mm)	Size Height (mm)	Configuration	Supplier/ Product Code	Location	Comments
GROUND FLOOR	2400 / 2400	IW-	5	2400	2400	BI-FOLDING	TBA	Café/Lobby	POWDERCOATED ALUMINIUM FRAME STANDARD SINGLE GLAZED

External Windows Schedule

SW 2760

13-08-26

LEVEL	IMAGE	ID CC	ID DA	Qty (pc)	Size Width (mm)	Size Height (mm)	Configuration	Supplier/ Product Code	Location	Comments
GROUND FLOOR	1730 / 2100	W-01	G-01	1	1730	2400	Hinged Double Swing Glass Door	TBA	Lobby	POWDERCOATED ALUMINIUM FRAME STANDARD SINGLE GLAZED
	2100 / 2400	W-02	G-02	1	2100	2400	Sliding+Fixed	TBA	Lobby	POWDERCOATED ALUMINIUM FRAME STANDARD SINGLE GLAZED
	800 / 2400	W-03	G-06	2	800	2400	Fixed Glass	TBA	Café	POWDERCOATED ALUMINIUM FRAME STANDARD SINGLE GLAZED
	1400 / 1980 / 825	W-04	G-04	1	1980	1400	BI-FOLDING	TBA	Café	POWDERCOATED ALUMINIUM FRAME STANDARD SINGLE GLAZED

External Windows Schedule

SW 2760

13-08-26

LEVEL	IMAGE	ID CC	ID DA	Qty (pc)	Size Width (mm)	Size Height (mm)	Configuration	Supplier/ Product Code	Location	Comments
LEVEL3	1750 / 2100	W-06	W-06 L3	8	1750	2100	Sliding+Fixed	TBA	Living Rooms	POWDERCOATED ALUMINIUM FRAME STANDARD SINGLE GLAZED
	750 / 1600	W-07	W-07 L3	2	750	1600	Fixed panel	TBA	Hallways	POWDERCOATED ALUMINIUM FRAME STANDARD SINGLE GLAZED
	1800 / 2100	W-09	W-09 L3	2	1800	2100	Sliding+Fixed	TBA	Balconies	POWDERCOATED ALUMINIUM FRAME STANDARD SINGLE GLAZED

External Windows Schedule

SW 2760

13-08-26

LEVEL	IMAGE	ID CC	ID DA	Qty (pc)	Size Width (mm)	Size Height (mm)	Configuration	Supplier/ Product Code	Location	Comments
LEVEL 1	1750 / 2100	W-06	W-06 L1	8	1750	2100	Sliding+Fixed	TBA	Living Rooms	POWDERCOATED ALUMINIUM FRAME STANDARD SINGLE GLAZED
	750 / 1600	W-07	W-07 L1	1	750	1600	Fixed panel	TBA	Hallways	POWDERCOATED ALUMINIUM FRAME STANDARD SINGLE GLAZED
	1800 / 2100	W-09	W-09 L1	3	1800	2100	Sliding+Fixed	TBA	Balconies	POWDERCOATED ALUMINIUM FRAME STANDARD SINGLE GLAZED

13-08-26

LEVEL	IMAGE	ID CC	ID DA	Qty (pc)	Size Width (mm)	Size Height (mm)	Configuration	Supplier/ Product Code	Location	Comments
LEVEL 2	1750 / 2100	W-06	W-06 L2	8	1750	2100	Sliding+Fixed	TBA	Living Rooms	POWDERCOATED ALUMINIUM FRAME STANDARD SINGLE GLAZED
	750 / 1600	W-07	W-07 L2	2	750	1600	Fixed panel	TBA	Hallways	POWDERCOATED ALUMINIUM FRAME STANDARD SINGLE GLAZED
	1800 / 2100	W-09	W-09 L2	2	1800	2100	Sliding+Fixed	TBA	Balconies	POWDERCOATED ALUMINIUM FRAME STANDARD SINGLE GLAZED

External Windows Schedule

SW 2760

13-08-26

LEVEL	IMAGE	ID CC	ID DA	Qty (pc)	Size Width (mm)	Size Height (mm)	Configuration	Supplier/ Product Code	Location	Comments
LEVEL4	610 / 1200	W-10	W-10 L4	3	610	1200	Single Hung	TBA	Unit 4-1	POWDERCOATED ALUMINIUM FRAME STANDARD SINGLE GLAZED
	2100 / 2100	W-11	W-11 L4	1	2100	2100	Sliding + Fixed	TBA	Unit 4-1 Balcony	POWDERCOATED ALUMINIUM FRAME STANDARD SINGLE GLAZED
	2400 / 2100	W-12	W-12 L4	2	2400	2100	Sliding + Fixed	TBA	Communal Private Open Space	POWDERCOATED ALUMINIUM FRAME STANDARD SINGLE GLAZED
	770 / 1650	W-13	W-13 L4	6	770	1650	Operable Louvre	TBA	Communal Area	POWDERCOATED ALUMINIUM FRAME STANDARD SINGLE GLAZED

DOOR LOCKS & HARDWARE

32.DOOR LOCKS AND WINDOW LOCKS TO BE INSTALLED IN ACCORDANCE WITH AS4145.2-2008 LOCKSETS AND HARDWARE FOR DOORS AND WINDOWS.
33. ALL DOOR LOCKSETS, LATCHES AND ASSOCIATED HARDWARE TO COMPLY WITH THE NCC 2022 AND RELEVANT AUSTRALIAN STANDARDS.
34. DOORS IN REQUIRED EXITS, FORMING PART OF A REQUIRED EXIT OR IN A PATH OF TRAVEL TO A REQUIRED EXIT SHALL BE FITTED WITH LATCHING DEVICES COMPLYING WITH NCC 2022 D3D26.
35. LATCHING DEVICES SHALL BE READILY OPERABLE FROM THE EGRESS SIDE WITHOUT A KEY AND

CONSTRUCTION CERTIFICATE NOTES:

GENERAL

1.ALL WORK SHALL COMPLY WITH THE NCC (BCA VOL 1 2025 EDITION), CONDITIONS OF CONSENT, AND THE RELEVANT AUSTRALIAN STANDARDS AS LISTED BELOW.
2. FOR CONSTRUCTION CERTIFICATE ONLY NOT FOR CONSTRUCTION. ALL DIMENSIONS SHALL BE VERIFIED ON SITE PRIOR TO COMMENCEMENT OF WORK. DO NOT SCALE DRAWINGS.
3.BYDA BEFORE YOU DIG FOR ANY UNDERGROUND SERVICES.WWW.BYDA.COM.AU
4. ANY DISCREPANCIES BETWEEN DRAWINGS, SITE CONDITIONS, OR SPECIFICATIONS SHALL BE REFERRED TO THE ARCHITECT BEFORE PROCEEDING.
5. DRAWINGS ARE TO BE READ IN CONJUNCTION WITH THE ARCHITECTURAL SPECIFICATION AND ALL CONSULTANT DRAWINGS AND SPECIFICATIONS, INCLUDING STRUCTURAL, CIVIL, HYDRAULIC, MECHANICAL, ELECTRICAL, FIRE, LANDSCAPE AND SECTION J DOCUMENTATION.
6. THE BUILDER SHALL CARRY OUT ALL WORK IN ACCORDANCE WITH: NCC (BCA VOL 1 2025), CONDITIONS OF DEVELOPMENT CONSENT, WHS REGULATION (NSW), AND RELEVANT AUSTRALIAN STANDARDS.
7. PROVIDE ADEQUATE PROTECTION TO EXISTING STRUCTURES, PUBLIC SPACES AND SERVICES DURING CONSTRUCTION.
8. THE BUILDER SHALL COORDINATE ALL TRADES AND ENSURE PENETRATIONS, SET-OUTS AND SERVICE ROUTES ARE ACCURATELY LOCATED.
9. ALL DIMENSIONS TO BE CHECKED ON SITE AND SETOUT BY A SURVEYOR PRIOR TO COMMENCEMENT OF CONSTRUCTION.

27. ALL EXTERNAL GLAZED DOORS INCLUDING FRAMES AND ASSOCIATED COMPONENTS SHALL COMPLY WITH AS2047.

36. DOOR HARDWARE TO ACCESSIBLE DOORS SHALL COMPLY WITH AS 1428.1:2021.
37. WHERE FIRE DOORS ARE REQUIRED, DOOR LEAF, FRAME, CLOSER, LOCKSET AND ASSOCIATED HARDWARE SHALL BE COMPATIBLE WITH THE REQUIRED FIRE-RESISTANCE LEVEL AND TESTED/APPROVED AS PART OF THE FIRE DOOR ASSEMBLY.
38. ALL LOCKSETS AND HARDWARE SHALL BE SELECTED AND INSTALLED IN ACCORDANCE WITH THE MANUFACTURER'S REQUIREMENTS AND RELEVANT AUSTRALIAN STANDARDS.

0 2 3 5 m

FOR CC SUBMISSION

No.	Date	Issue Notes
CC-A	02-Sep-26	FOR CC SUBMISSION

Consultant / Notes:
SURVEY BY
REGISTERED SURVEYORS
PO BOX

COPYRIGHT
THIS DRAWING IS THE PROPERTY OF LYLE MARSHALL AND PARTNERS P/L AND MAY ONLY BE USED FOR THE PURPOSE FOR WHICH IT WAS COMMISSIONED & IN ACCORDANCE WITH THE TERMS OF ENGAGEMENT FOR THAT COMMISSION. UNAUTHORISED USE OF THIS DRAWING IS PROHIBITED.

Design By	EMMC
Drawn By	EMMC
Reviewed By	EMMC
Passed By	EMMC
Job No.	5187-26
Scale	1:200
Date	02-Sep-26
Date of Issue	
Sheet No.	A500
of	
Issue	CC-A

TEST PROJECT ONLY

SAMPLE PROJECT A - ARCHITECTURAL - RECRUITMENT ASSESSMENT ONLY

Regulated Design Record

Project Address:

Project Title:

Consent No: DA18/0471.03 | Body Corporate Reg No:

Drawing Title: MATERIALS AND FINISHES SCHEDULE | Drawing No: 5187-26-A501

Rev	Date dd.mm.yy	Description	DEP Full Name	Reg No
CC-A	02/09/26	FOR CC SUBMISSION	ERICA MARSHALL-EVANS	DEP 0001207

CONSTRUCTION CERTIFICATE NOTES:

GENERAL

1.ALL WORK SHALL COMPLY WITH THE NCC (BCA VOL 1 2025 EDITION), CONDITIONS OF CONSENT, AND THE RELEVANT AUSTRALIAN STANDARDS AS LISTED BELOW.
2. FOR CONSTRUCTION CERTIFICATE ONLY NOT FOR CONSTRUCTION. ALL DIMENSIONS SHALL BE VERIFIED ON SITE PRIOR TO COMMENCEMENT OF WORK. DO NOT SCALE DRAWINGS.
3.BYDA BEFORE YOU DIG FOR ANY UNDERGROUND SERVICES.WWW.BYDA.COM.AU
4. ANY DISCREPANCIES BETWEEN DRAWINGS, SITE CONDITIONS, OR SPECIFICATIONS SHALL BE REFERRED TO THE ARCHITECT BEFORE PROCEEDING.
5. DRAWINGS ARE TO BE READ IN CONJUNCTION WITH THE ARCHITECTURAL SPECIFICATION AND ALL CONSULTANT DRAWINGS AND SPECIFICATIONS, INCLUDING STRUCTURAL, CIVIL, HYDRAULIC, MECHANICAL, ELECTRICAL, FIRE, LANDSCAPE AND SECTION J DOCUMENTATION.
6. THE BUILDER SHALL CARRY OUT ALL WORK IN ACCORDANCE WITH: NCC (BCA VOL 1 2025), CONDITIONS OF DEVELOPMENT CONSENT, WHS REGULATION (NSW), AND RELEVANT AUSTRALIAN STANDARDS.
7. PROVIDE ADEQUATE PROTECTION TO EXISTING STRUCTURES, PUBLIC SPACES AND SERVICES DURING CONSTRUCTION.
8. THE BUILDER SHALL COORDINATE ALL TRADES AND ENSURE PENETRATIONS, SET-OUTS AND SERVICE ROUTES ARE ACCURATELY LOCATED.
9. ALL DIMENSIONS TO BE CHECKED ON SITE AND SETOUT BY A SURVEYOR PRIOR TO COMMENCEMENT OF CONSTRUCTION.
30. WHERE POSSIBLE, EXTERNAL SURFACES THAT ARE ACCESSIBLE TO THE PUBLIC ARE TO INCORPORATE AN APPROPRIATE ANTI-GRAFFITI RESISTANT COATING, INCLUDING SIGNAGE, STREET FURNITURE, PLANTER BOXES AND OTHER EXPOSED EXTERNAL SURFACES. THE COATING IS TO BE COMPATIBLE WITH THE NOMINATED SURFACE FINISH AND APPLIED IN ACCORDANCE WITH THE MANUFACTURER'S RECOMMENDATIONS.

MATERIALS AND FINISHES


Planting - P


Dark Grey Face Brick - B


Painted Concrete Panels- C1


Painted V-groove panels - C2


Black Powdercoated Handrail - H


Black Aluminium Framed Windows- W



Black Aluminium Framed Doors - D


Black Aluminium Framed Louvres - L


LEGEND

BOUNDARY LINE


NGL NATURAL GROUND LEVEL

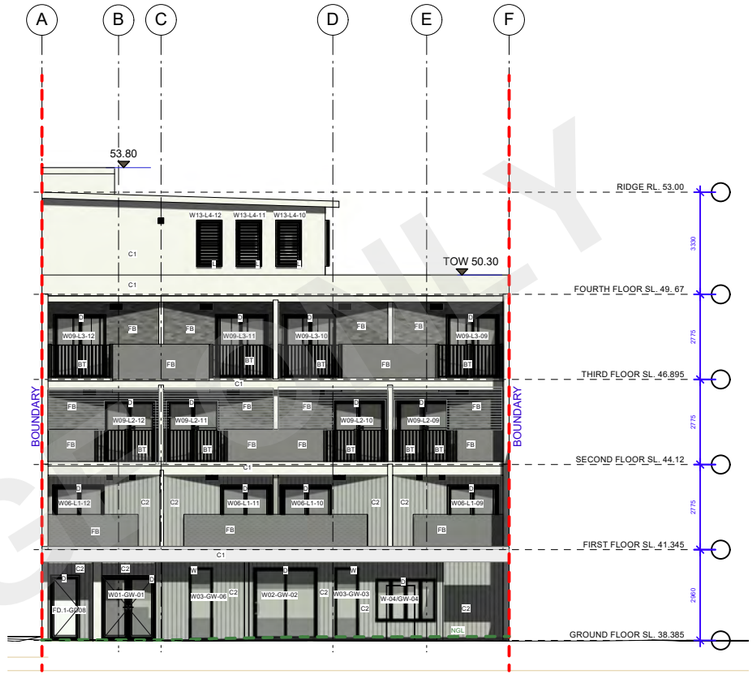

SOUTH FACING ELEVATION
scale 1:200

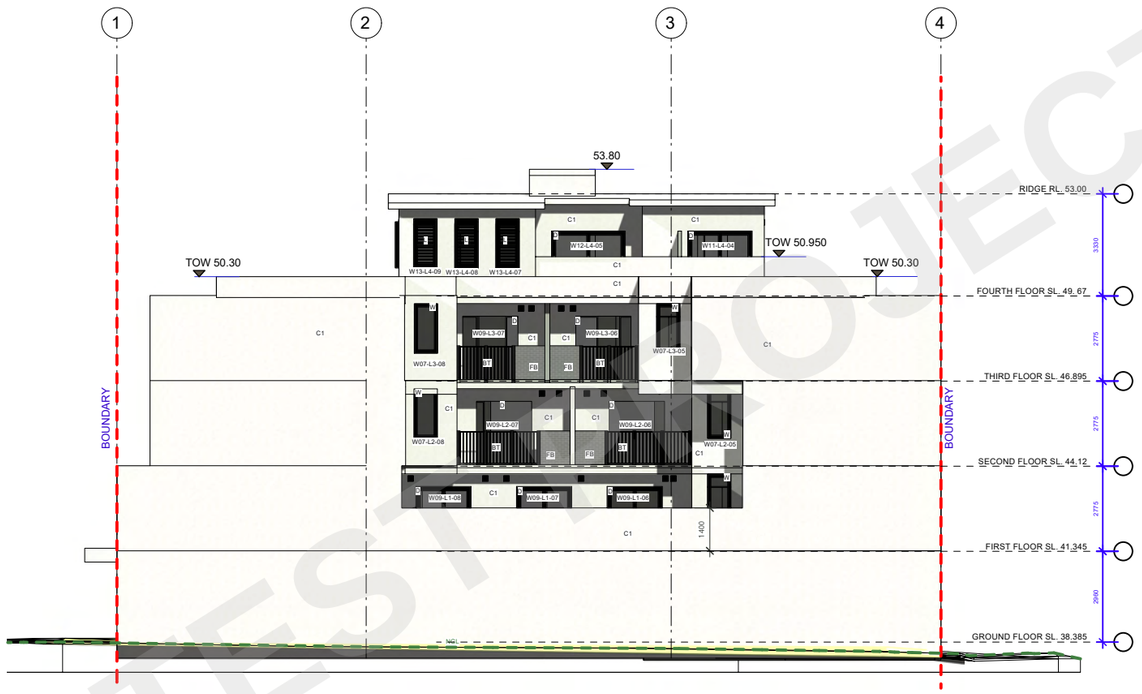

EAST FACING ELEVATION
scale 1:200

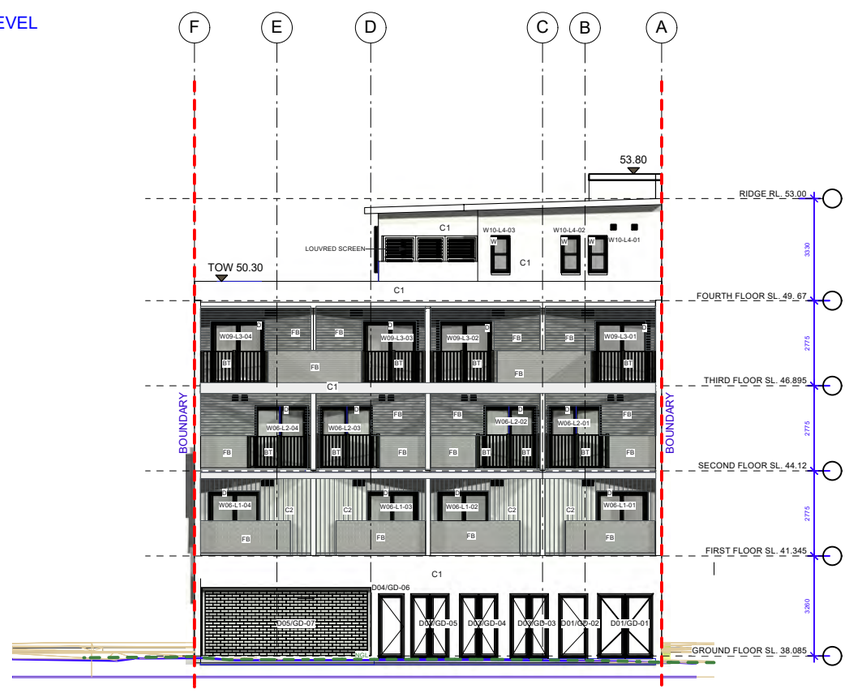

NORTH FACING ELEVATION
scale 1:200

0 2 3 5 m

FOR CC SUBMISSION

No.	Date	Issue Notes
CC-A	02-Sep-26	FOR CC SUBMISSION

Consultant / Notes:
SURVEY BY
REGISTERED SURVEYORS
PO BOX

COPYRIGHT
THIS DRAWING IS THE PROPERTY OF LYLE MARSHALL AND PARTNERS P/L AND MAY ONLY BE USED FOR THE PURPOSE FOR WHICH IT WAS COMMISSIONED & IN ACCORDANCE WITH THE TERMS OF ENGAGEMENT FOR THAT COMMISSION. UNAUTHORISED USE OF THIS DRAWING IS PROHIBITED.

LE

Design By: EMMC	Job No.: 5187-26		
Drawn By: EMMC	Scale: 1:200		
Reviewed By: EMMC	Date: 02-Sep-26	Sheet No.: A501 of	Issue: CC-A
Passed By: EMMC	Date of Issue:		