MULTI DWELLING

REGULATED DESIGN RECORD


PROJECT ADDRESS:			
PROJECT TITLE:	MULTI DWELLING		
CONSENT NO:	STR208 - 2023	BODY CORPORATE REG NO:	DEP0001320
DRAWING TITLE:	COVER SHEET/ DRAWING SCHEDULE	DRAWING NO:	STR000


REV	DATE DD.MM.YY	DESCRIPTION	DP FULL NAME	REG NO
E	10-09-26	ISSUED FOR CONSTRUCTIO		

DRAWING SCHEDULE A3

SHEET #	SHEET TITLE	REVISIONS	DATE
STR000	COVER SHEET/ DRAWING SCHEDULE	E	10-09-26
STR001	GENERAL NOTES AND DETAILS - 01	E	10-09-26
STR002	GENERAL NOTES AND DETAILS - 02	E	10-09-26
STR200	GROUND FLOOR FOOTING & SLAB PLAN	E	10-09-26
STR202	GROUND FLOOR COLUMN AND WALL LAYOUT PLAN	D	10-09-26
STR210	GROUND FLOOR LOADING PLAN	E	10-09-26
STR220	SECTION AND DETAILS	E	10-09-26
STR230	SECTION AND DETAILS	E	10-09-26
STR240	SECTION AND DETAILS	E	10-09-26
STR250	SECTION AND DETAILS	E	10-09-26
STR260	SECTION AND DETAILS	E	10-09-26
STR261	SECTION AND DETAILS	E	10-09-26
STR262	SECTION AND DETAILS	D	10-09-26
STR270	SECTION AND DETAILS	E	10-09-26
STR280	STAIR DETAILS	E	10-09-26
STR281	STAIR DETAILS	E	10-09-26
STR282	STAIR DETAILS	E	10-09-26
STR283	STAIR DETAILS	E	10-09-26
STR290	LIFT DETAILS	E	10-09-26
STR291	SECTION AND DETAILS	D	10-09-26
STR500	LEVEL 1 FLOOR PLAN	E	10-09-26
STR501	LEVEL 1 WALL LAYOUT PLAN	E	10-09-26
STR510	LEVEL 1 BOTTOM REINFORCEMENT PLAN	E	10-09-26
STR511	LEVEL 1 TOP REINFORCEMENT PLAN	E	10-09-26
STR520	LEVEL 1 LOADING PLAN	E	10-09-26
STR530	SECTION AND DETAILS	E	10-09-26
STR540	SECTION AND DETAILS	E	10-09-26
STR600	LEVEL 2 FLOOR PLAN	E	10-09-26
STR601	LEVEL 2 WALL LAYOUT PLAN	E	10-09-26
STR610	LEVEL 2 BOTTOM REINFORCEMENT PLAN	E	10-09-26
STR611	LEVEL 2 TOP REINFORCEMENT PLAN	E	10-09-26
STR620	LEVEL 2 LOADING PLAN	E	10-09-26
STR630	SECTION AND DETAILS	E	10-09-26
STR700	LEVEL 3 FLOOR PLAN	E	10-09-26
STR701	LEVEL 3 WALL LAYOUT PLAN	E	10-09-26
STR710	LEVEL 3 BOTTOM REINFORCEMENT PLAN	E	10-09-26
STR711	LEVEL 3 TOP REINFORCEMENT PLAN	E	10-09-26
STR720	LEVEL 3 LOADING PLAN	E	10-09-26
STR730	SECTION AND DETAILS	E	10-09-26
STR800	LEVEL 4 FLOOR PLAN	E	10-09-26
STR801	LEVEL 4 WALL LAYOUT PLAN	E	10-09-26
STR810	LEVEL 4 BOTTOM REINFORCEMENT PLAN	E	10-09-26
STR811	LEVEL 4 TOP REINFORCEMENT PLAN	E	10-09-26
STR820	LEVEL 4 LOADING PLAN	E	10-09-26
STR830	SECTION AND DETAILS	E	10-09-26
STR900	ROOF PLAN	E	10-09-26
STR901	ROOF BOTTOM REINFORCEMENT PLAN	E	10-09-26
STR902	ROOF TOP REINFORCEMENT PLAN	E	10-09-26
STR903	ROOF LOADING PLAN	E	10-09-26
STR904	SECTION AND DETAILS	E	10-09-26
STR905	SECTION AND DETAILS	E	10-09-26

TOTAL: 51

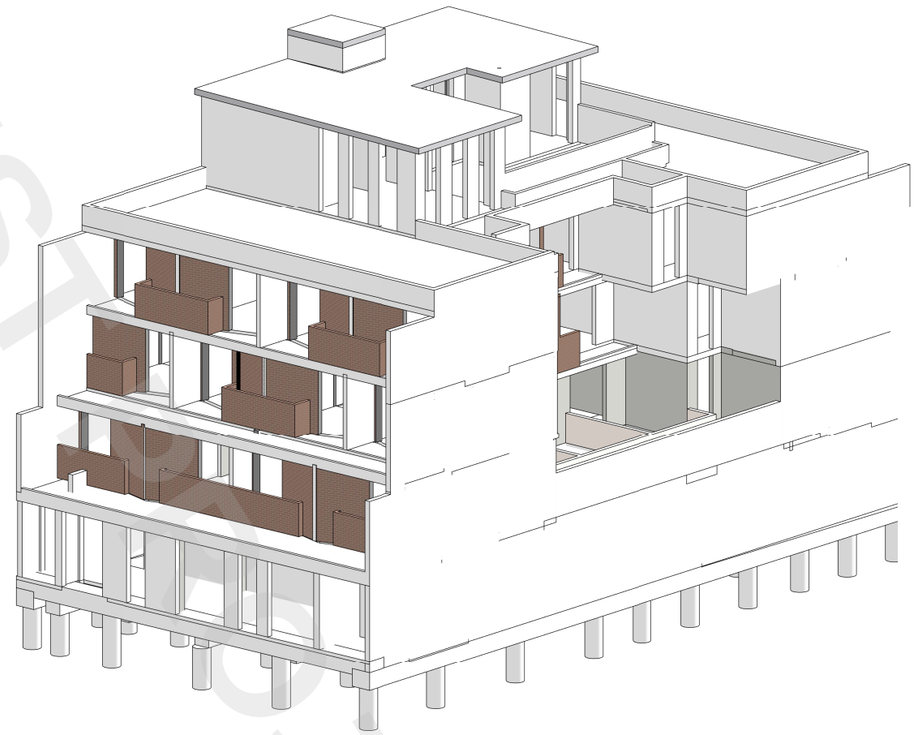

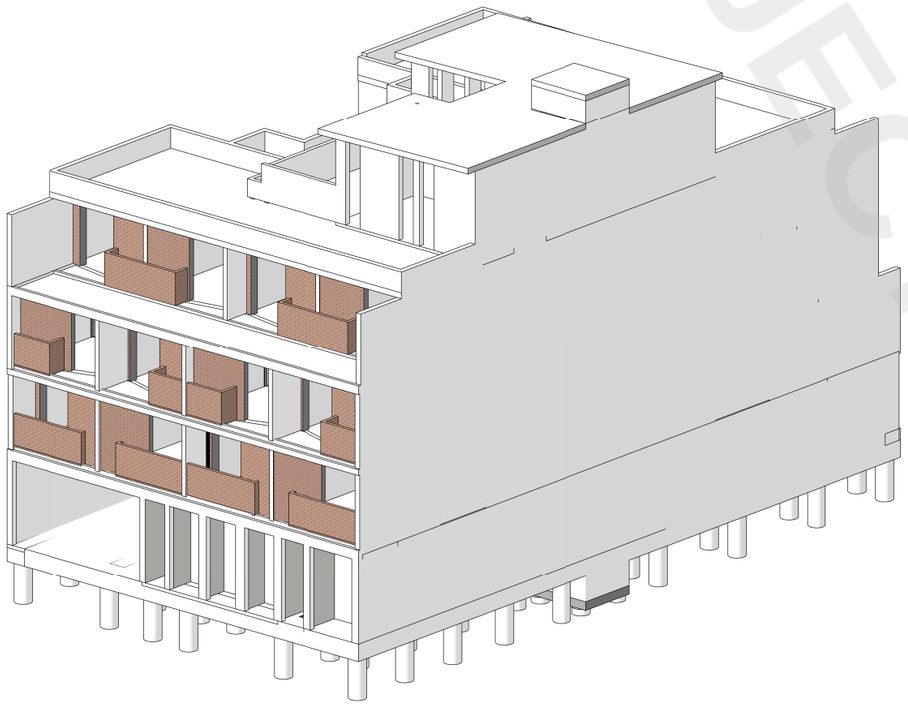

TYPICAL DETAIL (WHEN REQUIRED)

NOTE:
- LOCATION OF SWT & RWT TO BE CONFIRMED BY CIVIL / STORM WATER ENGINEER PRIOR TO CONSTRUCTION
- DRAWINGS TO BE READ & PRINTED IN COLOUR.

NOTE:
- FIRST FLOOR STRUCTURAL FRAMING NOT SHOWN FOR CLARITY. PLEASE REFER TO SHEET STR500 FOR DETAILS.

PRINT IN COLOUR

MODULAR ENGINEERS P/L

Structural Engineering | Civil Engineering
Stormwater Engineering | Flood Engineering
Traffic Engineering | Temporary works

ABN : 66 646 960 929
TEL. : 02 873 08473
MOB. : 04 208 98999
EMAIL :
WEBSITE :
ADDRESS :

CLIENT:

PROJECT TITLE:
MULTI DWELLING

SHEET NAME:
COVER SHEET/ DRAWING SCHEDULE

PROJECT NUMBER:
175-2026

INTERNAL REVISIONS:

ISSUE	DATE	DESCRIPTION	BY
E	10-09-26	ISSUED FOR CONSTRUCTION	D.A.
D	08-09-26	ISSUED FOR CONSTRUCTION	D.A.
C	24-08-26	ISSUED FOR PRELIMINARY	D.A.
B	21-08-26	ISSUED FOR PRELIMINARY	D.A.

AMENDMENTS

DRAWN : L.M. DATE: 17-07-26
DESIGNED : A.O. REVISION DATE:
QA CHECK : A.O. 10-09-26

APPROVED BY:

RPEQ: 28316
NPER: 5358554
DATE: 10-09-26

ISSUE TYPE:
CONSTRUCTION

SHEET NUMBER:
STR000

SHEET SIZE: **A3**
REVISION: **E**

SAMPLE PROJECT A - STRUCTURAL REV E - CURRENT - RECRUITMENT ASSESSMENT ONLY

TEST PROJECT USE ONLY

NOTE: THE DESIGN AND DETAILS SHOWN ON THESE DRAWINGS ARE APPLICABLE TO THIS PROJECT ONLY AND MAY NOT BE REPRODUCED IN WHOLE OR IN PART OR BE USED FOR ANY OTHER PROJECT OR PURPOSE WITHOUT THE WRITTEN PERMISSION OF WITH WHOM COPYRIGHT RESIDES.

REGULATED DESIGN RECORD

PROJECT ADDRESS:	
PROJECT TITLE:	MULTI DWELLING
CONSENT NO:	STR208 - 2023
BODY CORPORATE REG NO:	DEP0001320
DRAWING TITLE:	GENERAL NOTES AND DETAILS - 01
DRAWING NO:	STR001

REV	DATE DD.MM.YY	DESCRIPTION	DP FULL NAME	REG NO
E	10-09-26	ISSUED FOR CONSTRUCTIO		

LEGEND

	DENOTED MASS CONCRETE PIERS TAKEN TO SHALE (REFER TO SECTION AND DETAILS)
	DENOTED REINFORCED CONCRETE PIERS TAKEN TO SHALE (REFER TOSECTION AND DETAILS)
	DENOTES SCREW PILE
PF1	DENOTED PAD CONCRETE FOOTING (REFER TO SECTION AND DETAILS)
	DENOTED COMPLETE WAFFLE POD 1090 x 1090 STANDARD POD
SP/(O/U)	DENOTED STEEL POST OVER/UNDER (REFER TO SCHEDULE)
TP/(O/U)	DENOTED TIMBER POST OVER/UNDER (REFER TO SCHEDULE)
DS/(O/U)	DENOTED TIMBER DOUBLE STUDS (OVER/UNDER)
	DENOTES EXISTING BRICK/TIMBER WALLS OVER
	DENOTES DEMOLISH BRICK/TIMBER WALLS (ALTERATION AND ADDITION PROJECTS)
	DENOTES NEW BRICK/TIMBER WALLS OVER (ALTERATION AND ADDITION PROJECTS)
	DENOTES COLUMN/WALLS UNDER
	DENOTES CONCRETE COLUMN/WALLS OVER
	DENOTES BLOCK WORK WALLS OVER
	DENOTES REINFORCED DINCEL WALLS OVER
EP	DENOTES ENGAGE PIER
I.J.	DENOTES ISOLATION JOINT-10mm POLYETHYLENE BETWEEN WALLS/COLUMNS AND NEW SLAB
S.J.	DENOTES SAWN CONTROL JOINT (REFER TO DETAIL)
K.J.	DENOTES KEY CONSTRUCTION JOINT (REFER TO DETAIL)
G.D.	DENOTES GRADED DRAIN
STEP	DENOTES SLAB STEP (REFER TO ARCHITECTURE)
	DENOTES 30mm WET AREA (REFER TO DETAIL)
TR	DENOTES 3N12 TRIMER BAR 1.5m LONG
N.G.L.	DENOTES NATURAL GROUND LEVEL
RD.L.	DENOTES ROAD LEVEL
B	DENOTES BRACING (REFER TO DETAILS)
BONDEK 125	DENOTES BONDEK DIRECTION AND THICKENS
F21	DENOTES FLOOR JOIST WITH DIRECTION (REFER TO SCHEDULE)
TB1	DENOTES TIMBER BEAM (REFER TO SCHEDULE)
SB1	DENOTES STEEL BEAM (REFER TO SCHEDULE)

CONCRETE QUALITY

ELEMENT	SLUMP	AGGREGATE (MAX. SIZE)	CEMENT TYPE	f'c
SLAB ON GROUND	80mm	20mm	A	25MPa U.O.N.
PIERS	80mm	20mm	A	25MPa U.O.N.
FOOTING	80mm	20mm	A	25MPa U.O.N.
COLUMN AND WALLS	80mm	20mm	A	REFER TO SCHEDULE
SUSPENDED SLAB	80mm	20mm	A	32MPa U.O.N.
BEAMS	80mm	20mm	A	32MPa U.O.N.

REINFORCEMENT COVER SCHEDULE

MEMBER	COVER (mm)			EXPOSURE CLASSIFICATION
	TOP	BOTTOM	SIDES	
INTERNAL SLAB ON GROUND	30mm	30mm	30mm	A1
EXTERNAL SLAB ON GROUND	40mm	40mm	40mm	A2
SUSPENDED SLAB INTERNAL	30mm	30mm	30mm	A1
SUSPENDED SLAB EXTERNAL	40mm	40mm	40mm	B1
FOOTING	50mm	50mm	50mm	B1
COLUMNS AND WALLS	40mm	40mm	40mm	A2

BRICK LINTEL SCHEDULE

OPENING SIZE(mm)	INTERNAL SKIN	EXTERNAL SKIIN	END BEARING
UP TO 900mm	100 x 8mm FLAT BAR	100 x 6mm FLAT BAR	100mm
1200	100 x 10mm FLAT BAR	100 x 8mm FLAT BAR	100mm
1500	100 x 100 x 8mm ANGLE	100 x 100 x 6mm ANGLE	150mm
2100	100 x 100 x 8mm ANGLE	100 x 100 x 6mm ANGLE	150mm
2400	100 x 100 x 8mm ANGLE	100 x 100 x 8mm ANGLE	150mm
2700	100 x 100 x 10mm ANGLE	100 x 100 x 10mm ANGLE	150mm
3000	100 x 100 x 12mm ANGLE	100 x 100 x 12mm ANGLE	150mm

NOTES:
A. ALL STEEL LINTELS TO BE HOT DIPPED GALVANIZED OR BY ANTI RUST PAINTING.
B. ABOVE ALL LINTELS, PROVIDE M.E.T MASONRY REINFORCEMENT FOR 2 COURSES AND CONTINUE 1000mm PAST OPENING.
C. MINIMUM THREE COURSES OF BRICK ABOVE THE LINTEL.

PIERING USED FOR WAFFLE POD SLABS

PIER BEARING STRATA	BEARING SOIL CAPACITY	2 STOREY BUILDING	PIER EMBEDMENT DEPTH
SHALE TO ROCK	450 KPa	300Ømm BORED PIERS AT 1800mm MAX CTS	1000mm EMBEDMENT INTO STRATA
STIFF CLAY	250 KPa	450Ømm BORED PIERS AT 1800mm MAX CTS	1500mm EMBEDMENT INTO STRATA
CONTROLLED FILL (CLAY)	150 KPa	-	
SAND	100 KPa	-	

LAPPING OF MESH

REINFORCEMENT IN RAFT AND SLABS SHALL HAVE COVERS AND BE SPLICED IN ACCORDANCE WITH THE FOLLOWING:


a. COVER FOR THE REINFORCEMENT SHALL BE 40mm TO UNPROTECTED GROUND, 40mm TO EXTERNAL EXPOSURE, 30mm TO A MEMBRANE IN CONTACT WITH THE GROUND, AND 20mm TO AN INTERNAL SURFACE. THE SLAB MESH SHALL BE PLACED TOWARDS THE TOP OF THE RAFT OR SLAB WITHIN THE ZONE DEFINED BY THESE LIMITS.

b. RAFT OR SLAB MESH SHALL BE LAPPED BY ONE FULL PANEL OF MESH SO THAT THE TWO OUTERMOST TRANSVERSE WIRES OF ONE SHEET OVERLAP THE TWO OUTERMOST TRANSVERSE WIRES OF THE SHEET BEING LAPPED, SUCH AS SHOWN IN.

c. TRENCH MESH SHALL HAVE AL CROSS WIRE CUT FLUSH WITH THE OUTER MAIN WIRES.. TRENCH MESH IN BEAMS SHALL BE OVERLAPPED BY THE WIDTH OF THE FABRIC AT T- AND L INTERSECTION. TRENCH MESH SHALL BE SPLICED, WHERE NECESSARY, BY LAP OF 500MM.


d. REINFORCING BARS SHALL HAVE A LAP LENGTH AT SPLICES NOT LESS THAN 500 MM, AT T- AND L- INTERSECTIONS, THE BARS SHALL BE CONTINUED ACROSS THE FULL WIDTH OF THE INTERSECTION. AT L-INTERSEXTIONS. ONE OUTER BAR SHALL BE BENT AND CONTINUED 500 MM, OR A BENT LAP BAR 500MM LONG ON EACH LEG SHALL BE PROVIDED.

e. SERVICES PENETRATIONS SHALL BE PERMITTED THROUGH THE MIDDLE THIRD OF THE EDGE AND STIFFENING BEAMS. THE EFFECT OF OTHER SERVICES PENETRATIONS SHALL BE TAKEN INTO ACCOUNT BY THE PROVISION OF EXTRA CONCRETE DEPTH OR REINFORCEMENT.

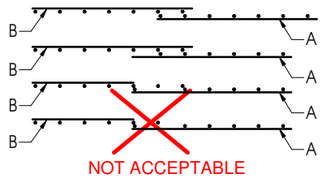


TYPICAL LAPPING MESH DETAILS

NOT TO SCALE

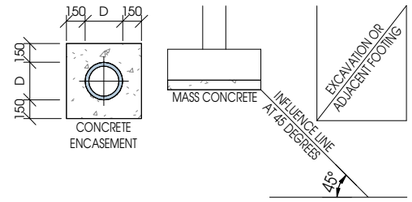

TYPICAL BACK PROPPING SEQUENCE

NOT TO SCALE

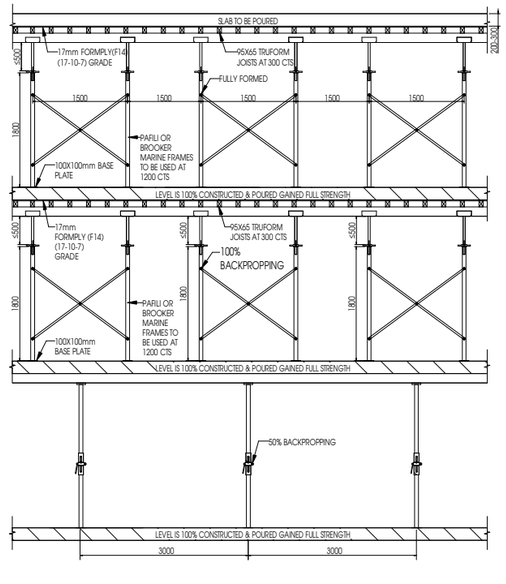

TYPICAL BACK PROPPING SEQUENCE

NOT TO SCALE

GENERAL NOTES OF BACKPROPPING FOR SLABS UP TO 300mm

1. THE FORMS TO A NEWLY POURED SLAB MAY BE REMOVED AND THE SLAB BACKPROPPED WHEN THE CONCRETE HAS REACHED A STRENGTH OF 24 MPA AND A MINIMUM AGE OF 7 DAYS. A MINIMUM OF TWO TEST CYLINDERS ARE REQUIRE TO VERIFY CONCRETE STRENGTH.
2. WHEN REMOVING FORMS, REMOVE FORMS UP TO MID-SPAN ONLY IN ANY ONE BAY BEFORE BACKPROPPING.
3. PROPS/BACKPROPS TO GROUND LEVEL WHEN SUPPORTING NEW FORMWORK TO LEVEL 1 ARE TO BE RELEASED AND TIGHTENED IMMEDIATELY PRIOR TO POURING THE NEW LEVEL 2 SLAB. THIS PROCESS IS TO OCCUR ONE PANEL AT TIME SEQUENTIALLY ACROSS THE WHOLE FLOOR, BEFORE POURING THE NEW LEVEL 2 SLAB THE LEVELS OF FORMS MUST BE CHECKED AND ADJUSTED AS NECESSARY. PROPS MUST ALSO BE MONITORED DURING POUR THE RELEASE AND TIGHTEN PROCESS IS TO OCCUR ONLY ONCE.
4. PT SLABS, THERE MUST ALWAYS BE AT LEAST 2 FLOORS SUPPORTING THE SLAB TO BE POURED (EXCLUSIVE OF NEWLY CAST FLOOR) THE LOWEST LEVEL OF BACKPROPPS MAY ONLY BE REMOVED WHEN THE LAST SLAB POURED HAS SATISFIED THE CRITERIA OF ITEM 1 ABOVE AND THE PROPS UNDER THIS NEWEST SLAB, HAVE BEEN RELEASED AND RE-TIGHTENED.
5. RC SLABS, THERE MUST ALWAYS BE AT LEAST 3 FLOORS SUPPORTING THE SLAB TO BE POURED (EXCLUSIVE OF NEWLY LAST FLOOR) THE LOWEST LEVEL OF BACKROPS MAY ONLY BE REMOVED WHEN THE LAST SLAB POURED HAS SATISFIED THE CRITERIA OF ITEM 1 ABOVE AND THE PROPS UNDER THIS NEWEST SLAB, HAVE BEEN RELEASED AND RE-TIGHTENED.
6. NO BACKPROPPS ARE TO BE REMOVED UNTIL THE CONCRETE IN THE SLAB HAS ACHIEVED ITS DESIGN STRENGTH AND THERE ARE THE REQUIRED NUMBER OF LEVELS TO PROPS, AND BACKPROPPS ABOVE THE SLAB IN QUESTION TO SUPPORT.
7. WHEN REMOVING BACKPROPPS, PROPS AT MID-SPAN ARE TO BE REMOVED FIRST FOLLOWED IN SEQUENCE BY THOSE TOWARDS THE SUPPORT POINTS. THE UPPERMOST SLAB.
8. BRICKWOR/BLOCKWORK MUST NOT BE BUILT ON CONCRETE SLABS OR BEAMS UNTIL FORMWORK / BACKPROPPS SUPPORTING THE SAME HAVE BEEN REMOVED.

PRINT IN COLOUR

MODULAR ENGINEERS P/L
Structural Engineering | Civil Engineering
Stormwater Engineering | Flood Engineering
Traffic Engineering | Temporary works
ABN : 66 646 960 929
TEL. : 02 873 08473
MOB. : 04 208 98999
EMAIL :
WEBSITE :
ADDRESS :

CLIENT:

PROJECT TITLE:
MULTI DWELLING

SHEET NAME:
GENERAL NOTES AND DETAILS - 01

PROJECT NUMBER:
175-2026

INTERNAL REVISIONS:

ISSUE	DATE	DESCRIPTION	BY
E	10-09-26	ISSUED FOR CONSTRUCTION	D.A.
D	08-09-26	ISSUED FOR CONSTRUCTION	D.A.
C	24-08-26	ISSUED FOR PRELIMINARY	D.A.
B	21-08-26	ISSUED FOR PRELIMINARY	D.A.

AMENDMENTS

DRAWN : L.M. DATE: 17-07-26
DESIGNED : A.O. REVISION DATE:
QA CHECK : A.O. 10-09-26
APPROVED BY:

RPEQ: 28316
NPER: 5358554
DATE: 10-09-26

ISSUE TYPE:
CONSTRUCTION

SHEET NUMBER:
STR001

SHEET SIZE: **A3** REVISION: **E**

SAMPLE PROJECT A - STRUCTURAL REVIEW - CURRENT - RECRUITMENT ASSESSMENT ONLY

NOTE: THE DESIGN AND DETAILS SHOWN ON THESE DRAWINGS ARE APPLICABLE TO THIS PROJECT ONLY AND MAY NOT BE REPRODUCED IN WHOLE OR IN PART OR BE USED FOR ANY OTHER PROJECT OR PURPOSE WITHOUT THE WRITTEN PERMISSION OF WITH WHOM COPYRIGHT RESIDES.

REGULATED DESIGN RECORD

PROJECT ADDRESS:	
PROJECT TITLE:	MULTI DWELLING
CONSENT NO:	STR208 - 2023
BODY CORPORATE REG NO:	DEP0001320
DRAWING TITLE:	GENERAL NOTES AND DETAILS - 02
DRAWING NO:	STR002

REV	DATE DD.MM.YY	DESCRIPTION	DP FULL NAME	REG NO
E	10-09-26	ISSUED FOR CONSTRUCTIO		

GENERAL:

A. THESE ENGINEERING DRAWINGS HAVE BEEN PREPARED FROM INFORMATION AVAILABLE AT THE TIME OF ISSUE. AS THIS INFORMATION MAY BE THE SUBJECT OF CHANGE PRIOR TO OR DURING CONSTRUCTION THE CONTRACTOR IS TO ADVISE THE ENGINEER WHERE DISCREPANCIES OCCUR.
B. THESE DRAWINGS SHALL NOT BE USED FOR FINAL SETOUT OF THE PROJECT UNLESS SPECIFICALLY STATED.
C. INSPECTIONS ARE REQUIRED TO BE PERFORMED BY A DULY APPOINTED INSPECTOR FROM . THESE INSPECTIONS ARE REQUIRED TO BE PERFORMED IN ACCORDANCE WITH THE SCOPE OF INSPECTIONS PREPARED BY .THE INSPECTOR IS TO BE GIVEN A MINIMUM OF 48 HOURS NOTICE.
D. PRIOR TO THE COMMENCEMENT OF WORKS THE CONTRACTOR IS TO IDENTIFY ALL EXISTING SERVICES. ANY DAMAGE TO EXISTING SERVICES IS TO BE RECTIFIED AT THE CONTRACTORS EXPENSE. SERVICES SHOWN ON DRAWINGS ARE INDICATIVE ONLY.
E. DURING CONSTRUCTION THE CONTRACTOR SHALL BE RESPONSIBLE FOR MAINTAINING THE STABILITY OF THE WORKS AND ENSURE NO PART IS OVERSTRESSED.
F. WORKMANSHIP AND MATERIALS SHALL BE IN ACCORDANCE WITH THE CURRENT AUSTRALIAN STANDARDS AND BCA STATUTORY REQUIREMENTS, EXCEPT WHERE VARIED BY THE CONTRACT DOCUMENTS.
G. THE CONTRACTOR SHALL BE RESPONSIBLE FOR ENSURING THAT SUFFICIENT TOLERANCES ARE PROVIDED AND INTEGRATED THROUGHOUT ALL THE ELEMENTS OF THE WORKS.
H. ALL NON-LOAD BEARING ELEMENTS SHALL BE KEPT CLEAR OF THE STRUCTURE SOFFIT BY AN ALLOWANCE DETERMINED FROM SPAN/250 OR CANTILEVER/125 BUT NOT LESS THAN 20mm, UNLESS NOTED OTHERWISE ON THE DRAWINGS.
I. ALL DIMENSIONS ARE IN MILLIMETERS UNLESS STATED OTHERWISE.
J. SUPERIMPOSED DEAD LOADS AND LIVE LOADS HAVE BEEN DETERMINED IN ACCORDANCE WITH AS1170.1 AND ARE SHOWN ON THE GENERAL ARRANGEMENT DRAWINGS.

FOUNDATION MAINTENANCE AND DRAINAGE:

A. ALL LOOSE MATERIAL AND WATER TO BE CLEANED OUT OF THE FOUNDATION. FORMWORK TO BE USED WHERE THE SIDES OF THE FOUNDATION ARE NOT STABLE.
B. 5. A 50mm MINIMUM BLINDING LAYER SHOULD BE APPLIED TO THE BASE OF ALL FOUNDATIONS. WHERE THE FOUNDING MATERIAL IS DEEPER THAN REQUIRED FOR THE FOOTING THE EXCAVATION IS TO BE BACKFILLED WITH A WEAK MIX CONCRETE (N10) TO THE UNDERSIDE OF THE FOOTING.
C. ALL WORKMANSHIP AND MATERIALS MUST BE IN ACCORDANCE WITH AS2870.
D. SURFACE DRAINAGE MUST BE PLANNED AND DEVELOPED TO AVOID WATER ENTERING AGAINST OR NEAR THE FOOTING. THE GROUND IN THE DIRECT LOCALITY OF THE PERIMETER FOOTING, INCLUDING THE FOUND UPHILL FROM THE SLAB ON CUT-AND-FILL SITES , MUST BE GRADED TO FALL 50MM MINIMUM AWAY FROM THE FOOTING OVER A DISTANCE OF 1 M AND SHAPED TO PREVENT THE ENTRANCE OF WATER. FILLING MUST BE PLACED ADJACENT TO THE BUILDING, THE FILLING MUST BE COMPACTED AND GRADED TO SAFEGUARD DRAINAGE OF WATER AWAY FROM THE BUILDING.
E. ANY PRIVATE SERVICE TRENCHES MUST BE SLOPED AWAY FROM THE BUILDING AND SUITABLY BACKFILLED, IN ACCORDANCE WITH AS2870.
F. MODERATELY & HIGH REACTIVE SITES REQUIRE SUPPLEMENTARY PLUMBING SERVICES & REQUIREMENTS.
G. AVOID PENETRATIONS OF FOOTINGS AND EDGE BEAMS. HOWEVER, NECESSARY PENETRATIONS MUST BE SLEEVED TO ALLOW FOR MOVEMENT.
H. AVOID DRAINAGE & PLUMBING BELOW THE SLAB UNLESS REQUIRED. REFER TO AS/NZS 3500 CLAUSE 4.10
I. IT IS ESSENTIAL THAT THE CELL POLYETHYLENE MEMBRANE MUST BE SURROUNDING ALL PIPE WORK INCLUDING STORMWATER & SANITARY PLUMBING DRAIN PIPE PENETRATIONS
J. ALL WALLS AND COLUMNS SHALL BE CONCENTRIC WITH THE SUPPORTING FOOTINGS UNLESS NOTED OTHERWISE ON THE DRAWINGS.
K. WHERE AN EXCAVATION IS REQUIRED OR EXISTS BELOW THE BASE OF A FOOTING THE SIDE OF THE EXCAVATION SHALL BE LOCATED AWAY FROM EDGE OF FOOTING BY THE AME DISTANCE THAT THE EXCAVATION IS BELOW FOOTING BASE. WHERE THIS CANNOT BE ACHIEVED, SHALL BE CONTACTED FOR FURTHER DIRECTION. SHALL BE CONTACTED FOR FURTHER DIRECTION. MASS CONCRETE IS TO EXTEND TO THE INFLUENCE LINE AS REQUIRED.

GENERAL CONCRETE NOTES:

A. CONCRETE WORK SHALL BE IN ACCORDANCE WITH AS3600 AND WITH THE PROJECT SPECIFICATIONS.
B. CONSTRUCTION JOINTS SHALL BE PROPERLY FORMED AND USED ONLY WHERE SHOWN ON DRAWINGS OR SPECIFICALLY APPROVED BY .
C. ALL THICKNESS SHOWN ARE MINIMUM STRUCTURAL REQUIREMENTS, NO REDUCTION THICKNESS DUE TO FALLS OR TOPPING IS PERMITTED. REFER ARCHITECT DRAWINGS FOR ALL SLAB FALLS AND CONFIRMATION OF SLAB STEPS.
D. UNLESS A GROOVE LINE ALLOWANCE HAS BEEN NOTED ON THE DRAWINGS, NO GROOVE LINES ARE PERMITTED, EXCEPT AT SLAB LINES. ALL GROOVE LINES ARE TO BE SUBMITTED TO FOR APPROVAL.
E. THE FACE OF ALL CONCRETE AGAINST WHICH NEW CONCRETE IS TO BE CAST IS TO BE THOROUGHLY MECHANICALLY SCRABBLED, FULLY EXPOSING THE AGGREGATE MATRIX.
F. NO PENETRATIONS GREATER THAN 150mm DIAMETER, OR EMBEDMENT OF PIPES GREATER THAN 40mm DIAMETER OTHER THAN THOSE SHOWN ON THE STRUCTURAL DRAWINGS SHALL BE MADE IN CONCRETE SLABS. FOR ALL OTHER CONCRETE MEMBERS NO PENETRATIONS, CHASES OR EMBEDMENT SHALL BE MADE WITHOUT PRIOR APPROVAL BY .
G. CONDUITS GREATER THAN 25mm DIAMETER CAST INTO CONCRETE MEMBERS SHALL BE SPACED AT A MAXIMUM DISTANCE POSSIBLE AND UNDER NO CIRCUMSTANCES CLOSER THAN A CLEAR SPACING OF TWICE THE LARGER CONDUIT DIAMETER FROM PARALLEL REINFORCEMENT OR ANY OTHER CONDUIT.
H. THE CHARACTERISTIC COMPRESSIVE STRENGTH (f'c) AT 28 DAYS OF IN PLACE CONCRETE SHALL BE AS NOTED ON THE DRAWINGS.
I. MAXIMUM AGGREGATE SIZE.....20mm.
J. SLUMP.....80mm.
K. ALL CONCRETE SHALL BE VIBRATED.
L. ALL CONCRETE SHALL BE CURED IN ACCORDANCE WITH THE SPECIFICATION.
M. ALL CONCRETE SHALL BE SAMPLED AND TESTED IN ACCORDANCE WITH AS1012 AND THE PROJECT SPECIFICATION.
N. ALL FORMWORK SHALL COMPLY WITH AS3610.
O. EACH FLOOR SHALL BE FULLY PROPPED TO THE FLOOR BELOW IN ACCORDANCE WITH AS3610 (FORMWORK CODE).
P. THE FLOOR BELOW SHALL BE BACKPROPPED THROUGH A MINIMUM OF TWO STOREY BELOW. THIS RESULTS IN A MINIMUM OF THREE STOREY PROPPED AT ALL TIMES. (REFER TO TYPICAL BACK PROPPING SEQUENCE DIAGRAM).
Q. PROPS MAY BE REMOVED AFTER 28 DAYS OF CURING OR AFTER 14 DAYS IF THE CONCRETE HAS REACHED ITS CHARACTERISTIC STRENGTH (AS PROVED BY CYLINDER TEST RESULTS).

REINFORCEMENT:

A. REINFORCEMENT IS TO BE MANUFACTURED IN ACCORDANCE WITH AS1302 AND SHALL BE FIXED AS SHOWN ON DRAWINGS.
B. REINFORCEMENT IS SHOWN IN DRAWINGS AND IS NOT NECESSARILY IN TRUE PROJECTION. CONNECTIONS TO REINFORCEMENT MUST BE MADE ONLY AT THE LOCATIONS SHOWN. IF REINFORCEMENT IS NEEDED ELSEWHERE IT MUST BE APPROVED BY THE PROJECT ENGINEER.
C. MODIFYING REINFORCEMENT/S IS NOT PERMITTED UNLESS SHOWN ON THE STRUCTURAL DRAWINGS OR APPROVED BY THE PROJECT ENGINEER.
D. THE BAR SIZE IS INDICATED BY A NUMBER AFTER THE SYMBOL, WHICH INDICATES THE BAR DIAMETER IN MILLIMETERS.
E. ALL REINFORCEMENT BARS AND FABRIC MUST FULFIL WITH AS4671. FABRIC MUST BE SOURED IN THE FORM OF FLAT SHEETS.
F. REINFORCEMENT SPACING NOMINATED ON DRAWINGS IS TO ASSIST SCHEDULER AND STEEL FIXER TO ASSESS TOTAL NUMBER OF BARS REQUIRED. WHERE BARS PLACED IN ACCORDANCE WITH SPACING NOMINATED FOUL WITH OTHER STRUCTURAL REQUIREMENTS, PREFERENCE IS TO BE GIVEN TO RELOCATING BARS BY LOCALLY ADJUSTING SPACING TO ENABLE ASSEMBLY OF REINFORCEMENT TO BE COMPLETED. ENGINEER IS TO BE CONTACTED IN THE EVENT THAT REINFORCEMENT IS NEEDED TO BE CUT ON SITE PRIOR TO CONTINUING.
G. REINFORCEMENT MATERIAL IS INDICATED BY THE SYMBOLS BELOW:

Y - DEFORMED BAR GRADE 400
N - DEFORMED BAR GRADE 500 (NORMAL DUCTILITY)
R - PLAIN ROUND BAR GRADE 250
W- PLAIN WIRE GRADE 450
F - FABRICS GRADE 450
TM - TRENCH MESH

H. FABRIC REINFORCEMENT MUST BE LAPPED ONE MESH PLUS 30 mm AT SPLICES AND PLACED ON BAR CHAIRS AT 1m CTS.
I. REINFORCING BARS MUST HAVE A LAP LENGTH AT SPLICES NOT LESS THAN 500mm UP TO A BAR DIA. OF 12mm, AND 700mm UP TO A BAR DIA. OF 16mm. UNLESS NOTED OTHERWISE.
J. WELDING OF REINFORCEMENT BARS IS NOT PERMITTED UNLESS APPROVED.
K. BENEATH THE SLAB FABRIC REINFORCING BARS SHOULD BE TIED IF USED OR OTHERWISE PLACED ON CHAIRS.
L. SPLICES IN REINFORCEMENT MADE IN POSITIONS OTHER THAN SHOWN, MUST BE APPROVED BY THIS CONSULTANCY'S ENGINEER. WHERE LAP LENGTH IS NOT SHOWN, LAPPING MUST BE APPROPRIATE TO IMPROVE THE FULL STRENGTH OF THE REINFORCEMENT.
M. CONCRETE COVERS NOTED ARE MEASURED FROM THE FORMWORK OR GROUND FACE TO THE OUTERMOST REINFORCEMENT COMPONENT. ie. IN COLUMNS AND BEAMS TO THE OUTSIDE OF TIES OR LIGATURES.
N. COVER SHALL BE AS NOTED ON THE RELEVANT DRAWINGS.
O. COVER TO BE MAINTAINED DURING POURING BY THE USE OF PLASTIC CHAIRS OR PLASTIC TIPPED METAL CHAIRS.
P. WHERE NO REINFORCEMENT IS SHOWN ON THE DRAWING AT RIGHT ANGLES TO THE MAIN REINFORCEMENT DISTRIBUTION REINFORCEMENTS IS TO BE PROVIDED.
Q. PRIOR TO POURING CONCRETE REINFORCEMENT AND VOID FORMERS MUST BE FIXED INTO POSITION THROUGH PROPRIETARY SPACERS, BAR CHAIRS AND LIGATURES TO ACCOMPLISH THE REQUIRED REINFORCEMENT POSITION AND COVER. ALL REINFORCEMENT MUST BE SUPPORTED ON A PLASTIC SPREAD OR STEEL CHAIRS AT A MAXIMUM OF 4 PER POD.

AGGRESSIVE SOILS:

A. ANY CONTAMINATING MATERIALS SHOULD BE REMOVED OFF THE SITE IN ACCORDANCE WITH LOCAL AUTHORITY GUIDELINES.
B. BUILDINGS WITH MASONRY OR CONCRETE THAT IS UNPROTECTED FROM SALINE OR ACID SULFATE SOILS MUST BE PROTECTED IN ACCORDANCE WITH THE SITE MANAGEMENT PLANS PRODUCED BY THE CONTRACTED GEOTECHNICAL AND LOCAL AUTHORITIES.
C. ANY PROTECTION REQUIREMENTS MUST BE DELIVERED TO THIS OFFICE BY THE CONTRACTOR PRECEDING TO COMMENCEMENT OF DESIGN.

CLAY BRICK MASONRY:

A. MASONRY, MORTAR AND BUILT MASONRY COMPONENTS MUST COMPLY WITH AS3700 AND AS4773 AND THE PROJECT SPECIFICATION.
B. THE SLAB IS PLANED FOR ARTICULATION REQUIREMENTS. ARTICULATION JOINTS SHALL BE CARRIED OUT IN ACCORDANCE WITH AS4773 AND CEMENT, CONCRETE AND AGGREGATES AUSTRALIA BOOKLET TECHNICAL NOTE 61 (ARTICULATED WALLING) AND AS3700 SECTION 12 16.4.
C. MASONRY UNITS TO HAVE A MINIMUM CHARACTERISTIC UNCONFINED STRENGTH OF 20MPa IN ACCORDANCE WITH AS2733.
D. MASONRY TO BE BEDDED IN FRESHLY PREPARED MORTAR.

1. CONCRETE BLOCKS :
MORTAR MIX TO BE UNIFORMLY MIXED IN A RATIO OF ONE PART CEMENT, ONE PART LIME AND SIX PARTS SAND CONFORMING TO AS2701. 'BRICKIES LOAM' SHALL NOT BE USED.
2. CLAY BRICKS :
MORTAR MIX TO BE UNIFORMLY MIXED IN THE RATIO OF ONE PART CEMENT, THREE PARTS SAND AND ONE FOURTH PART LIME CONFORMING TO AS2701. 'BRICKIES LOAM' SHALL NOT BE USED.

E. MASONRY ARTICULATION JOINTS SHALL BE POSITIONED AT ANY POSITION WHERE NEW BRICKWORK ALIGNS WITH OLD BRICKWORK.
F. WHERE MASONRY ARTICULATION IS INDICATED AT THE SIDE OF OPENINGS WITH BRICKWORK ABOVE THE OPENING, A SLIP JOINT AROUND THE END OF THE LINTEL MUST BE DELIVERED WITH CARE.
G. MASONRY MUST BE LAYED IN FRESHLY PRIMED MORTAR. CONCRETE BLOCKS: MORTAR MIX TO BE UNIFORMLY MIXED TO A RATIO OF ONE-PART CEMENT, ONE-PART LIME AND SIX PARTS SAND CONFORMING TO AS2701.

H. CLAY BLOCKS: MORTAR MIX TO BE UNIFORMLY MIXED TO A RA 110 OF ONE-PART CEMENT, THREE PARTS SAND AND ONE FOURTH PART LIME CONFORMING TO AS2701.
I. GROUT MUST HAVE A COMPRESSIVE STRENGTH (F'C) OF 20 MPa AT 28 DAYS, A SLUMP PF 125mm IN A 150mm SLUMP CONE, A MAXIMUM AGGREGATE SIZE OF 10mm AND MUST BE IN ACCORDANCE WITH AS3700.
J. THE LAYING OF MASONRY MUST BE FULL FACE WITH CROSS JOINTS ENTIRELY FILLED, JOINT THICKNESS SHALL NOT EXCEED 12mm.
K. THE CAVITY MUST NOT SURPASS 100mm AND SHALL NOT BE SMALLER THAN 40mm UNLESS NOTED OTHERWISE. CAVITY MUST BE KEPT CLEAN AND CLEAR OF IMPEDIMENTS AND COMPLIANT WITH NCC.
L. VERTICAL JOINTS UNLESS NOTED OTHERWISE BRICKS WITH A POTENTIAL FIVE YEAR EXPANSION OF 1 mm/m. BUILDER MUST NOTIFY PACE STRUCTURAL IF DISTINGUISHING EXPANSION OF BRICK UNITS IS DIFFERENT BY 10% OR MORE.
M. RAKING OF JOINTS IS NOT ALLOWABLE WITHOUT AUTHORIZATION FROM AN ENGINEER.
N. ALL WALLS ARE TO BE KEPT STEADY AT ALL STAGES OF CONSTRUCTION AND MUST NOT BE OVER STRESSED AT ANY POINT DURING DEVELOPMENT.
O. UNLESS NOTED OTHERWISE, NO CHASES OR RECESSES IS ACCEPTABLE IN MASONRY WALLS WITHOUT THE APPROVAL OF THE ENGINEER.
P. WALL TIES TO BE DEVELOPED IN AND FLEXED TO THE TIMBER FRAME 300 EACH SIDE OF ANY ARTICULATION JOINT, AT EVERY THIRD (3RD) COURSE.
Q. NON LOAD BEARING WALLS MUST BE DISCONNECTED FROM CONCRETE ABOVE BY 12MM THICK CLOSE CELL POLYETHYLENE STRIPS.
R. BEDDING OF MASONRY SHALL BE FULL FACE WITH CROSS JOINTS COMPLETELY FILLED. JOINT THICKNESS SHALL NOT EXCEED 12mm.
S. PROVIDE WALL TIES AT 600mm MAXIMUM CENTERS VERTICALLY AND HORIZONTALLY. REFER TO MASONRY DETAILS FOR WALL TIE SETOUT AT OPENINGS.

GENERAL MAINTENANCE:

A. IN ACCORDANCE TO AS3660 IT IS PERMITTED TO PROTECT THE RESIDENCE FROM TERMITES IF IT IS NECESSARY.
B. INSPECTIONS OF THE RESIDENCE AND IMMEDIATE SURROUNDINGS MUST BE CARRIED OUT BY A FULLY QUALIFIED PEST PROFESSIONAL YEARLY BY THE OWNER.
C. THE MAINTENANCE OF THE SITE IS WHOLLY THE RESPONSIBILITY OF THE OWNER. ALL SANCTIONS OUTLINED IN THE FOLLOWING SHOULD BE CARRIED OUT IN ITS ENTIRETY: CISRO BOOKLET FOUNDATION MAINTENANCE AND FOOTING PERFORMANCE: A HOME OWNERS GUIDE.
D. S2870 APPENDIX B 'PERFORMANCE CRITERIA AND FOUND All ON MAINTENANCE' AND APPENDIX C 'CLASSIFICATION OF DAMAGE DUE TO FOUNDATION MOVEMENTS'.
E. THE ENDORSED DISTANCE OF A NEW TREE ON SITE MUST BE EQUAL OR GREATER THAN 75% OF THE MATURE TREE HEIGHT FOR M SITES, 100% OF THE MATURE HEIGHT FOR H1 AND H2 SITES, AND 150% OF THE MATURE HEIGHT FOR E SITES.
F. GARDEN BEDS ADJACENT TO THE HOUSE SHOULD BE REMOVED. ADDITIONALLY, AVOID OVER WATERING GARDENS CLOSE TO THE RESIDENTIAL FOOTINGS.
G. ANY FUTURE CRACKING OCCURRING IN THE SLAB AND/OR FOOTINGS MUST BE ASSESSED BY A QUALIFIED PEST EXPERT AND THIS CONSULTANCY.

STRUCTURAL STEELWORK NOTES:

A. MATERIALS FABRICATIONS AND ERECTION TO BE STRICTLY IN ACCORDANCE WITH AS1538, AS1554, AND 4100 AND WITH THE SPECIFICATIONS.
B. UNLESS NOTED OTHERWISE ALL STEEL SHALL BE IN ACCORDANCE WITH BHP 300 PLUS TO ASNZ3679.1 (1996)- HOT ROLLED SECTIONS GRADE 300 TO AS3679.2 (1991)- WELDED SECTIONS.
C. GRADE 250 TO AS3678 (1996)- HOT ROLLED PLATES & SLABS. GRADE 350 TO AS1163 (1993)- HOLLOW SECTIONS
D. WELDING SHALL COMPLY WITH AS 1554.
E. WELDS SHALL BE 6mm CONTINUOUS FILLET UNLESS NOTED OTHERWISE. WELDS TO PURLING CLEATS SHALL BE 4mm cfw.
F. ELECTRODES SHALL BE E41XX OR E48XX.
G. BOLTS DENOTED 46/S - ARE COMMERCIAL BOLTS OF STRENGTH GRADE 46 TO AS1111 - SNUG TIGHT.
H. BOLTS DENOTED 8.8/S,8.8/TB AND 8.8/TF ARE HIGH STRENGTH STRUCTURAL BOLTS OF STRENGTH GRADE 8.8 TO AS 1252; 8.8/S DENOTED BOLTS SNUG TIGHT; 8.8/TB AND 8.8/TF DENOTES BOLTS FULLY TENSIONED TO AS1511; 8.8/TB DENOTES BEARING JOINT; 8.8/TF DENOTES FRICTION JOINT.
I. LOAD INDICATOR WASHERS SHALL BE USED UNDER THE THE BOLT HEAD FOR ALL 8.8/TF 8.8/TB BOLTS.
J. BOLTS SHALL BE M20 UNLESS NOTED NOTED OTHERWISE. BOLTS SHALL BE 8.8/S UNLESS NOTED OTHERWISE.
K. PURLIN BOLTS TO BE M12 - 4.6/S WITH A MINIMUM OF 2 BOLTS PER PURLIN END.
L. BOLT HOLES SHALL BE BOLT DIAMETER. +2mm FOR STEEL TO STEEL CONNECTIONS. +4mm FOR STEEL TO CONCRETE CONNECTIONS. +6mm FOR BASE PLATES.
M. ALL PLATES AND STIFFENERS SHALL BE 10mm THICK U.N.O. CORROSION PROTECTION.

	SURFACE PREPARATION	PRIMER
ALL U.N.O.	POWER WIRE BRUSH TO AS1627:2 CLASS 3	R.O.Z.C.
EMBEDDED ITEMS, SHELF ANGLES & EXPOSED STEELWORK		HOT DIPPED GALVANISED TO AS1650

N. CONCRETE ENCASED STEELWORK TO BE WRAPPED IN ACCORDANCE WITH AS 4100 AND TO HAVE 50mm MINIMUM COVER TO CONCRETE. LOCATION OF PURLOIN AND GRITS TO BE OBTAINED FROM ARCHITECTS
O. DRAWINGS OR ROOFING CONTRACTORS.
P. PROVIDE SEAL PLATES TO ENDS OF HOLLOW SECTIONS.
Q. ALL STRUCTURAL STEELWORK WHICH IS EXPOSED OR IN CONTACT WITH EXPOSED BRICKWORK OR BLOCKWORK AND ALL LINTELS, SHALL BE HOT DIP GALVANIZED UNLESS NOTED OTHERWISE.
R. ALL STEELWORK TO BE TEMPORARILY BUT SECURELY BRACED UNTIL ALL FINAL BRACING, CLADDING,AND STABILIZING BRICKWORK OR BLOCKWORK HAVE BEEN COMPLETED.
S. ARRANGE FOR CERTIFICATION FROM A QUALIFIED CONSULTANCY THAT THE TRUSSES ARE STRUCTURALLY SATISFACTORY.

ROOF SUPPORT AND LOADING:

A. ROOF LOADINGS MUST BE SUPPORTED BY PATENTED TRUSSES ONTO EXTERNAL WALLS ONLY UNLESS NOTED OTHERWISE.
B. PITCHED ROOF REQUIREMENTS MUST BE DELIVERED BY THE CONTRACTOR TO THIS CONSULTANCY IN ADVANCED OF DETAILING.
C. THE BASIS OF DESIGN MUST BE SAA LOADING CODE AS1170.1, AS 1170.2 AND SAA TIMBER STRUCTURE CODE AS1720.1.
D. PLAN OF THE ROOF TRUSSES MUST BE IN ACCORDANCE WITH THE WIND CLASSIFICATIONS AS SPECIFIED.
E. PROVIDE ANY TEMPORARY BRACING NEEDED TO MAINTAIN THE STRENGTH OF THE TRUSSES AT ALL STAGES OF PRODUCTION.
F. MAKE ALLOWANCES FOR SIZE AND LOCATIONS OF MECHANICAL SERVICES AND AIR CONDITIONING DUCTWORK IF APPLICABLE.
G. ARRANGE FOR CERTIFICATION FROM A QUALIFIED CONSULTANCY THAT THE TRUSSES ARE STRUCTURALLY SATISFACTORY.

PRINT IN COLOUR

MODULAR ENGINEERS P/L
Structural Engineering | Civil Engineering
Stormwater Engineering | Flood Engineering
Traffic Engineering | Temporary works
ABN : 66 646 960 929
TEL. : 02 873 08473
MOB. : 04 208 98999
EMAIL :
WEBSITE :
ADDRESS :

CLIENT:

PROJECT TITLE:
MULTI DWELLING

SHEET NAME:
GENERAL NOTES AND DETAILS - 02

PROJECT NUMBER:
175-2026

INTERNAL REVISIONS:

ISSUE	DATE	DESCRIPTION	BY
E	10-09-26	ISSUED FOR CONSTRUCTION	D.A.
D	08-09-26	ISSUED FOR CONSTRUCTION	D.A.
C	24-08-26	ISSUED FOR PRELIMINARY	D.A.
B	21-08-26	ISSUED FOR PRELIMINARY	D.A.

AMENDMENTS

DRAWN : L.M. DATE: 17-07-26
DESIGNED : A.O. REVISION DATE:
QA CHECK : A.O. 10-09-26
APPROVED BY:

RPEQ: 28316
NPER: 5358554
DATE: 10-09-26

ISSUE TYPE:
CONSTRUCTION

SHEET NUMBER:
STR002

SHEET SIZE: A3
REVISION: E

SAMPLE PROJECT A - STRUCTURAL REVIEW - CURRENT - RECRUITMENT ASSESSMENT ONLY

NOTE: THE DESIGN AND DETAILS SHOWN ON THESE DRAWINGS ARE APPLICABLE TO THIS PROJECT ONLY AND MAY NOT BE REPRODUCED IN WHOLE OR IN PART OR BE USED FOR ANY OTHER PROJECT OR PURPOSE WITHOUT THE WRITTEN PERMISSION OF WITH WHOM COPYRIGHT RESIDES.

REGULATED DESIGN RECORD

PROJECT ADDRESS:	
PROJECT TITLE:	MULTI DWELLING
CONSENT NO:	STR208 - 2023
BODY CORPORATE REG NO:	DEP0001320
DRAWING TITLE:	GROUND FLOOR FOOTING & SLAB PLAN
DRAWING NO:	STR200

REV	DATE DD.MM.YY	DESCRIPTION	DP FULL NAME	REG NO
E	10-09-26	ISSUED FOR CONSTRUCTIO		

REINFORCEMENT COVER SCHEDULE

ELEMENT	COVER (mm)			EXPOSURE CLASSIFICATION
	TOP	BOT	SIDES	
FOOTING	50mm	50mm	50mm	A2

CONCRETE QUALITY

ELEMENT	SLUMP	AGGREGATE (MAX. SIZE)	CEMENT TYPE	f'c
FOOTING	80mm	20mm	A	32 MPa

- ASSUMED ALLOWABLE BEARING CAPACITY OF ROCK = 400 kPa
- GEOTECHNICAL ENGINEER TO CONFIRM THE SAFE BEARING CAPACITY OF THE FOUNDING MATERIAL PRIOR TO CONSTRUCTION.

FOOTING SCHEDULE

MARK	SIZE	REINFORCEMENT	REMARKS
PF1	2370 x 2150 x 300D	N12-200 TOP & BOT. B.W.	
PF2	3000 x 3000 x 700D	N16-150 U-BARS, 600 COG, EACH WAY	
PF3	3700 x 3700 x 800D	N16-150 U-BARS, 700 COG, EACH WAY	
PF4	6400 x 7400 x 300D	N16-200 TOP & BOT. B.W.	


CONCRETE COLUMN SCHEDULE

MARK	SIZE	REINFORCEMENT	f'c
C1	300 x 1000	14N20 VERTICAL 3N12-200 TIES	32MPa
C2	300 x 1000	16N20 VERTICAL 3N12-200 TIES	32MPa

NOTE:
- BUILDER TO INSPECT BOUNDARIES OF THE PROPERTY FOR ANY EXISTING RETAINING WALLS OR FOOTINGS & INFORM IF CONDITION DIFFERS FROM DRAWINGS TO PROVIDE REQUIRED RETAINING WALL, SHORING OR UNDERPINNING INSTRUCTIONS.

PIER FOUNDING / GEOTECHNICAL NOTE:

- PIER DEPTHS AND FOUNDING LEVELS SHOWN ON THESE DRAWINGS ARE PRELIMINARY AND ARE SUBJECT TO CONFIRMATION BY A SUITABLY QUALIFIED GEOTECHNICAL ENGINEER.
- THE CURRENT GEOTECHNICAL INFORMATION IS INSUFFICIENT TO CONFIRM THE REQUIRED PIER FOUNDING DEPTH AND FOUNDING CONDITIONS. PRIOR TO CONSTRUCTION OF THE PIERS, THE GEOTECHNICAL ENGINEER SHALL CONFIRM:
  - SUITABLE FOUNDING MATERIAL AND MINIMUM FOUNDING DEPTH/LEVEL;
  - ALLOWABLE BEARING CAPACITY AT THE PIER FOUNDING LEVEL;
  - PRESENCE AND EXTENT OF ANY UNCONTROLLED FILL, SOFT/LOOSE SOILS OR OTHER UNSUITABLE MATERIAL;
  - GROUNDWATER CONDITIONS, WHERE RELEVANT; AND
  - THAT THE PROPOSED PIER FOUNDING CONDITIONS ARE SUITABLE FOR THE DESIGN LOADS.
- ALL PIERS SHALL BE FOUNDED INTO COMPETENT NATURAL MATERIAL AS CONFIRMED BY THE GEOTECHNICAL ENGINEER. PIER DEPTHS SHALL NOT BE TAKEN FROM THESE DRAWINGS AS A GUARANTEED FOUNDING DEPTH.
- ANY VARIATION FROM THE ASSUMED FOUNDING CONDITIONS SHALL BE REFERRED TO THE STRUCTURAL ENGINEER FOR REVIEW AND, WHERE REQUIRED, REDESIGN PRIOR TO CONSTRUCTION.

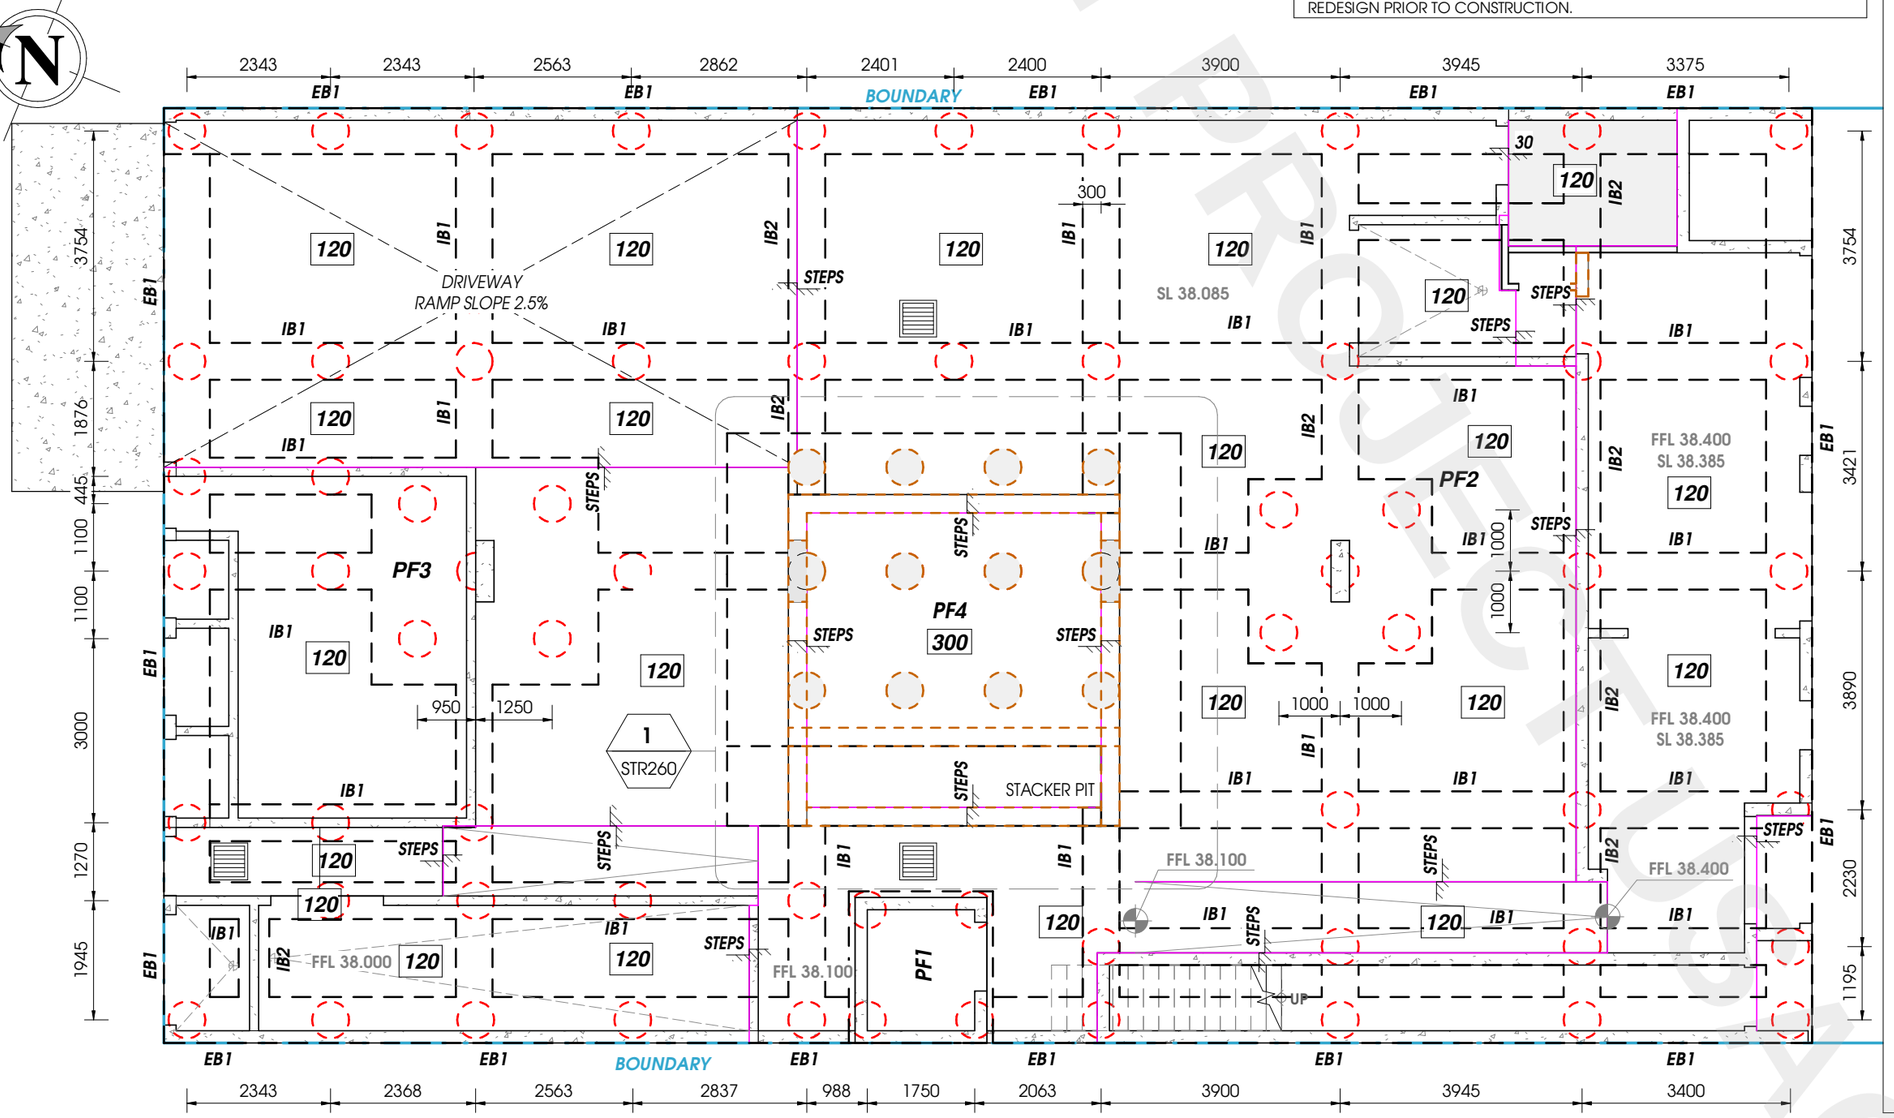

GROUND FLOOR SLAB LAYOUT AND FOOTING PLAN

SCALE: 1 : 100

NOTES:

RAFT SLAB:
A. DRAWING TO BE READ IN CONJUNCTION WITH ARCHITECTURE DRAWINGS .
B. REFER TO ARCHITECTURAL DRAWINGS FOR ALL SETOUT, LEVELS, STEPS, FOLDS & FALLS ETC.
C. REFER TO STORMWATER DRAINAGE DRAWINGS FOR LOCATION OF PUMP WELL AND SUMP PITS.
D. ASSUMED SITE IN ACCORDANCE WITH AS2870 CLASS M - GEOTECH TO CONFIRM.
E. SAFE BEARING CAPACITY HAS BEEN ASSUMED TO BE A MIN. OF 150 kN/m^2/ TO BE BEARING ON STIFF CLAY.
F. GEOTECHNICAL ENGINEER TO VERIFY THE SAFE BEARING CAPACITY OF FOUNDATION MATERIAL PRIOR TO CONSTRUCTION.
G. CONCRETE RAFT (f'c)=32 MPa. FOR SALINITY FOR SOIL OTHERWISE 25MPa WITH A SLUMP OF 80MM.
H. ALL CORNERS TO HAVE L-BAR WITH 500mm LEGS TOP AND BOTTOM
I. ALL SLABS TO BE REINFORCED SL82 TOP MESH.
J. AGGREGATE MINIMUM SIZE 20MM.
K. ALL BRICKS WALLS TO BE ARTICULATED, EXPANSION JOINT SPACING TO BE 6000mm
L. ALL CORNERS TO HAVE L-BAR WITH 500mm LEGS TOP AND BOTTOM.
M. ALL EXPOSED SLABS TO BE WATERPROOFED WITH APPROVED SYSTEMS.
N. ALL WATERPROOFING TO BE CARRIED OUT IN ACCORDANCE WITH BCA REQUIREMENTS .
O. FOLLOW PIERS ARRANGEMENT AS SHOWN IN THE PLAN WHEN 150KPA NOT ACHIEVABLE OR ROCK IS ENCOUNTERED IN PART OF THE FOUNDATION THEN ALL PIERS MUST BE FOUNDED ON ROCK

DRIVEWAY SLAB ON GROUND (S1):
A. 140 THICK SLAB, SL82 FABRIC TOP.
B. POUR DRIVEWAY SLABS ON 100 COMPACTED CRUSHED ROCK.
C. ALL CONCRETE TO BE PLACED BY PUMPING AND COMPACTED WITH A VIBRATOR.
D. MAX 6m SAWN CONTROL JOINT.
E. MAX 15m KEYED CONSTRUCTION JOINT.
F. MAX 30m EXPANSION JOINT.

SOIL SALINITY
A. A LAYER OF SAND MINIMUM 50MM THICK MUST BE LAID BEFORE POURING SLAB.
B. A DAMP-PROOF MEMBRANE (RATHER THAN A VAPOR PROOF MEMBRANE) MUST BE LAID UNDER THE SLAB (BCA 3.2.2.6).
C. THE DAMP PROOF MEMBRANE MUST BE EXTENDED TO THE OUTSIDE FACE OF THE EXTERNAL EDGE BEAM UP TO THE FINISHED GROUND LEVEL.
D. CLASS 32 MPA CONCRETE MUST BE USED OR A SULPHATE RESISTING TYPE SR CEMENT WITH A WATER CEMENT RATIO OF 0.5 MUST BE USED, FOR BOTH CONCRETE SLAB AND PIERS.
E. SLABS MUST BE VIBRATED AND CURED FOR A MINIMUM OF SEVEN DAYS.
F. MINIMUM COVER TO REINFORCEMENT MUST BE 45MM FROM MEMBRANE IN CONTACT WITH GROUND.
G. ADMIXTURES FOR WATER PROOFING AND CORROSION PREVENTION MAY BE USED.

MODULAR ENGINEERS P/L
Structural Engineering | Civil Engineering
Stormwater Engineering | Flood Engineering
Traffic Engineering | Temporary works
ABN : 66 646 960 929
TEL. : 02 873 08473
MOB. : 04 208 98999
EMAIL :
WEBSITE :
ADDRESS :

CLIENT:

PROJECT TITLE:
MULTI DWELLING

SHEET NAME:
GROUND FLOOR FOOTING & SLAB PLAN

PROJECT NUMBER:
175-2026

INTERNAL REVISIONS:

ISSUE	DATE	DESCRIPTION	BY
E	10-09-26	ISSUED FOR CONSTRUCTION	D.A.
D	08-09-26	ISSUED FOR CONSTRUCTION	D.A.
C	24-08-26	ISSUED FOR PRELIMINARY	D.A.
B	21-08-26	ISSUED FOR PRELIMINARY	D.A.

AMENDMENTS

DRAWN : L.M. DATE: 17-07-26
DESIGNED : A.O. REVISION DATE:
QA CHECK : A.O. 10-09-26
APPROVED BY:

RPEQ: 28316
NPER: 5358554
DATE: 10-09-26

ISSUE TYPE:
CONSTRUCTION

SHEET NUMBER:
STR200

SHEET SIZE: **A3** REVISION: **E**

PRINT IN COLOUR

SAMPLE PROJECT A - STRUCTURAL REVIEW - CURRENT - RECRUITMENT ASSESSMENT ONLY
NOT FOR CONSTRUCTION
NOTE: THE DESIGN AND DETAILS SHOWN ON THESE DRAWINGS ARE APPLICABLE TO THIS PROJECT ONLY AND MAY NOT BE REPRODUCED IN WHOLE OR IN PART OR BE USED FOR ANY OTHER PROJECT OR PURPOSE WITHOUT THE WRITTEN PERMISSION OF WITH WHOM COPYRIGHT RESIDES.

REGULATED DESIGN RECORD

PROJECT ADDRESS:	
PROJECT TITLE:	MULTI DWELLING
CONSENT NO:	STR208 - 2023
BODY CORPORATE REG NO:	DEP0001320
DRAWING TITLE:	GROUND FLOOR COLUMN AND WALL LAYOUT PLAN
DRAWING NO:	STR202

REV	DATE DD.MM.YY	DESCRIPTION	DP FULL NAME	REG NO
D	10-09-26	ISSUED FOR CONSTRUCTIO		

CONCRETE COLUMN SCHEDULE

MARK	SIZE	REINFORCEMENT	f'c
C1	300 x 1000	14N20 VERTICAL 3N12-200 TIES	32MPa
C2	300 x 1000	16N20 VERTICAL 3N12-200 TIES	32MPa


LEGEND:

- DENOTES CONCRETE COLUMN/ WALL **OVER ONLY**
- DENOTES BRICK WALLS **OVER ONLY**
- DENOTES BLOCK WORK WALLS **OVER ONLY**
- DENOTES RITEK WALLS **OVER ONLY**
- DENOTES CONCRETE WALL/COLUMN **UNDER ONLY**
- DENOTES WET AREA WITH 2mm FALL
- DENOTES SLAB PENETRATION
- DENOTES STEP ON SLAB
- C00 DENOTES COLUMN MARK
- W00 DENOTES WALL MARK
- 000 DENOTES SLAB THICKNESS
- DENOTES EXTENT OF SLAB STEP

FOR STRUCTURAL NOTES REFER TO DRAWING STR00 SERIES

WALL SCHEDULE

FLOOR LEVEL	TYPE	DESCRIPTION	THK (mm)	VERT. REINF.	HORZ. REINF.	f'c
GROUND	GW1	RITEK WALL	200	N12-200 E.F.	N12-200 E.F.	32 MPa
	GW2	RITEK WALL	200	N12-200 E.F.	N12-200 E.F.	32 MPa

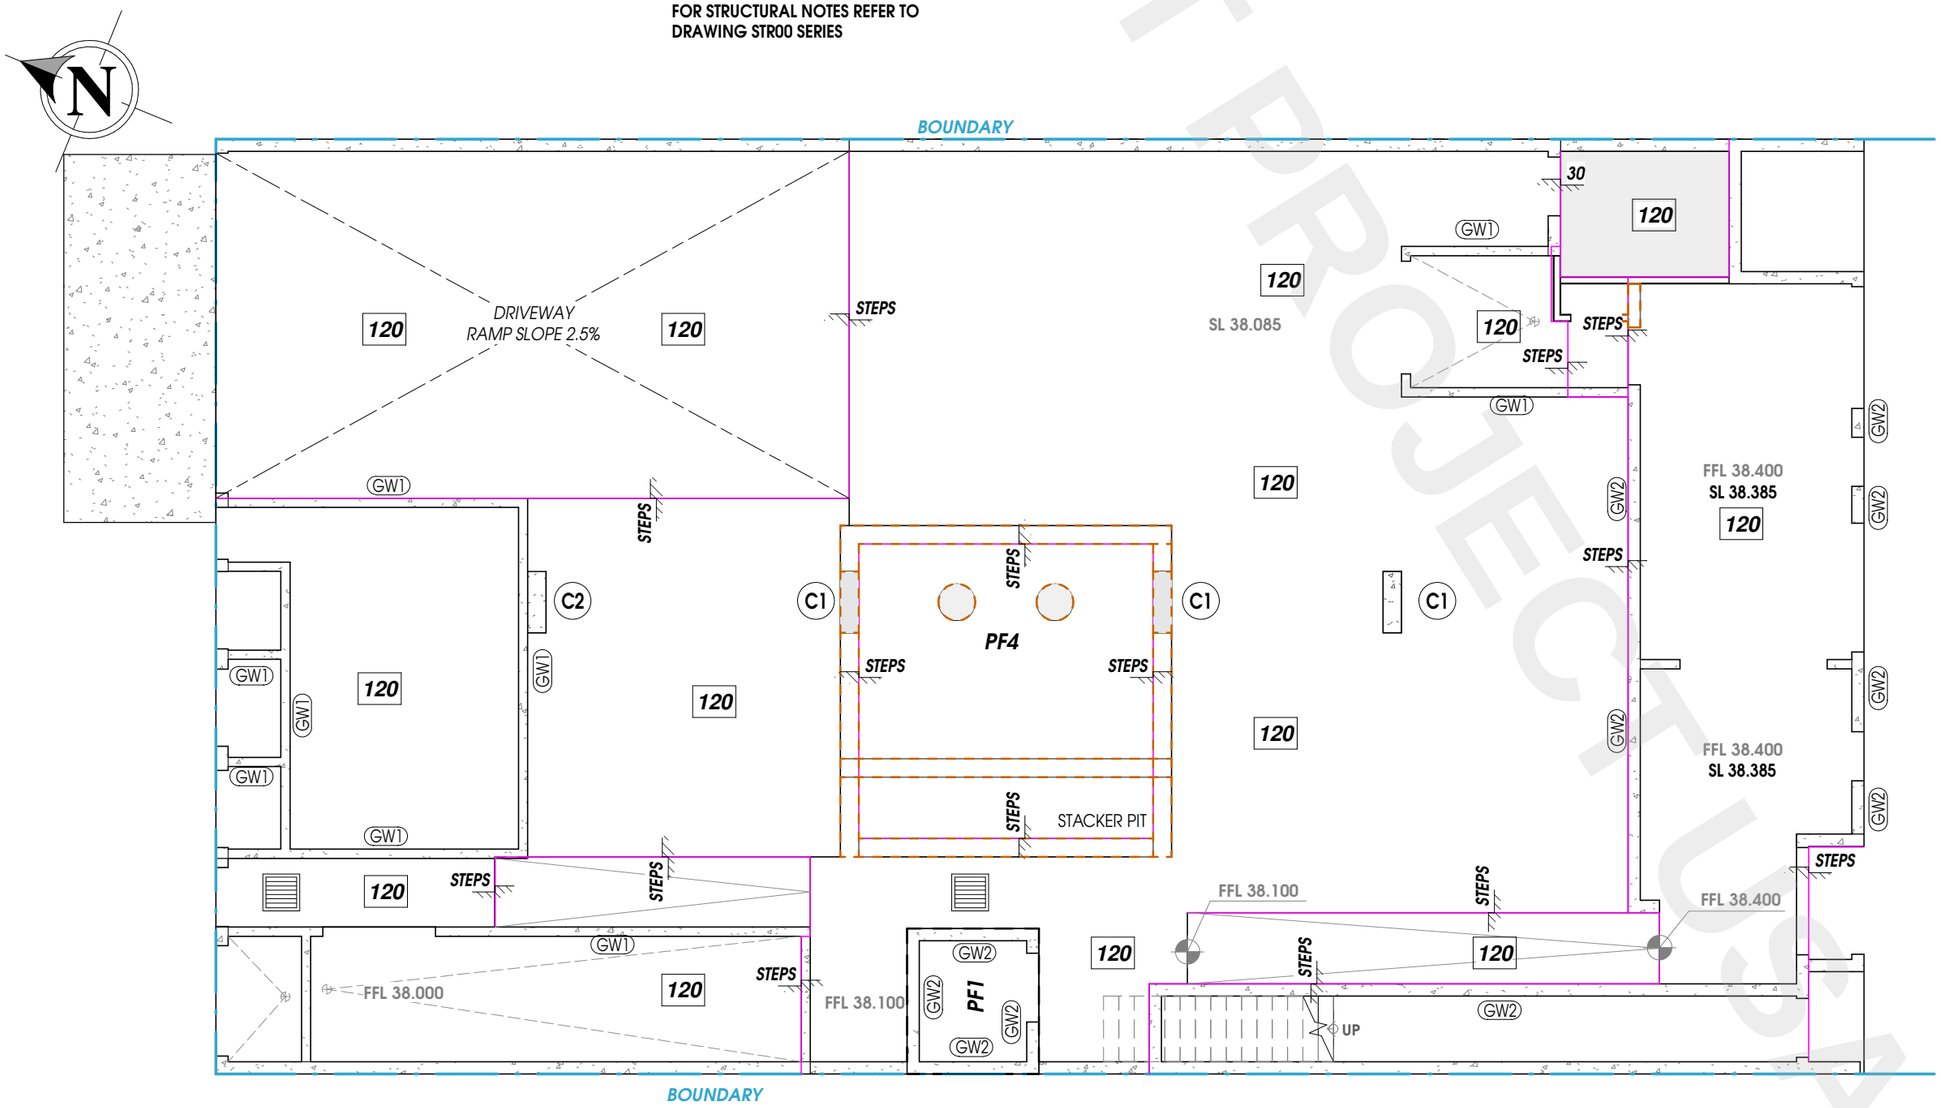

GROUND FLOOR COLUMN AND WALL LAYOUT PLAN

SCALE: 1 : 100

PRINT IN COLOUR

MODULAR ENGINEERS P/L

Structural Engineering | Civil Engineering
Stormwater Engineering | Flood Engineering
Traffic Engineering | Temporary works

ABN : 66 646 960 929
TEL. : 02 873 08473
MOB. : 04 208 98999
EMAIL :
WEBSITE :
ADDRESS :

CLIENT:

PROJECT TITLE:
MULTI DWELLING

SHEET NAME:
GROUND FLOOR COLUMN AND WALL LAYOUT PLAN

PROJECT NUMBER:
175-2026

INTERNAL REVISIONS:

ISSUE	DATE	DESCRIPTION	BY
D	10-09-26	ISSUED FOR CONSTRUCTION	D.A.
C	08-09-26	ISSUED FOR CONSTRUCTION	D.A.
B	21-08-26	ISSUED FOR PRELIMINARY	D.A.
A	30-07-26	ISSUED FOR PRELIMINARY	L.M.

AMENDMENTS

DRAWN : L.M. DATE: 17-07-26
DESIGNED : A.O. REVISION DATE:
QA CHECK : A.O. 10-09-26

APPROVED BY:

RPEQ: 28316
NPER: 5358554
DATE: 10-09-26

ISSUE TYPE:
CONSTRUCTION

SHEET NUMBER:
STR202

SHEET SIZE: **A3**
REVISION: **D**

SAMPLE PROJECT A - STRUCTURAL REV E - CURRENT - RECRUITMENT ASSESSMENT ONLY

TEST PROJECT USAGE

NOTE: THE DESIGN AND DETAILS SHOWN ON THESE DRAWINGS ARE APPLICABLE TO THIS PROJECT ONLY AND MAY NOT BE REPRODUCED IN WHOLE OR IN PART OR BE USED FOR ANY OTHER PROJECT OR PURPOSE WITHOUT THE WRITTEN PERMISSION OF WITH WHOM COPYRIGHT RESIDES.

REGULATED DESIGN RECORD

PROJECT ADDRESS:	
PROJECT TITLE:	MULTI DWELLING
CONSENT NO:	STR208 - 2023
BODY CORPORATE REG NO:	DEP0001320
DRAWING TITLE:	GROUND FLOOR LOADING PLAN
DRAWING NO:	STR210

REV	DATE DD.MM.YY	DESCRIPTION	DP FULL NAME	REG NO
E	10-09-26	ISSUED FOR CONSTRUCTIO		

DEFLECTION NOTES (LONG-TERM)


- LONG-TERM DEFLECTION IS BASED ON DL + 0.3LL FOR SUSTAINED LOADS.
- CREEP FACTOR Λ = 2.0 TO 3.0 APPLIED PER AS3600.
- TOTAL DEFLECTION:
  Δ TOTAL=Δ IMMEDIATE + Λ × Δ SUSTAINED
- IMMEDIATE DEFLECTION: DL + LL
- LONG-TERM DEFLECTION: DL + 0.3LL × Λ

LOADING TABLE
WHERE APPLICABLE

MARK	COLOUR	AREA	SUPERIMPOSED DEAD LOAD	LIVE LOAD
1		RESIDENTIAL	1.5 kPa	1.5 kPa
2		PARKING	0.5 kPa EXC. FALLS AND GRADING	2.5 kPa
3		STORAGE	0.5 kPa	5.0 kPa
4		CORRIDOR / STAIR	1.5 kPa	4.0 kPa
5		LOBBY	1.5 kPa	4.0 kPa
6		BALCONY	1.5 kPa	2.0 kPa
7		MECH ROOM,FAN ROOM	1.5 kPa	5.0 kPa
8		COMMON AREA	1.5 kPa	4.0 kPa
9		LIGHT WEIGHT ROOF	0.5 kPa	0.5 kPa

LOADING TABLE
WHERE APPLICABLE

MARK	COLOUR	AREA	SUPERIMPOSED DEAD LOAD	LIVE LOAD
10		WASTE ROOM	0.5 kPa	5.0 kPa
11		RETAILS	1.5 kPa	4.0 kPa
12		ROOF (NON-TRAFFICABLE)	2.0 kPa	1.5 kPa
13		LANDSCAPE 400mm SOIL MAX.	4.0 kPa	1.5 kPa
14		LANDSCAPE 1000mm SOIL MAX.	10.0 kPa	1.5 kPa
15		SUBSTATION	1.0 kPa	2.0 kPa
16		LOADING DECK	1.0 kPa	10.0 kPa
17		PEBBLES	4.0 kPa	1.5 kPa
18		OSD TANK/ WATER STORAGE TANK	10.0 kPa FOR EVERY METRE HEIGHT OF WATER	

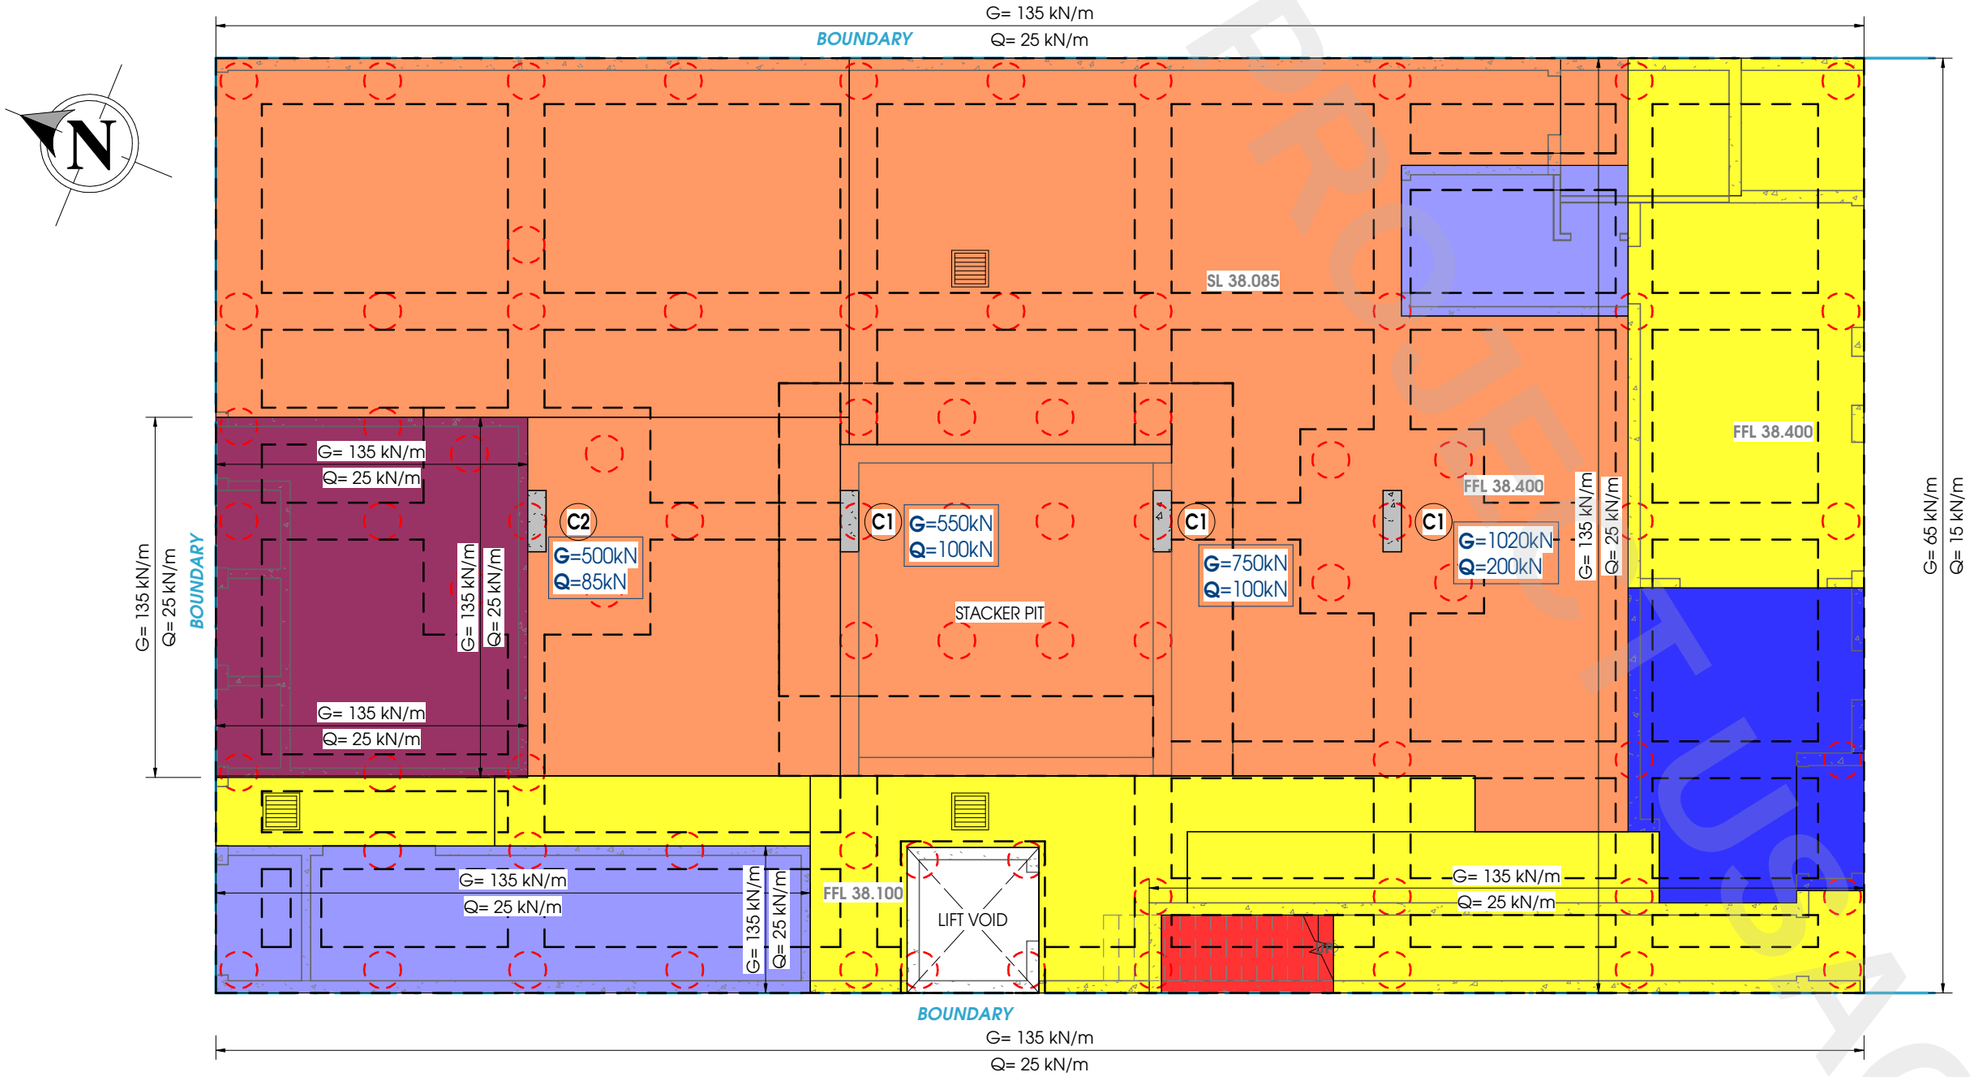

GROUND FLOOR LOADING PLAN

SCALE: 1 : 100

TEST PROJECT

MODULAR ENGINEERS P/L

Structural Engineering | Civil Engineering
Stormwater Engineering | Flood Engineering
Traffic Engineering | Temporary works

ABN : 66 646 960 929
TEL. : 02 873 08473
MOB. : 04 208 98999
EMAIL :
WEBSITE :
ADDRESS :

CLIENT:

PROJECT TITLE:
MULTI DWELLING

SHEET NAME:
GROUND FLOOR LOADING PLAN

PROJECT NUMBER:
175-2026

INTERNAL REVISIONS:

ISSUE	DATE	DESCRIPTION	BY
E	10-09-26	ISSUED FOR CONSTRUCTION	D.A.
D	08-09-26	ISSUED FOR CONSTRUCTION	D.A.
C	24-08-26	ISSUED FOR PRELIMINARY	D.A.
B	21-08-26	ISSUED FOR PRELIMINARY	D.A.

AMENDMENTS

DRAWN : L.M. DATE: 17-07-26
DESIGNED : A.O. REVISION DATE:
QA CHECK : A.O. 10-09-26

APPROVED BY:

RPEQ: 28316
NPER: 5358554
DATE: 10-09-26

ISSUE TYPE:
CONSTRUCTION

SHEET NUMBER:
STR210

SHEET SIZE: **A3**
REVISION: **E**

PRINT IN COLOUR

SAMPLE PROJECT A - STRUCTURAL REV E - CURRENT - RECRUITMENT ASSESSMENT ONLY

NOTE: THE DESIGN AND DETAILS SHOWN ON THESE DRAWINGS ARE APPLICABLE TO THIS PROJECT ONLY AND MAY NOT BE REPRODUCED IN WHOLE OR IN PART OR BE USED FOR ANY OTHER PROJECT OR PURPOSE WITHOUT THE WRITTEN PERMISSION OF WITH WHOM COPYRIGHT RESIDES.


REGULATED DESIGN RECORD

PROJECT ADDRESS:			
PROJECT TITLE:	MULTI DWELLING		
CONSENT NO:	STR208 - 2023	BODY CORPORATE REG NO:	DEP0001320
DRAWING TITLE:	SECTION AND DETAILS	DRAWING NO:	STR220


REV	DATE DD.MM.YY	DESCRIPTION	DP FULL NAME	REG NO
E	10-09-26	ISSUED FOR CONSTRUCTIO		

FOOTING SCHEDULE

MARK	SIZE	REINFORCEMENT	REMARKS
PF1	2370 x 2150 x 300D	N12-200 TOP & BOT. B.W.	
PF2	3000 x 3000 x 700D	N16-150 U-BARS, 600 COG, EACH WAY	
PF3	3700 x 3700 x 800D	N16-150 U-BARS, 700 COG, EACH WAY	
PF4	6400 x 7400 x 300D	N16-200 TOP & BOT. B.W.	

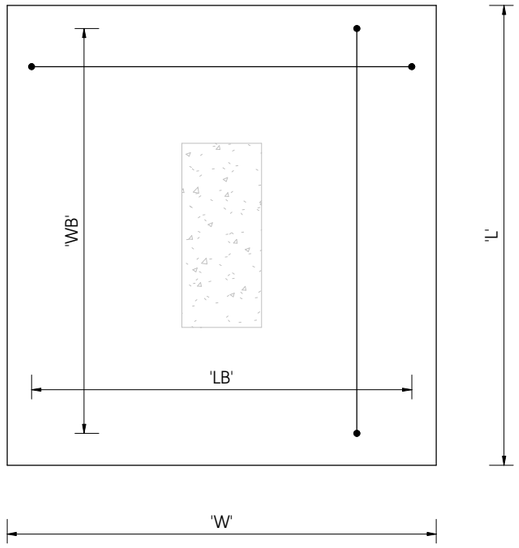

TYPICAL PAD FOOTING PLAN

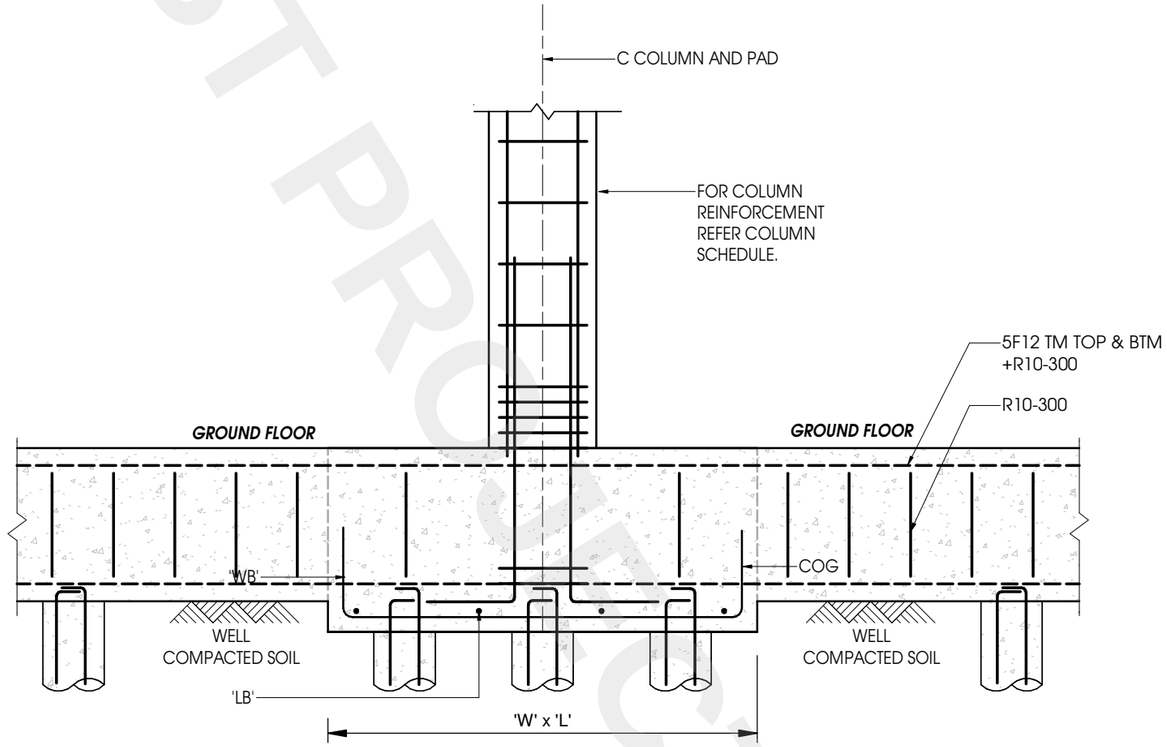

PAD FOOTING 'PF2 & PF3' TYPICAL DETAILS

TEST PROJECT USAGE

PRINT IN COLOUR

MODULAR ENGINEERS P/L
Structural Engineering | Civil Engineering
Stormwater Engineering | Flood Engineering
Traffic Engineering | Temporary works
ABN : 66 646 960 929
TEL. : 02 873 08473
MOB. : 04 208 98999
EMAIL :
WEBSITE :
ADDRESS :

CLIENT:

PROJECT TITLE:
MULTI DWELLING

SHEET NAME:
SECTION AND DETAILS

PROJECT NUMBER:
175-2026

INTERNAL REVISIONS:

ISSUE	DATE	DESCRIPTION	BY
E	10-09-26	ISSUED FOR CONSTRUCTION	D.A.
D	08-09-26	ISSUED FOR CONSTRUCTION	D.A.
C	24-08-26	ISSUED FOR PRELIMINARY	D.A.
B	21-08-26	ISSUED FOR PRELIMINARY	D.A.

AMENDMENTS

DRAWN : L.M. DATE: 17-07-26
DESIGNED : A.O. REVISION DATE:
QA CHECK : A.O. 10-09-26

APPROVED BY:

RPEQ: 28316
NPER: 5358554
DATE: 10-09-26

ISSUE TYPE:
CONSTRUCTION

SHEET NUMBER:
STR220

SHEET SIZE: **A3**
REVISION: **E**


SAMPLE PROJECT A - STRUCTURAL REV E - CURRENT - RECRUITMENT ASSESSMENT ONLY

NOTE: THE DESIGN AND DETAILS SHOWN ON THESE DRAWINGS ARE APPLICABLE TO THIS PROJECT ONLY AND MAY NOT BE REPRODUCED IN WHOLE OR IN PART OR BE USED FOR ANY OTHER PROJECT OR PURPOSE WITHOUT THE WRITTEN PERMISSION OF WITH WHOM COPYRIGHT RESIDES.

REGULATED DESIGN RECORD


PROJECT ADDRESS:			
PROJECT TITLE:	MULTI DWELLING		
CONSENT NO:	STR208 - 2023	BODY CORPORATE REG NO:	DEP0001320
DRAWING TITLE:	SECTION AND DETAILS	DRAWING NO:	STR230

REV	DATE DD.MM.YY	DESCRIPTION	DP FULL NAME	REG NO
E	10-09-26	ISSUED FOR CONSTRUCTIO		

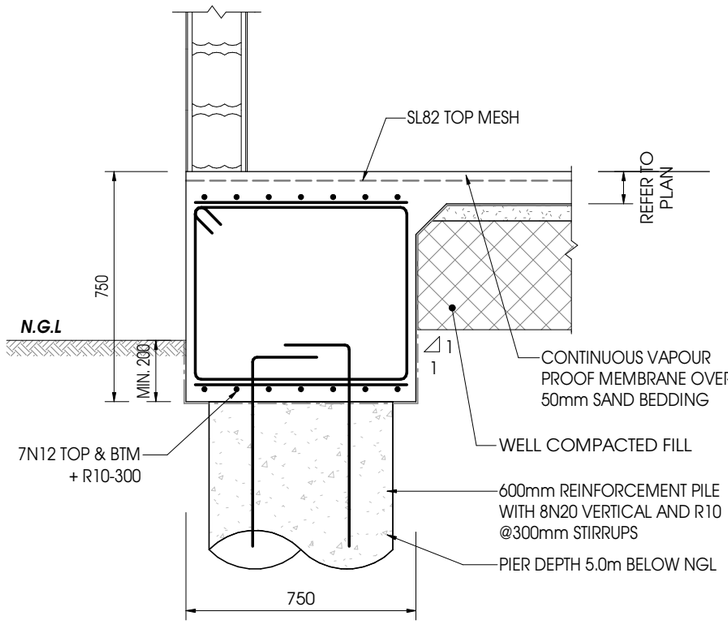


EXTERNAL FOOTING BEAM (EB1)

SCALE 1:20

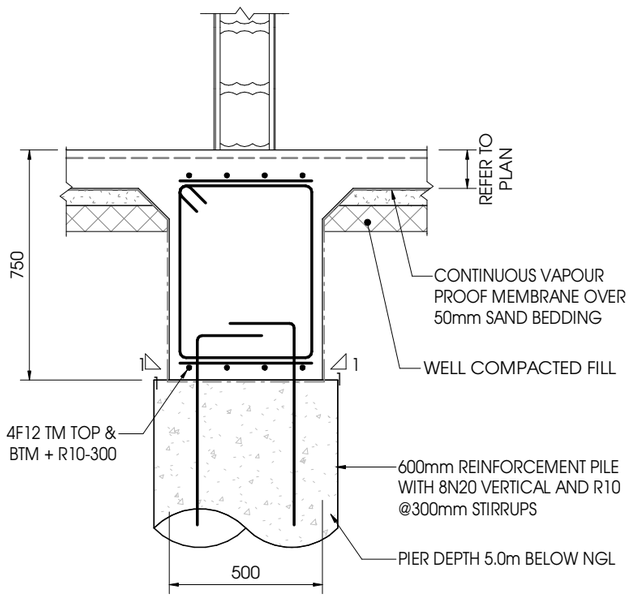


OR

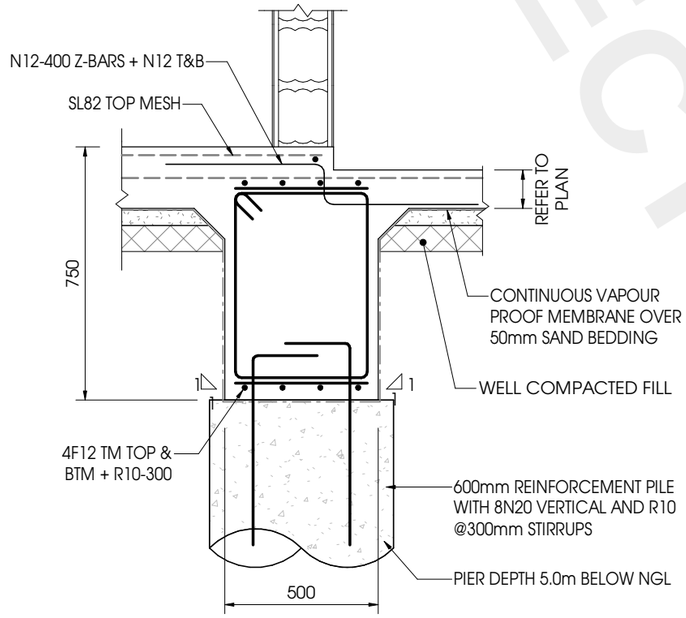


INTERNAL FOOTING BEAM (IB2)

SCALE 1:20

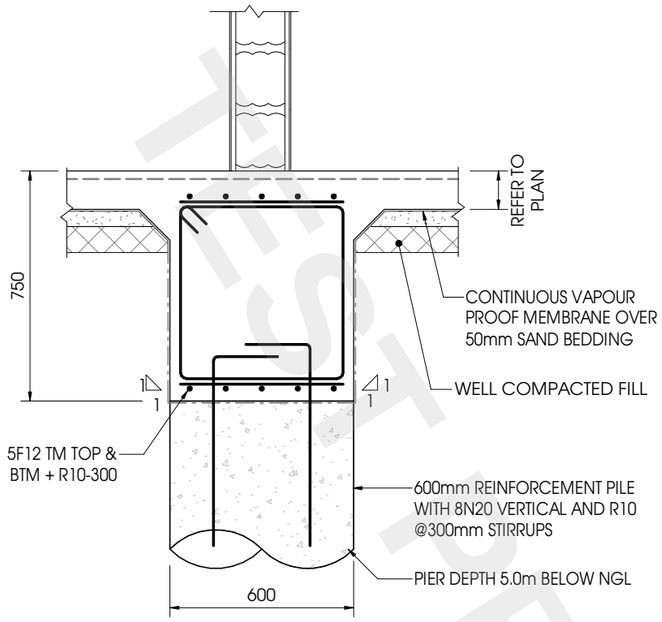



OR

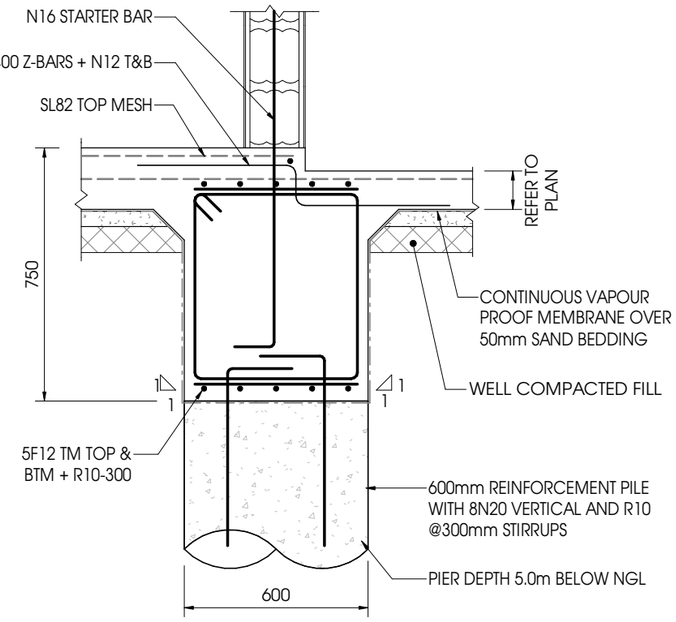

INTERNAL FOOTING BEAM (IB1)

SCALE 1:20

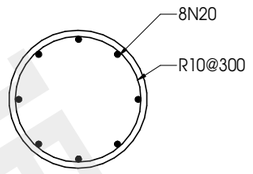

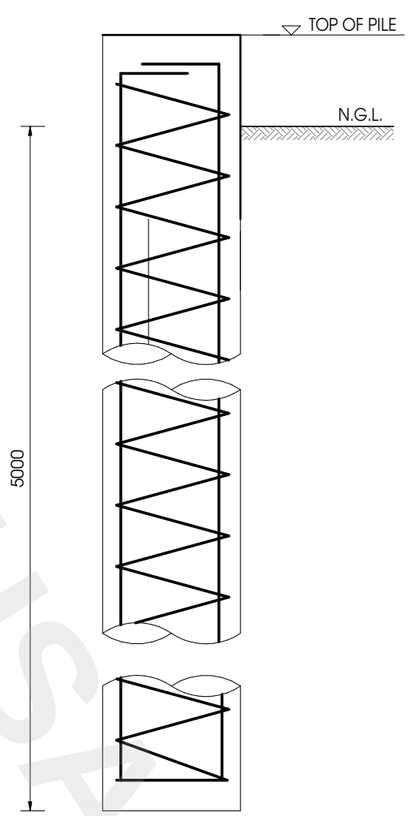

BORED PIER DETAIL

PRINT IN COLOUR

TEST PROJECT USE ONLY

MODULAR ENGINEERS P/L
Structural Engineering | Civil Engineering
Stormwater Engineering | Flood Engineering
Traffic Engineering | Temporary works
ABN : 66 646 960 929
TEL. : 02 873 08473
MOB. : 04 208 98999
EMAIL :
WEBSITE :
ADDRESS :

CLIENT:

PROJECT TITLE:
MULTI DWELLING

SHEET NAME:
SECTION AND DETAILS

PROJECT NUMBER:
175-2026

INTERNAL REVISIONS:

ISSUE	DATE	DESCRIPTION	BY
E	10-09-26	ISSUED FOR CONSTRUCTION	D.A.
D	08-09-26	ISSUED FOR CONSTRUCTION	D.A.
C	24-08-26	ISSUED FOR PRELIMINARY	D.A.
B	21-08-26	ISSUED FOR PRELIMINARY	D.A.

AMENDMENTS

DRAWN : L.M. DATE: 17-07-26
DESIGNED : A.O. REVISION DATE:
QA CHECK : A.O. 10-09-26

APPROVED BY:

RPEQ: 28316
NPER: 5358554
DATE: 10-09-26

ISSUE TYPE:
CONSTRUCTION

SHEET NUMBER:
STR230

SHEET SIZE: **A3**
REVISION: **E**

SAMPLE PROJECT A - STRUCTURAL REV E - CURRENT - RECRUITMENT ASSESSMENT ONLY

NOTE: THE DESIGN AND DETAILS SHOWN ON THESE DRAWINGS ARE APPLICABLE TO THIS PROJECT ONLY AND MAY NOT BE REPRODUCED IN WHOLE OR IN PART OR BE USED FOR ANY OTHER PROJECT OR PURPOSE WITHOUT THE WRITTEN PERMISSION OF WITH WHOM COPYRIGHT RESIDES.

REGULATED DESIGN RECORD


PROJECT ADDRESS:	
PROJECT TITLE:	MULTI DWELLING
CONSENT NO:	STR208 - 2023
BODY CORPORATE REG NO:	DEP0001320
DRAWING TITLE:	SECTION AND DETAILS
DRAWING NO:	STR240

REV	DATE DD.MM.YY	DESCRIPTION	DP FULL NAME	REG NO
E	10-09-26	ISSUED FOR CONSTRUCTIO		

GROUND FLOOR	SIZE VERT. REINF. TIES & TYPE	300 x 1000 14N20 3N12-200	300 x 1000 16N20 N12-200
	DETAIL NUMBER	1	1
STARTER BARS			
COLUMN MARK		**C1**	**C2**


CONCRETE COLUMN SCHEDULE

MARK	SIZE	REINFORCEMENT	f'c
C1	300 x 1000	14N20 VERTICAL 3N12-200 TIES	32MPa
C2	300 x 1000	16N20 VERTICAL 3N12-200 TIES	32MPa

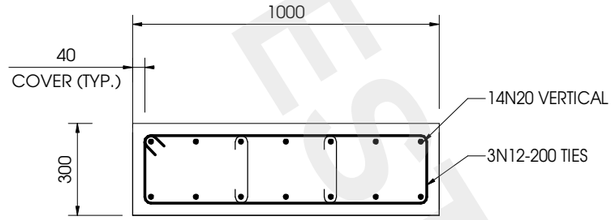

COLUMN DETAIL (C1)


SCALE 1:20

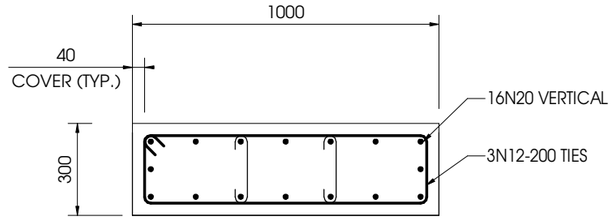

COLUMN DETAIL (C2)

SCALE 1:20


NOTE:
1. STARTER BARS TO BE SAME NUMBER, DIAMETER AND ARRANGEMENT AS COLUMN OVER.
2. REFER TO COLUMN SCHEDULE FOR COLUMN SIZES AND REINFORCEMENT.
3. LIGATURES 50mm BELOW SLABS WHERE THREE OR LESS INTERSECTING BEAMS OR LIGATURES 50mm BELOW THE SHALLOWEST BEAM WHERE FOUR INTERSECTING BEAMS.

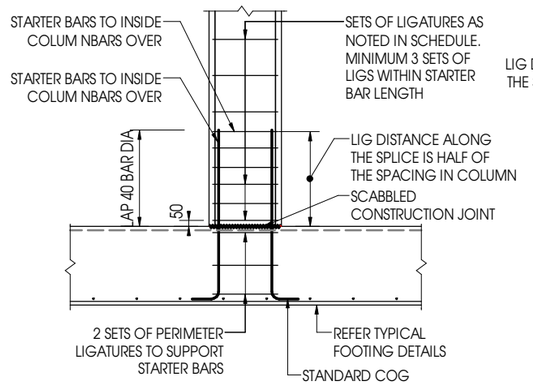


TYPICAL COLUMN DETAIL AT FOOTING

NOT TO SCALE

DETAIL 1 / -

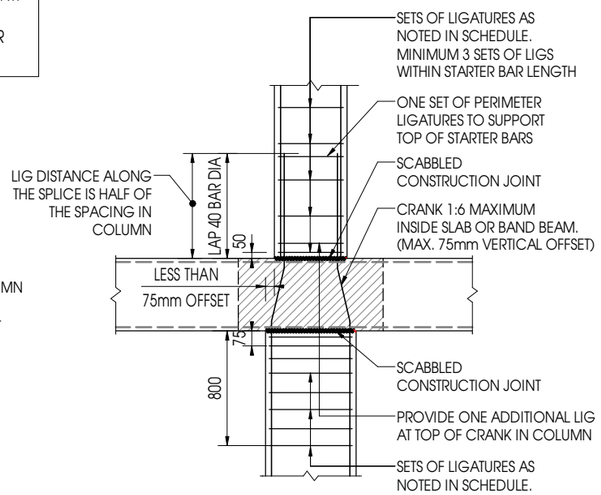

DETAIL 2 / -

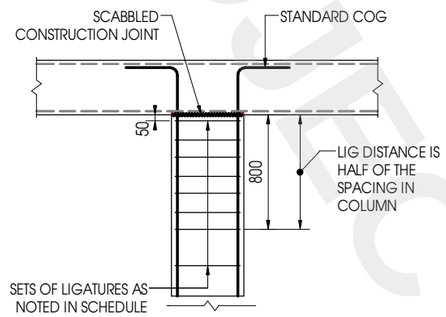


TYPICAL COLUMN TERMINATION DETAIL

NOT TO SCALE

DETAIL 3 / -

NOTE:
1. STARTER BARS TO BE SAME NUMBER, DIAMETER AND ARRANGEMENT AS COLUMN OVER.
2. REFER TO COLUMN SCHEDULE FOR COLUMN SIZES AND REINFORCEMENT.
3. LIGATURES 50mm BELOW SLABS WHERE THREE OR LESS INTERSECTING BEAMS OR LIGATURES 50mm BELOW THE SHALLOWEST BEAM WHERE FOUR INTERSECTING BEAMS.

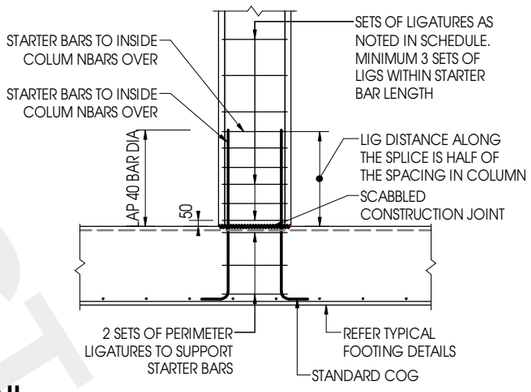

TYPICAL COLUMN DETAIL AT FOOTING

NOT TO SCALE

DETAIL 4 / -

TYPICAL COLUMN AND TIES DETAIL

TEST PROJECT USAGE

PRINT IN COLOUR

MODULAR ENGINEERS P/L
Structural Engineering | Civil Engineering
Stormwater Engineering | Flood Engineering
Traffic Engineering | Temporary works
ABN : 66 646 960 929
TEL. : 02 873 08473
MOB. : 04 208 98999
EMAIL :
WEBSITE :
ADDRESS :

CLIENT:

PROJECT TITLE:
MULTI DWELLING

SHEET NAME:
SECTION AND DETAILS

PROJECT NUMBER:
175-2026

INTERNAL REVISIONS:

ISSUE	DATE	DESCRIPTION	BY
E	10-09-26	ISSUED FOR CONSTRUCTION	D.A.
D	08-09-26	ISSUED FOR CONSTRUCTION	D.A.
C	24-08-26	ISSUED FOR PRELIMINARY	D.A.
B	21-08-26	ISSUED FOR PRELIMINARY	D.A.

AMENDMENTS

DRAWN : L.M. DATE: 17-07-26
DESIGNED : A.O. REVISION DATE:
QA CHECK : A.O. 10-09-26

APPROVED BY:

RPEQ: 28316
NPER: 5358554
DATE: 10-09-26

ISSUE TYPE:
CONSTRUCTION

SHEET NUMBER:
STR240

SHEET SIZE: **A3**
REVISION: **E**


SAMPLE PROJECT A - STRUCTURAL REV E - CURRENT - RECRUITMENT ASSESSMENT ONLY

NOTE: THE DESIGN AND DETAILS SHOWN ON THESE DRAWINGS ARE APPLICABLE TO THIS PROJECT ONLY AND MAY NOT BE REPRODUCED IN WHOLE OR IN PART OR BE USED FOR ANY OTHER PROJECT OR PURPOSE WITHOUT THE WRITTEN PERMISSION OF WITH WHOM COPYRIGHT RESIDES.


REGULATED DESIGN RECORD

PROJECT ADDRESS:			
PROJECT TITLE:	MULTI DWELLING		
CONSENT NO:	STR208 - 2023	BODY CORPORATE REG NO:	DEP0001320
DRAWING TITLE:	SECTION AND DETAILS	DRAWING NO:	STR250


REV	DATE DD.MM.YY	DESCRIPTION	DP FULL NAME	REG NO
E	10-09-26	ISSUED FOR CONSTRUCTIO		

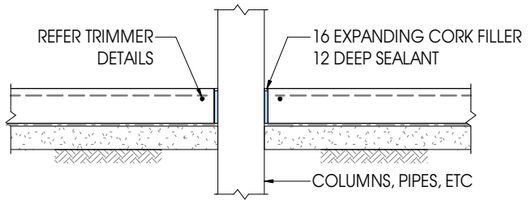


SLAB PENETRATION
SCALE 1:25

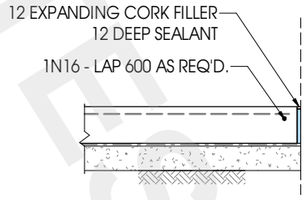


EDGE OF SLAB
SCALE 1:25

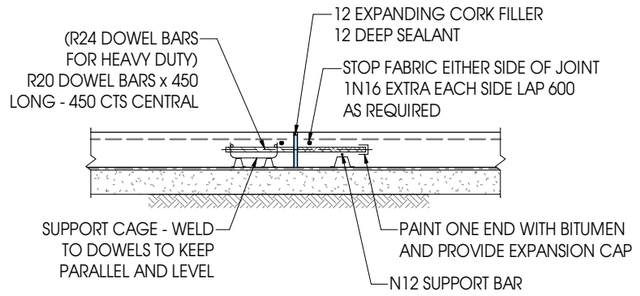


E.J. - EXPANSION JOINT
SCALE 1:25

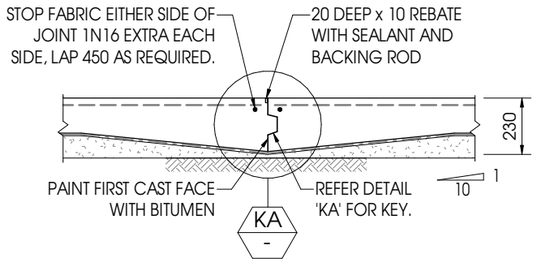


K.J. - KEYED CONSTRUCTION JOINT
SCALE 1:25 CARPARK AND OFFICE FLOORS

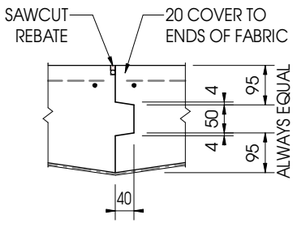


DETAIL KA
NOT TO SCALE

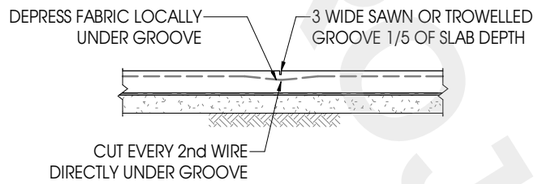


S.J. - SAWN CONTROL JOINT
SCALE 1:25
NOTE: SAWCUT TO BE MADE WITHIN 16 HOURS OF CASTING SLAB

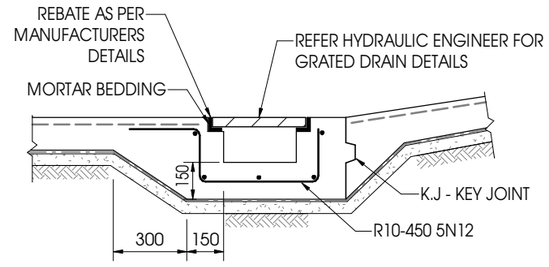


TYPICAL GRATED DRAIN DETAIL
SCALE 1:25

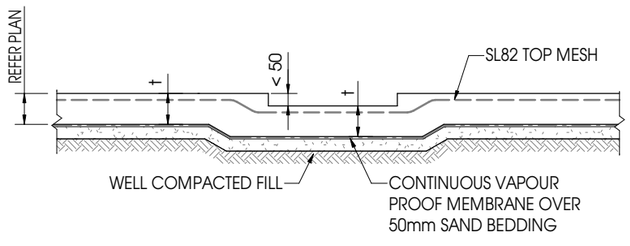

TYPICAL SLAB DETAIL AT A RECESS
SCALE 1:25

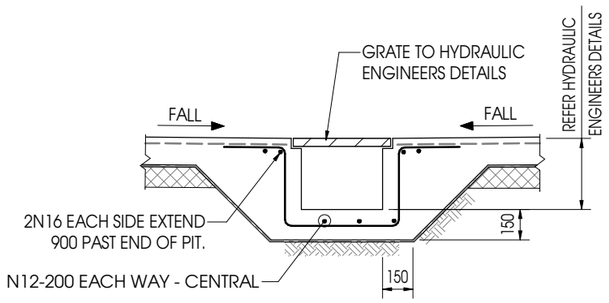

TYPICAL PIT DETAIL FW
SCALE 1:25

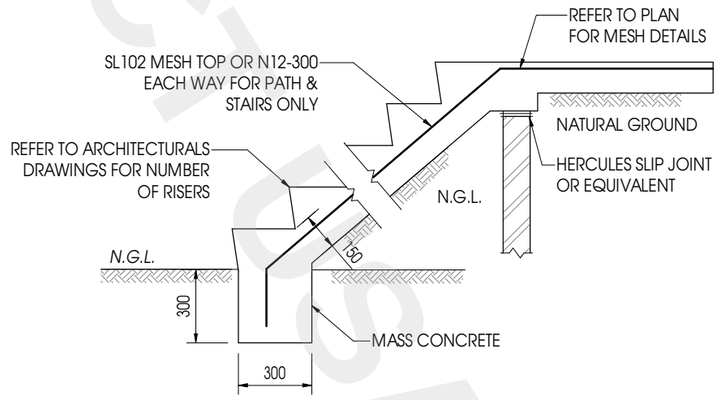

TYPICAL EXTERNAL STAIR DETAILS
SCALE 1:25

PRINT IN COLOUR

NOTE: THE DESIGN AND DETAILS SHOWN ON THESE DRAWINGS ARE APPLICABLE TO THIS PROJECT ONLY AND MAY NOT BE REPRODUCED IN WHOLE OR IN PART OR BE USED FOR ANY OTHER PROJECT OR PURPOSE WITHOUT THE WRITTEN PERMISSION OF WITH WHOM COPYRIGHT RESIDES.

MODULAR ENGINEERS P/L
Structural Engineering | Civil Engineering
Stormwater Engineering | Flood Engineering
Traffic Engineering | Temporary works
ABN : 66 646 960 929
TEL. : 02 873 08473
MOB. : 04 208 98999
EMAIL :
WEBSITE :
ADDRESS :

CLIENT:

PROJECT TITLE:
MULTI DWELLING

SHEET NAME:
SECTION AND DETAILS

PROJECT NUMBER:
175-2026

INTERNAL REVISIONS:

ISSUE	DATE	DESCRIPTION	BY
E	10-09-26	ISSUED FOR CONSTRUCTION	D.A.
D	08-09-26	ISSUED FOR CONSTRUCTION	D.A.
C	24-08-26	ISSUED FOR PRELIMINARY	D.A.
B	21-08-26	ISSUED FOR PRELIMINARY	D.A.

AMENDMENTS

DRAWN : L.M. DATE: 17-07-26
DESIGNED : A.O. REVISION DATE:
QA CHECK : A.O. 10-09-26
APPROVED BY:

RPEQ: 28316
NPER: 5358554
DATE: 10-09-26

ISSUE TYPE:
CONSTRUCTION

SHEET NUMBER:
STR250


SHEET SIZE: **A3** REVISION: **E**

SAMPLE PROJECT A - STRUCTURAL REV E - CURRENT - RECRUITMENT ASSESSMENT ONLY


REGULATED DESIGN RECORD


PROJECT ADDRESS:			
PROJECT TITLE:	MULTI DWELLING		
CONSENT NO:	STR208 - 2023	BODY CORPORATE REG NO:	DEP0001320
DRAWING TITLE:	SECTION AND DETAILS	DRAWING NO:	STR260

REV	DATE DD.MM.YY	DESCRIPTION	DP FULL NAME	REG NO
E	10-09-26	ISSUED FOR CONSTRUCTIO		

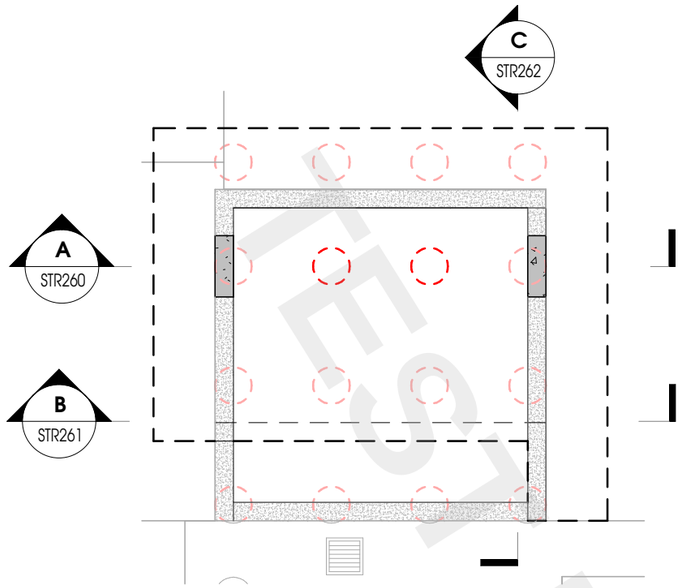

1 STR200 **PF4 LAYOUT PLAN**
NOT TO SCALE

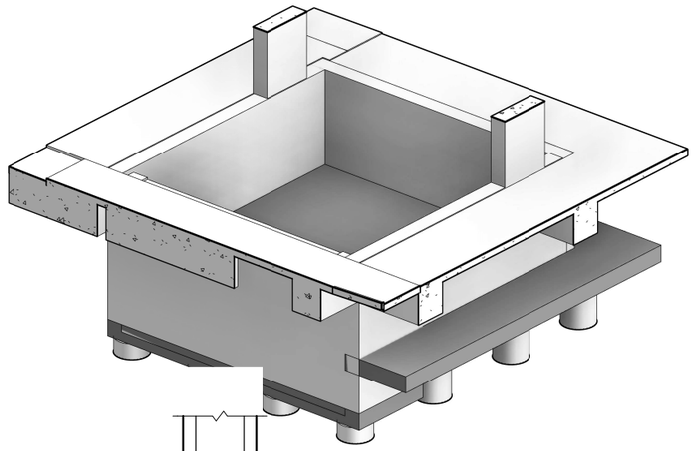

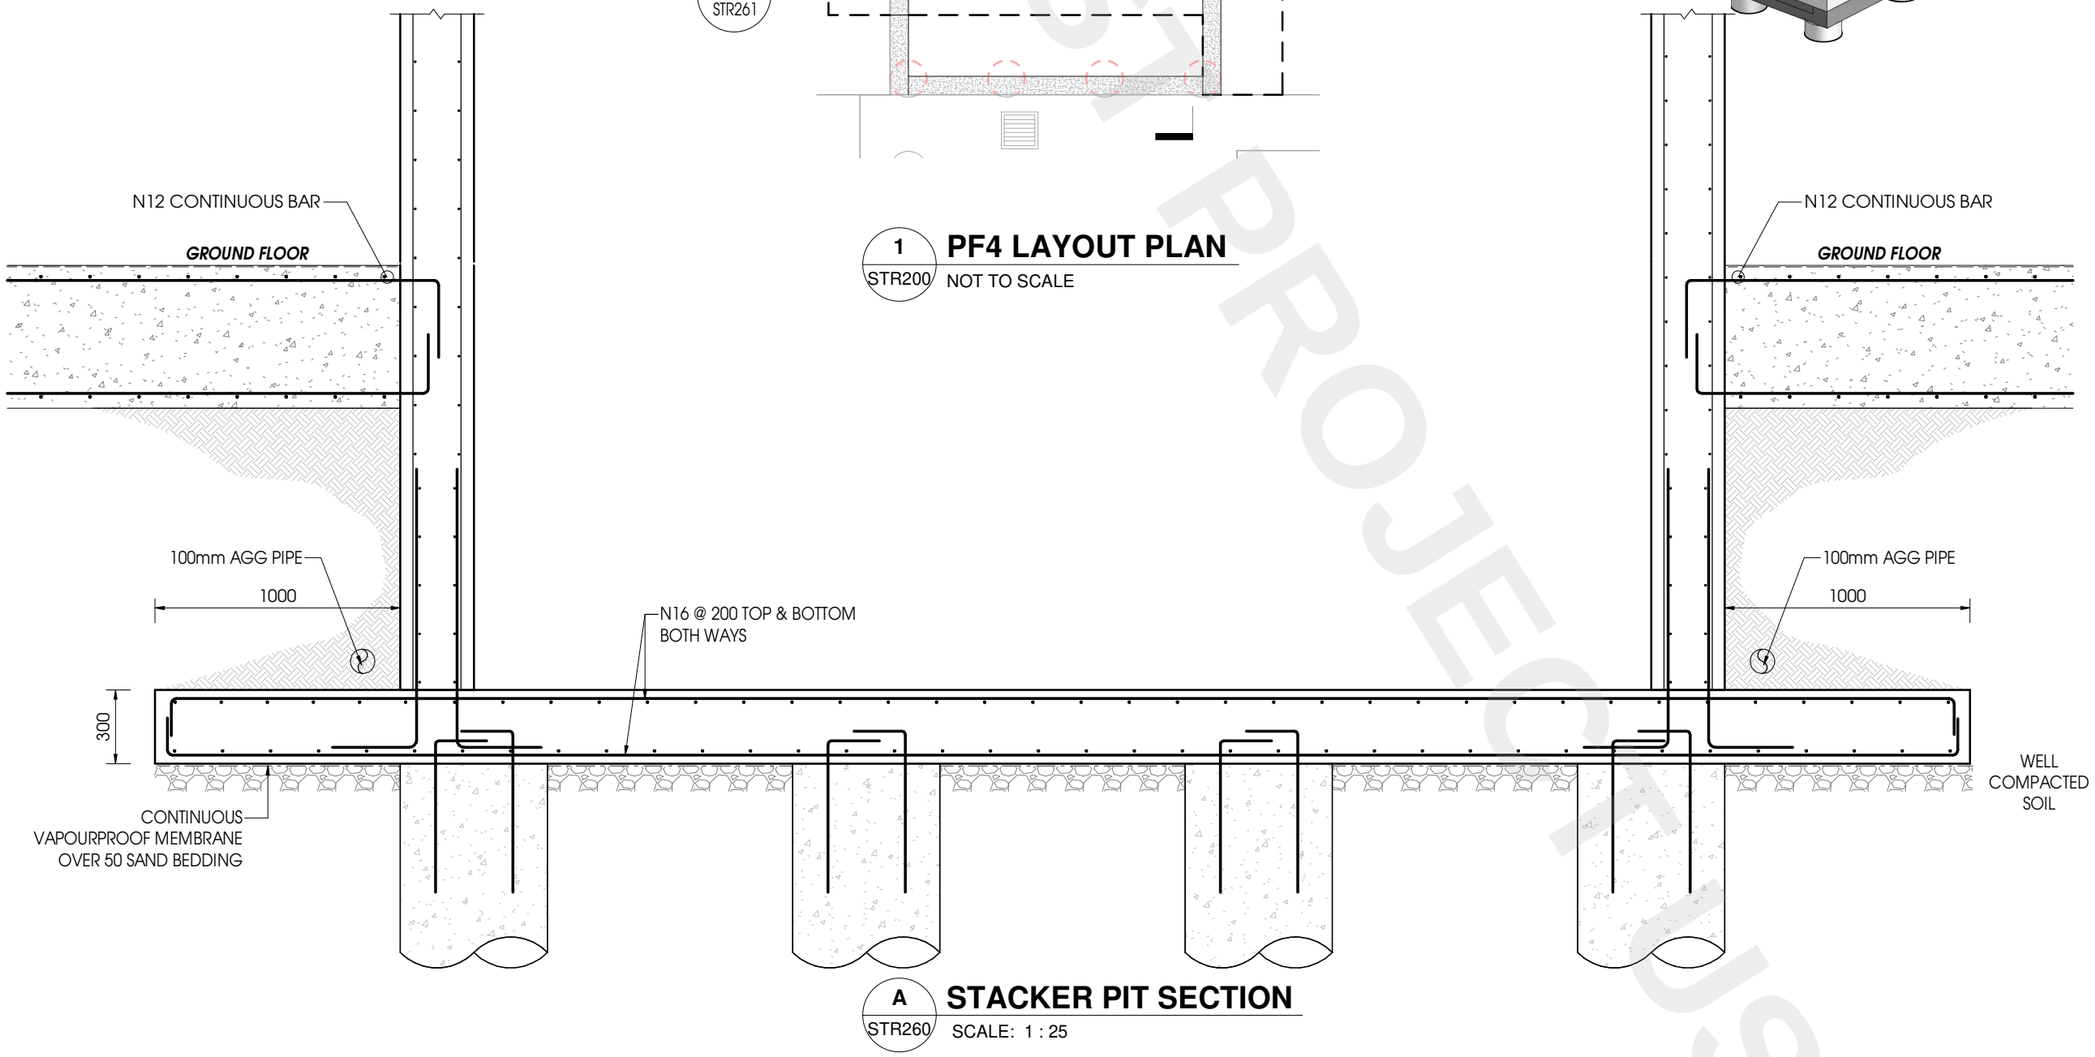

A STR260 **STACKER PIT SECTION**
SCALE: 1 : 25

PRINT IN COLOUR

MODULAR ENGINEERS P/L
Structural Engineering | Civil Engineering
Stormwater Engineering | Flood Engineering
Traffic Engineering | Temporary works

ABN : 66 646 960 929
TEL. : 02 873 08473
MOB. : 04 208 98999
EMAIL :
WEBSITE :
ADDRESS :

CLIENT:

PROJECT TITLE:
MULTI DWELLING

SHEET NAME:
SECTION AND DETAILS

PROJECT NUMBER:
175-2026

INTERNAL REVISIONS:

ISSUE	DATE	DESCRIPTION	BY
E	10-09-26	ISSUED FOR CONSTRUCTION	D.A.
D	08-09-26	ISSUED FOR CONSTRUCTION	D.A.
C	24-08-26	ISSUED FOR PRELIMINARY	D.A.
B	21-08-26	ISSUED FOR PRELIMINARY	D.A.

AMENDMENTS

DRAWN : L.M. DATE: 17-07-26
DESIGNED : A.O. REVISION DATE:
QA CHECK : A.O. 10-09-26
APPROVED BY:

RPEQ: 28316
NPER: 5358554
DATE: 10-09-26

ISSUE TYPE:
CONSTRUCTION

SHEET NUMBER:
STR260

SHEET SIZE: **A3** REVISION: **E**

SAMPLE PROJECT A - STRUCTURAL REV E - CURRENT - RECRUITMENT ASSESSMENT ONLY


TEST PROJECT USAGE ONLY

NOTE: THE DESIGN AND DETAILS SHOWN ON THESE DRAWINGS ARE APPLICABLE TO THIS PROJECT ONLY AND MAY NOT BE REPRODUCED IN WHOLE OR IN PART OR BE USED FOR ANY OTHER PROJECT OR PURPOSE WITHOUT THE WRITTEN PERMISSION OF WITH WHOM COPYRIGHT RESIDES.

REGULATED DESIGN RECORD

PROJECT ADDRESS:	
PROJECT TITLE:	MULTI DWELLING
CONSENT NO:	STR208 - 2023
BODY CORPORATE REG NO:	DEP0001320
DRAWING TITLE:	SECTION AND DETAILS
DRAWING NO:	STR261

REV	DATE DD.MM.YY	DESCRIPTION	DP FULL NAME	REG NO
E	10-09-26	ISSUED FOR CONSTRUCTIO		

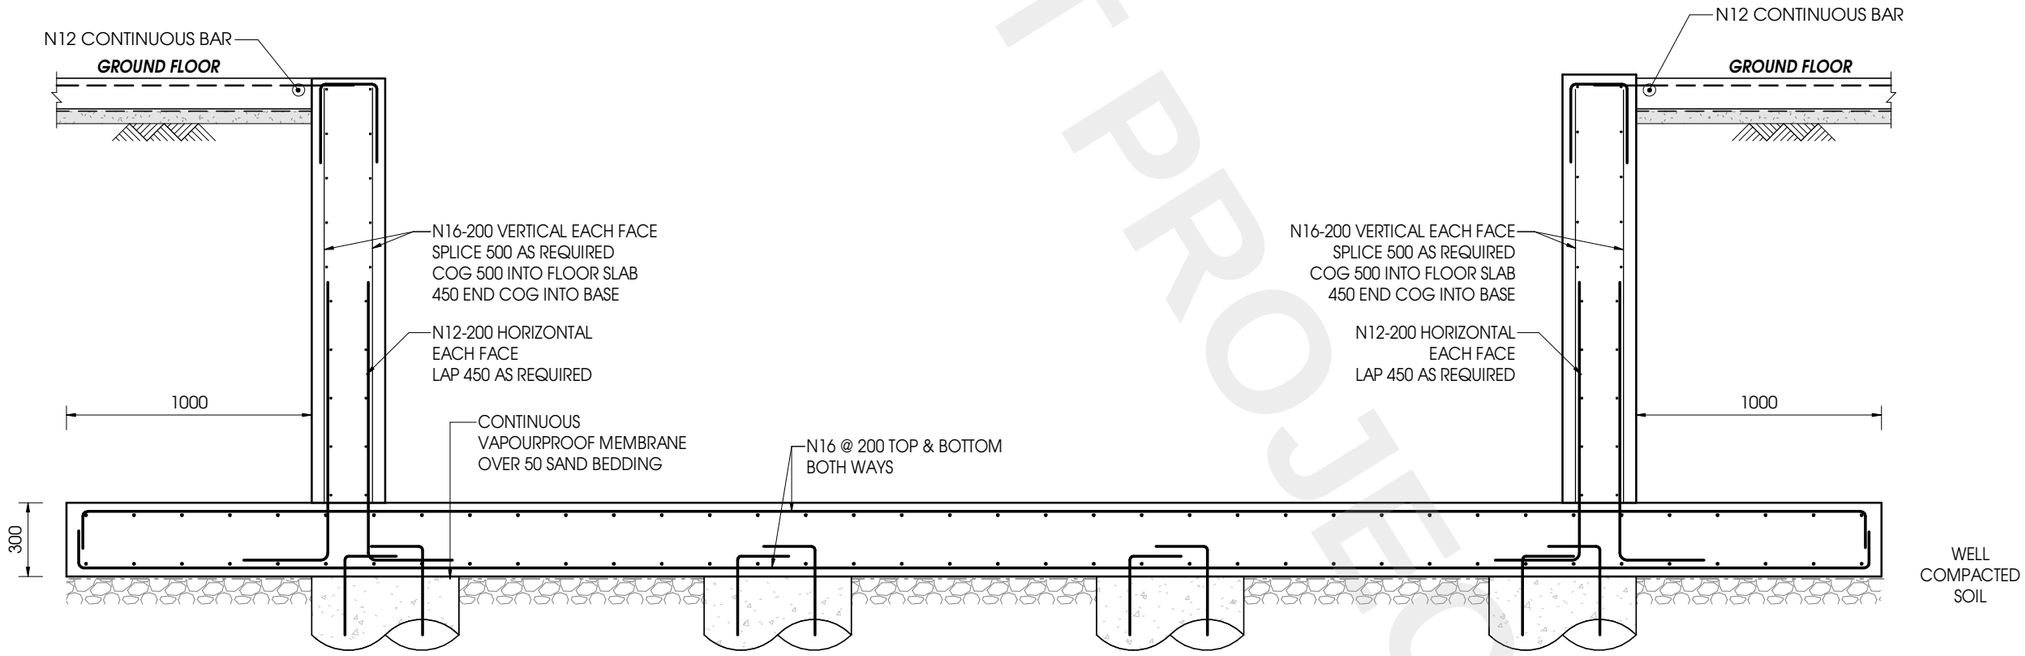

B / STR260 **STACKER PIT SECTION**

SCALE: 1 : 25

TEST PROJECT USAGE

MODULAR ENGINEERS P/L
Structural Engineering | Civil Engineering
Stormwater Engineering | Flood Engineering
Traffic Engineering | Temporary works
ABN : 66 646 960 929
TEL. : 02 873 08473
MOB. : 04 208 98999
EMAIL :
WEBSITE :
ADDRESS :

CLIENT:

PROJECT TITLE:
MULTI DWELLING

SHEET NAME:
SECTION AND DETAILS

PROJECT NUMBER:
175-2026

INTERNAL REVISIONS:

ISSUE	DATE	DESCRIPTION	BY
E	10-09-26	ISSUED FOR CONSTRUCTION	D.A.
D	08-09-26	ISSUED FOR CONSTRUCTION	D.A.
C	24-08-26	ISSUED FOR PRELIMINARY	D.A.
B	21-08-26	ISSUED FOR PRELIMINARY	D.A.

AMENDMENTS

DRAWN : L.M. DATE: 17-07-26
DESIGNED : A.O. REVISION DATE:
QA CHECK : A.O. 10-09-26
APPROVED BY:

RPEQ: 28316
NPER: 5358554
DATE: 10-09-26

ISSUE TYPE:
CONSTRUCTION

SHEET NUMBER:
STR261

SHEET SIZE: **A3**
REVISION: **E**

PRINT IN COLOUR


SAMPLE PROJECT A - STRUCTURAL REV E - CURRENT - RECRUITMENT ASSESSMENT ONLY

NOTE: THE DESIGN AND DETAILS SHOWN ON THESE DRAWINGS ARE APPLICABLE TO THIS PROJECT ONLY AND MAY NOT BE REPRODUCED IN WHOLE OR IN PART OR BE USED FOR ANY OTHER PROJECT OR PURPOSE WITHOUT THE WRITTEN PERMISSION OF WITH WHOM COPYRIGHT RESIDES.

REGULATED DESIGN RECORD

PROJECT ADDRESS:			
PROJECT TITLE:	MULTI DWELLING		
CONSENT NO:	STR208 - 2023	BODY CORPORATE REG NO:	DEP0001320
DRAWING TITLE:	SECTION AND DETAILS	DRAWING NO:	STR262

REV	DATE DD.MM.YY	DESCRIPTION	DP FULL NAME	REG NO
D	10-09-26	ISSUED FOR CONSTRUCTIO		

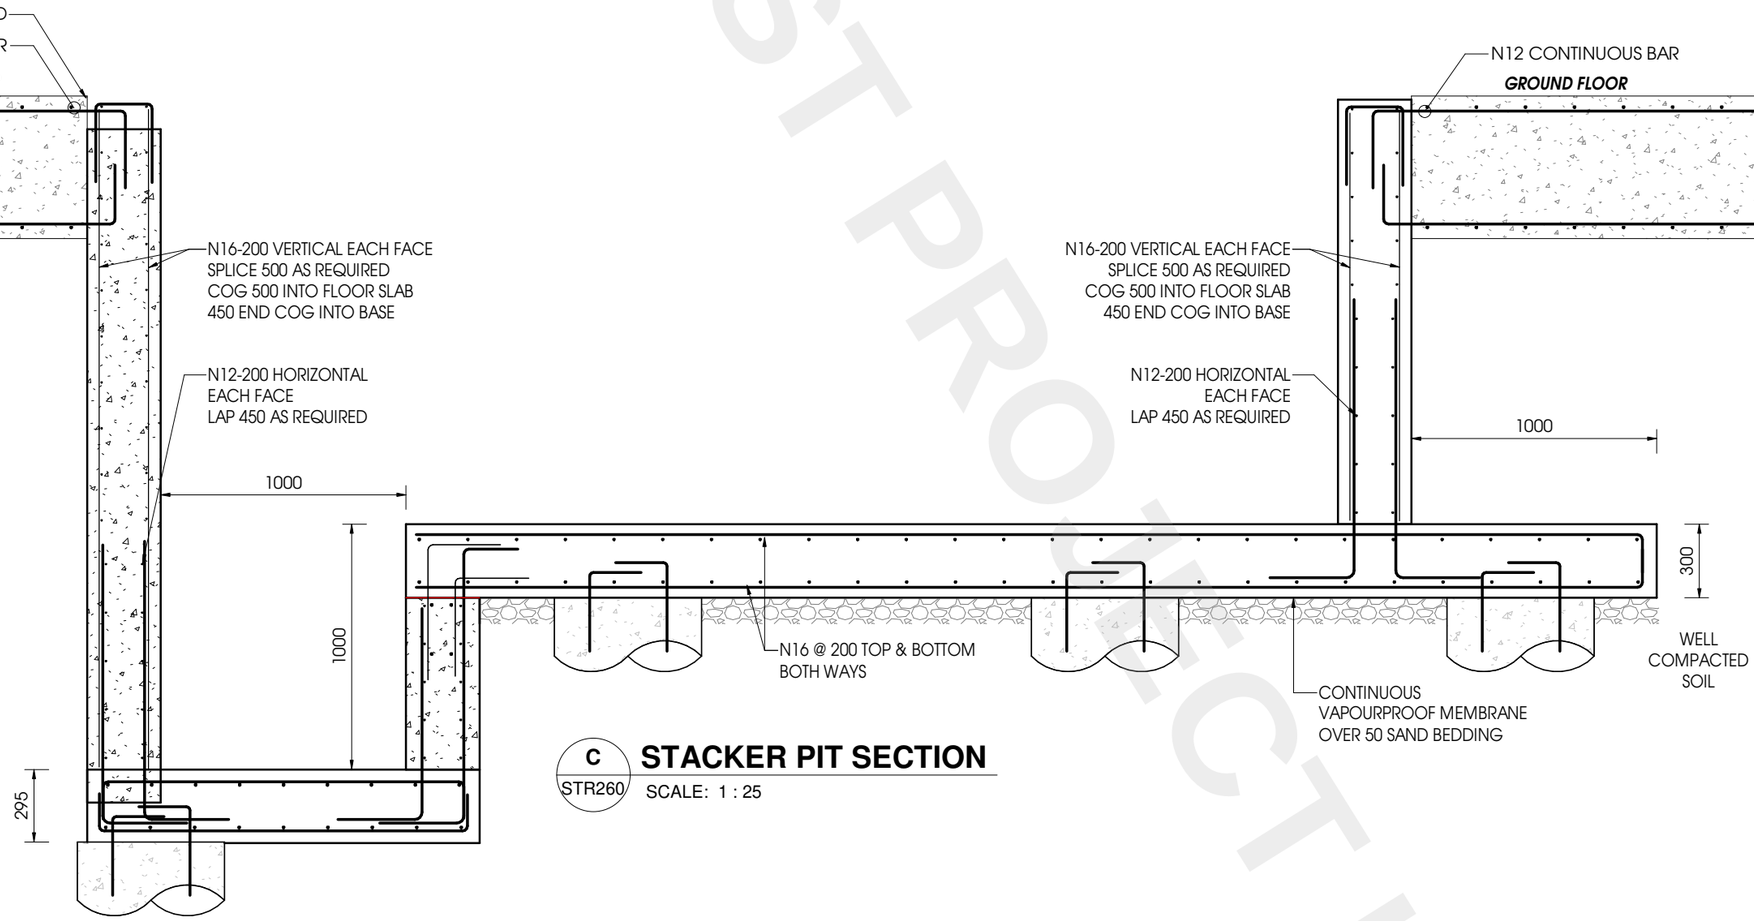

C / STR260 **STACKER PIT SECTION**

SCALE: 1 : 25

TEST PROJECT USAGE

MODULAR ENGINEERS P/L

Structural Engineering | Civil Engineering
Stormwater Engineering | Flood Engineering
Traffic Engineering | Temporary works

ABN : 66 646 960 929
TEL. : 02 873 08473
MOB. : 04 208 98999
EMAIL :
WEBSITE :
ADDRESS :

CLIENT:

PROJECT TITLE:
MULTI DWELLING

SHEET NAME:
SECTION AND DETAILS

PROJECT NUMBER:
175-2026

INTERNAL REVISIONS:

ISSUE	DATE	DESCRIPTION	BY
D	10-09-26	ISSUED FOR CONSTRUCTION	D.A.
C	08-09-26	ISSUED FOR CONSTRUCTION	D.A.
B	24-08-26	ISSUED FOR PRELIMINARY	D.A.
A	21-08-26	ISSUED FOR PRELIMINARY	D.A.

AMENDMENTS

DRAWN : L.M. DATE: 17-07-26
DESIGNED : A.O. REVISION DATE:
QA CHECK : A.O. 10-09-26

APPROVED BY:

RPEQ: 28316
NPER: 5358554
DATE: 10-09-26

ISSUE TYPE:
CONSTRUCTION

SHEET NUMBER:
STR262

SHEET SIZE: **A3** REVISION: **D**

PRINT IN COLOUR

SAMPLE PROJECT A - STRUCTURAL REV E - CURRENT - RECRUITMENT ASSESSMENT ONLY

NOTE: THE DESIGN AND DETAILS SHOWN ON THESE DRAWINGS ARE APPLICABLE TO THIS PROJECT ONLY AND MAY NOT BE REPRODUCED IN WHOLE OR IN PART OR BE USED FOR ANY OTHER PROJECT OR PURPOSE WITHOUT THE WRITTEN PERMISSION OF WITH WHOM COPYRIGHT RESIDES.


REGULATED DESIGN RECORD

PROJECT ADDRESS:	
PROJECT TITLE:	MULTI DWELLING
CONSENT NO:	STR208 - 2023
BODY CORPORATE REG NO:	DEP0001320
DRAWING TITLE:	SECTION AND DETAILS
DRAWING NO:	STR270


REV	DATE DD.MM.YY	DESCRIPTION	DP FULL NAME	REG NO
E	10-09-26	ISSUED FOR CONSTRUCTIO		

WALL SCHEDULE


FLOOR LEVEL	TYPE	DESCRIPTION	THK (mm)	VERT. REINF.	HORZ. REINF.	f'c
GROUND	GW1	RITEK WALL	150	N12-200 E.F.	N12-200 E.F.	32 MPa
	GW2	RITEK WALL	200	N12-200 E.F.	N12-00 E.F.	32 MPa
LEVEL 1	1W1	RITEK WALL	200	N12-200 E.F.	N12-200 E.F.	32 MPa
	1W2	RITEK WALL	200	N12-200 E.F.	N12-200 E.F.	32 MPa
	1W3	RITEK WALL	150	N12-200 E.F.	N12-200 E.F.	32 MPa
LEVEL 2	2W1	RITEK WALL	200	N12-200 E.F.	N12-200 E.F.	32 MPa
	2W2	RITEK WALL	200	N12-200 E.F.	N12-300 E.F.	32 MPa
	2W3	RITEK WALL	150	N12-200 E.F.	N12-200 E.F.	32 MPa
LEVEL 3	3W1	RITEK WALL	200	N12-250 E.F.	N12-250 E.F.	32 MPa
	3W2	RITEK WALL	200	N12-250 E.F.	N12-250 E.F.	32 MPa
	3W3	RITEK WALL	150	N12-250 E.F.	N12-250 E.F.	32 MPa
LEVEL 4	4W1	RITEK WALL	200	N12-300 E.F.	N12-300 E.F.	32 MPa

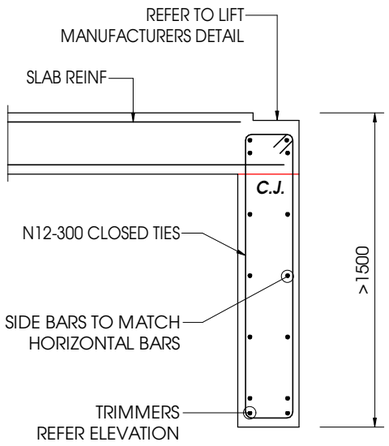


DOORHEAD

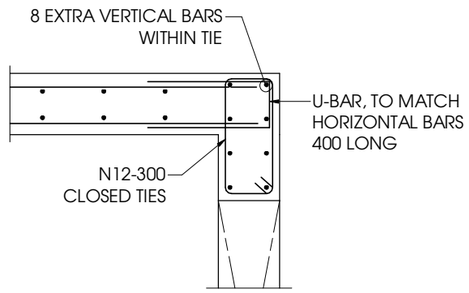


END OF WALL WITH DOOR OPENING

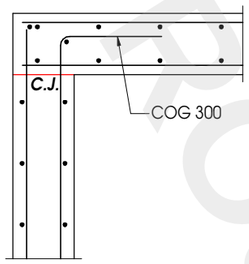

TOP OF WALL AT SLAB

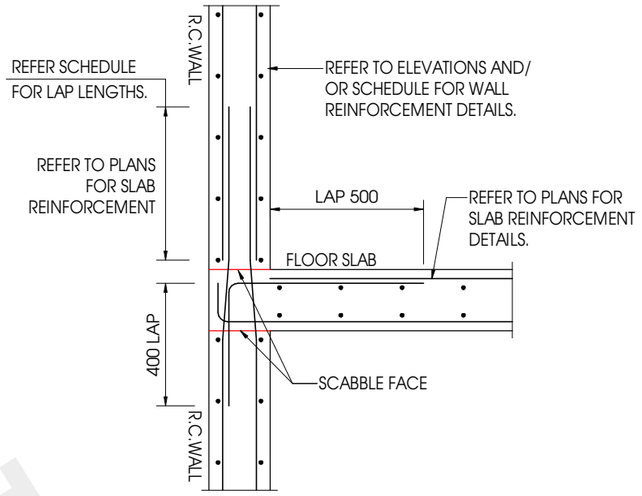


TYPICAL CONTINUOUS PERIMETER WALL TO SLAB DETAILS

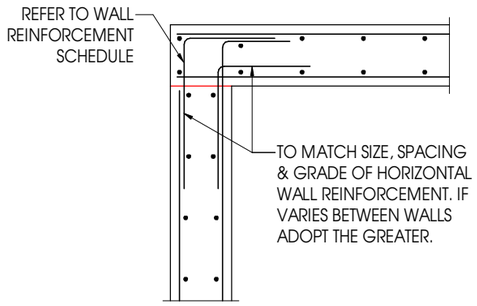


CORNER DETAIL


NOTE:
- WALL SECTION EACH FACE REINFORCEMENT

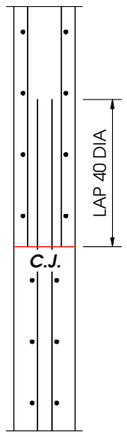

INTERMEDIATE SPLICE DETAIL

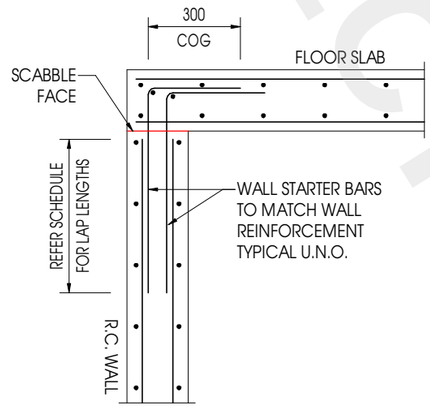

TYPICAL PERIMETER WALL UNDER DETAILS

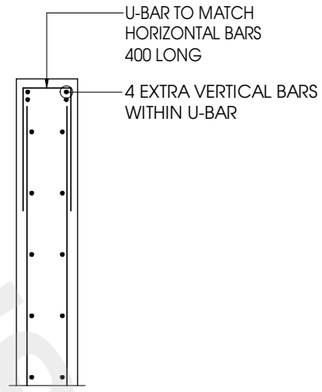

END OF WALL

TYPICAL R.C. WALL DETAILS - DOUBLE LAYER

PRINT IN COLOUR

NOTE: THE DESIGN AND DETAILS SHOWN ON THESE DRAWINGS ARE APPLICABLE TO THIS PROJECT ONLY AND MAY NOT BE REPRODUCED IN WHOLE OR IN PART OR BE USED FOR ANY OTHER PROJECT OR PURPOSE WITHOUT THE WRITTEN PERMISSION OF WITH WHOM COPYRIGHT RESIDES.

TEST PROJECT USAGE ONLY

SAMPLE PROJECT A - STRUCTURAL REV E - CURRENT - RECRUITMENT ASSESSMENT ONLY

MODULAR ENGINEERS P/L
Structural Engineering | Civil Engineering
Stormwater Engineering | Flood Engineering
Traffic Engineering | Temporary works
ABN : 66 646 960 929
TEL. : 02 873 08473
MOB. : 04 208 98999
EMAIL :
WEBSITE :
ADDRESS :

CLIENT:

PROJECT TITLE:
MULTI DWELLING

SHEET NAME:
SECTION AND DETAILS

PROJECT NUMBER:
175-2026

INTERNAL REVISIONS:

ISSUE	DATE	DESCRIPTION	BY
E	10-09-26	ISSUED FOR CONSTRUCTION	D.A.
D	08-09-26	ISSUED FOR CONSTRUCTION	D.A.
C	24-08-26	ISSUED FOR PRELIMINARY	D.A.
B	21-08-26	ISSUED FOR PRELIMINARY	D.A.

AMENDMENTS

DRAWN :	L.M.	DATE:	17-07-26
DESIGNED :	A.O.	REVISION DATE:	
QA CHECK :	A.O.		10-09-26

APPROVED BY:

RPEQ:	28316
NPER:	5358554
DATE:	10-09-26

ISSUE TYPE:
CONSTRUCTION

SHEET NUMBER:
STR270

SHEET SIZE:	REVISION:
A3	E


REGULATED DESIGN RECORD

PROJECT ADDRESS:			
PROJECT TITLE:	MULTI DWELLING		
CONSENT NO:	STR208 - 2023	BODY CORPORATE REG NO:	DEP0001320
DRAWING TITLE:	STAIR DETAILS	DRAWING NO:	STR280

REV	DATE DD.MM.YY	DESCRIPTION	DP FULL NAME	REG NO
E	10-09-26	ISSUED FOR CONSTRUCTIO		

STAIR CONCRETE SCHEDULE


MAX LENGTH OF FLIGHT (L)	WIDTH (L)	GENERAL LAYOUT	REBAR (U.N.O.)				THICKNESS	f'c (MPa)
			LONGITUDINAL		CROSS ROD			
			BOT	TOP	BOT	TOP		
2.5m	1.2m		N12-150	N12-150	N12-300	N12-300	180	32
3.0m	1.2m		N12-150	N12-150	N12-300	N12-300	180	32
4.0m	1.2m		N12-150	N12-150	N12-300	N12-300	180	32
5.0m	1.2m		N12-150	N12-150	N12-300	N12-300	200	32
6.0m	1.2m		N12-150	N12-150	N12-300	N12-300	200	32

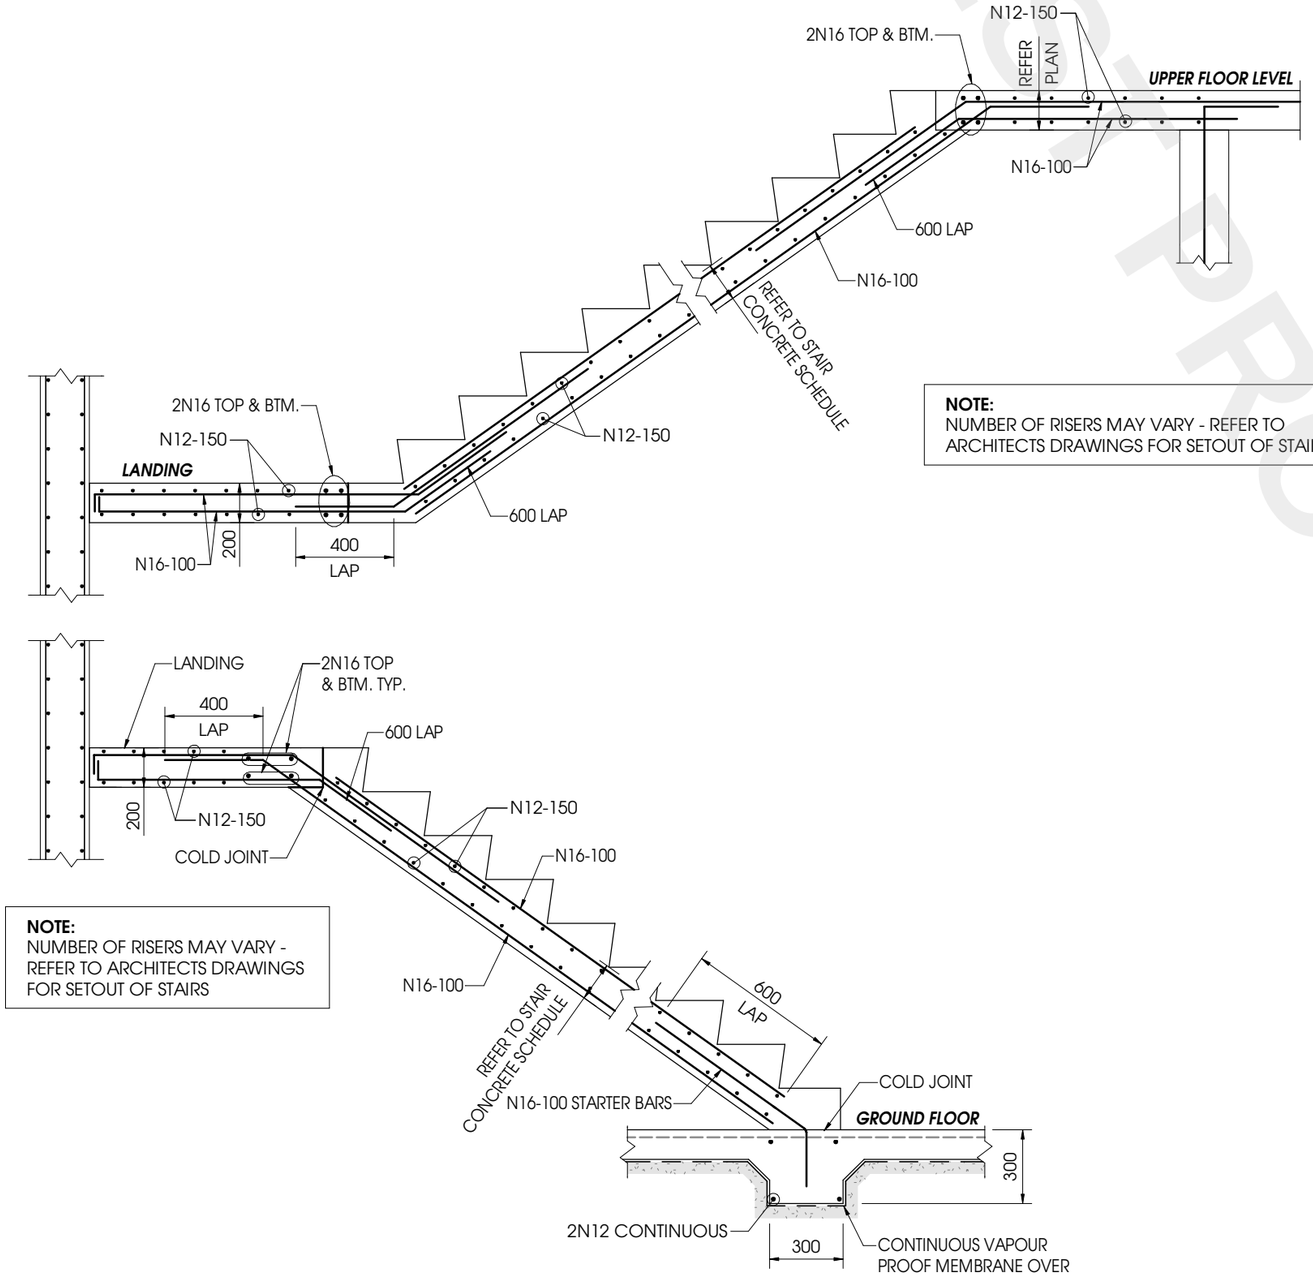

NOTE:
NUMBER OF RISERS MAY VARY - REFER TO ARCHITECTS DRAWINGS FOR SETOUT OF STAIRS

NOTE:
NUMBER OF RISERS MAY VARY - REFER TO ARCHITECTS DRAWINGS FOR SETOUT OF STAIRS

TYPICAL MAIN FLIGHT

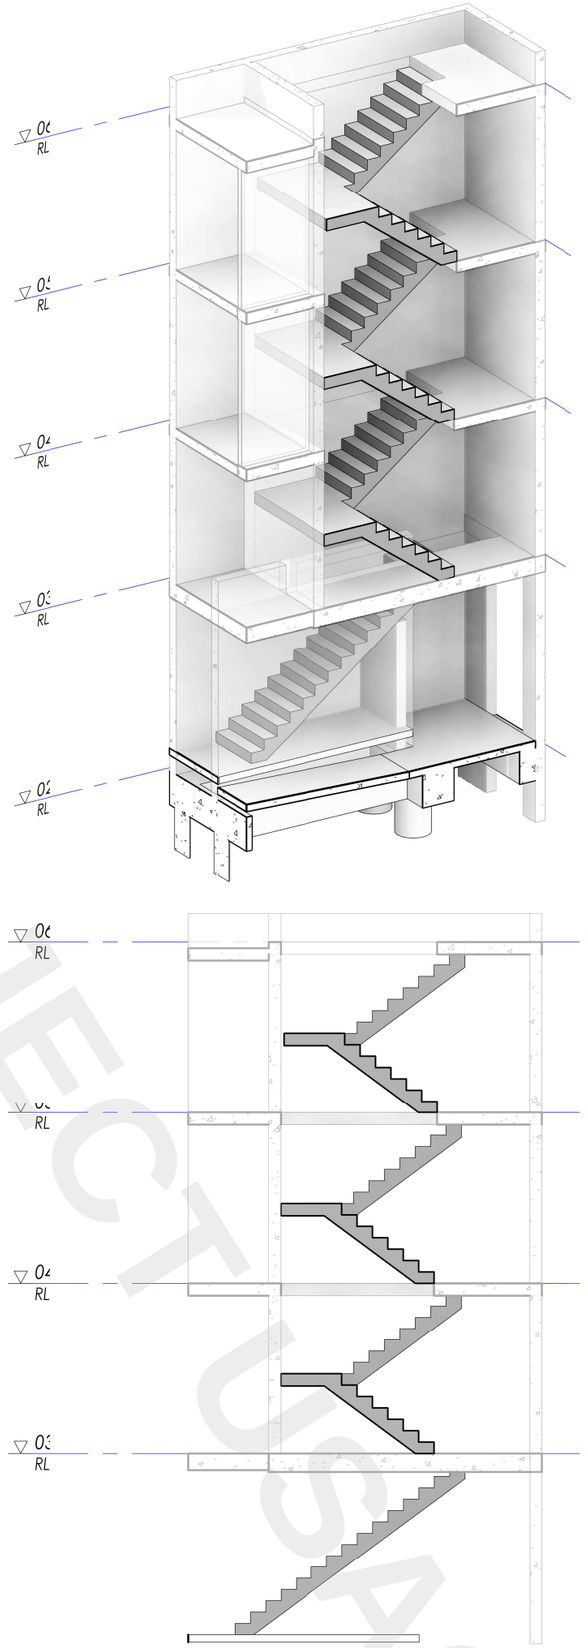

MODULAR ENGINEERS P/L

Structural Engineering | Civil Engineering
Stormwater Engineering | Flood Engineering
Traffic Engineering | Temporary works

ABN : 66 646 960 929
TEL. : 02 873 08473
MOB. : 04 208 98999
EMAIL :
WEBSITE :
ADDRESS :

CLIENT:

PROJECT TITLE:
MULTI DWELLING

SHEET NAME:
STAIR DETAILS

PROJECT NUMBER:
175-2026

INTERNAL REVISIONS:

ISSUE	DATE	DESCRIPTION	BY
E	10-09-26	ISSUED FOR CONSTRUCTION	D.A.
D	08-09-26	ISSUED FOR CONSTRUCTION	D.A.
C	24-08-26	ISSUED FOR PRELIMINARY	D.A.
B	21-08-26	ISSUED FOR PRELIMINARY	D.A.

AMENDMENTS

DRAWN : L.M. DATE: 17-07-26
DESIGNED : A.O. REVISION DATE:
QA CHECK : A.O. 10-09-26

APPROVED BY:

RPEQ: 28316
NPER: 5358554
DATE: 10-09-26

ISSUE TYPE:
CONSTRUCTION

SHEET NUMBER:
STR280

SHEET SIZE: **A3** REVISION: **E**

PRINT IN COLOUR

SAMPLE PROJECT A - STRUCTURAL REV E - CURRENT - RECRUITMENT ASSESSMENT ONLY

SAMPLE PROJECT USAGE

NOTE: THE DESIGN AND DETAILS SHOWN ON THESE DRAWINGS ARE APPLICABLE TO THIS PROJECT ONLY AND MAY NOT BE REPRODUCED IN WHOLE OR IN PART OR BE USED FOR ANY OTHER PROJECT OR PURPOSE WITHOUT THE WRITTEN PERMISSION OF WITH WHOM COPYRIGHT RESIDES.


REGULATED DESIGN RECORD

PROJECT ADDRESS:			
PROJECT TITLE:	MULTI DWELLING		
CONSENT NO:	STR208 - 2023	BODY CORPORATE REG NO:	DEP0001320
DRAWING TITLE:	STAIR DETAILS	DRAWING NO:	STR281

REV	DATE DD.MM.YY	DESCRIPTION	DP FULL NAME	REG NO
E	10-09-26	ISSUED FOR CONSTRUCTIO		


STAIR CONCRETE SCHEDULE

MAX LENGTH OF FLIGHT (L)	WIDTH (L)	GENERAL LAYOUT	REBAR (U.N.O.)				THICKNESS	f'c (MPa)
			LONGITUDINAL		CROSS ROD			
			BOT	TOP	BOT	TOP		
2.5m	1.2m		N12-150	N12-150	N12-300	N12-300	180	32
3.0m	1.2m		N12-150	N12-150	N12-300	N12-300	180	32
4.0m	1.2m		N12-150	N12-150	N12-300	N12-300	180	32
5.0m	1.2m		N12-150	N12-150	N12-300	N12-300	200	32
6.0m	1.2m		N12-150	N12-150	N12-300	N12-300	200	32

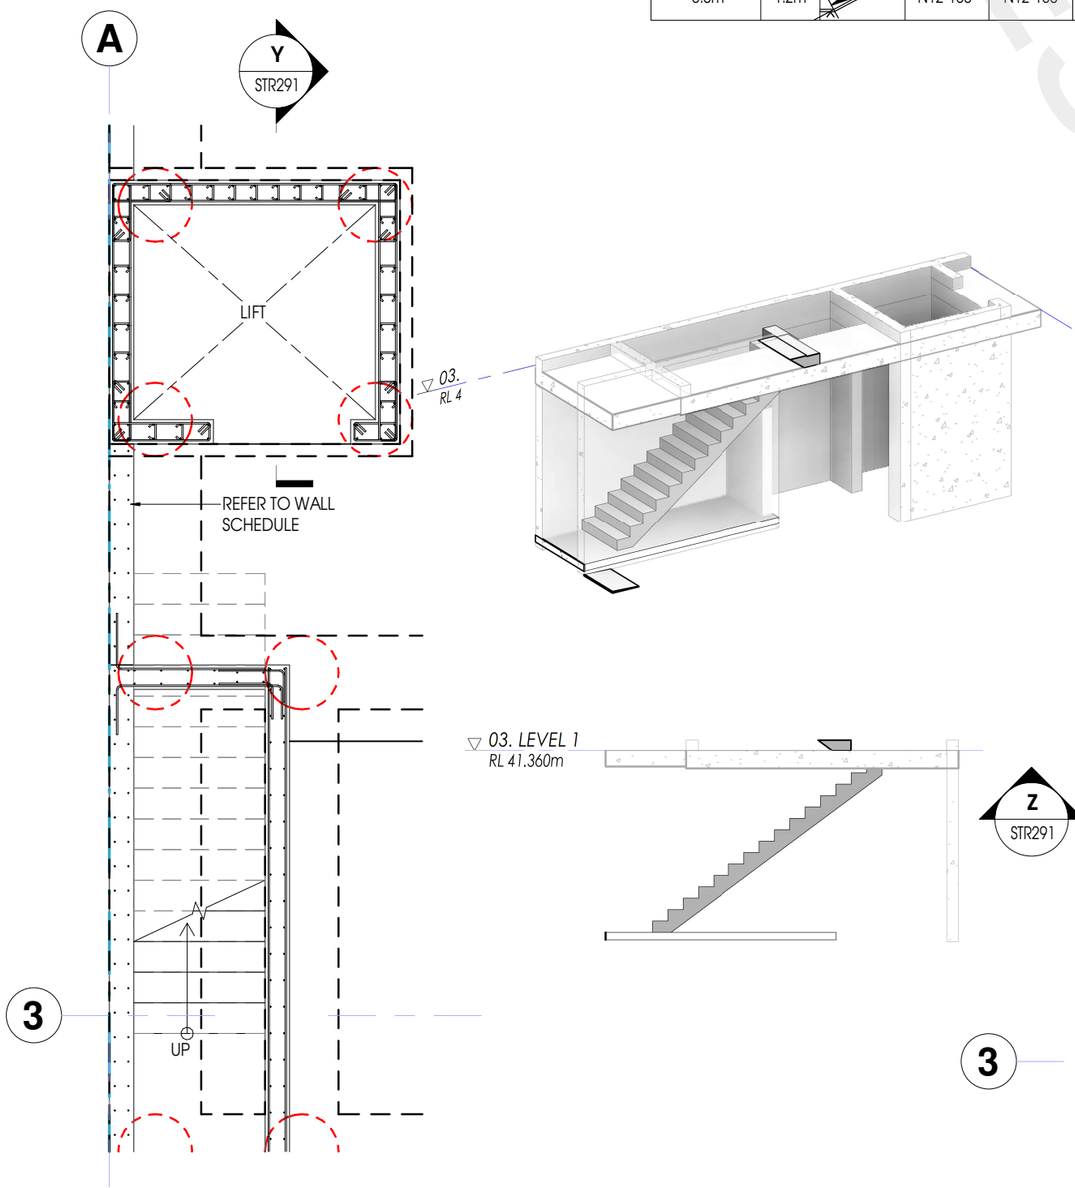

STAIR PLAN (GROUND FLOOR)

SCALE: 1 : 50

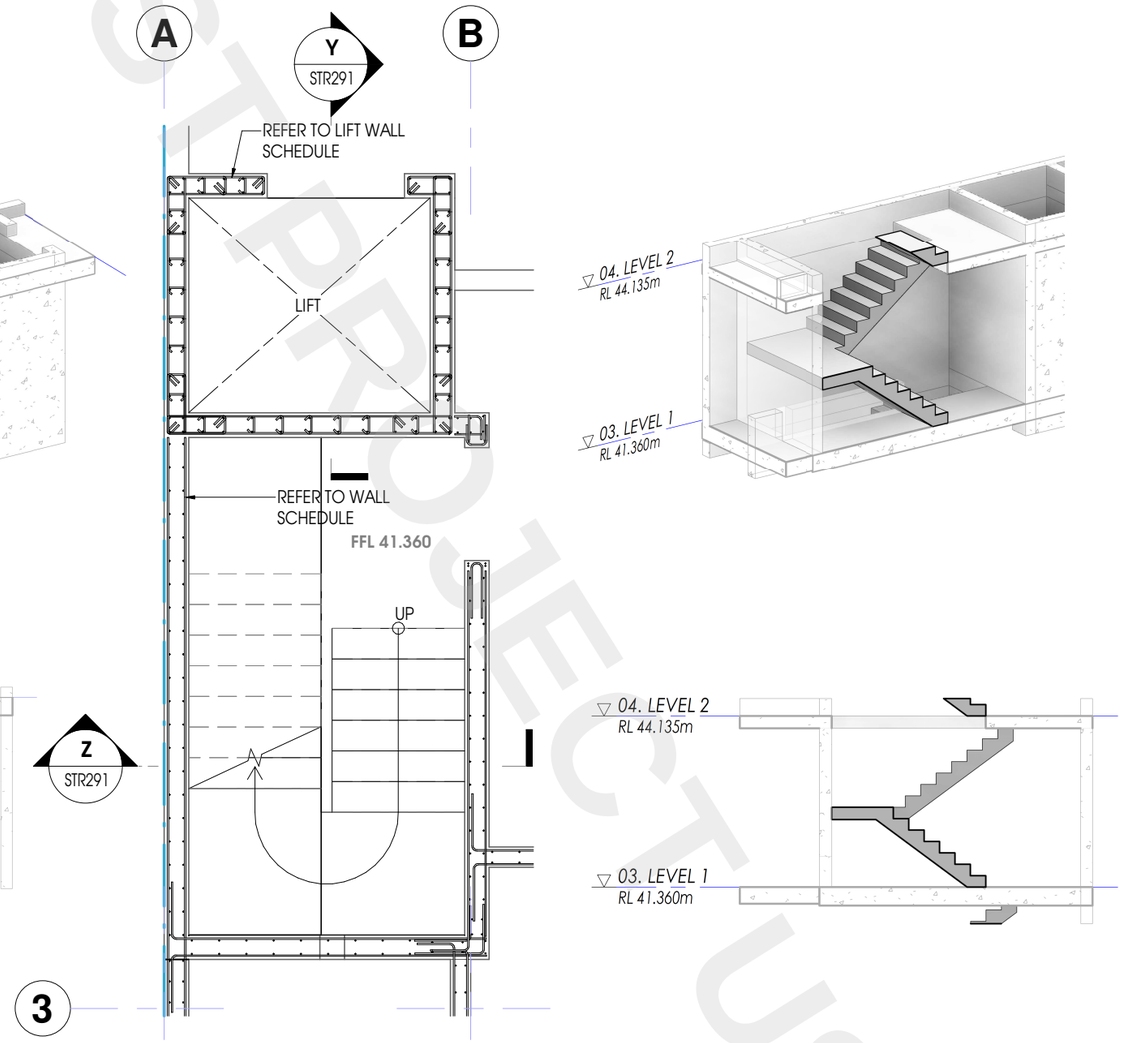

STAIR PLAN (LEVEL 1)

SCALE: 1 : 50

PROJECT TUSAC

PRINT IN COLOUR

MODULAR ENGINEERS P/L

Structural Engineering | Civil Engineering
Stormwater Engineering | Flood Engineering
Traffic Engineering | Temporary works

ABN : 66 646 960 929
TEL. : 02 873 08473
MOB. : 04 208 98999
EMAIL :
WEBSITE :
ADDRESS :

CLIENT:

PROJECT TITLE:
MULTI DWELLING

SHEET NAME:
STAIR DETAILS

PROJECT NUMBER:
175-2026

INTERNAL REVISIONS:

ISSUE	DATE	DESCRIPTION	BY
E	10-09-26	ISSUED FOR CONSTRUCTION	D.A.
D	08-09-26	ISSUED FOR CONSTRUCTION	D.A.
C	24-08-26	ISSUED FOR PRELIMINARY	D.A.
B	21-08-26	ISSUED FOR PRELIMINARY	D.A.

AMENDMENTS

DRAWN : L.M. DATE: 17-07-26
DESIGNED : A.O. REVISION DATE:
QA CHECK : A.O. 10-09-26
APPROVED BY:

RPEQ: 28316
NPER: 5358554
DATE: 10-09-26

ISSUE TYPE:
CONSTRUCTION

SHEET NUMBER:
STR281

SHEET SIZE: **A3** REVISION: **E**

SAMPLE PROJECT A - STRUCTURAL REV E - CURRENT - RECRUITMENT ASSESSMENT ONLY

NOTE: THE DESIGN AND DETAILS SHOWN ON THESE DRAWINGS ARE APPLICABLE TO THIS PROJECT ONLY AND MAY NOT BE REPRODUCED IN WHOLE OR IN PART OR BE USED FOR ANY OTHER PROJECT OR PURPOSE WITHOUT THE WRITTEN PERMISSION OF WITH WHOM COPYRIGHT RESIDES.


REGULATED DESIGN RECORD

PROJECT ADDRESS:	
PROJECT TITLE:	MULTI DWELLING
CONSENT NO:	STR208 - 2023
BODY CORPORATE REG NO:	DEP0001320
DRAWING TITLE:	STAIR DETAILS
DRAWING NO:	STR282

REV	DATE DD.MM.YY	DESCRIPTION	DP FULL NAME	REG NO
E	10-09-26	ISSUED FOR CONSTRUCTIO		


STAIR CONCRETE SCHEDULE

MAX LENGTH OF FLIGHT (L)	WIDTH (L)	GENERAL LAYOUT	REBAR (U.N.O.)				THICKNESS	f'c (MPa)
			LONGITUDINAL		CROSS ROD			
			BOT	TOP	BOT	TOP		
2.5m	1.2m		N12-150	N12-150	N12-300	N12-300	180	32
3.0m	1.2m		N12-150	N12-150	N12-300	N12-300	180	32
4.0m	1.2m		N12-150	N12-150	N12-300	N12-300	180	32
5.0m	1.2m		N12-150	N12-150	N12-300	N12-300	200	32
6.0m	1.2m		N12-150	N12-150	N12-300	N12-300	200	32

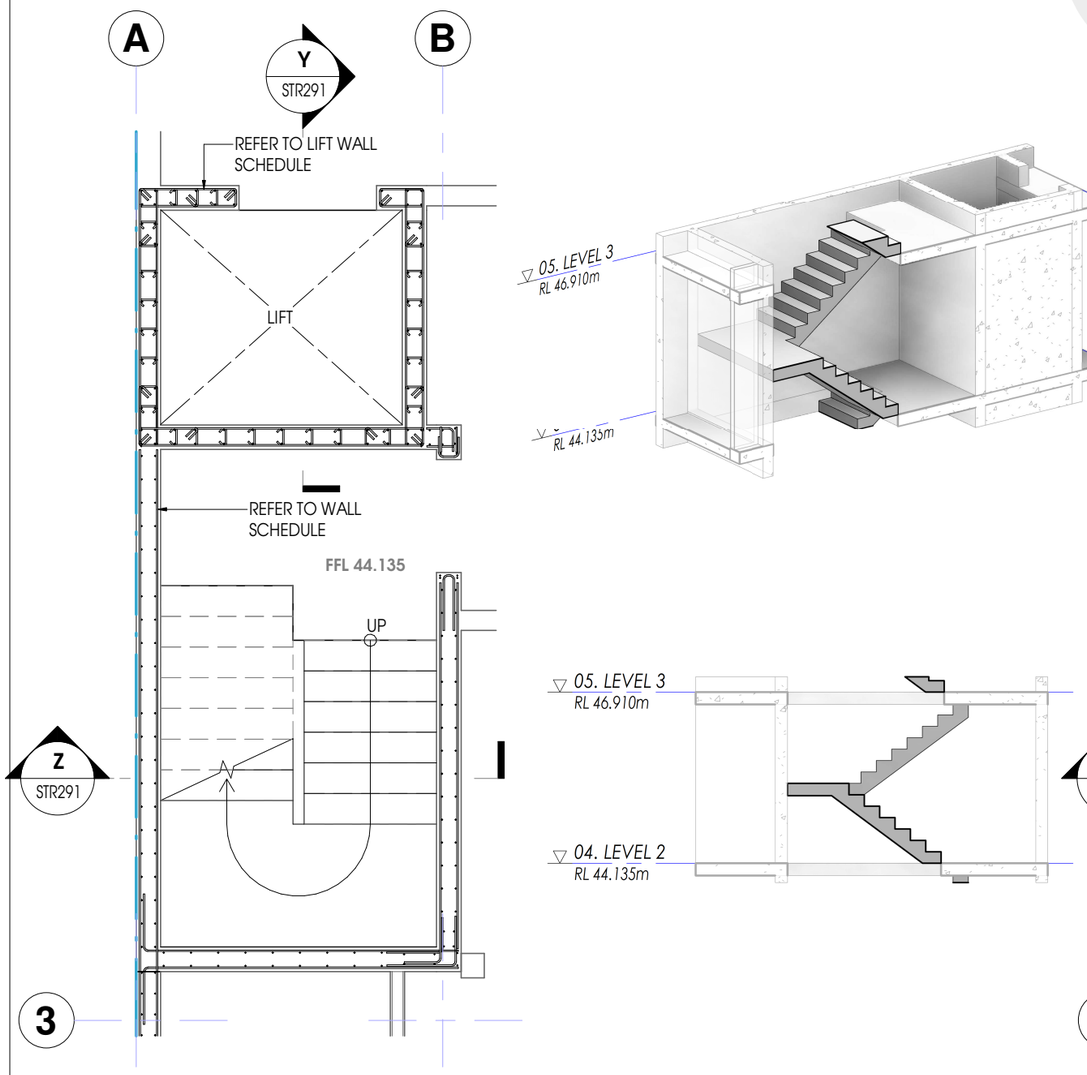

STAIR PLAN (LEVEL 2)

SCALE: 1 : 50

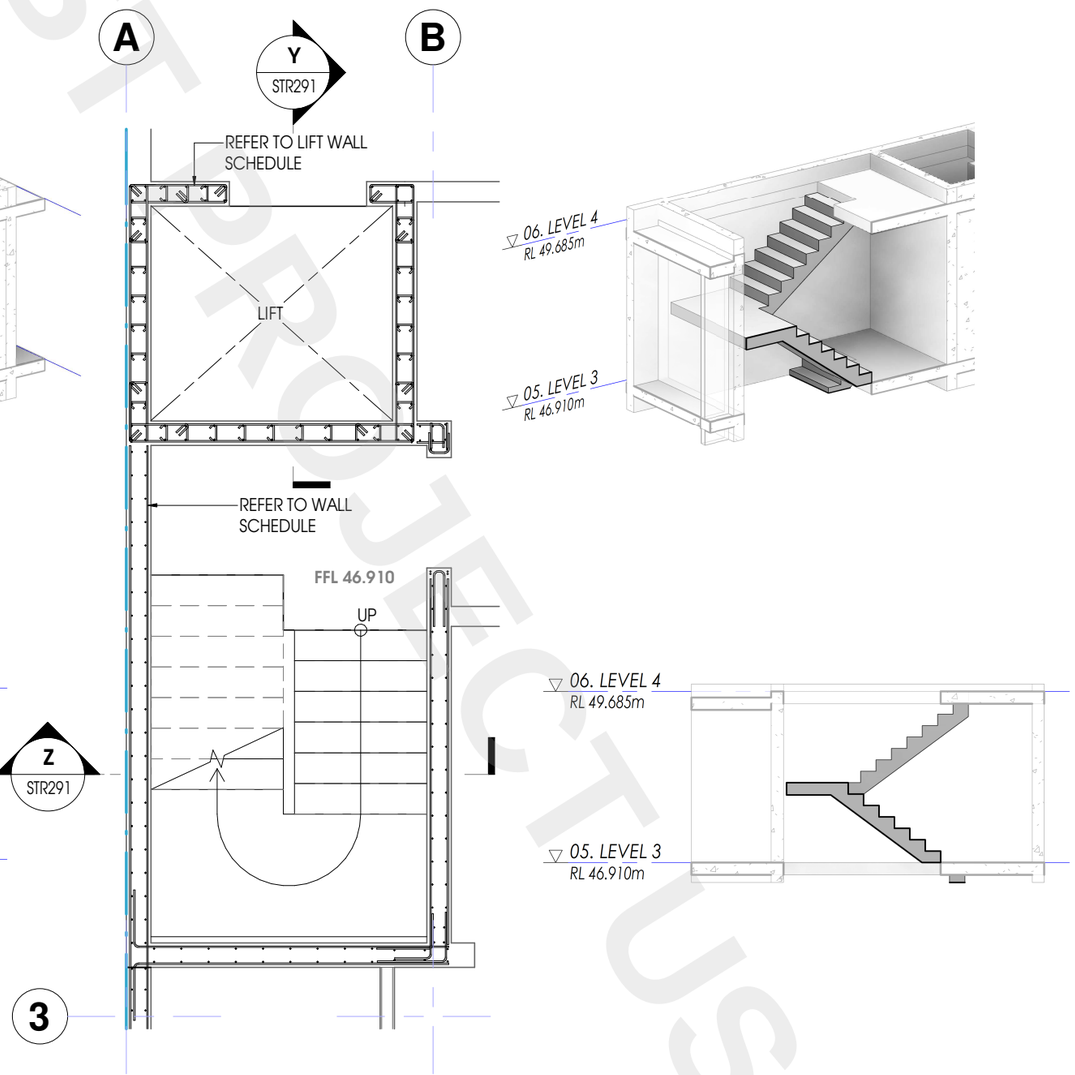

STAIR PLAN (LEVEL 3)

SCALE: 1 : 50

PRINT IN COLOUR

MODULAR ENGINEERS P/L

Structural Engineering | Civil Engineering
Stormwater Engineering | Flood Engineering
Traffic Engineering | Temporary works

ABN : 66 646 960 929
TEL. : 02 873 08473
MOB. : 04 208 98999
EMAIL :
WEBSITE :
ADDRESS :

CLIENT:

PROJECT TITLE:
MULTI DWELLING

SHEET NAME:
STAIR DETAILS

PROJECT NUMBER:
175-2026

INTERNAL REVISIONS:

ISSUE	DATE	DESCRIPTION	BY
E	10-09-26	ISSUED FOR CONSTRUCTION	D.A.
D	08-09-26	ISSUED FOR CONSTRUCTION	D.A.
C	24-08-26	ISSUED FOR PRELIMINARY	D.A.
B	21-08-26	ISSUED FOR PRELIMINARY	D.A.

AMENDMENTS

DRAWN : L.M. DATE: 17-07-26
DESIGNED : A.O. REVISION DATE:
QA CHECK : A.O. 10-09-26
APPROVED BY:

RPEQ: 28316
NPER: 5358554
DATE: 10-09-26

ISSUE TYPE:
CONSTRUCTION

SHEET NUMBER:
STR282

SHEET SIZE: **A3**
REVISION: **E**

SAMPLE PROJECT A - STRUCTURAL REV E - CURRENT - RECRUITMENT ASSESSMENT ONLY

TEST PROJECT USAGE ONLY

NOTE: THE DESIGN AND DETAILS SHOWN ON THESE DRAWINGS ARE APPLICABLE TO THIS PROJECT ONLY AND MAY NOT BE REPRODUCED IN WHOLE OR IN PART OR BE USED FOR ANY OTHER PROJECT OR PURPOSE WITHOUT THE WRITTEN PERMISSION OF WITH WHOM COPYRIGHT RESIDES.


REGULATED DESIGN RECORD


PROJECT ADDRESS:	
PROJECT TITLE:	MULTI DWELLING
CONSENT NO:	STR208 - 2023
BODY CORPORATE REG NO:	DEP0001320
DRAWING TITLE:	STAIR DETAILS
DRAWING NO:	STR283


REV	DATE DD.MM.YY	DESCRIPTION	DP FULL NAME	REG NO
E	10-09-26	ISSUED FOR CONSTRUCTIO		

STAIR CONCRETE SCHEDULE

MAX LENGTH OF FLIGHT (L)	WIDTH (L)	GENERAL LAYOUT	REBAR (U.N.O.)				THICKNESS	f'c (MPa)
			LONGITUDINAL		CROSS ROD			
			BOT	TOP	BOT	TOP		
2.5m	1.2m		N12-150	N12-150	N12-300	N12-300	180	32
3.0m	1.2m		N12-150	N12-150	N12-300	N12-300	180	32
4.0m	1.2m		N12-150	N12-150	N12-300	N12-300	180	32
5.0m	1.2m		N12-150	N12-150	N12-300	N12-300	200	32
6.0m	1.2m		N12-150	N12-150	N12-300	N12-300	200	32

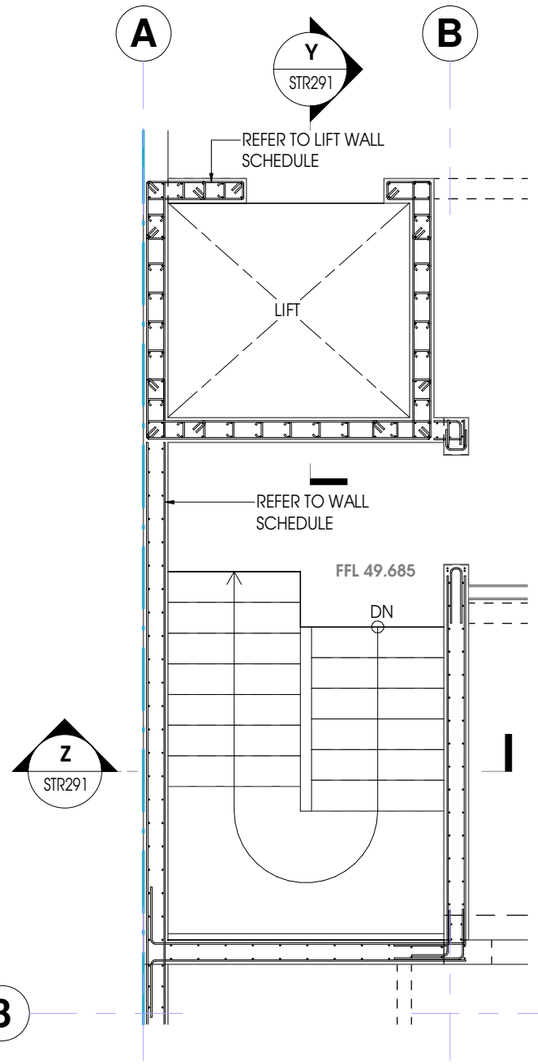

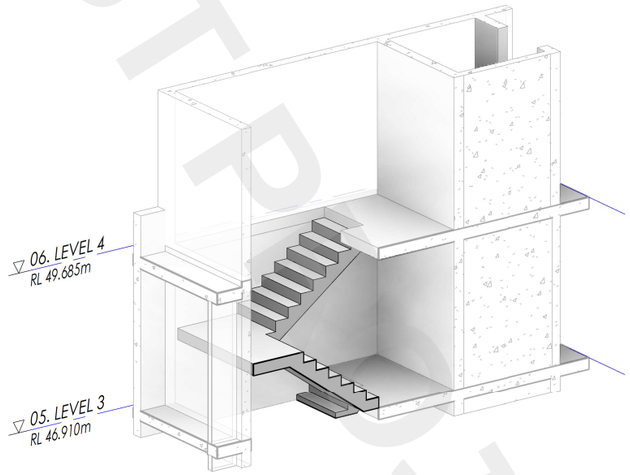

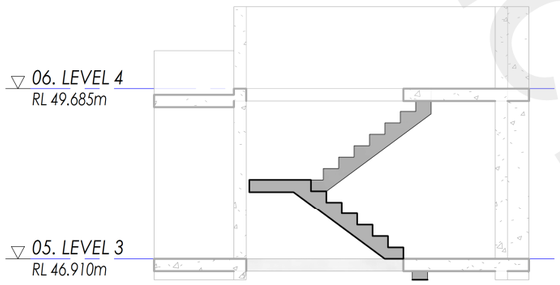

STAIR PLAN (LEVEL 4)

SCALE: 1 : 50

TEST PROJECT USAGE ONLY

MODULAR ENGINEERS P/L
Structural Engineering | Civil Engineering
Stormwater Engineering | Flood Engineering
Traffic Engineering | Temporary works
ABN : 66 646 960 929
TEL. : 02 873 08473
MOB. : 04 208 98999
EMAIL :
WEBSITE :
ADDRESS :

CLIENT:

PROJECT TITLE:
MULTI DWELLING

SHEET NAME:
STAIR DETAILS

PROJECT NUMBER:
175-2026

INTERNAL REVISIONS:

ISSUE	DATE	DESCRIPTION	BY
E	10-09-26	ISSUED FOR CONSTRUCTION	D.A.
D	08-09-26	ISSUED FOR CONSTRUCTION	D.A.
C	24-08-26	ISSUED FOR PRELIMINARY	D.A.
B	21-08-26	ISSUED FOR PRELIMINARY	D.A.

AMENDMENTS

DRAWN : L.M. DATE: 17-07-26
DESIGNED : A.O. REVISION DATE:
QA CHECK : A.O. 10-09-26
APPROVED BY:

RPEQ: 28316
NPER: 5358554
DATE: 10-09-26

ISSUE TYPE:
CONSTRUCTION

SHEET NUMBER:
STR283

SHEET SIZE: **A3** REVISION: **E**

PRINT IN COLOUR

SAMPLE PROJECT A - STRUCTURAL REV E - CURRENT - RECRUITMENT ASSESSMENT ONLY

NOTE: THE DESIGN AND DETAILS SHOWN ON THESE DRAWINGS ARE APPLICABLE TO THIS PROJECT ONLY AND MAY NOT BE REPRODUCED IN WHOLE OR IN PART OR BE USED FOR ANY OTHER PROJECT OR PURPOSE WITHOUT THE WRITTEN PERMISSION OF WITH WHOM COPYRIGHT RESIDES.

REGULATED DESIGN RECORD

PROJECT ADDRESS:	
PROJECT TITLE:	MULTI DWELLING
CONSENT NO:	STR208 - 2023
BODY CORPORATE REG NO:	DEP0001320
DRAWING TITLE:	LIFT DETAILS
DRAWING NO:	STR290

REV	DATE DD.MM.YY	DESCRIPTION	DP FULL NAME	REG NO
E	10-09-26	ISSUED FOR CONSTRUCTIO		


LIFT WALL SCHEDULE

MARK	FLOOR LEVEL	THICKNESS (mm)	VERT. REINF.	HORZ. REINF.	f'c
LW1 - LW4	LIFT PIT TO GF	200 CONCRETE WALL	N16-200 E.F.	N12-200 E.F.	40 MPa
	GF - LEVEL 1	200 CONCRETE WALL	N16-200 E.F.	N16-200 E.F.	40 MPa
	LEVEL 1 - LEVEL 2	200 CONCRETE WALL	N16-200 E.F.	N16-200 E.F.	40 MPa
	LEVEL 2 - LEVEL 3	200 CONCRETE WALL	N16-200 E.F.	N16-200 E.F.	40 MPa
	LEVEL 3 - LEVEL 4	200 CONCRETE WALL	N16-200 E.F.	N16-200 E.F.	40 MPa

NOTES:
1. FOR EXTENT OF WALLS REFER ARCHITECTURAL PLANS.
2. STARTER BARS FOR WALLS TO MATCH VERTICAL REINFORCEMENT IN SCHEDULE.


(REFER ARCHITECTURAL DRAWINGS FOR EXTENT OF LIFT HEIGHT)

NOTE:
1. ALL LIFT WALL ELEVATIONS ARE VIEWED FROM INTERNAL FACE OF WALL, OUTWARDS.
2. REINFORCE WALLS AS PER LIFT WALL SCHEDULE.
3. REFER TO LIFT WALL SCHEDULE FOR WALL THICKNESS.
4. CONCRETE QUALITY AND REINFORCEMENT COVER AS SCHEDULED.

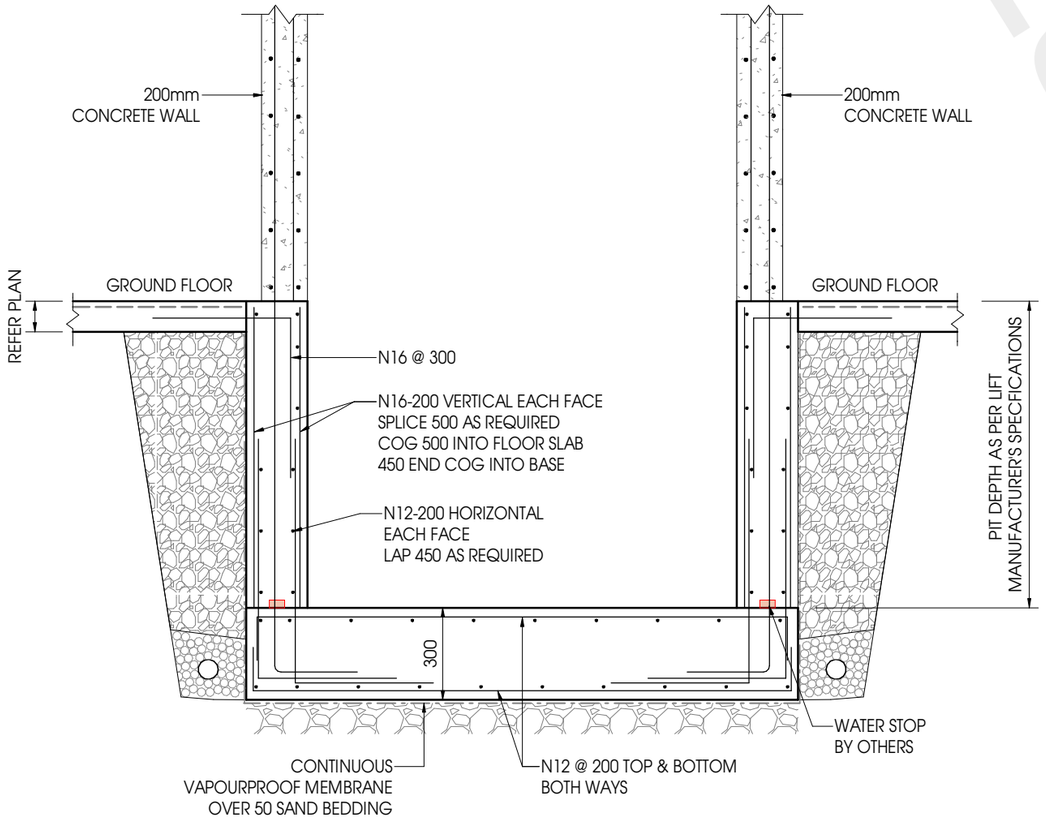


LIFT PIT BASE DETAIL - PF1

NOT TO SCALE

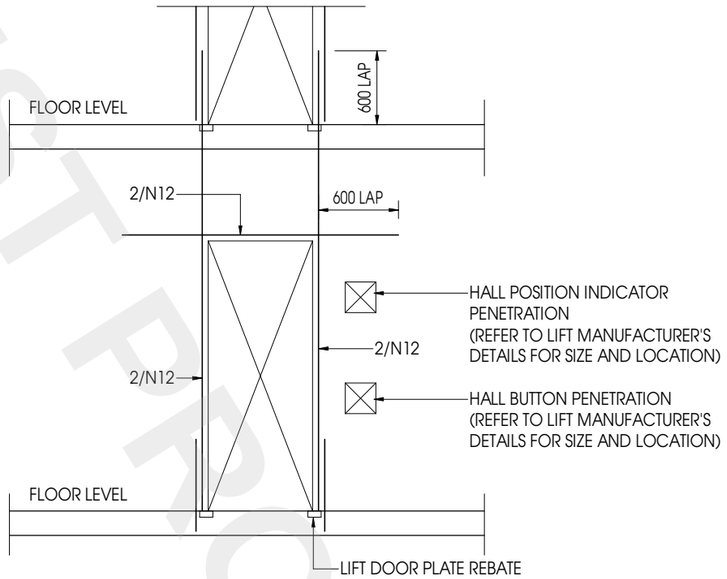


TRIMMERS TO DOOR OPENINGS

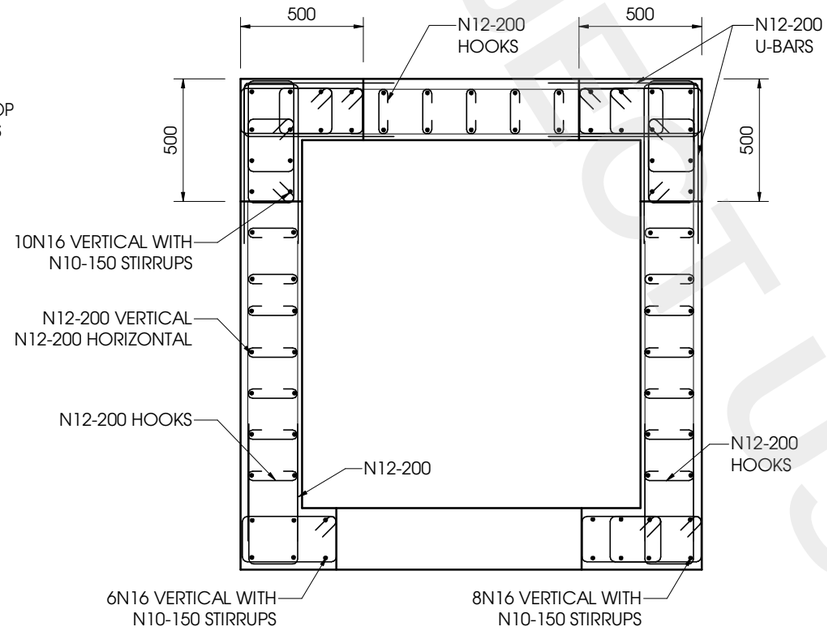

LIFT WALL REINFORCEMENT PLAN

NOT TO SCALE

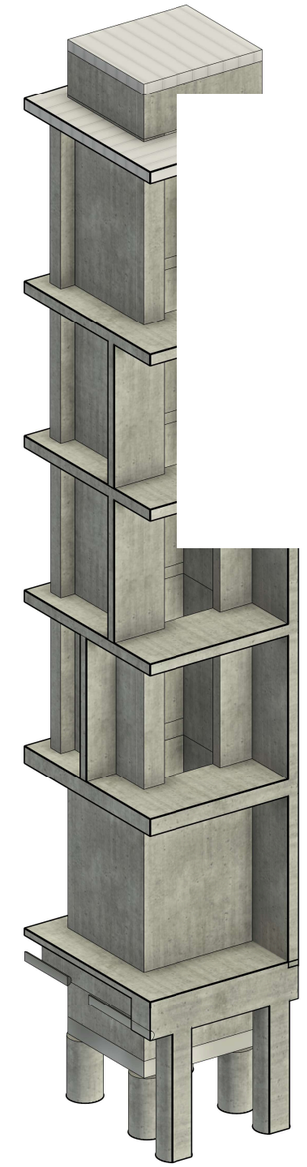

PRINT IN COLOUR

MODULAR ENGINEERS P/L

Structural Engineering | Civil Engineering
Stormwater Engineering | Flood Engineering
Traffic Engineering | Temporary works

ABN : 66 646 960 929
TEL. : 02 873 08473
MOB. : 04 208 98999
EMAIL :
WEBSITE :
ADDRESS :

CLIENT:

PROJECT TITLE:
MULTI DWELLING

SHEET NAME:
LIFT DETAILS

PROJECT NUMBER:
175-2026

INTERNAL REVISIONS:

ISSUE	DATE	DESCRIPTION	BY
E	10-09-26	ISSUED FOR CONSTRUCTION	D.A.
D	08-09-26	ISSUED FOR CONSTRUCTION	D.A.
C	24-08-26	ISSUED FOR PRELIMINARY	D.A.
B	21-08-26	ISSUED FOR PRELIMINARY	D.A.

AMENDMENTS

DRAWN : L.M. DATE: 17-07-26
DESIGNED : A.O. REVISION DATE:
QA CHECK : A.O. 10-09-26

APPROVED BY:

RPEQ: 28316
NPER: 5358554
DATE: 10-09-26

ISSUE TYPE:
CONSTRUCTION

SHEET NUMBER:
STR290

SHEET SIZE: **A3**
REVISION: **E**

SAMPLE PROJECT A - STRUCTURAL REV E - CURRENT - RECRUITMENT ASSESSMENT ONLY


TEST PROJECT USAGE ONLY

NOTE: THE DESIGN AND DETAILS SHOWN ON THESE DRAWINGS ARE APPLICABLE TO THIS PROJECT ONLY AND MAY NOT BE REPRODUCED IN WHOLE OR IN PART OR BE USED FOR ANY OTHER PROJECT OR PURPOSE WITHOUT THE WRITTEN PERMISSION OF WITH WHOM COPYRIGHT RESIDES.

REGULATED DESIGN RECORD

PROJECT ADDRESS:			
PROJECT TITLE:	MULTI DWELLING		
CONSENT NO:	STR208 - 2023	BODY CORPORATE REG NO:	DEP0001320
DRAWING TITLE:	SECTION AND DETAILS	DRAWING NO:	STR291

REV	DATE DD.MM.YY	DESCRIPTION	DP FULL NAME	REG NO
D	10-09-26	ISSUED FOR CONSTRUCTIO		

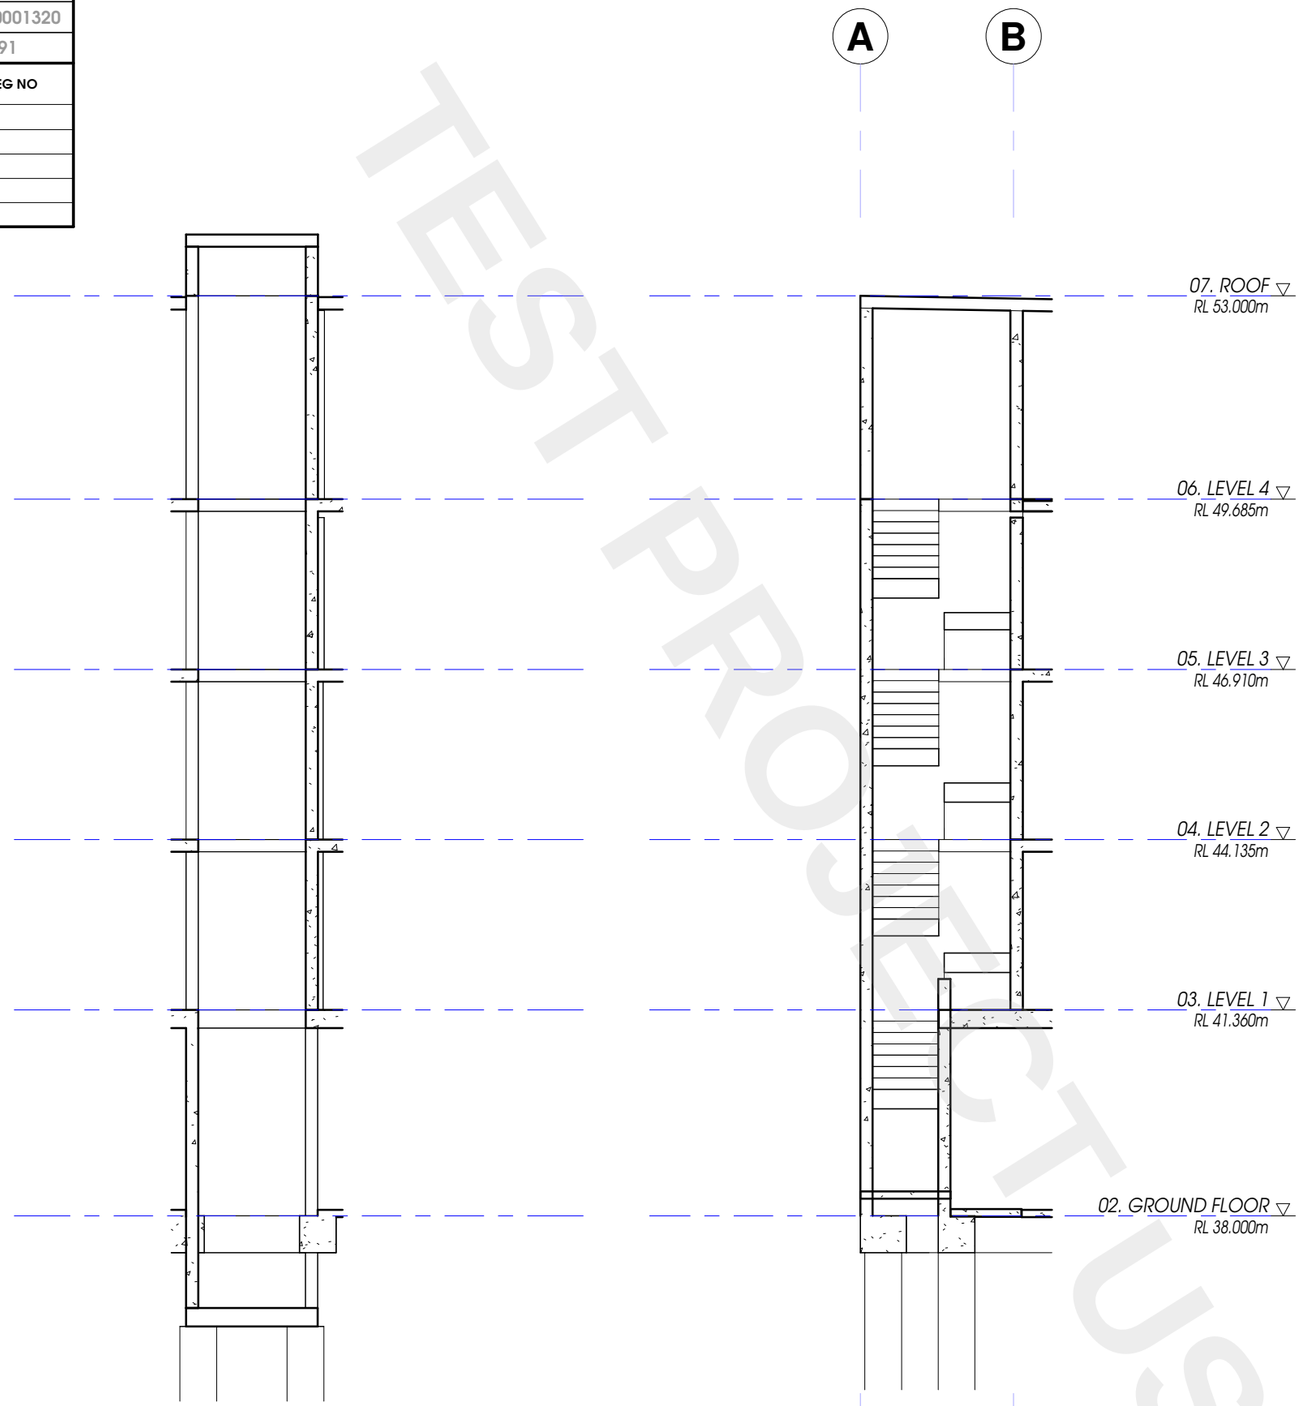

SECTION Y
NOT TO SCALE STR281

SECTION Z
NOT TO SCALE STR281

TEST PROJECT USAGE

PRINT IN COLOUR

MODULAR ENGINEERS P/L

Structural Engineering | Civil Engineering
Stormwater Engineering | Flood Engineering
Traffic Engineering | Temporary works

ABN : 66 646 960 929
TEL. : 02 873 08473
MOB. : 04 208 98999
EMAIL :
WEBSITE :
ADDRESS :

CLIENT:

PROJECT TITLE:
MULTI DWELLING

SHEET NAME:
SECTION AND DETAILS

PROJECT NUMBER:
175-2026

INTERNAL REVISIONS:

ISSUE	DATE	DESCRIPTION	BY
D	10-09-26	ISSUED FOR CONSTRUCTION	D.A.
C	08-09-26	ISSUED FOR CONSTRUCTION	D.A.
B	24-08-26	ISSUED FOR PRELIMINARY	D.A.
A	21-08-26	ISSUED FOR PRELIMINARY	D.A.

AMENDMENTS

DRAWN : L.M. DATE: 17-07-26
DESIGNED : A.O. REVISION DATE:
QA CHECK : A.O. 10-09-26

APPROVED BY:

RPEQ: 28316
NPER: 5358554
DATE: 10-09-26

ISSUE TYPE:
CONSTRUCTION

SHEET NUMBER:
STR291

SHEET SIZE: **A3** REVISION: **D**

SAMPLE PROJECT A - STRUCTURAL REVIEW - CURRENT - RECRUITMENT ASSESSMENT ONLY

NOTE: THE DESIGN AND DETAILS SHOWN ON THESE DRAWINGS ARE APPLICABLE TO THIS PROJECT ONLY AND MAY NOT BE REPRODUCED IN WHOLE OR IN PART OR BE USED FOR ANY OTHER PROJECT OR PURPOSE WITHOUT THE WRITTEN PERMISSION OF WITH WHOM COPYRIGHT RESIDES.

REGULATED DESIGN RECORD

PROJECT ADDRESS:			
PROJECT TITLE:	MULTI DWELLING		
CONSENT NO:	STR208 - 2023	BODY CORPORATE REG NO:	DEP0001320
DRAWING TITLE:	LEVEL 1 FLOOR PLAN	DRAWING NO:	STR500

REV	DATE DD.MM.YY	DESCRIPTION	DP FULL NAME	REG NO
E	10-09-26	ISSUED FOR CONSTRUCTIO		


CONCRETE BEAM SCHEDULE

MARK	SIZE	REINFORCEMENT	REMARKS
1B1	2000x400	10N24 T&B 6N12-200 TIES	
1B2	1500x400	10N24 T&B 6N12-200 TIES	

LEGEND:

- DENOTES CONCRETE COLUMN/ WALL **OVER ONLY**
- DENOTES BRICK WALLS **OVER ONLY**
- DENOTES BLOCK WORK WALLS **OVER ONLY**
- DENOTES RITEK WALLS **OVER ONLY**
- DENOTES CONCRETE WALL/COLUMN **UNDER ONLY**
- DENOTES WET AREA WITH 2mm FALL
- DENOTES SLAB PENETRATION
- DENOTES STEP ON SLAB
- C00 DENOTES COLUMN MARK
- W00 DENOTES WALL MARK
- 000 DENOTES SLAB THICKNESS
- DENOTES EXTENT OF SLAB STEP

FOR STRUCTURAL NOTES REFER TO DRAWING STR00 SERIES

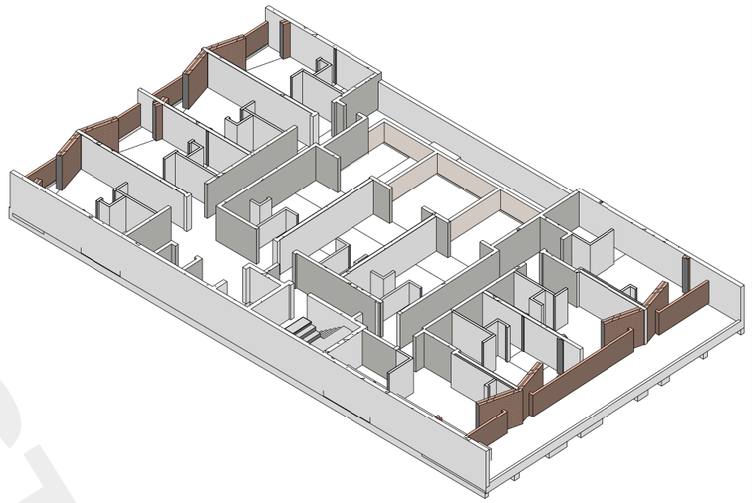


NOTES:

SUSPENDED SLAB:

A. DRAWING TO BE READ IN CONJUNCTION WITH ARCHITECTURE DRAWINGS .
B. REFER TO ARCHITECTURAL DRAWINGS FOR ALL SETOUT, LEVELS, STEPS, FOLDS & FALLS ETC.
C. REFER TO STORMWATER DRAINAGE DRAWINGS FOR LOCATION OF PUMP WELL AND SUMP PITS.
D. ALL CONCRETE CYLINDERS TO BE STORED AND CURED ON SITE PRIOR TESTING TO AS3600.
E. CONCRETE SLAB (f'c)=32 MPa WITH A SLUMP OF 80MM.
F. AGGREGATE MINIMUM SIZE 20MM.
G. ALL BRICKS WALLS TO BE ARTICULATED, EXPANSION JOINT SPACING TO BE 6000mm
H. ALL EXPOSED SLABS TO BE WATERPROOFED WITH APPROVED SYSTEMS.
I. ACOUSTIC ENGINEER TO CHECK AND VERIFY ALL FLOOR SLAB FOR ACOUSTIC REQUIREMENTS IN ACCORDANCE WITH THE BCA REGULATIONS AND ADVISE ON ANY ACOUSTIC TREATMENT NEEDED TO SATISFY THE REGULATION.
J. FOR FOLD REINFORCEMENTS REFER TO TYPICAL SECTION U.N.O.

FIRST FLOOR SLAB: FRL 120/120/120

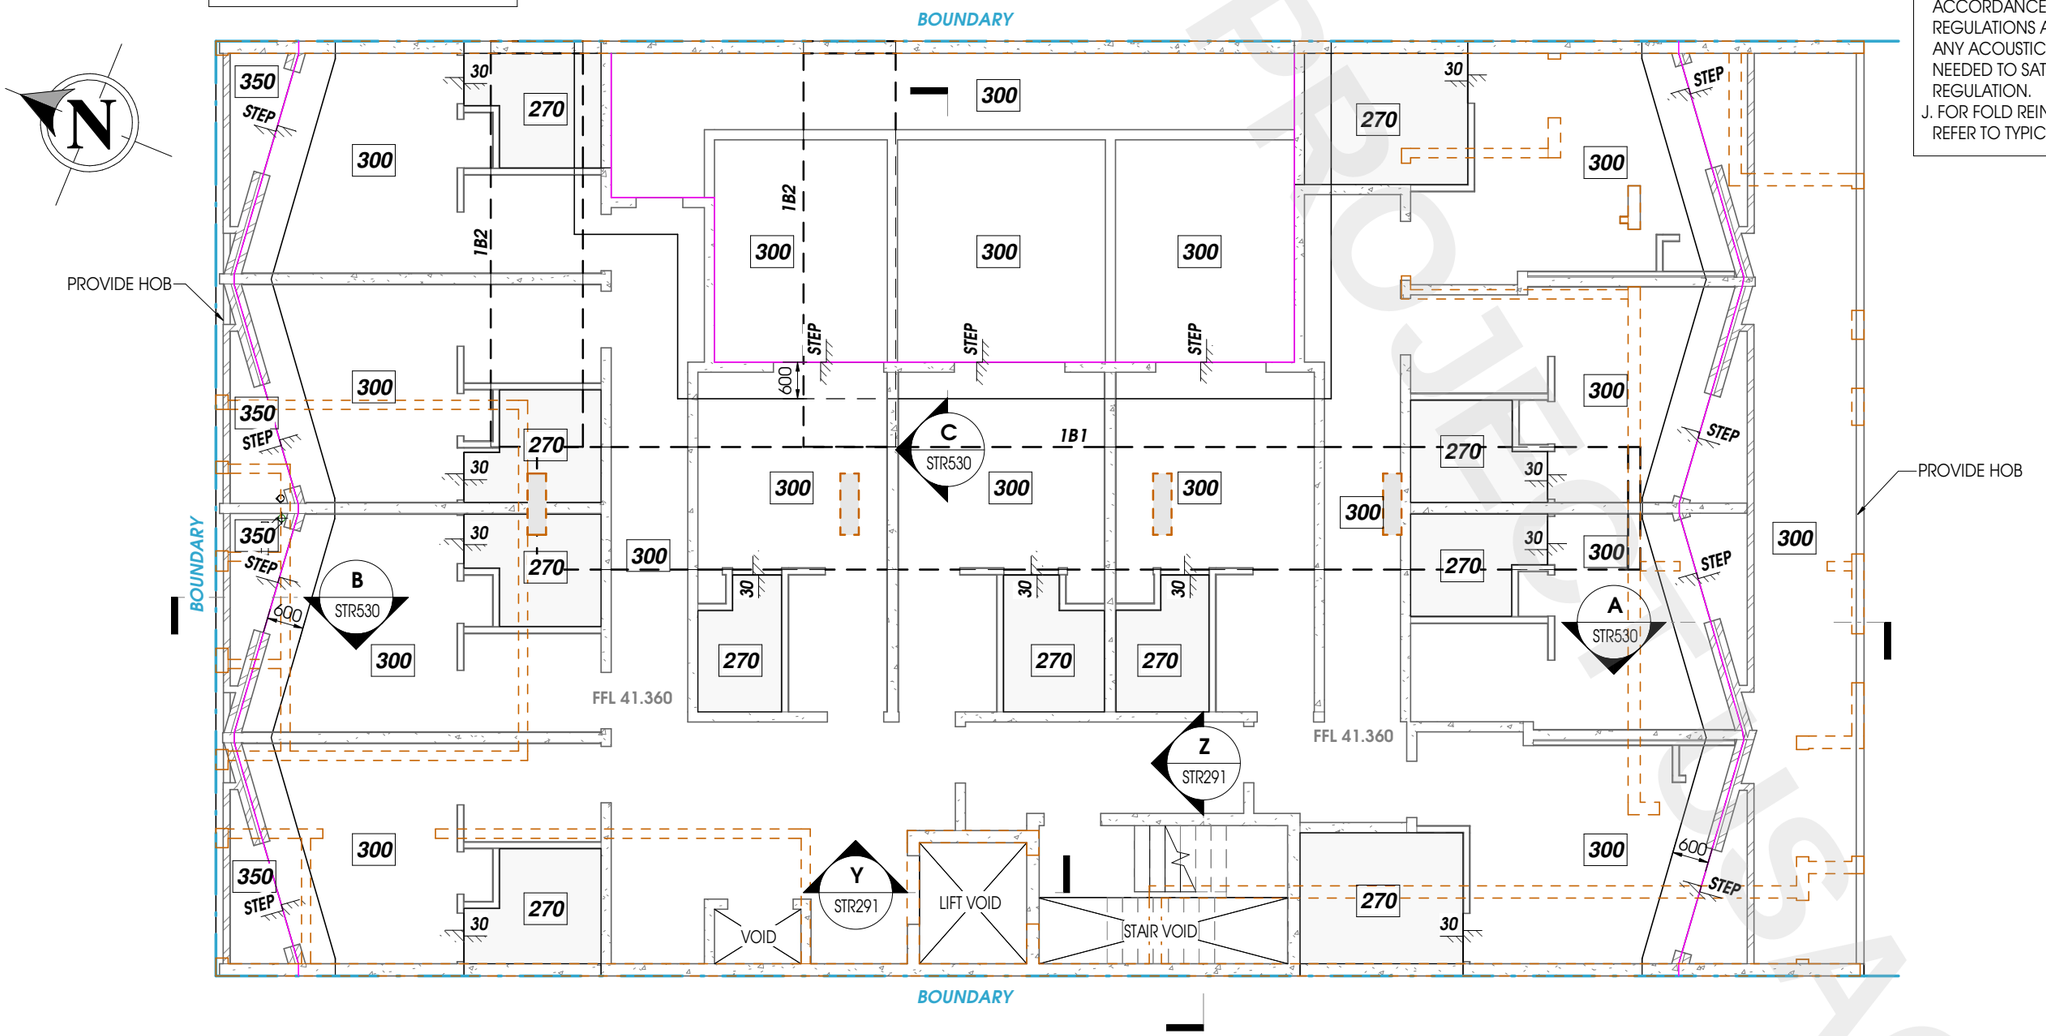

LEVEL 1 SUSPENDED CONCRETE SLAB PLAN

SCALE: 1 : 100

PRINT IN COLOUR

MODULAR ENGINEERS P/L

Structural Engineering | Civil Engineering
Stormwater Engineering | Flood Engineering
Traffic Engineering | Temporary works

ABN : 66 646 960 929
TEL. : 02 873 08473
MOB. : 04 208 98999
EMAIL :
WEBSITE :
ADDRESS :

CLIENT:

PROJECT TITLE:
MULTI DWELLING

SHEET NAME:
LEVEL 1 FLOOR PLAN

PROJECT NUMBER:
175-2026

INTERNAL REVISIONS:

ISSUE	DATE	DESCRIPTION	BY
E	10-09-26	ISSUED FOR CONSTRUCTION	D.A.
D	08-09-26	ISSUED FOR CONSTRUCTION	D.A.
C	24-08-26	ISSUED FOR PRELIMINARY	D.A.
B	21-08-26	ISSUED FOR PRELIMINARY	D.A.

AMENDMENTS

DRAWN : L.M. DATE: 17-07-26
DESIGNED : A.O. REVISION DATE:
QA CHECK : A.O. 10-09-26

APPROVED BY:

RPEQ: 28316
NPER: 5358554
DATE: 10-09-26

ISSUE TYPE:
CONSTRUCTION

SHEET NUMBER:
STR500

SHEET SIZE: **A3** REVISION: **E**

SAMPLE PROJECT A - STRUCTURAL REV E - CURRENT - RECRUITMENT ASSESSMENT ONLY

TEST PROJECT ISSUED

NOTE: THE DESIGN AND DETAILS SHOWN ON THESE DRAWINGS ARE APPLICABLE TO THIS PROJECT ONLY AND MAY NOT BE REPRODUCED IN WHOLE OR IN PART OR BE USED FOR ANY OTHER PROJECT OR PURPOSE WITHOUT THE WRITTEN PERMISSION OF WITH WHOM COPYRIGHT RESIDES.

REGULATED DESIGN RECORD

PROJECT ADDRESS:	
PROJECT TITLE:	MULTI DWELLING
CONSENT NO:	STR208 - 2023
BODY CORPORATE REG NO:	DEP0001320
DRAWING TITLE:	LEVEL 1 WALL LAYOUT PLAN
DRAWING NO:	STR501

REV	DATE DD.MM.YY	DESCRIPTION	DP FULL NAME	REG NO
E	10-09-26	ISSUED FOR CONSTRUCTIO		

LEGEND:


- DENOTES CONCRETE COLUMN/ WALL **OVER ONLY**
- DENOTES BRICK WALLS **OVER ONLY**
- DENOTES BLOCK WORK WALLS **OVER ONLY**
- DENOTES RITEK WALLS **OVER ONLY**
- DENOTES CONCRETE WALL/COLUMN **UNDER ONLY**
- DENOTES WET AREA WITH 2mm FALL
- DENOTES SLAB PENETRATION
- DENOTES STEP ON SLAB
- C00 DENOTES COLUMN MARK
- W00 DENOTES WALL MARK
- 000 DENOTES SLAB THICKNESS
- DENOTES EXTENT OF SLAB STEP

FOR STRUCTURAL NOTES REFER TO DRAWING STR00 SERIES

WALL SCHEDULE

FLOOR LEVEL	TYPE	DESCRIPTION	THK (mm)	VERT. REINF.	HORZ. REINF.	f'c
LEVEL 1	1W1	RITEK WALL	200	N12-200 E.F.	N12-200 E.F.	32 MPa
	1W2	RITEK WALL	200	N12-200 E.F.	N12-200 E.F.	32 MPa
	1W3	RITEK WALL	150	N12-200 E.F.	N12-200 E.F.	32 MPa

FIRST FLOOR SLAB: FRL 120/120/120

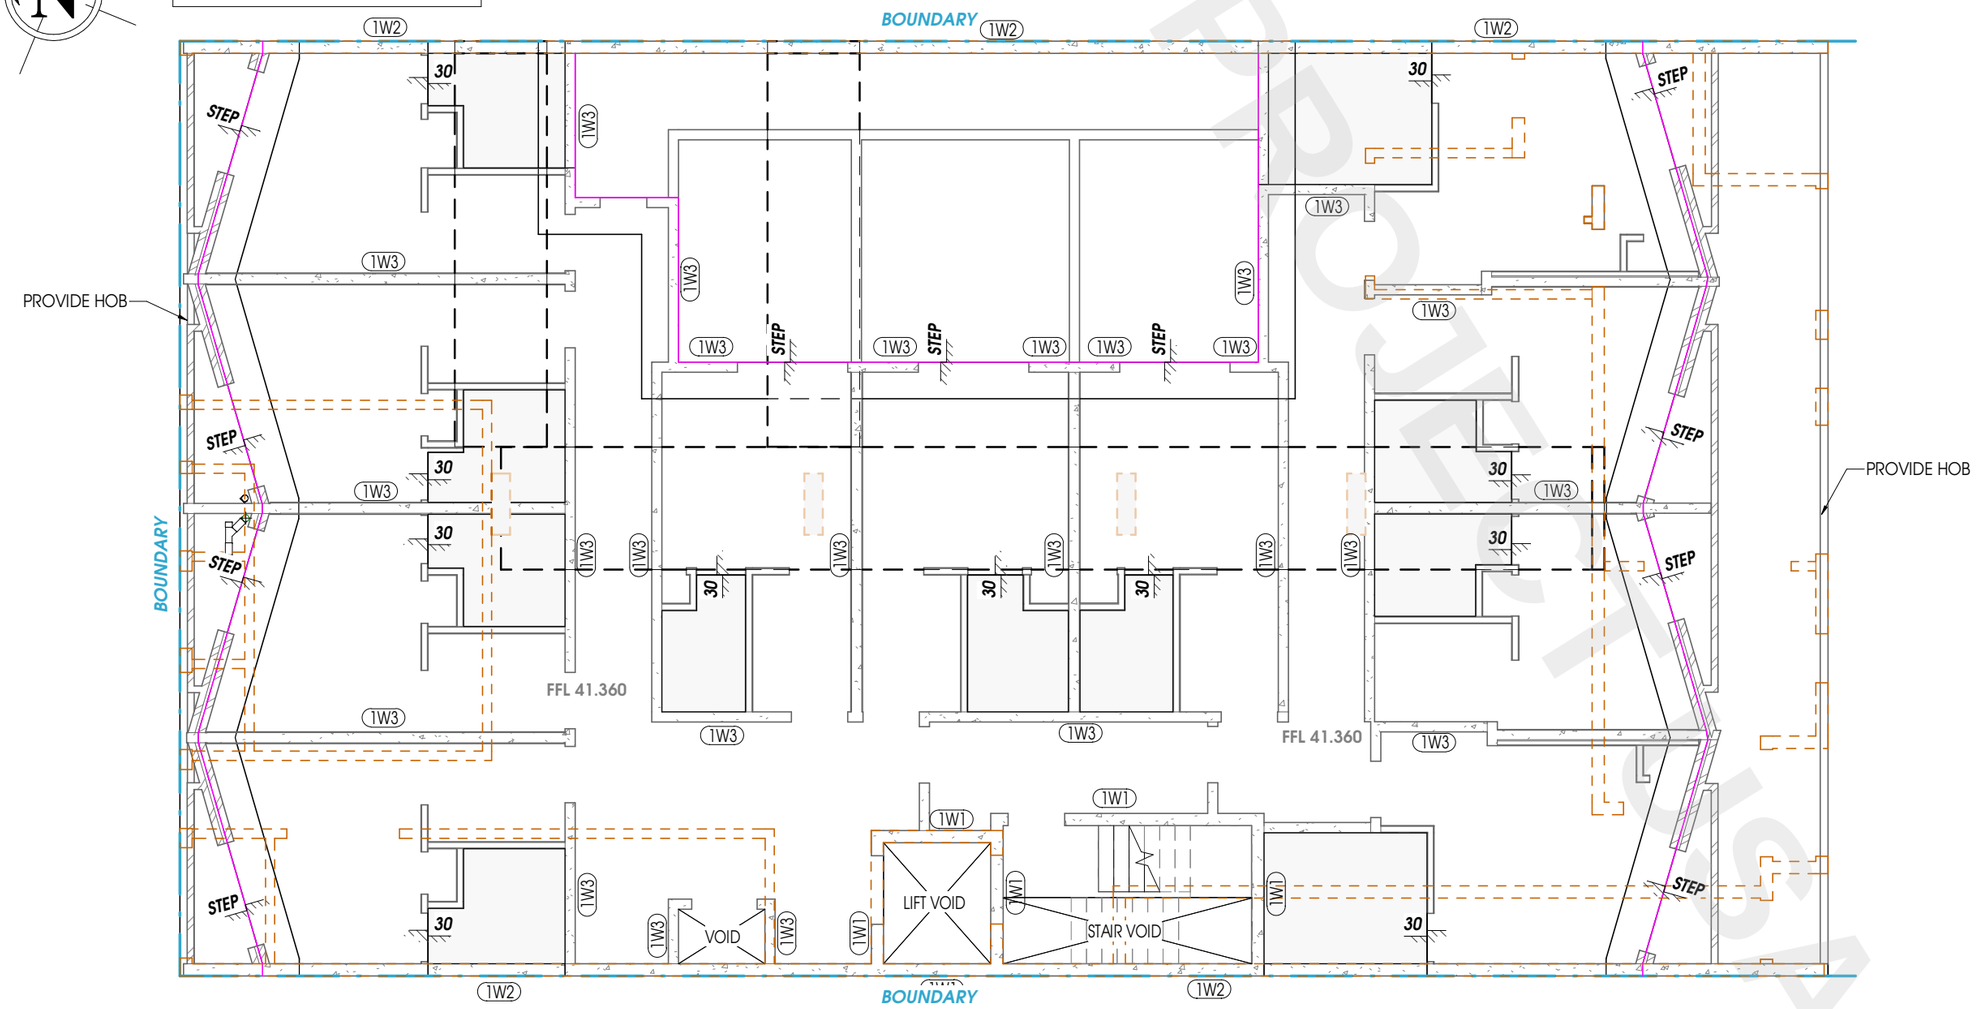

LEVEL 1 WALL LAYOUT PLAN

SCALE: 1 : 100

PRINT IN COLOUR

NOTE: THE DESIGN AND DETAILS SHOWN ON THESE DRAWINGS ARE APPLICABLE TO THIS PROJECT ONLY AND MAY NOT BE REPRODUCED IN WHOLE OR IN PART OR BE USED FOR ANY OTHER PROJECT OR PURPOSE WITHOUT THE WRITTEN PERMISSION OF WITH WHOM COPYRIGHT RESIDES.

TEST PROJECT

SAMPLE PROJECT A - STRUCTURAL REV E - CURRENT - RECRUITMENT ASSESSMENT ONLY

MODULAR ENGINEERS P/L

Structural Engineering | Civil Engineering
Stormwater Engineering | Flood Engineering
Traffic Engineering | Temporary works

ABN : 66 646 960 929
TEL. : 02 873 08473
MOB. : 04 208 98999
EMAIL :
WEBSITE :
ADDRESS :

CLIENT:

PROJECT TITLE:
MULTI DWELLING

SHEET NAME:
LEVEL 1 WALL LAYOUT PLAN

PROJECT NUMBER:
175-2026

INTERNAL REVISIONS:

ISSUE	DATE	DESCRIPTION	BY
E	10-09-26	ISSUED FOR CONSTRUCTION	D.A.
D	08-09-26	ISSUED FOR CONSTRUCTION	D.A.
C	24-08-26	ISSUED FOR PRELIMINARY	D.A.
B	21-08-26	ISSUED FOR PRELIMINARY	D.A.

AMENDMENTS

DRAWN : L.M. DATE: 17-07-26
DESIGNED : A.O. REVISION DATE:
QA CHECK : A.O. 10-09-26

APPROVED BY:

RPEQ: 28316
NPER: 5358554
DATE: 10-09-26

ISSUE TYPE:
CONSTRUCTION

SHEET NUMBER:
STR501

SHEET SIZE: **A3**
REVISION: **E**


REGULATED DESIGN RECORD

PROJECT ADDRESS:	
PROJECT TITLE:	MULTI DWELLING
CONSENT NO:	STR208 - 2023
BODY CORPORATE REG NO:	DEP0001320
DRAWING TITLE:	LEVEL 1 BOTTOM REINFORCEMENT PLAN
DRAWING NO:	STR510

REV	DATE DD.MM.YY	DESCRIPTION	DP FULL NAME	REG NO
E	10-09-26	ISSUED FOR CONSTRUCTIO		




BAR LAYING SEQUENCE

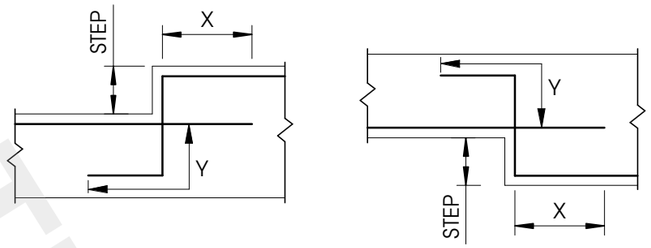

TYPICAL REINFORCEMENT LAPPING



N12-200 MAIN MESH BOTH DIRECTION TOP & BOTTOM

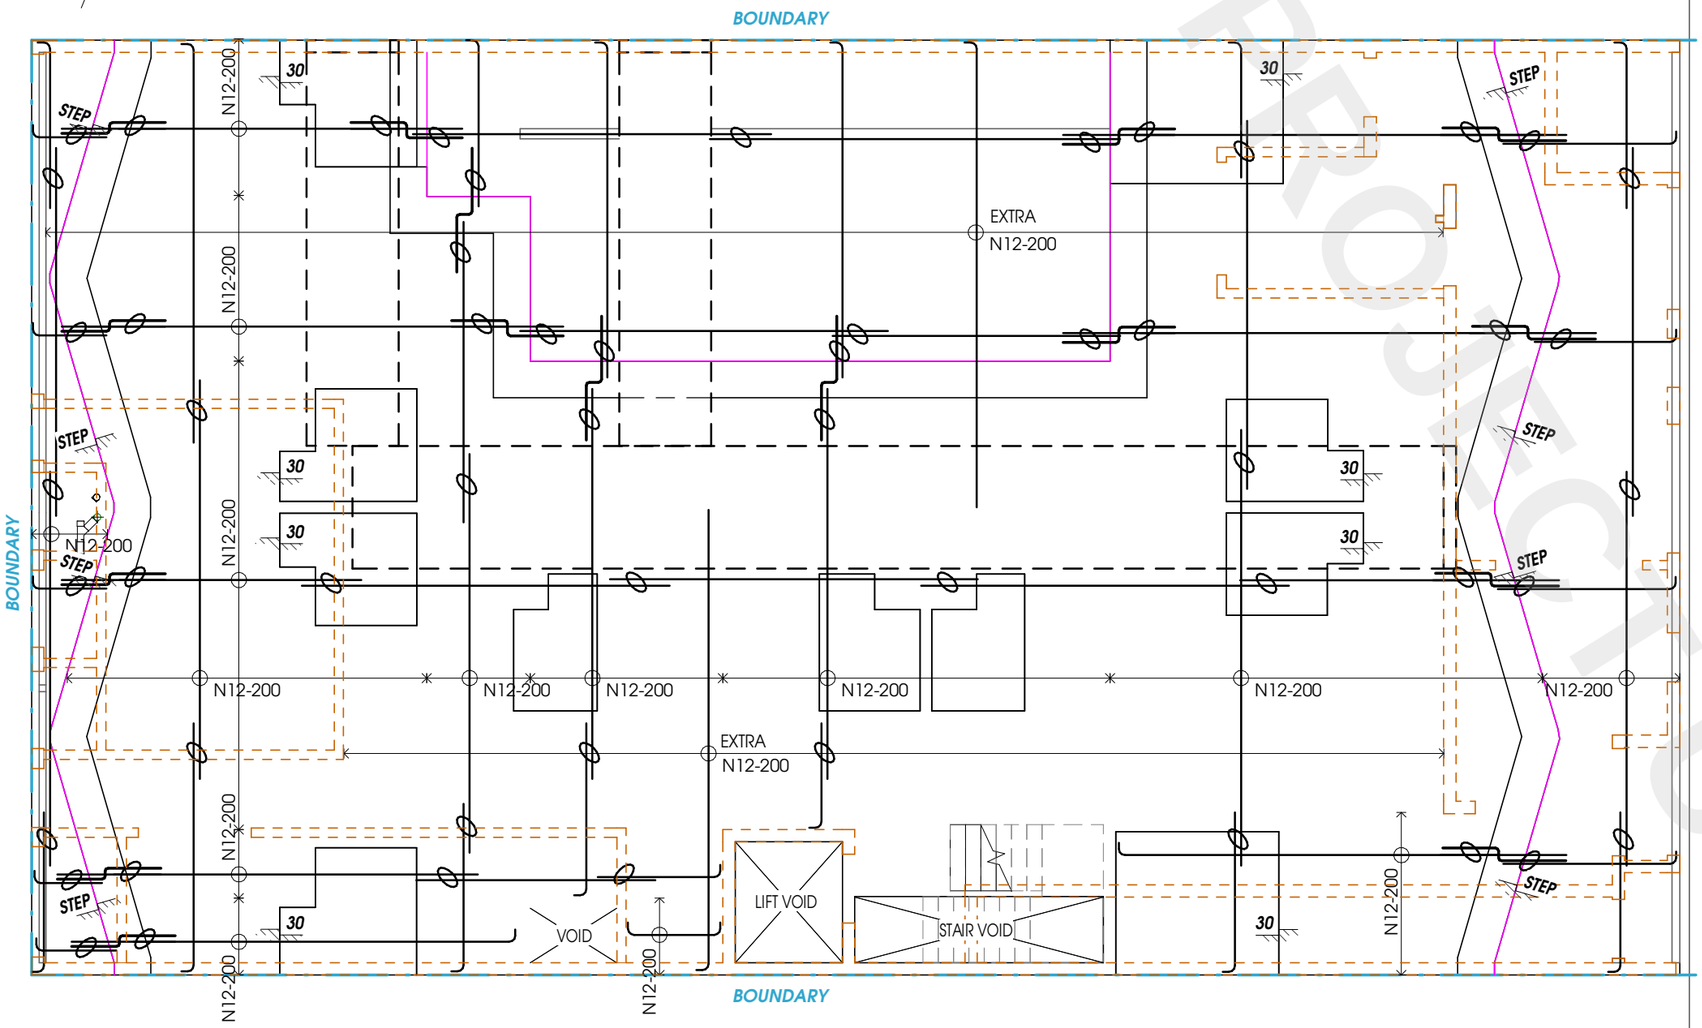


LEVEL 1 BOTTOM REINFORCEMENT PLAN

SCALE: 1 : 100


NOTES:

SUSPENDED SLAB:


A. DRAWING TO BE READ IN CONJUNCTION WITH ARCHITECTURE DRAWINGS .
B. REFER TO ARCHITECTURAL DRAWINGS FOR ALL SETOUT, LEVELS, STEPS, FOLDS & FALLS ETC.
C. REFER TO STORMWATER DRAINAGE DRAWINGS FOR LOCATION OF PUMP WELL AND SUMP PITS.
D. ALL CONCRETE CYLINDERS TO BE STORED AND CURED ON SITE PRIOR TESTING TO AS3600.
E. CONCRETE SLAB (f'c)=32 MPa WITH A SLUMP OF 80MM.
F. AGGREGATE MINIMUM SIZE 20MM.
G. ALL BRICKS WALLS TO BE ARTICULATED, EXPANSION JOINT SPACING TO BE 6000mm
H. ALL EXPOSED SLABS TO BE WATERPROOFED WITH APPROVED SYSTEMS.
I. ACOUSTIC ENGINEER TO CHECK AND VERIFY ALL FLOOR SLAB FOR ACOUSTIC REQUIREMENTS IN ACCORDANCE WITH THE BCA REGULATIONS AND ADVISE ON ANY ACOUSTIC TREATMENT NEEDED TO SATISFY THE REGULATION.
J. FOR FOLD REINFORCEMENTS REFER TO SECTION S4 U.N.O.
K. ENSURE 50mm MINIMUM SPACING BETWEEN BARS.
L. PROVIDE ALL EXTRA REINFORCEMENT AS SHOWN ON PLAN.
M. PROVIDE 3N16 TOP AND BOTTOM AT THE PERIMETER OF THE SLAB.
N. SLAB REINFORCEMENT LAYING SEQUENCE U.N.O.:

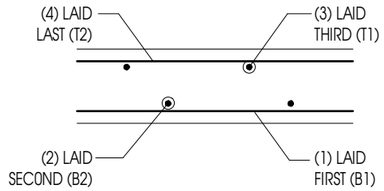

O. TYPICAL TRIMMERS AT PENETRATION/OPENING DETAIL:

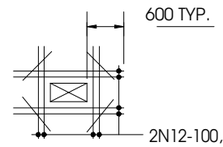

P. TYPICAL TRIMMERS AT RE-ENTRANT CORNERS:

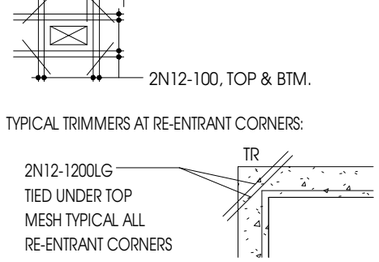

Q. PROVIDE TOP & BOTTOM BARS ON ALL WALL OPENINGS AS PER THE SCHEDULE BELOW:

LENGTH OF OPENING (m)	BOTTOM BAR	TOP BAR
1.0 - 1.8	2N16	2N16
1.8 - 2.5	2N20	2N20
2.5 - 3.5	2N24	2N24

R. PROVIDE ADEQUATE OVERLAP AT MESH JOINTS AS FOLLOWS :
- 400 MIN. LAP FOR SL82 MESH
- 500 MIN. LAP FOR SL92 MESH
- 600 MIN. LAP FOR SL102 MESH

S. PROVIDE ADEQUATE OVERLAP FOR BARS AS FOLLOWS:

BAR(X-Y)	MIN LAPPING REQUIRED
N12	500 mm
N16	800 mm
N20	1000 mm
N24	1200 mm
N28	1400 mm

MODULAR ENGINEERS P/L

Structural Engineering | Civil Engineering
Stormwater Engineering | Flood Engineering
Traffic Engineering | Temporary works

ABN : 66 646 960 929
TEL. : 02 873 08473
MOB. : 04 208 98999
EMAIL :
WEBSITE :
ADDRESS :

CLIENT:

PROJECT TITLE:
MULTI DWELLING

SHEET NAME:
LEVEL 1 BOTTOM REINFORCEMENT PLAN

PROJECT NUMBER:
175-2026

INTERNAL REVISIONS:

ISSUE	DATE	DESCRIPTION	BY
E	10-09-26	ISSUED FOR CONSTRUCTION	D.A.
D	08-09-26	ISSUED FOR CONSTRUCTION	D.A.
C	24-08-26	ISSUED FOR PRELIMINARY	D.A.
B	21-08-26	ISSUED FOR PRELIMINARY	D.A.

AMENDMENTS

DRAWN : L.M. DATE: 17-07-26
DESIGNED : A.O. REVISION DATE:
QA CHECK : A.O. 10-09-26
APPROVED BY:

RPEQ: 28316
NPER: 5358554
DATE: 10-09-26

ISSUE TYPE:
CONSTRUCTION

SHEET NUMBER:
STR510

SHEET SIZE: **A3**
REVISION: **E**

PRINT IN COLOUR

SAMPLE PROJECT A - STRUCTURAL REVIEW - CURRENT - RECRUITMENT ASSESSMENT ONLY

TEST PROJECT NOT FOR CONSTRUCTION

NOTE: THE DESIGN AND DETAILS SHOWN ON THESE DRAWINGS ARE APPLICABLE TO THIS PROJECT ONLY AND MAY NOT BE REPRODUCED IN WHOLE OR IN PART OR BE USED FOR ANY OTHER PROJECT OR PURPOSE WITHOUT THE WRITTEN PERMISSION OF WITH WHOM COPYRIGHT RESIDES.


REGULATED DESIGN RECORD

PROJECT ADDRESS:	
PROJECT TITLE:	MULTI DWELLING
CONSENT NO:	STR208 - 2023
BODY CORPORATE REG NO:	DEP0001320
DRAWING TITLE:	LEVEL 1 TOP REINFORCEMENT PLAN
DRAWING NO:	STR511


REV	DATE DD.MM.YY	DESCRIPTION	DP FULL NAME	REG NO
E	10-09-26	ISSUED FOR CONSTRUCTIO		



BAR LAYING SEQUENCE

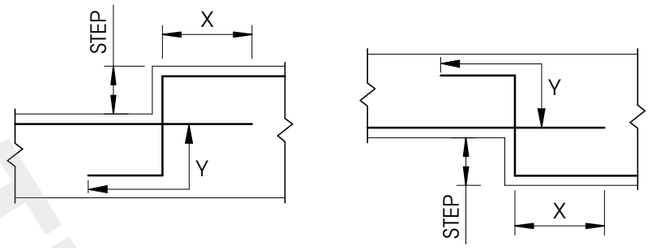

TYPICAL REINFORCEMENT LAPPING

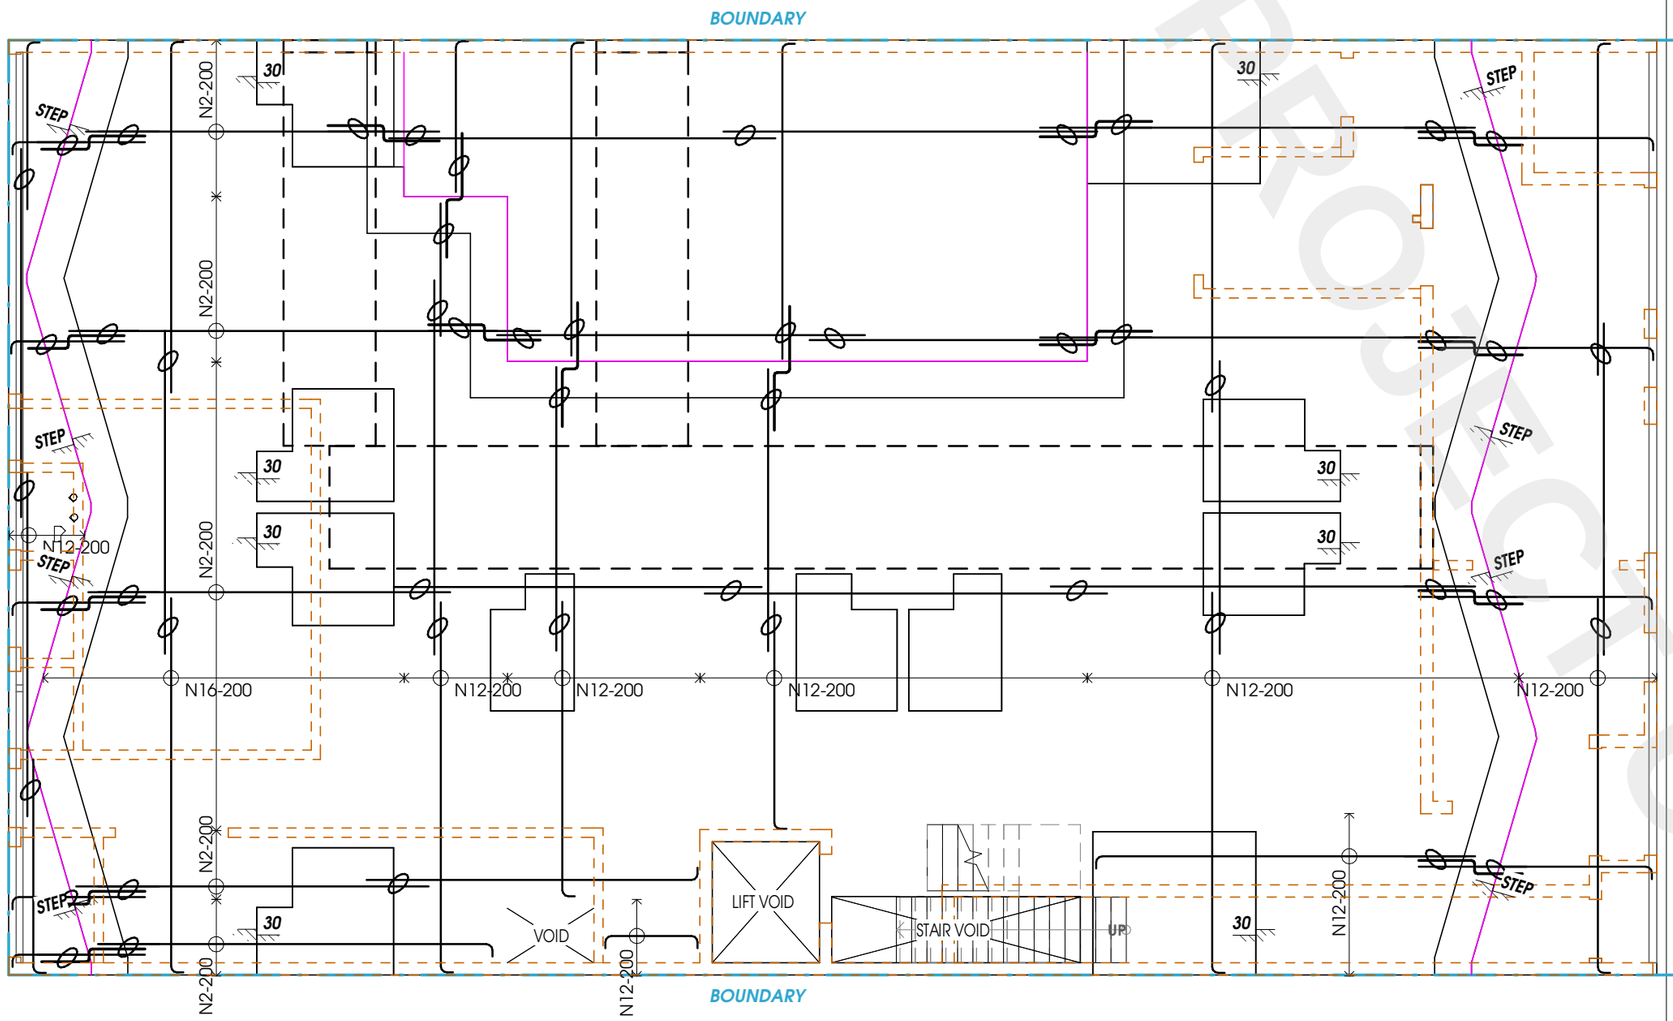


LEVEL 1 TOP REINFORCEMENT PLAN

SCALE: 1 : 100


NOTES:

SUSPENDED SLAB:


A. DRAWING TO BE READ IN CONJUNCTION WITH ARCHITECTURE DRAWINGS .
B. REFER TO ARCHITECTURAL DRAWINGS FOR ALL SETOUT, LEVELS, STEPS, FOLDS & FALLS ETC.
C. REFER TO STORMWATER DRAINAGE DRAWINGS FOR LOCATION OF PUMP WELL AND SUMP PITS.
D. ALL CONCRETE CYLINDERS TO BE STORED AND CURED ON SITE PRIOR TESTING TO AS3600.
E. CONCRETE SLAB (f'c)=32 MPa WITH A SLUMP OF 80MM.
F. AGGREGATE MINIMUM SIZE 20MM.
G. ALL BRICKS WALLS TO BE ARTICULATED, EXPANSION JOINT SPACING TO BE 6000mm
H. ALL EXPOSED SLABS TO BE WATERPROOFED WITH APPROVED SYSTEMS.
I. ACOUSTIC ENGINEER TO CHECK AND VERIFY ALL FLOOR SLAB FOR ACOUSTIC REQUIREMENTS IN ACCORDANCE WITH THE BCA REGULATIONS AND ADVISE ON ANY ACOUSTIC TREATMENT NEEDED TO SATISFY THE REGULATION.
J. FOR FOLD REINFORCEMENTS REFER TO SECTION S4 U.N.O.
K. ENSURE 50mm MINIMUM SPACING BETWEEN BARS.
L. PROVIDE ALL EXTRA REINFORCEMENT AS SHOWN ON PLAN.
M. PROVIDE 3N16 TOP AND BOTTOM AT THE PERIMETER OF THE SLAB.
N. SLAB REINFORCEMENT LAYING SEQUENCE U.N.O.:

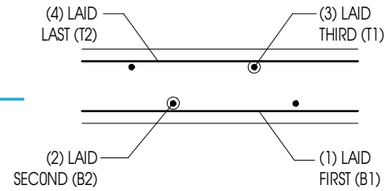

O. TYPICAL TRIMMERS AT PENETRATION/OPENING DETAIL:

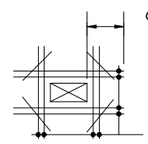

P. TYPICAL TRIMMERS AT RE-ENTRANT CORNERS:

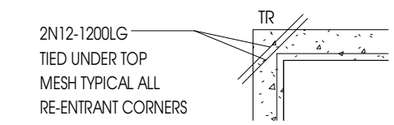

Q. PROVIDE TOP & BOTTOM BARS ON ALL WALL OPENINGS AS PER THE SCHEDULE BELOW:

LENGTH OF OPENING (m)	BOTTOM BAR	TOP BAR
1.0 - 1.8	2N16	2N16
1.8 - 2.5	2N20	2N20
2.5 - 3.5	2N24	2N24

R. PROVIDE ADEQUATE OVERLAP AT MESH JOINTS AS FOLLOWS :
- 400 MIN. LAP FOR SL82 MESH
- 500 MIN. LAP FOR SL92 MESH
- 600 MIN. LAP FOR SL102 MESH

S. PROVIDE ADEQUATE OVERLAP FOR BARS AS FOLLOWS:

BAR(X-Y)	MIN LAPPING REQUIRED
N12	500 mm
N16	800 mm
N20	1000 mm
N24	1200 mm
N28	1400 mm

MODULAR ENGINEERS P/L

Structural Engineering | Civil Engineering
Stormwater Engineering | Flood Engineering
Traffic Engineering | Temporary works

ABN : 66 646 960 929
TEL. : 02 873 08473
MOB. : 04 208 98999
EMAIL :
WEBSITE :
ADDRESS :

CLIENT:

PROJECT TITLE:
MULTI DWELLING

SHEET NAME:
LEVEL 1 TOP REINFORCEMENT PLAN

PROJECT NUMBER:
175-2026

INTERNAL REVISIONS:

ISSUE	DATE	DESCRIPTION	BY
E	10-09-26	ISSUED FOR CONSTRUCTION	D.A.
D	08-09-26	ISSUED FOR CONSTRUCTION	D.A.
C	24-08-26	ISSUED FOR PRELIMINARY	D.A.
B	21-08-26	ISSUED FOR PRELIMINARY	D.A.

AMENDMENTS

DRAWN : L.M. DATE: 17-07-26
DESIGNED : A.O. REVISION DATE:
QA CHECK : A.O. 10-09-26
APPROVED BY:

RPEQ: 28316
NPER: 5358554
DATE: 10-09-26

ISSUE TYPE:
CONSTRUCTION

SHEET NUMBER:
STR511

SHEET SIZE: **A3** REVISION: **E**

PRINT IN COLOUR

SAMPLE PROJECT A - STRUCTURAL REVE - CURRENT - RECRUITMENT ASSESSMENT ONLY

TEST PRO


NOT FOR CONSTRUCTION

NOTE: THE DESIGN AND DETAILS SHOWN ON THESE DRAWINGS ARE APPLICABLE TO THIS PROJECT ONLY AND MAY NOT BE REPRODUCED IN WHOLE OR IN PART OR BE USED FOR ANY OTHER PROJECT OR PURPOSE WITHOUT THE WRITTEN PERMISSION OF WITH WHOM COPYRIGHT RESIDES.

REGULATED DESIGN RECORD

PROJECT ADDRESS:			
PROJECT TITLE:	MULTI DWELLING		
CONSENT NO:	STR208 - 2023	BODY CORPORATE REG NO:	DEP0001320
DRAWING TITLE:	LEVEL 1 LOADING PLAN	DRAWING NO:	STR520

REV	DATE DD.MM.YY	DESCRIPTION	DP FULL NAME	REG NO
E	10-09-26	ISSUED FOR CONSTRUCTIO		

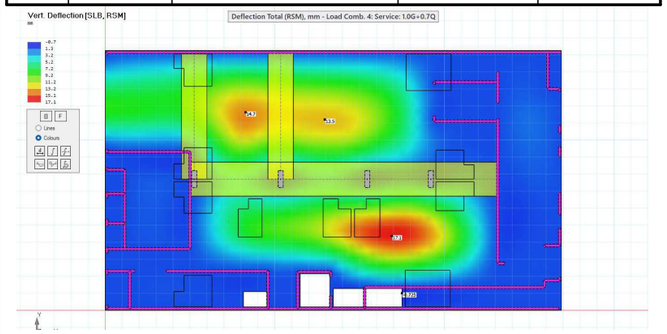


LOADING TABLE
WHERE APPLICABLE

MARK	COLOUR	AREA	SUPERIMPOSED DEAD LOAD	LIVE LOAD
1		RESIDENTIAL	1.5 kPa	1.5 kPa
2		PARKING	0.5 kPa EXC. FALLS AND GRADING	2.5 kPa
3		STORAGE	0.5 kPa	5.0 kPa
4		CORRIDOR / STAIR	1.5 kPa	4.0 kPa
5		LOBBY	1.5 kPa	4.0 kPa
6		BALCONY	1.5 kPa	2.0 kPa
7		MECH ROOM,FAN ROOM	1.5 kPa	5.0 kPa
8		COMMON AREA	1.5 kPa	4.0 kPa
9		LIGHT WEIGHT ROOF	0.5 kPa	0.5 kPa

LOADING TABLE
WHERE APPLICABLE

MARK	COLOUR	AREA	SUPERIMPOSED DEAD LOAD	LIVE LOAD
10		WASTE ROOM	0.5 kPa	5.0 kPa
11		RETAILS	1.5 kPa	4.0 kPa
12		ROOF (NON-TRAFFICABLE)	2.0 kPa	1.5 kPa
13		LANDSCAPE 400mm SOIL MAX.	4.0 kPa	1.5 kPa
14		LANDSCAPE 1000mm SOIL MAX.	10.0 kPa	1.5 kPa
15		SUBSTATION	1.0 kPa	2.0 kPa
16		LOADING DECK	1.0 kPa	10.0 kPa
17		PEBBLES	4.0 kPa	1.5 kPa
18		OSD TANK/ WATER STORAGE TANK	10.0 kPa FOR EVERY METRE HEIGHT OF WATER	

DEFLECTION NOTES (LONG-TERM)
- LONG-TERM DEFLECTION IS BASED ON DL + 0.3LL FOR SUSTAINED LOADS.
- CREEP FACTOR Λ = 2.0 TO 3.0 APPLIED PER AS3600.
- TOTAL DEFLECTION: Δ TOTAL=Δ IMMEDIATE + Λ × Δ SUSTAINED
- IMMEDIATE DEFLECTION: DL + LL
- LONG-TERM DEFLECTION: DL + 0.3LL × Λ

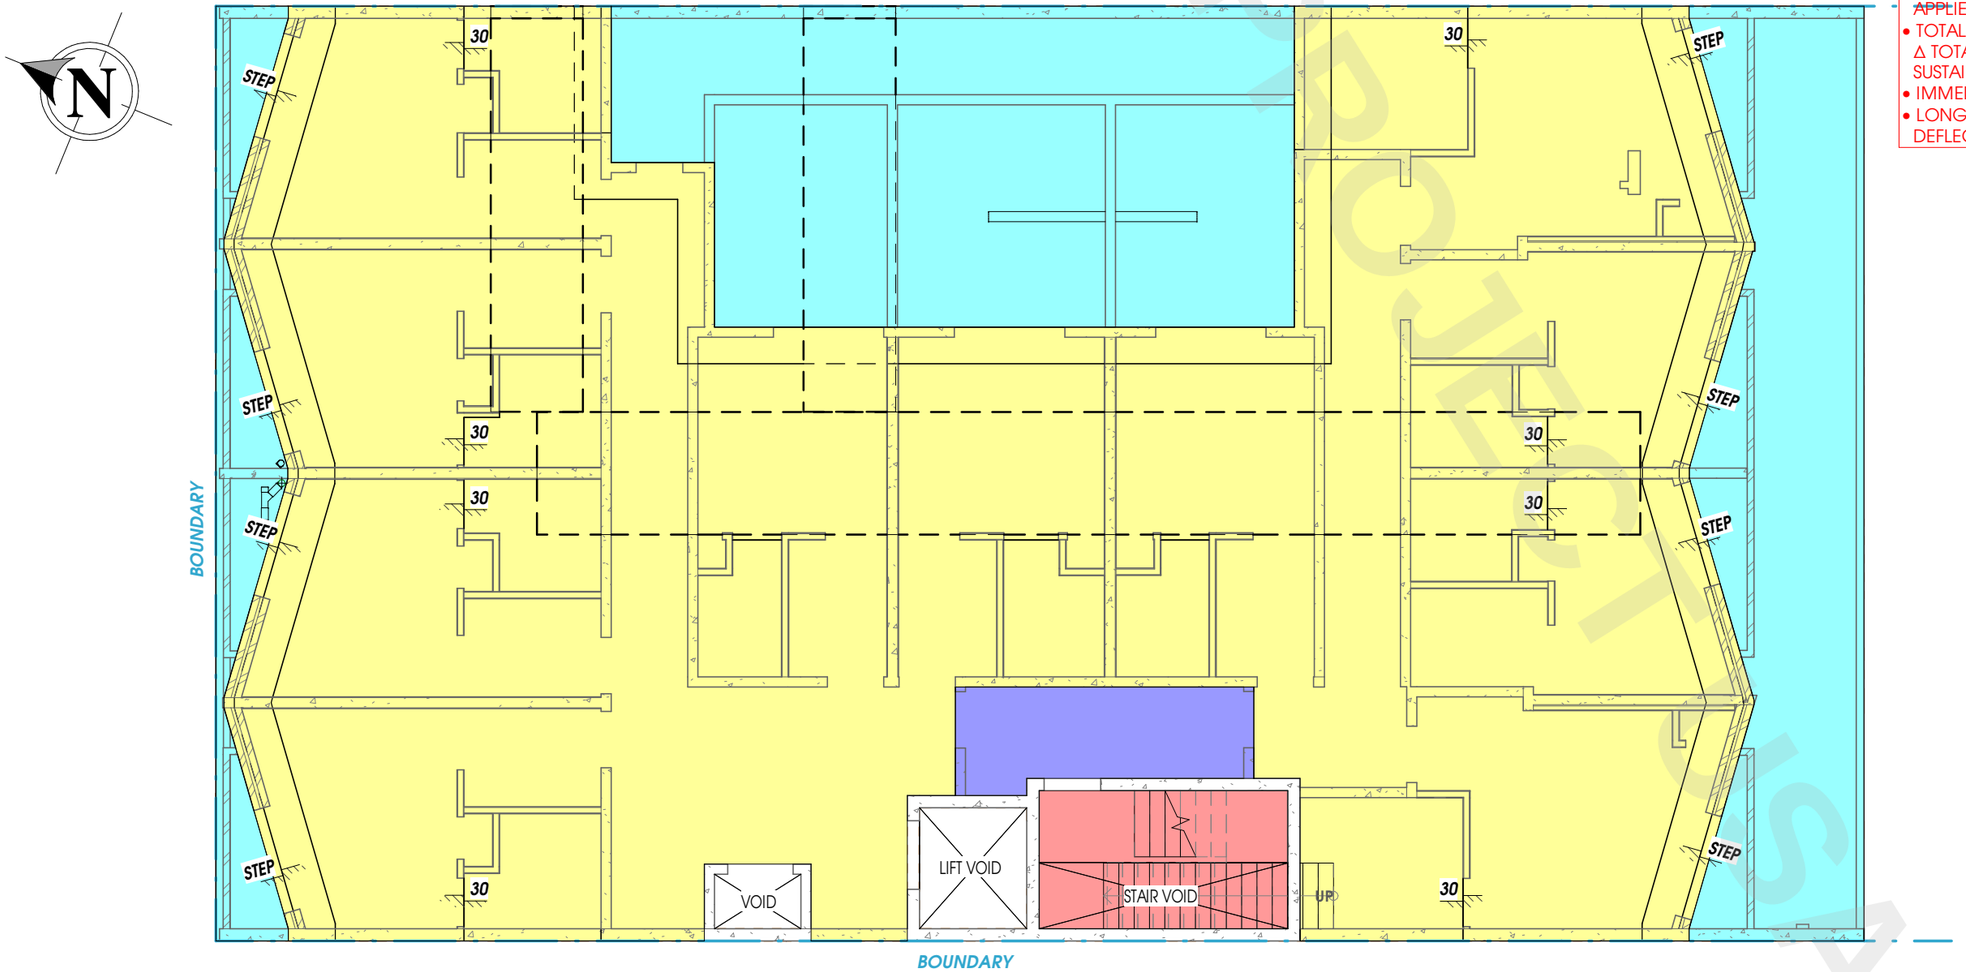

LEVEL 1 LOADING PLAN
SCALE: 1 : 100

PRINT IN COLOUR

MODULAR ENGINEERS P/L
Structural Engineering | Civil Engineering
Stormwater Engineering | Flood Engineering
Traffic Engineering | Temporary works
ABN : 66 646 960 929
TEL. : 02 873 08473
MOB. : 04 208 98999
EMAIL :
WEBSITE :
ADDRESS :

CLIENT:

PROJECT TITLE:
MULTI DWELLING

SHEET NAME:
LEVEL 1 LOADING PLAN

PROJECT NUMBER:
175-2026

INTERNAL REVISIONS:

ISSUE	DATE	DESCRIPTION	BY
E	10-09-26	ISSUED FOR CONSTRUCTION	D.A.
D	08-09-26	ISSUED FOR CONSTRUCTION	D.A.
C	24-08-26	ISSUED FOR PRELIMINARY	D.A.
B	21-08-26	ISSUED FOR PRELIMINARY	D.A.

AMENDMENTS

DRAWN : L.M. DATE: 17-07-26
DESIGNED : A.O. REVISION DATE:
QA CHECK : A.O. 10-09-26

APPROVED BY:

RPEQ: 28316
NPER: 5358554
DATE: 10-09-26

ISSUE TYPE:
CONSTRUCTION

SHEET NUMBER:
STR520


SHEET SIZE: **A3**
REVISION: **E**

SAMPLE PROJECT A - STRUCTURAL REVIEW - CURRENT - RECRUITMENT ASSESSMENT ONLY
TEST PROJECT ISSUE
NOTE: THE DESIGN AND DETAILS SHOWN ON THESE DRAWINGS ARE APPLICABLE TO THIS PROJECT ONLY AND MAY NOT BE REPRODUCED IN WHOLE OR IN PART OR BE USED FOR ANY OTHER PROJECT OR PURPOSE WITHOUT THE WRITTEN PERMISSION OF WITH WHOM COPYRIGHT RESIDES.


REGULATED DESIGN RECORD

PROJECT ADDRESS:			
PROJECT TITLE:	MULTI DWELLING		
CONSENT NO:	STR208 - 2023	BODY CORPORATE REG NO:	DEP0001320
DRAWING TITLE:	SECTION AND DETAILS	DRAWING NO:	STR530


REV	DATE DD.MM.YY	DESCRIPTION	DP FULL NAME	REG NO
E	10-09-26	ISSUED FOR CONSTRUCTIO		

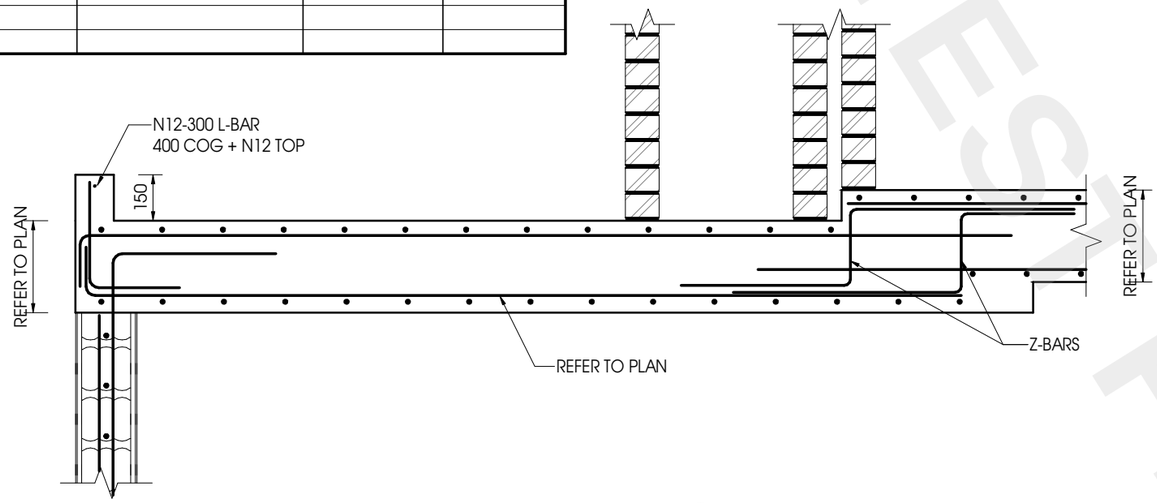

SECTION A
NOT TO SCALE STR500

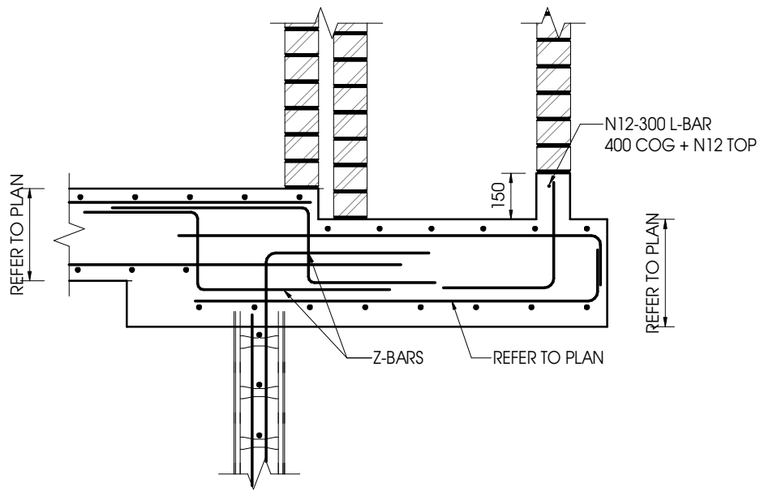

SECTION B
NOT TO SCALE STR500

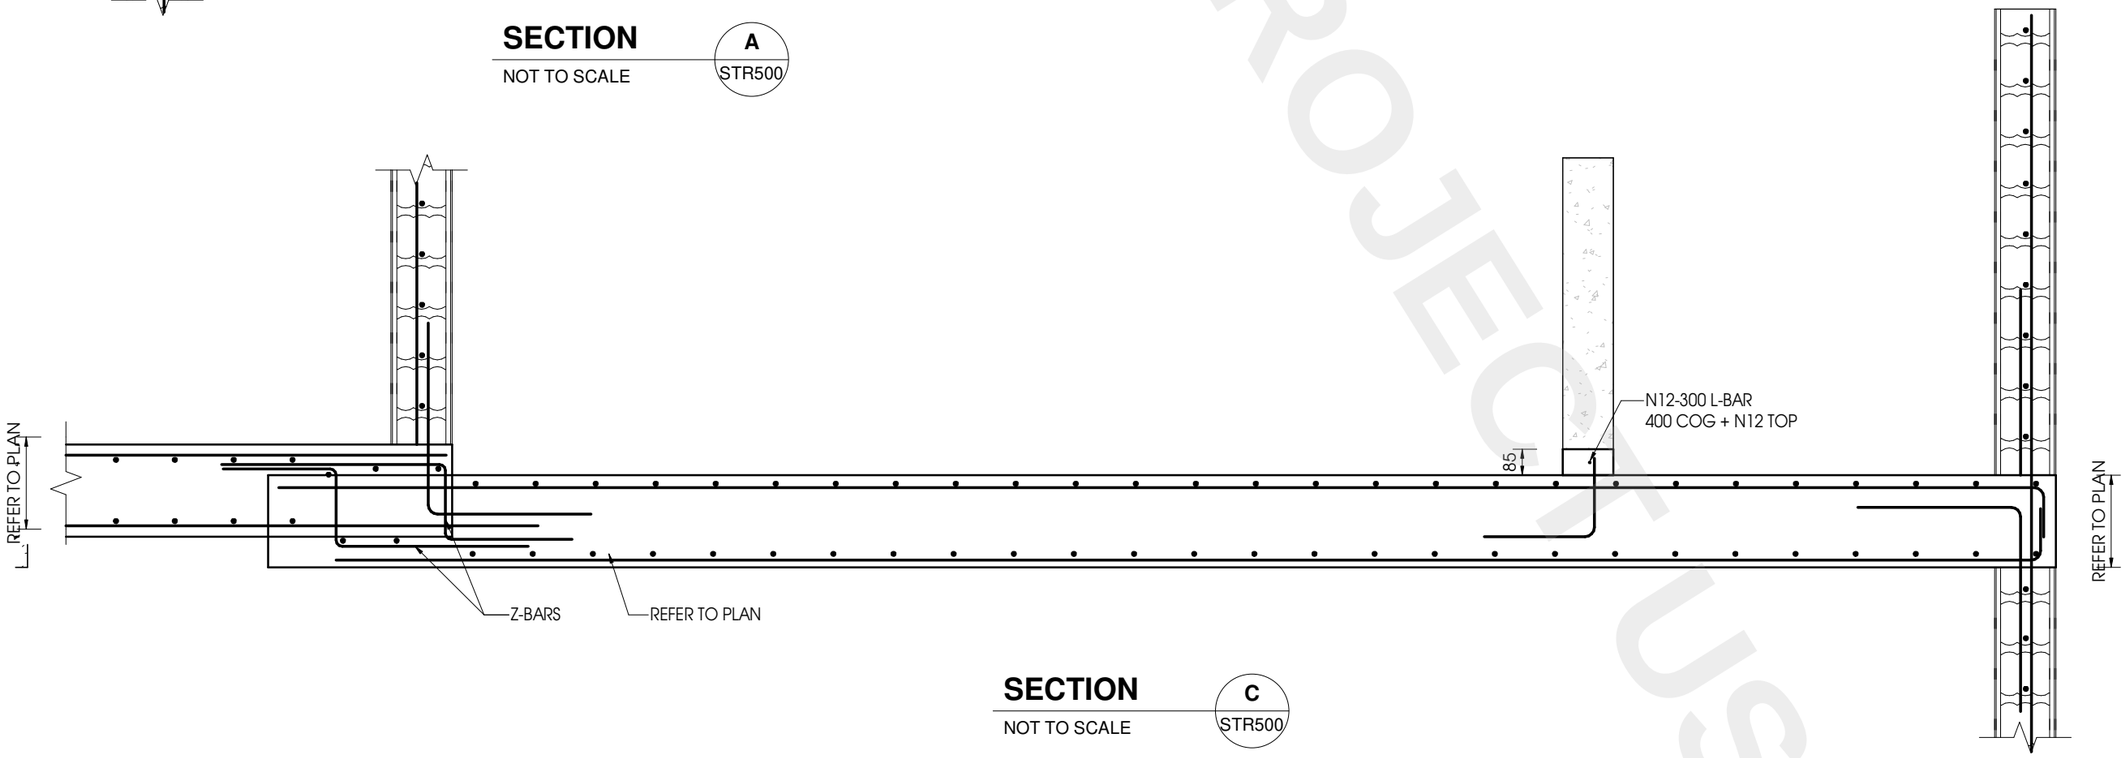

SECTION C
NOT TO SCALE STR500

TEST PROJECT
PROJECT NOT FOR USE

MODULAR ENGINEERS P/L
Structural Engineering | Civil Engineering
Stormwater Engineering | Flood Engineering
Traffic Engineering | Temporary works
ABN : 66 646 960 929
TEL. : 02 873 08473
MOB. : 04 208 98999
EMAIL :
WEBSITE :
ADDRESS :

CLIENT:

PROJECT TITLE:
MULTI DWELLING

SHEET NAME:
SECTION AND DETAILS

PROJECT NUMBER:
175-2026

INTERNAL REVISIONS:

ISSUE	DATE	DESCRIPTION	BY
E	10-09-26	ISSUED FOR CONSTRUCTION	D.A.
D	08-09-26	ISSUED FOR CONSTRUCTION	D.A.
C	24-08-26	ISSUED FOR PRELIMINARY	D.A.
B	21-08-26	ISSUED FOR PRELIMINARY	D.A.
AMENDMENTS			

DRAWN : L.M. DATE: 17-07-26
DESIGNED : A.O. REVISION DATE:
QA CHECK : A.O. 10-09-26
APPROVED BY:

RPEQ: 28316
NPER: 5358554
DATE: 10-09-26

ISSUE TYPE:
CONSTRUCTION

SHEET NUMBER:
STR530

SHEET SIZE: **A3** REVISION: **E**

PRINT IN COLOUR


SAMPLE PROJECT A - STRUCTURAL REV E - CURRENT - RECRUITMENT ASSESSMENT ONLY

NOTE: THE DESIGN AND DETAILS SHOWN ON THESE DRAWINGS ARE APPLICABLE TO THIS PROJECT ONLY AND MAY NOT BE REPRODUCED IN WHOLE OR IN PART OR BE USED FOR ANY OTHER PROJECT OR PURPOSE WITHOUT THE WRITTEN PERMISSION OF WITH WHOM COPYRIGHT RESIDES.


REGULATED DESIGN RECORD

PROJECT ADDRESS:			
PROJECT TITLE:	MULTI DWELLING		
CONSENT NO:	STR208 - 2023	BODY CORPORATE REG NO:	DEP0001320
DRAWING TITLE:	SECTION AND DETAILS	DRAWING NO:	STR540


REV	DATE DD.MM.YY	DESCRIPTION	DP FULL NAME	REG NO
E	10-09-26	ISSUED FOR CONSTRUCTIO		

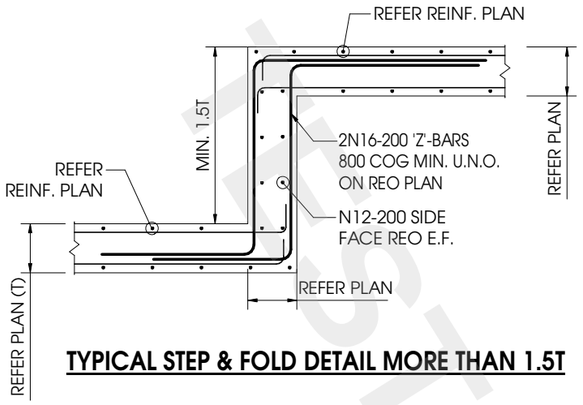


TYPICAL STEP & FOLD DETAIL MORE THAN 1.5T

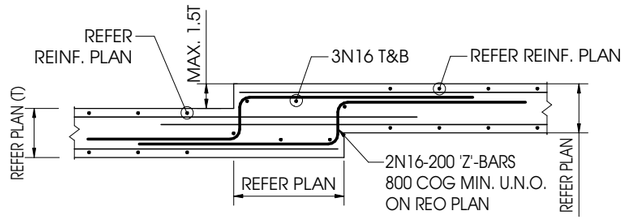


TYPICAL STEP & FOLD DETAIL LESS THAN 1.5T

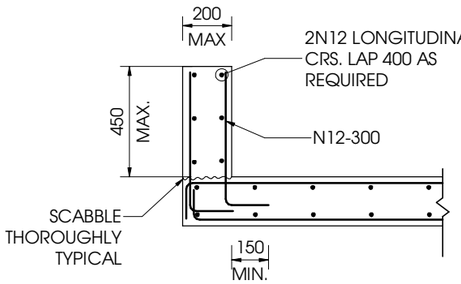

TYPICAL BALCONY HOB

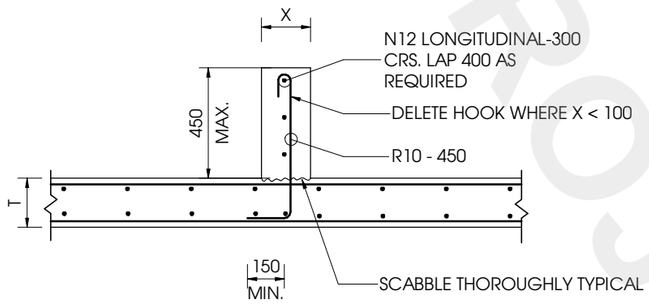


X = OR < 150

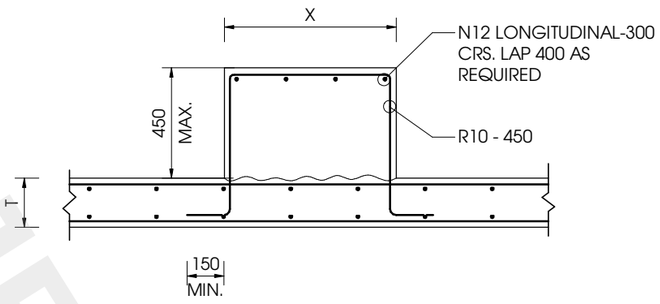


X = 451 TO 750

NOTES:

1. DETAILS APPLY UNLESS SHOWN OTHERWISE ON THE DRAWINGS
2. 'T' REFERS TO THE SLAB THICKNESS
3. 'X' REFERS TO THE PLINTH OR HOB WIDTH
4. FOR PLINTHS OR HOBS OTHER THAN SHOWN ON THESE DETAILS REFER TO SPECIFIC DETAILS ON THE DRAWINGS

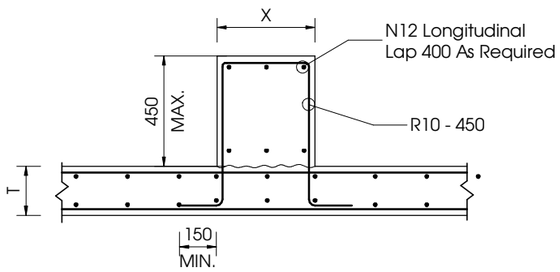

X = 150 TO 451

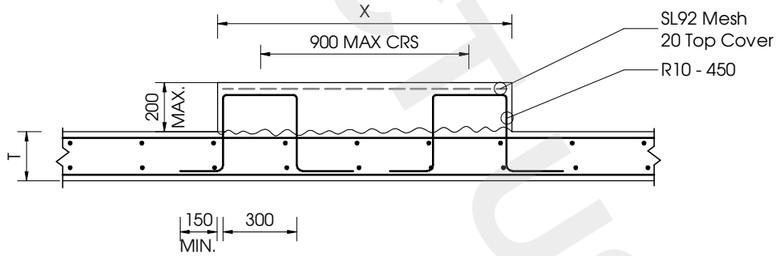

X = 750 TO 1200 MAX.

PLINTH AND HOB DETAILS

SCALE 1:20

TEST PROJECT USAGE ONLY

MODULAR ENGINEERS P/L
Structural Engineering | Civil Engineering
Stormwater Engineering | Flood Engineering
Traffic Engineering | Temporary works
ABN : 66 646 960 929
TEL. : 02 873 08473
MOB. : 04 208 98999
EMAIL :
WEBSITE :
ADDRESS :

CLIENT:

PROJECT TITLE:
MULTI DWELLING

SHEET NAME:
SECTION AND DETAILS

PROJECT NUMBER:
175-2026

INTERNAL REVISIONS:

ISSUE	DATE	DESCRIPTION	BY
E	10-09-26	ISSUED FOR CONSTRUCTION	D.A.
D	08-09-26	ISSUED FOR CONSTRUCTION	D.A.
C	24-08-26	ISSUED FOR PRELIMINARY	D.A.
B	21-08-26	ISSUED FOR PRELIMINARY	D.A.

AMENDMENTS

DRAWN : L.M. DATE: 17-07-26
DESIGNED : A.O. REVISION DATE:
QA CHECK : A.O. 10-09-26

APPROVED BY:

RPEQ: 28316
NPER: 5358554
DATE: 10-09-26

ISSUE TYPE:
CONSTRUCTION

SHEET NUMBER:
STR540

SHEET SIZE: **A3** REVISION: **E**

PRINT IN COLOUR

SAMPLE PROJECT A - STRUCTURAL REV E - CURRENT - RECRUITMENT ASSESSMENT ONLY

NOTE: THE DESIGN AND DETAILS SHOWN ON THESE DRAWINGS ARE APPLICABLE TO THIS PROJECT ONLY AND MAY NOT BE REPRODUCED IN WHOLE OR IN PART OR BE USED FOR ANY OTHER PROJECT OR PURPOSE WITHOUT THE WRITTEN PERMISSION OF WITH WHOM COPYRIGHT RESIDES.

REGULATED DESIGN RECORD


PROJECT ADDRESS:	
PROJECT TITLE:	MULTI DWELLING
CONSENT NO:	STR208 - 2023
BODY CORPORATE REG NO:	DEP0001320
DRAWING TITLE:	LEVEL 2 FLOOR PLAN
DRAWING NO:	STR600

REV	DATE DD.MM.YY	DESCRIPTION	DP FULL NAME	REG NO
E	10-09-26	ISSUED FOR CONSTRUCTIO		

LEGEND:

- DENOTES CONCRETE COLUMN/ WALL **OVER ONLY**
- DENOTES BRICK WALLS **OVER ONLY**
- DENOTES BLOCK WORK WALLS **OVER ONLY**
- DENOTES RITEK WALLS **OVER ONLY**
- DENOTES CONCRETE WALL/COLUMN **UNDER ONLY**
- DENOTES WET AREA WITH 2mm FALL
- DENOTES SLAB PENETRATION
- DENOTES STEP ON SLAB
- C00 DENOTES COLUMN MARK
- W00 DENOTES WALL MARK
- 000 DENOTES SLAB THICKNESS
- DENOTES EXTENT OF SLAB STEP

FOR STRUCTURAL NOTES REFER TO DRAWING STR00 SERIES

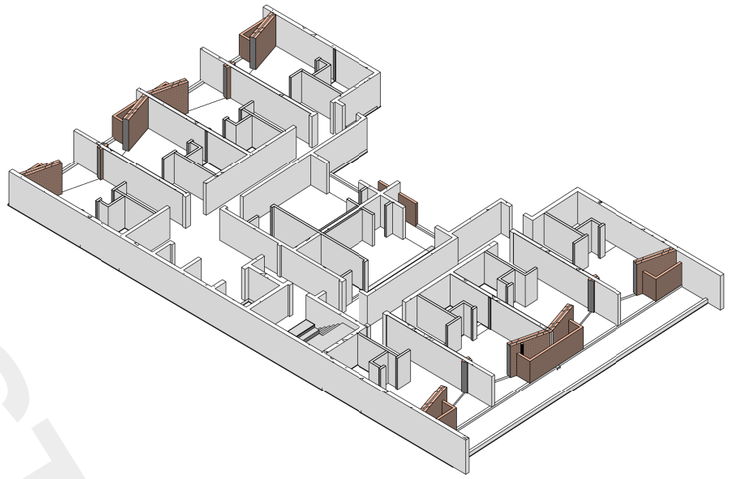


NOTES:

SUSPENDED SLAB:

A. DRAWING TO BE READ IN CONJUNCTION WITH ARCHITECTURE DRAWINGS .
B. REFER TO ARCHITECTURAL DRAWINGS FOR ALL SETOUT, LEVELS, STEPS, FOLDS & FALLS ETC.
C. REFER TO STORMWATER DRAINAGE DRAWINGS FOR LOCATION OF PUMP WELL AND SUMP PITS.
D. ALL CONCRETE CYLINDERS TO BE STORED AND CURED ON SITE PRIOR TESTING TO AS3600.
E. CONCRETE SLAB (f'c)=32 MPa WITH A SLUMP OF 80MM.
F. AGGREGATE MINIMUM SIZE 20MM.
G. ALL BRICKS WALLS TO BE ARTICULATED, EXPANSION JOINT SPACING TO BE 6000mm
H. ALL EXPOSED SLABS TO BE WATERPROOFED WITH APPROVED SYSTEMS.
I. ACOUSTIC ENGINEER TO CHECK AND VERIFY ALL FLOOR SLAB FOR ACOUSTIC REQUIREMENTS IN ACCORDANCE WITH THE BCA REGULATIONS AND ADVISE ON ANY ACOUSTIC TREATMENT NEEDED TO SATISFY THE REGULATION.
J. FOR FOLD REINFORCEMENTS REFER TO TYPICAL SECTION U.N.O.

SECOND FLOOR SLAB: FRL 90/90/90

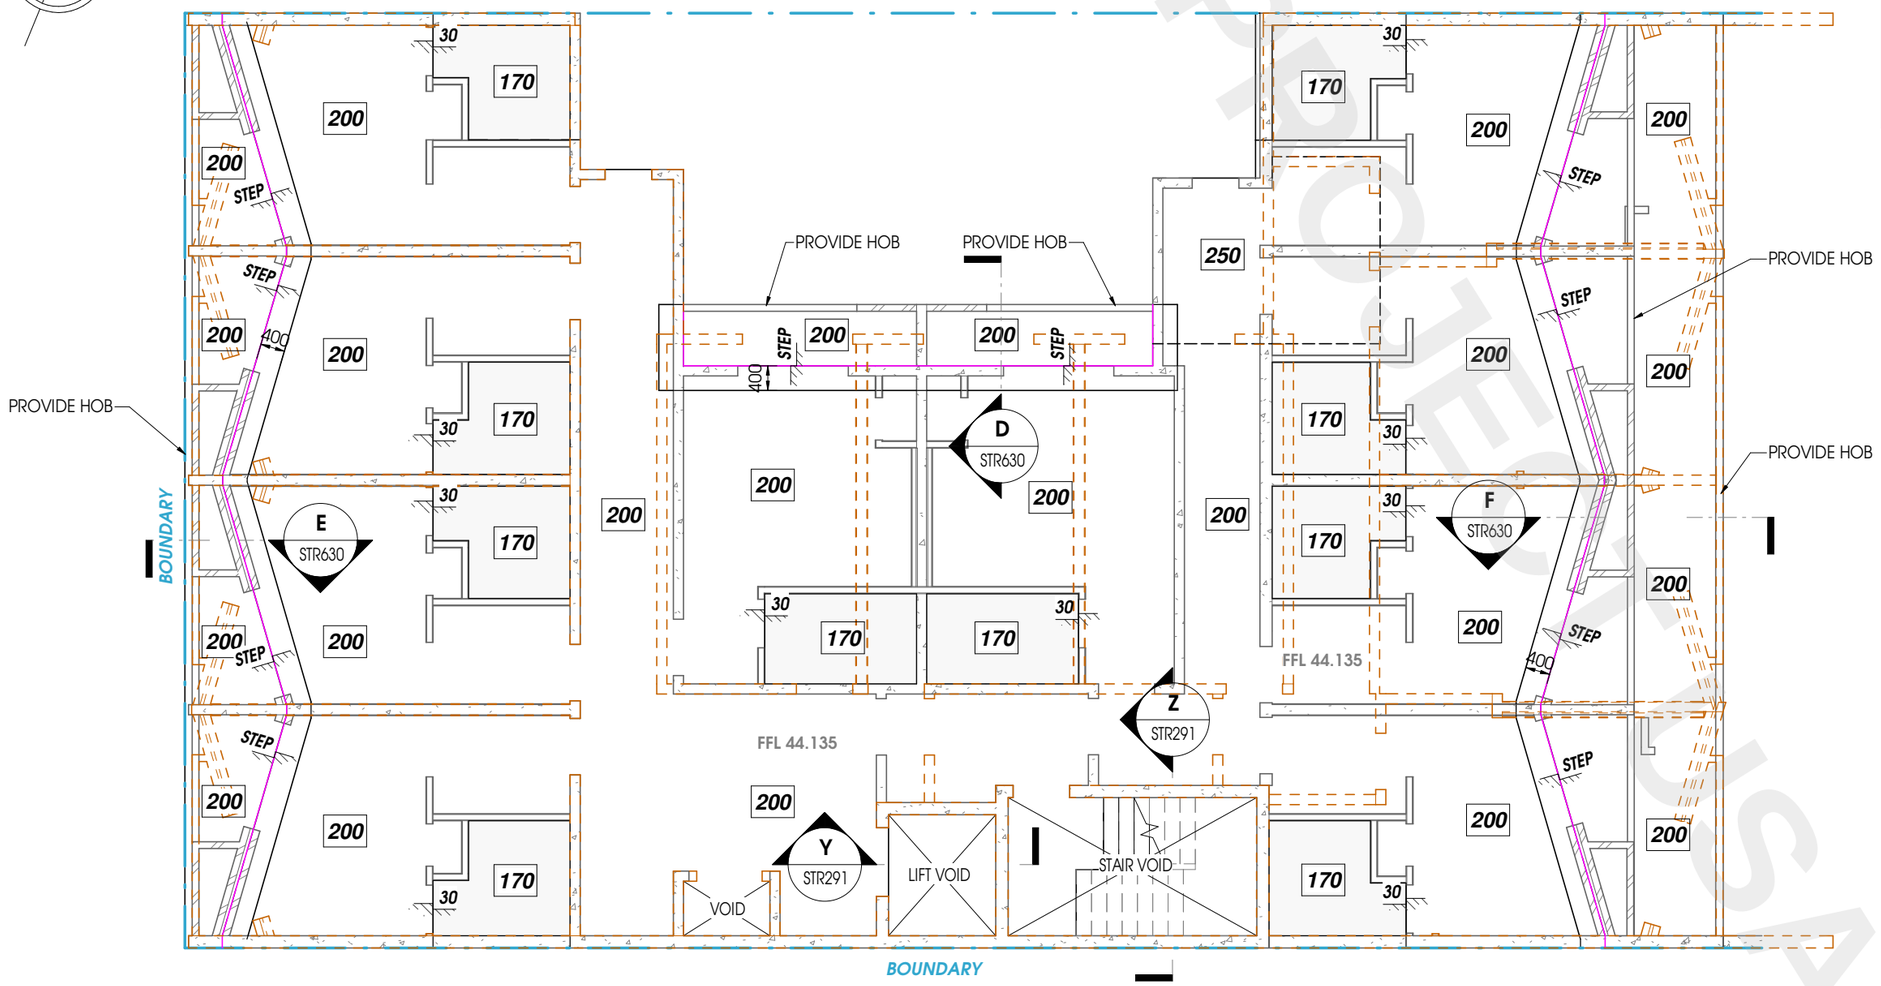

LEVEL 2 SUSPENDED CONCRETE SLAB PLAN

SCALE: 1 : 100

PRINT IN COLOUR

MODULAR ENGINEERS P/L

Structural Engineering | Civil Engineering
Stormwater Engineering | Flood Engineering
Traffic Engineering | Temporary works

ABN : 66 646 960 929
TEL. : 02 873 08473
MOB. : 04 208 98999
EMAIL :
WEBSITE :
ADDRESS :

CLIENT:

PROJECT TITLE:
MULTI DWELLING

SHEET NAME:
LEVEL 2 FLOOR PLAN

PROJECT NUMBER:
175-2026

INTERNAL REVISIONS:

ISSUE	DATE	DESCRIPTION	BY
E	10-09-26	ISSUED FOR CONSTRUCTION	D.A.
D	08-09-26	ISSUED FOR CONSTRUCTION	D.A.
C	24-08-26	ISSUED FOR PRELIMINARY	D.A.
B	21-08-26	ISSUED FOR PRELIMINARY	D.A.

AMENDMENTS

DRAWN : L.M. DATE: 17-07-26
DESIGNED : A.O. REVISION DATE:
QA CHECK : A.O. 10-09-26
APPROVED BY:

RPEQ: 28316
NPER: 5358554
DATE: 10-09-26

ISSUE TYPE:
CONSTRUCTION

SHEET NUMBER:
STR600

SHEET SIZE: **A3** REVISION: **E**

SAMPLE PROJECT A - STRUCTURAL REV E - CURRENT - RECRUITMENT ASSESSMENT ONLY

TEST PRO

NOT FOR ISSUE

NOTE: THE DESIGN AND DETAILS SHOWN ON THESE DRAWINGS ARE APPLICABLE TO THIS PROJECT ONLY AND MAY NOT BE REPRODUCED IN WHOLE OR IN PART OR BE USED FOR ANY OTHER PROJECT OR PURPOSE WITHOUT THE WRITTEN PERMISSION OF WITH WHOM COPYRIGHT RESIDES.

REGULATED DESIGN RECORD

PROJECT ADDRESS:	
PROJECT TITLE:	MULTI DWELLING
CONSENT NO:	STR208 - 2023
BODY CORPORATE REG NO:	DEP0001320
DRAWING TITLE:	LEVEL 2 WALL LAYOUT PLAN
DRAWING NO:	STR601

REV	DATE DD.MM.YY	DESCRIPTION	DP FULL NAME	REG NO
E	10-09-26	ISSUED FOR CONSTRUCTIO		

LEGEND:


- DENOTES CONCRETE COLUMN/ WALL **OVER ONLY**
- DENOTES BRICK WALLS **OVER ONLY**
- DENOTES BLOCK WORK WALLS **OVER ONLY**
- DENOTES RITEK WALLS **OVER ONLY**
- DENOTES CONCRETE WALL/COLUMN **UNDER ONLY**
- DENOTES WET AREA WITH 2mm FALL
- DENOTES SLAB PENETRATION
- DENOTES STEP ON SLAB
- C00 DENOTES COLUMN MARK
- W00 DENOTES WALL MARK
- 000 DENOTES SLAB THICKNESS
- DENOTES EXTENT OF SLAB STEP

FOR STRUCTURAL NOTES REFER TO DRAWING STR00 SERIES

WALL SCHEDULE

FLOOR LEVEL	TYPE	DESCRIPTION	THK (mm)	VERT. REINF.	HORZ. REINF.	f'c
LEVEL 2	2W1	RITEK WALL	200	N12-200 E.F.	N12-200 E.F.	32 MPa
	2W2	RITEK WALL	200	N12-200 E.F.	N12-200 E.F.	32 MPa
	2W3	RITEK WALL	150	N12-200 E.F.	N12-200 E.F.	32 MPa

SECOND FLOOR SLAB: FRL 90/90/90

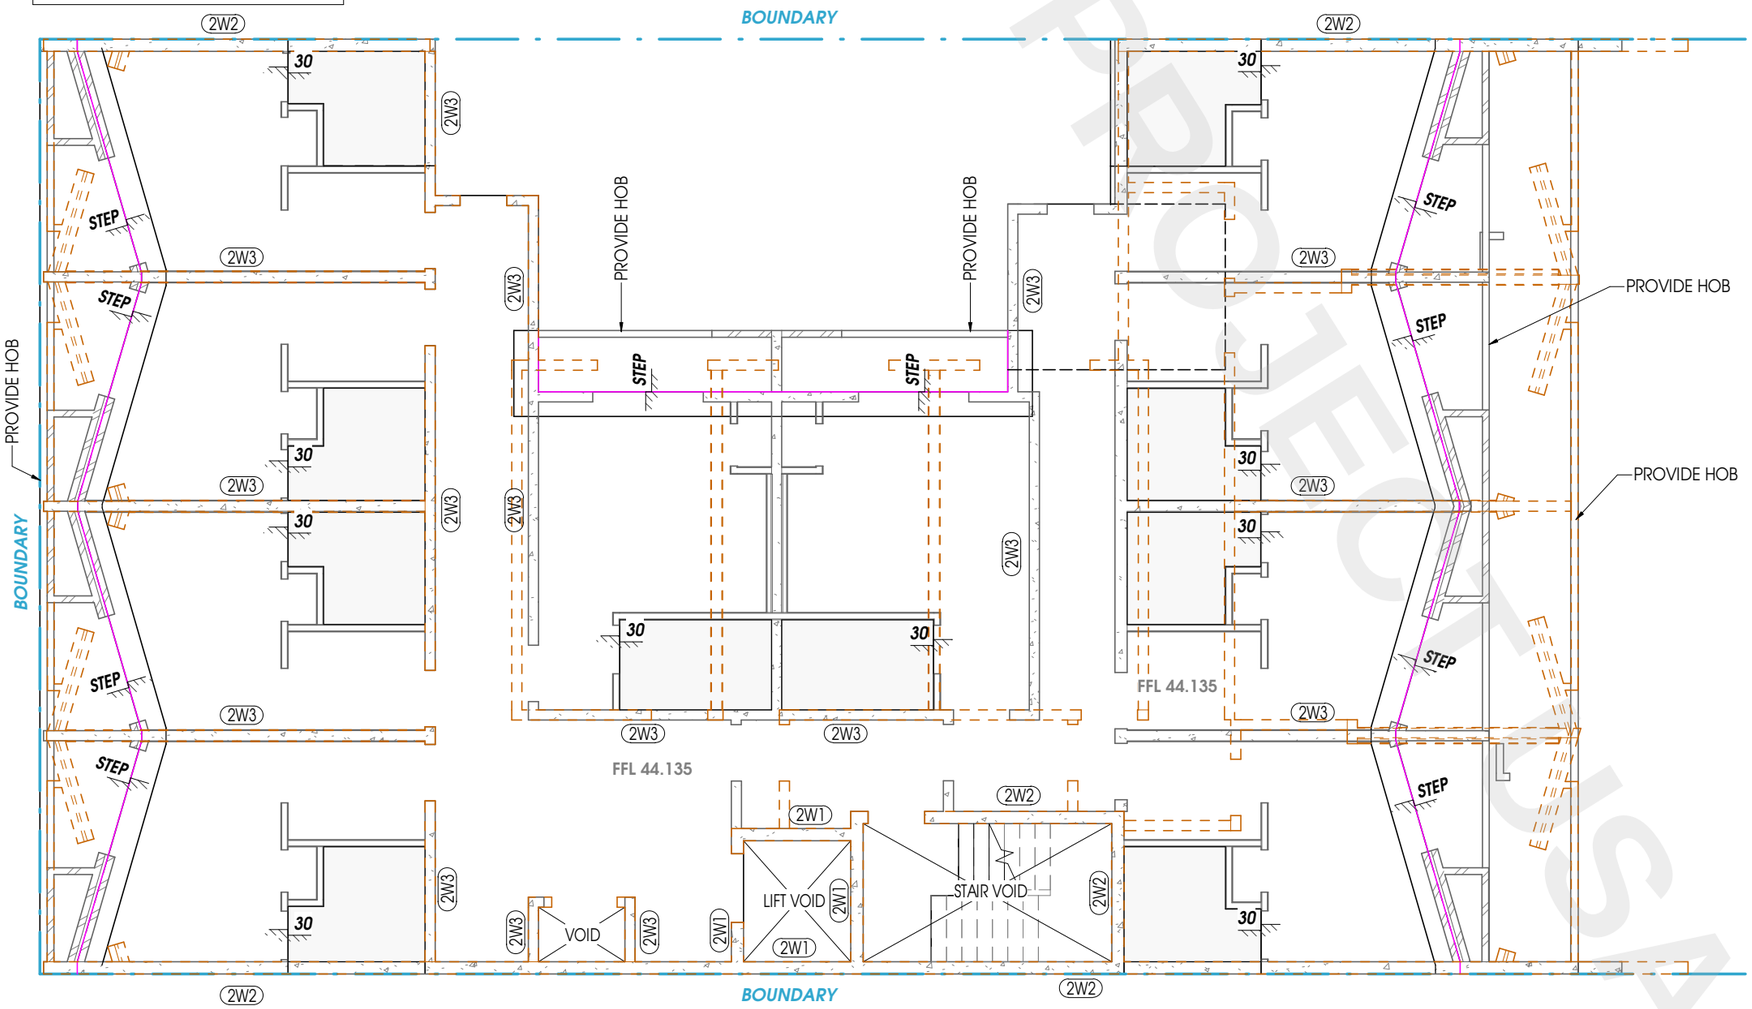

LEVEL 2 WALL LAYOUT PLAN

SCALE: 1 : 100

PRINT IN COLOUR

MODULAR ENGINEERS P/L

Structural Engineering | Civil Engineering
Stormwater Engineering | Flood Engineering
Traffic Engineering | Temporary works

ABN : 66 646 960 929
TEL. : 02 873 08473
MOB. : 04 208 98999
EMAIL :
WEBSITE :
ADDRESS :

CLIENT:

PROJECT TITLE: **MULTI DWELLING**

SHEET NAME: **LEVEL 2 WALL LAYOUT PLAN**

PROJECT NUMBER: **175-2026**

INTERNAL REVISIONS:

ISSUE	DATE	DESCRIPTION	BY
E	10-09-26	ISSUED FOR CONSTRUCTION	D.A.
D	08-09-26	ISSUED FOR CONSTRUCTION	D.A.
C	24-08-26	ISSUED FOR PRELIMINARY	D.A.
B	21-08-26	ISSUED FOR PRELIMINARY	D.A.

AMENDMENTS

DRAWN : L.M. DATE: 17-07-26
DESIGNED : A.O. REVISION DATE:
QA CHECK : A.O. 10-09-26
APPROVED BY:

RPEQ: 28316
NPER: 5358554
DATE: 10-09-26

ISSUE TYPE: **CONSTRUCTION**

SHEET NUMBER: **STR601**

SHEET SIZE: **A3** REVISION: **E**

SAMPLE PROJECT A - STRUCTURAL REV E - CURRENT - RECRUITMENT ASSESSMENT ONLY

TEST PROJECT

NOTE: THE DESIGN AND DETAILS SHOWN ON THESE DRAWINGS ARE APPLICABLE TO THIS PROJECT ONLY AND MAY NOT BE REPRODUCED IN WHOLE OR IN PART OR BE USED FOR ANY OTHER PROJECT OR PURPOSE WITHOUT THE WRITTEN PERMISSION OF WITH WHOM COPYRIGHT RESIDES.


REGULATED DESIGN RECORD

PROJECT ADDRESS:	
PROJECT TITLE:	MULTI DWELLING
CONSENT NO:	STR208 - 2023
BODY CORPORATE REG NO:	DEP0001320
DRAWING TITLE:	LEVEL 2 BOTTOM REINFORCEMENT PLAN
DRAWING NO:	STR610


REV	DATE DD.MM.YY	DESCRIPTION	DP FULL NAME	REG NO
E	10-09-26	ISSUED FOR CONSTRUCTIO		



BAR LAYING SEQUENCE

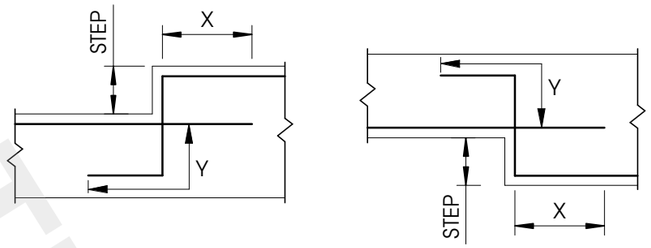

TYPICAL REINFORCEMENT LAPPING

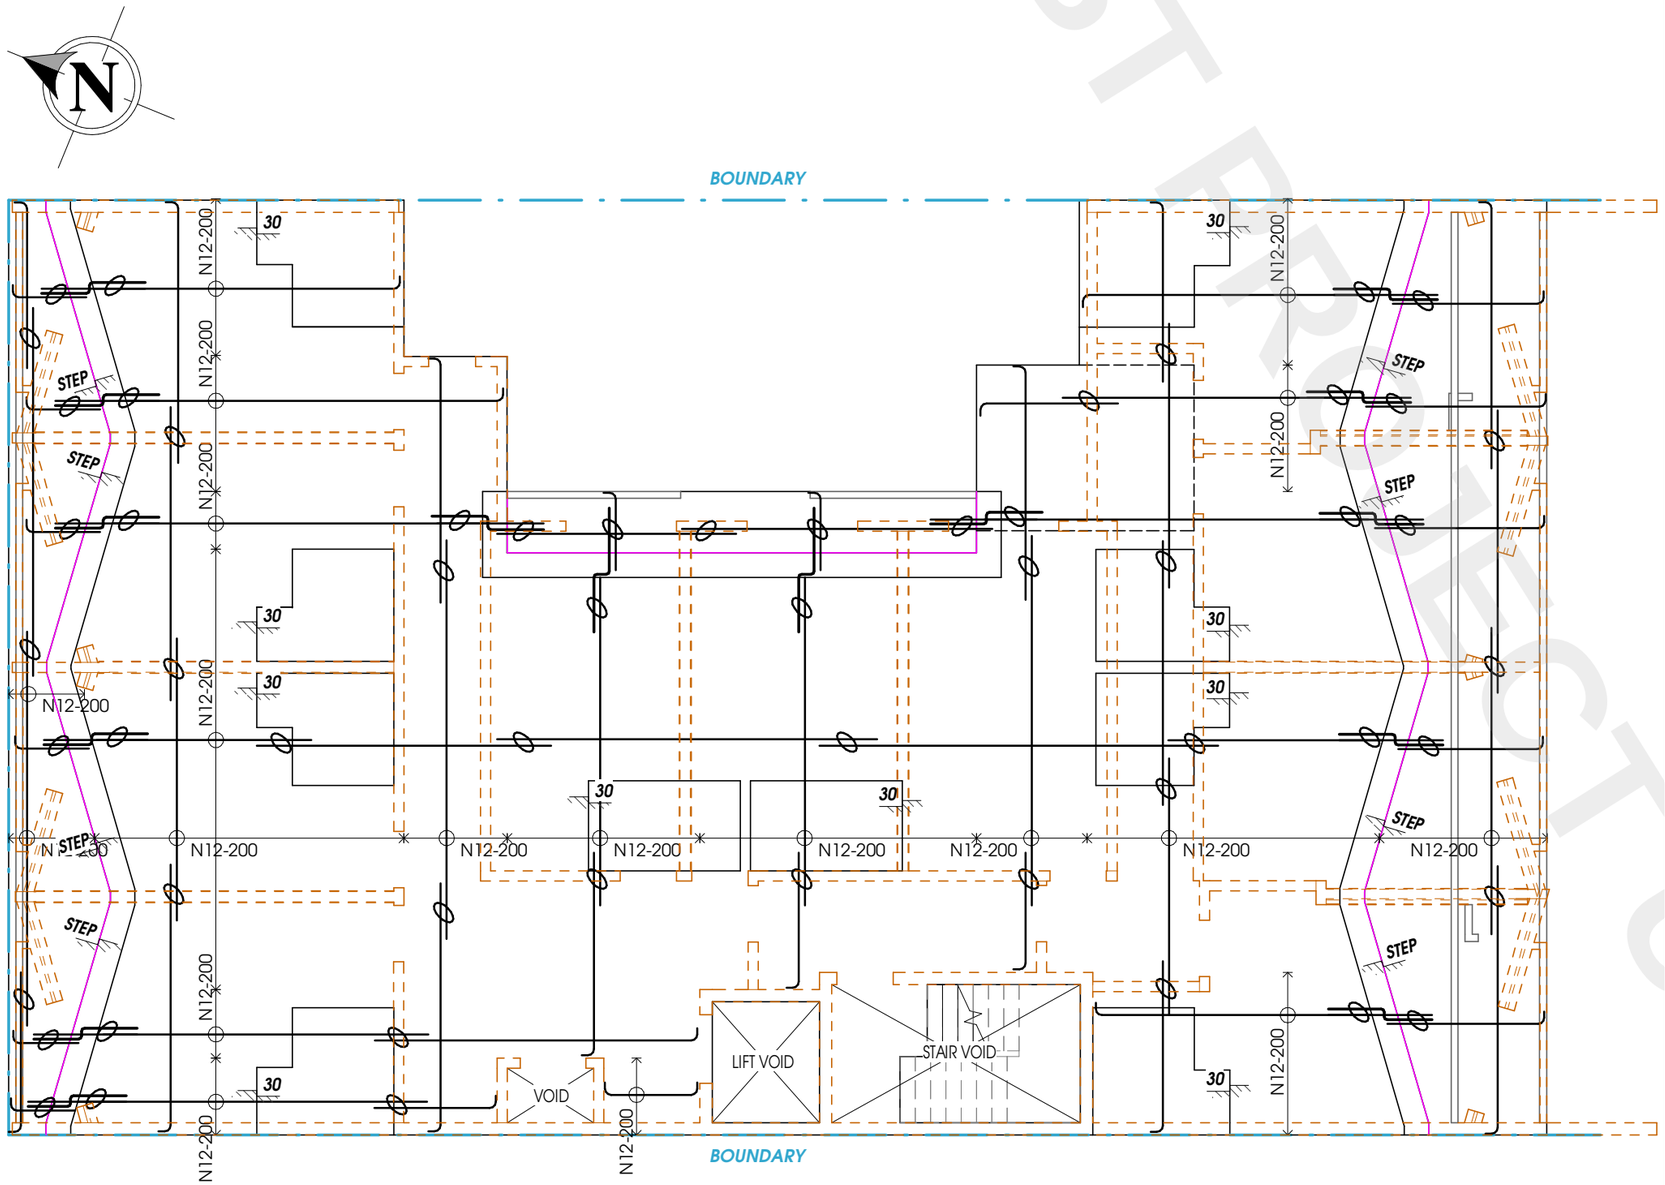


LEVEL 2 BOTTOM REINFORCEMENT PLAN

SCALE: 1 : 100


NOTES:

SUSPENDED SLAB:


A. DRAWING TO BE READ IN CONJUNCTION WITH ARCHITECTURE DRAWINGS .
B. REFER TO ARCHITECTURAL DRAWINGS FOR ALL SETOUT, LEVELS, STEPS, FOLDS & FALLS ETC.
C. REFER TO STORMWATER DRAINAGE DRAWINGS FOR LOCATION OF PUMP WELL AND SUMP PITS.
D. ALL CONCRETE CYLINDERS TO BE STORED AND CURED ON SITE PRIOR TESTING TO AS3600.
E. CONCRETE SLAB (f'c)=32 MPa WITH A SLUMP OF 80MM.
F. AGGREGATE MINIMUM SIZE 20MM.
G. ALL BRICKS WALLS TO BE ARTICULATED, EXPANSION JOINT SPACING TO BE 6000mm
H. ALL EXPOSED SLABS TO BE WATERPROOFED WITH APPROVED SYSTEMS.
I. ACOUSTIC ENGINEER TO CHECK AND VERIFY ALL FLOOR SLAB FOR ACOUSTIC REQUIREMENTS IN ACCORDANCE WITH THE BCA REGULATIONS AND ADVISE ON ANY ACOUSTIC TREATMENT NEEDED TO SATISFY THE REGULATION.
J. FOR FOLD REINFORCEMENTS REFER TO SECTION S4 U.N.O.
K. ENSURE 50mm MINIMUM SPACING BETWEEN BARS.
L. PROVIDE ALL EXTRA REINFORCEMENT AS SHOWN ON PLAN.
M. PROVIDE 3N16 TOP AND BOTTOM AT THE PERIMETER OF THE SLAB.
N. SLAB REINFORCEMENT LAYING SEQUENCE U.N.O.:

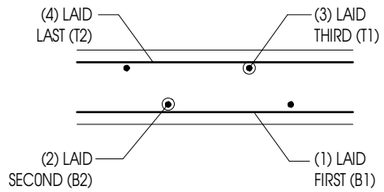

O. TYPICAL TRIMMERS AT PENETRATION/OPENING DETAIL:

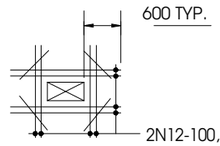

P. TYPICAL TRIMMERS AT RE-ENTRANT CORNERS:

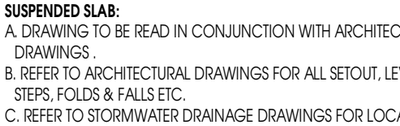

Q. PROVIDE TOP & BOTTOM BARS ON ALL WALL OPENINGS AS PER THE SCHEDULE BELOW:

LENGTH OF OPENING (m)	BOTTOM BAR	TOP BAR
1.0 - 1.8	2N16	2N16
1.8 - 2.5	2N20	2N20
2.5 - 3.5	2N24	2N24

R. PROVIDE ADEQUATE OVERLAP AT MESH JOINTS AS FOLLOWS :
- 400 MIN. LAP FOR SL82 MESH
- 500 MIN. LAP FOR SL92 MESH
- 600 MIN. LAP FOR SL102 MESH

S. PROVIDE ADEQUATE OVERLAP FOR BARS AS FOLLOWS:

BAR(X-Y)	MIN LAPPING REQUIRED
N12	500 mm
N16	800 mm
N20	1000 mm
N24	1200 mm
N28	1400 mm

PRINT IN COLOUR

MODULAR ENGINEERS P/L

Structural Engineering | Civil Engineering
Stormwater Engineering | Flood Engineering
Traffic Engineering | Temporary works

ABN : 66 646 960 929
TEL. : 02 873 08473
MOB. : 04 208 98999
EMAIL :
WEBSITE :
ADDRESS :

CLIENT:

PROJECT TITLE:
MULTI DWELLING

SHEET NAME:
LEVEL 2 BOTTOM REINFORCEMENT PLAN

PROJECT NUMBER:
175-2026

INTERNAL REVISIONS:

ISSUE	DATE	DESCRIPTION	BY
E	10-09-26	ISSUED FOR CONSTRUCTION	D.A.
D	08-09-26	ISSUED FOR CONSTRUCTION	D.A.
C	24-08-26	ISSUED FOR PRELIMINARY	D.A.
B	21-08-26	ISSUED FOR PRELIMINARY	D.A.

AMENDMENTS

DRAWN : L.M. DATE: 17-07-26
DESIGNED : A.O. REVISION DATE:
QA CHECK : A.O. 10-09-26
APPROVED BY:

RPEQ: 28316
NPER: 5358554
DATE: 10-09-26

ISSUE TYPE:
CONSTRUCTION

SHEET NUMBER:
STR610

SHEET SIZE: **A3**
REVISION: **E**

SAMPLE PROJECT A - STRUCTURAL REVIEW - CURRENT - RECRUITMENT ASSESSMENT ONLY

TEST PROJECT

NOTE: THE DESIGN AND DETAILS SHOWN ON THESE DRAWINGS ARE APPLICABLE TO THIS PROJECT ONLY AND MAY NOT BE REPRODUCED IN WHOLE OR IN PART OR BE USED FOR ANY OTHER PROJECT OR PURPOSE WITHOUT THE WRITTEN PERMISSION OF WITH WHOM COPYRIGHT RESIDES.


REGULATED DESIGN RECORD

PROJECT ADDRESS:	
PROJECT TITLE:	MULTI DWELLING
CONSENT NO:	STR208 - 2023
BODY CORPORATE REG NO:	DEP0001320
DRAWING TITLE:	LEVEL 2 TOP REINFORCEMENT PLAN
DRAWING NO:	STR611


REV	DATE DD.MM.YY	DESCRIPTION	DP FULL NAME	REG NO
E	10-09-26	ISSUED FOR CONSTRUCTIO		



BAR LAYING SEQUENCE

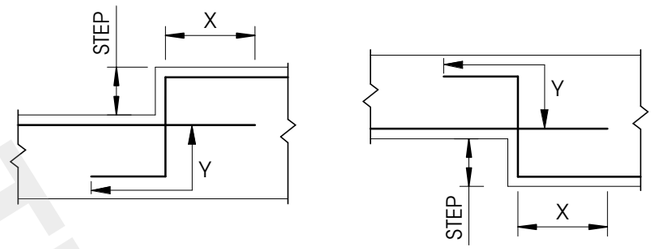

TYPICAL REINFORCEMENT LAPPING

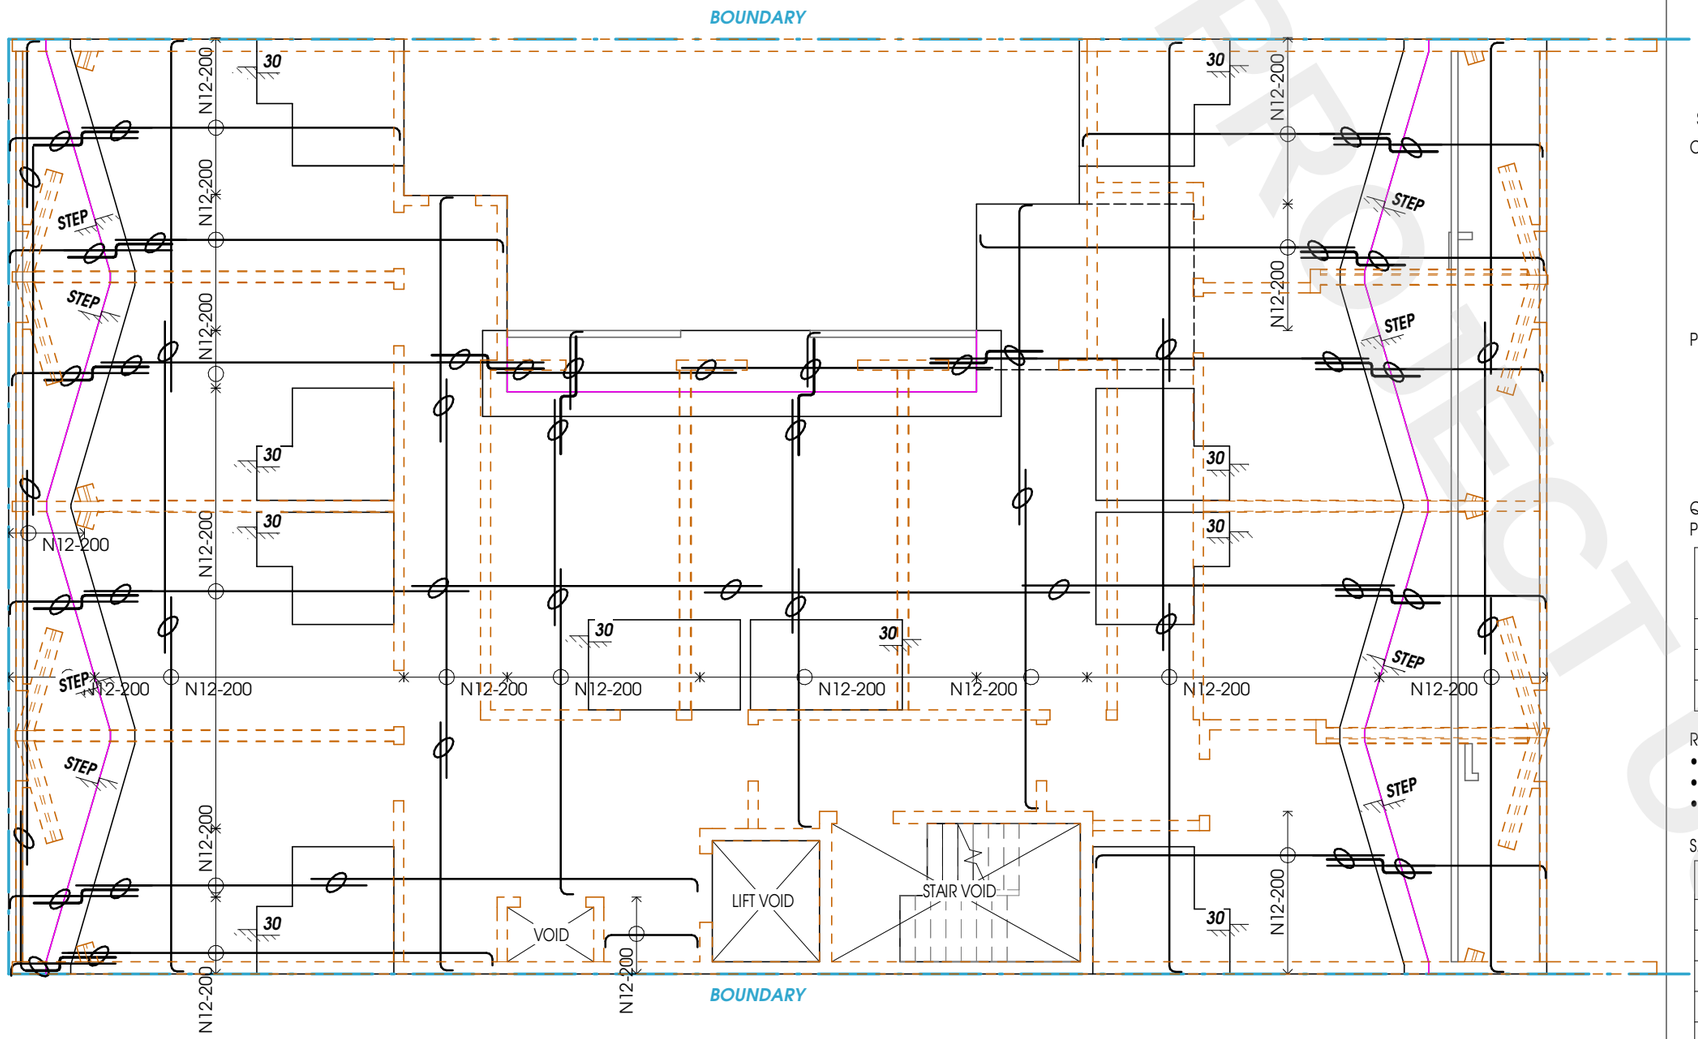


LEVEL 2 TOP REINFORCEMENT PLAN

SCALE: 1 : 100


NOTES:

SUSPENDED SLAB:


A. DRAWING TO BE READ IN CONJUNCTION WITH ARCHITECTURE DRAWINGS .
B. REFER TO ARCHITECTURAL DRAWINGS FOR ALL SETOUT, LEVELS, STEPS, FOLDS & FALLS ETC.
C. REFER TO STORMWATER DRAINAGE DRAWINGS FOR LOCATION OF PUMP WELL AND SUMP PITS.
D. ALL CONCRETE CYLINDERS TO BE STORED AND CURED ON SITE PRIOR TESTING TO AS3600.
E. CONCRETE SLAB (f'c)=32 MPa WITH A SLUMP OF 80MM.
F. AGGREGATE MINIMUM SIZE 20MM.
G. ALL BRICKS WALLS TO BE ARTICULATED, EXPANSION JOINT SPACING TO BE 6000mm
H. ALL EXPOSED SLABS TO BE WATERPROOFED WITH APPROVED SYSTEMS.
I. ACOUSTIC ENGINEER TO CHECK AND VERIFY ALL FLOOR SLAB FOR ACOUSTIC REQUIREMENTS IN ACCORDANCE WITH THE BCA REGULATIONS AND ADVISE ON ANY ACOUSTIC TREATMENT NEEDED TO SATISFY THE REGULATION.
J. FOR FOLD REINFORCEMENTS REFER TO SECTION S4 U.N.O.
K. ENSURE 50mm MINIMUM SPACING BETWEEN BARS.
L. PROVIDE ALL EXTRA REINFORCEMENT AS SHOWN ON PLAN.
M. PROVIDE 3N16 TOP AND BOTTOM AT THE PERIMETER OF THE SLAB.
N. SLAB REINFORCEMENT LAYING SEQUENCE U.N.O.:

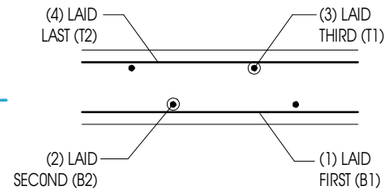

O. TYPICAL TRIMMERS AT PENETRATION/OPENING DETAIL:

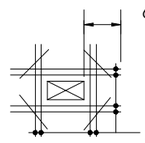

P. TYPICAL TRIMMERS AT RE-ENTRANT CORNERS:

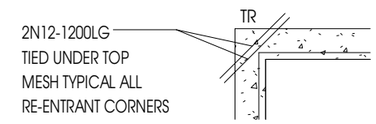

Q. PROVIDE TOP & BOTTOM BARS ON ALL WALL OPENINGS AS PER THE SCHEDULE BELOW:

LENGTH OF OPENING (m)	BOTTOM BAR	TOP BAR
1.0 - 1.8	2N16	2N16
1.8 - 2.5	2N20	2N20
2.5 - 3.5	2N24	2N24

R. PROVIDE ADEQUATE OVERLAP AT MESH JOINTS AS FOLLOWS :
- 400 MIN. LAP FOR SL82 MESH
- 500 MIN. LAP FOR SL92 MESH
- 600 MIN. LAP FOR SL102 MESH

S. PROVIDE ADEQUATE OVERLAP FOR BARS AS FOLLOWS:

BAR(X-Y)	MIN LAPPING REQUIRED
N12	500 mm
N16	800 mm
N20	1000 mm
N24	1200 mm
N28	1400 mm

MODULAR ENGINEERS P/L
Structural Engineering | Civil Engineering
Stormwater Engineering | Flood Engineering
Traffic Engineering | Temporary works
ABN : 66 646 960 929
TEL. : 02 873 08473
MOB. : 04 208 98999
EMAIL :
WEBSITE :
ADDRESS :

CLIENT:

PROJECT TITLE:
MULTI DWELLING

SHEET NAME:
LEVEL 2 TOP REINFORCEMENT PLAN

PROJECT NUMBER:
175-2026

INTERNAL REVISIONS:

ISSUE	DATE	DESCRIPTION	BY
E	10-09-26	ISSUED FOR CONSTRUCTION	D.A.
D	08-09-26	ISSUED FOR CONSTRUCTION	D.A.
C	24-08-26	ISSUED FOR PRELIMINARY	D.A.
B	21-08-26	ISSUED FOR PRELIMINARY	D.A.

AMENDMENTS

DRAWN : L.M. DATE: 17-07-26
DESIGNED : A.O. REVISION DATE:
QA CHECK : A.O. 10-09-26
APPROVED BY:

RPEQ: 28316
NPER: 5358554
DATE: 10-09-26

ISSUE TYPE:
CONSTRUCTION

SHEET NUMBER:
STR611

SHEET SIZE: **A3** REVISION: **E**

PRINT IN COLOUR

SAMPLE PROJECT A - STRUCTURAL REV E - CURRENT - RECRUITMENT ASSESSMENT ONLY
TEST PROJECT ONLY
NOTE: THE DESIGN AND DETAILS SHOWN ON THESE DRAWINGS ARE APPLICABLE TO THIS PROJECT ONLY AND MAY NOT BE REPRODUCED IN WHOLE OR IN PART OR BE USED FOR ANY OTHER PROJECT OR PURPOSE WITHOUT THE WRITTEN PERMISSION OF WITH WHOM COPYRIGHT RESIDES.

REGULATED DESIGN RECORD

PROJECT ADDRESS:			
PROJECT TITLE:	MULTI DWELLING		
CONSENT NO:	STR208 - 2023	BODY CORPORATE REG NO:	DEP0001320
DRAWING TITLE:	LEVEL 2 LOADING PLAN	DRAWING NO:	STR620

REV	DATE DD.MM.YY	DESCRIPTION	DP FULL NAME	REG NO
E	10-09-26	ISSUED FOR CONSTRUCTIO		




LOADING TABLE
WHERE APPLICABLE

MARK	COLOUR	AREA	SUPERIMPOSED DEAD LOAD	LIVE LOAD
1		RESIDENTIAL	1.5 kPa	1.5 kPa
2		PARKING	0.5 kPa EXC. FALLS AND GRADING	2.5 kPa
3		STORAGE	0.5 kPa	5.0 kPa
4		CORRIDOR / STAIR	1.5 kPa	4.0 kPa
5		LOBBY	1.5 kPa	4.0 kPa
6		BALCONY	1.5 kPa	2.0 kPa
7		MECH ROOM,FAN ROOM	1.5 kPa	5.0 kPa
8		COMMON AREA	1.5 kPa	4.0 kPa
9		LIGHT WEIGHT ROOF	0.5 kPa	0.5 kPa

LOADING TABLE
WHERE APPLICABLE

MARK	COLOUR	AREA	SUPERIMPOSED DEAD LOAD	LIVE LOAD
10		WASTE ROOM	0.5 kPa	5.0 kPa
11		RETAILS	1.5 kPa	4.0 kPa
12		ROOF (NON-TRAFFICABLE)	2.0 kPa	1.5 kPa
13		LANDSCAPE 400mm SOIL MAX.	4.0 kPa	1.5 kPa
14		LANDSCAPE 1000mm SOIL MAX.	10.0 kPa	1.5 kPa
15		SUBSTATION	1.0 kPa	2.0 kPa
16		LOADING DECK	1.0 kPa	10.0 kPa
17		PEBBLES	4.0 kPa	1.5 kPa
18		OSD TANK/ WATER STORAGE TANK	10.0 kPa FOR EVERY METRE HEIGHT OF WATER	

DEFLECTION NOTES (LONG-TERM)
- LONG-TERM DEFLECTION IS BASED ON DL + 0.3LL FOR SUSTAINED LOADS.
- CREEP FACTOR Λ = 2.0 TO 3.0 APPLIED PER AS3600.
- TOTAL DEFLECTION: Δ TOTAL=Δ IMMEDIATE + Λ × Δ SUSTAINED
- IMMEDIATE DEFLECTION: DL + LL
- LONG-TERM DEFLECTION: DL + 0.3LL × Λ

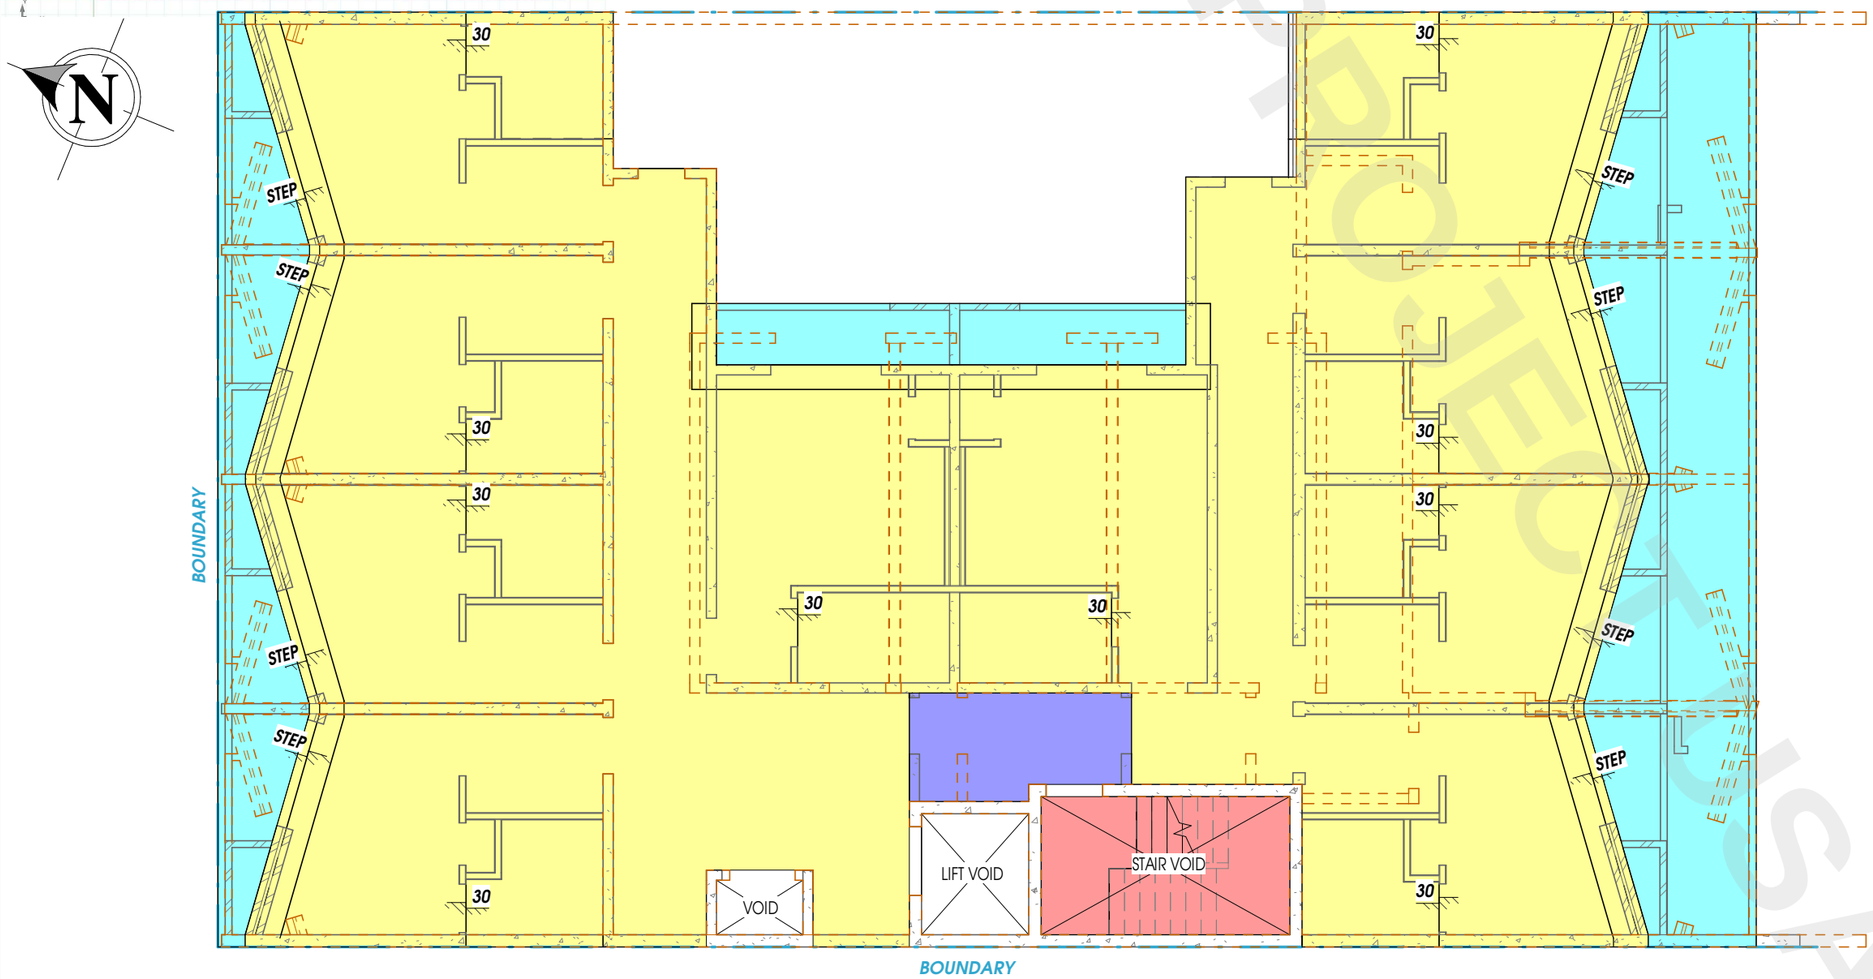

LEVEL 2 LOADING PLAN
SCALE: 1 : 100

PRINT IN COLOUR

MODULAR ENGINEERS P/L
Structural Engineering | Civil Engineering
Stormwater Engineering | Flood Engineering
Traffic Engineering | Temporary works
ABN : 66 646 960 929
TEL. : 02 873 08473
MOB. : 04 208 98999
EMAIL :
WEBSITE :
ADDRESS :

CLIENT:

PROJECT TITLE:
MULTI DWELLING

SHEET NAME:
LEVEL 2 LOADING PLAN

PROJECT NUMBER:
175-2026

INTERNAL REVISIONS:

ISSUE	DATE	DESCRIPTION	BY
E	10-09-26	ISSUED FOR CONSTRUCTION	D.A.
D	08-09-26	ISSUED FOR CONSTRUCTION	D.A.
C	24-08-26	ISSUED FOR PRELIMINARY	D.A.
B	21-08-26	ISSUED FOR PRELIMINARY	D.A.

AMENDMENTS

DRAWN : L.M. DATE: 17-07-26
DESIGNED : A.O. REVISION DATE:
QA CHECK : A.O. 10-09-26

APPROVED BY:

RPEQ: 28316
NPER: 5358554
DATE: 10-09-26

ISSUE TYPE:
CONSTRUCTION

SHEET NUMBER:
STR620

SHEET SIZE: **A3**
REVISION: **E**


SAMPLE PROJECT A - STRUCTURAL REVIEW - CURRENT - RECRUITMENT ASSESSMENT ONLY
TEST PROJECT ISSUE

NOTE: THE DESIGN AND DETAILS SHOWN ON THESE DRAWINGS ARE APPLICABLE TO THIS PROJECT ONLY AND MAY NOT BE REPRODUCED IN WHOLE OR IN PART OR BE USED FOR ANY OTHER PROJECT OR PURPOSE WITHOUT THE WRITTEN PERMISSION OF WITH WHOM COPYRIGHT RESIDES.


REGULATED DESIGN RECORD

PROJECT ADDRESS:			
PROJECT TITLE:	MULTI DWELLING		
CONSENT NO:	STR208 - 2023	BODY CORPORATE REG NO:	DEP0001320
DRAWING TITLE:	SECTION AND DETAILS	DRAWING NO:	STR630


REV	DATE DD.MM.YY	DESCRIPTION	DP FULL NAME	REG NO
E	10-09-26	ISSUED FOR CONSTRUCTIO		

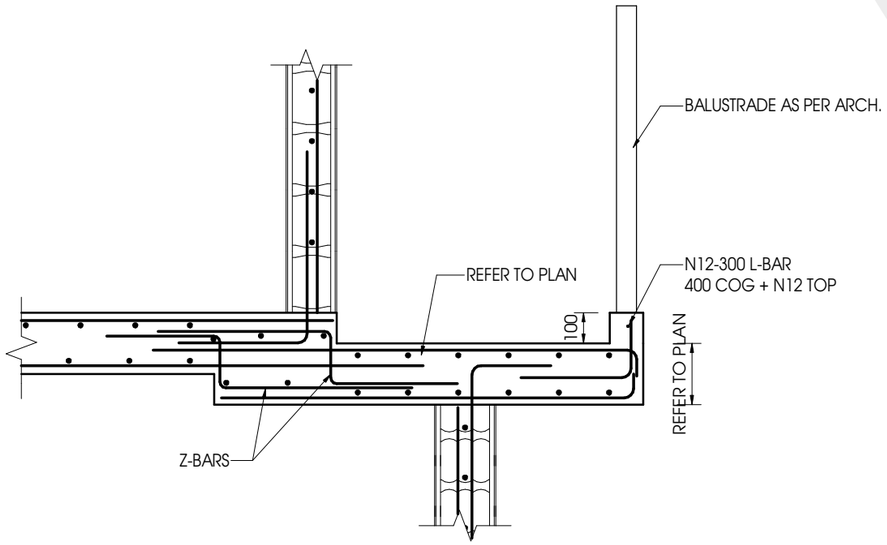

SECTION D
NOT TO SCALE STR600

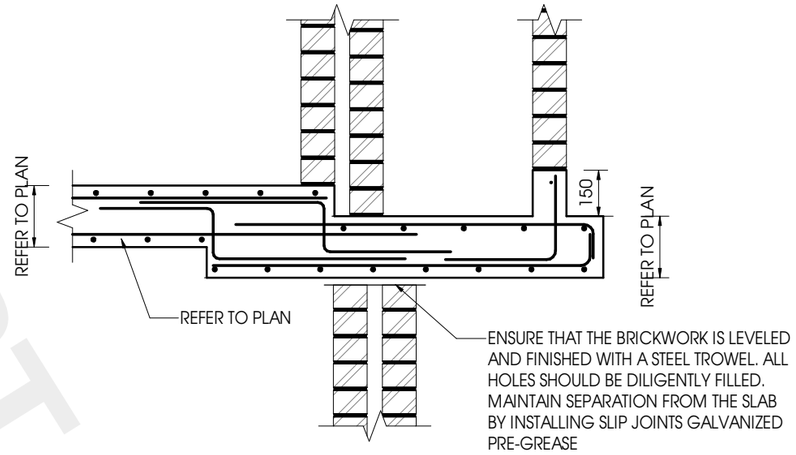

SECTION E
NOT TO SCALE STR600

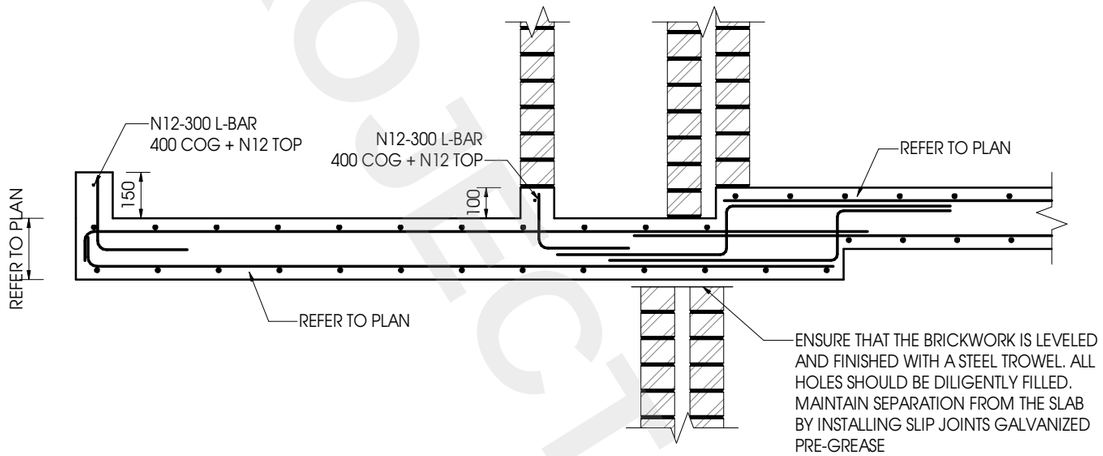

SECTION F
NOT TO SCALE STR600

MODULAR ENGINEERS P/L
Structural Engineering | Civil Engineering
Stormwater Engineering | Flood Engineering
Traffic Engineering | Temporary works
ABN : 66 646 960 929
TEL. : 02 873 08473
MOB. : 04 208 98999
EMAIL :
WEBSITE :
ADDRESS :

CLIENT:

PROJECT TITLE:
MULTI DWELLING

SHEET NAME:
SECTION AND DETAILS

PROJECT NUMBER:
175-2026

INTERNAL REVISIONS:

ISSUE	DATE	DESCRIPTION	BY
E	10-09-26	ISSUED FOR CONSTRUCTION	D.A.
D	08-09-26	ISSUED FOR CONSTRUCTION	D.A.
C	24-08-26	ISSUED FOR PRELIMINARY	D.A.
B	21-08-26	ISSUED FOR PRELIMINARY	D.A.

AMENDMENTS

DRAWN : L.M. DATE: 17-07-26
DESIGNED : A.O. REVISION DATE:
QA CHECK : A.O. 10-09-26

APPROVED BY:

RPEQ: 28316
NPER: 5358554
DATE: 10-09-26

ISSUE TYPE:
CONSTRUCTION

SHEET NUMBER:
STR630

SHEET SIZE: **A3** REVISION: **E**

PRINT IN COLOUR

SAMPLE PROJECT A - STRUCTURAL REV E - CURRENT - RECRUITMENT ASSESSMENT ONLY

TEST PROJECT USAGE

NOTE: THE DESIGN AND DETAILS SHOWN ON THESE DRAWINGS ARE APPLICABLE TO THIS PROJECT ONLY AND MAY NOT BE REPRODUCED IN WHOLE OR IN PART OR BE USED FOR ANY OTHER PROJECT OR PURPOSE WITHOUT THE WRITTEN PERMISSION OF WITH WHOM COPYRIGHT RESIDES.

REGULATED DESIGN RECORD


PROJECT ADDRESS:	
PROJECT TITLE:	MULTI DWELLING
CONSENT NO:	STR208 - 2023
BODY CORPORATE REG NO:	DEP0001320
DRAWING TITLE:	LEVEL 3 FLOOR PLAN
DRAWING NO:	STR700

REV	DATE DD.MM.YY	DESCRIPTION	DP FULL NAME	REG NO
E	10-09-26	ISSUED FOR CONSTRUCTIO		

LEGEND:

- DENOTES CONCRETE COLUMN/ WALL **OVER ONLY**
- DENOTES BRICK WALLS **OVER ONLY**
- DENOTES BLOCK WORK WALLS **OVER ONLY**
- DENOTES RITEK WALLS **OVER ONLY**
- DENOTES CONCRETE WALL/COLUMN **UNDER ONLY**
- DENOTES WET AREA WITH 2mm FALL
- DENOTES SLAB PENETRATION
- DENOTES STEP ON SLAB
- C00 DENOTES COLUMN MARK
- W00 DENOTES WALL MARK
- 000 DENOTES SLAB THICKNESS
- DENOTES EXTENT OF SLAB STEP

FOR STRUCTURAL NOTES REFER TO DRAWING STR00 SERIES

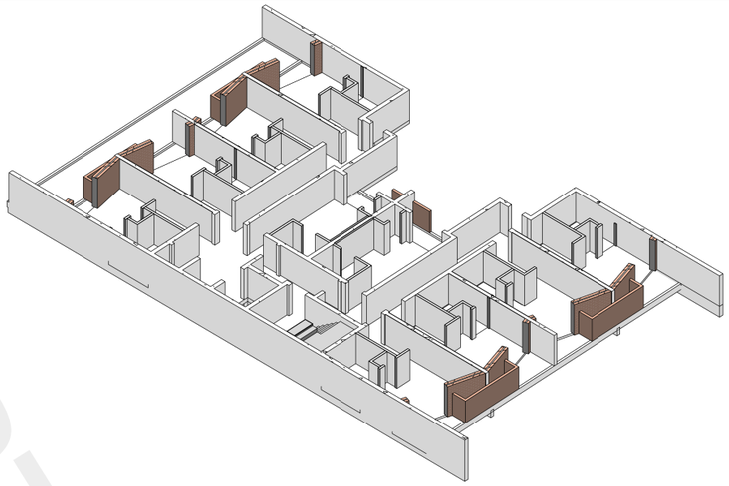


NOTES:

SUSPENDED SLAB:

A. DRAWING TO BE READ IN CONJUNCTION WITH ARCHITECTURE DRAWINGS .
B. REFER TO ARCHITECTURAL DRAWINGS FOR ALL SETOUT, LEVELS, STEPS, FOLDS & FALLS ETC.
C. REFER TO STORMWATER DRAINAGE DRAWINGS FOR LOCATION OF PUMP WELL AND SUMP PITS.
D. ALL CONCRETE CYLINDERS TO BE STORED AND CURED ON SITE PRIOR TESTING TO AS3600.
E. CONCRETE SLAB (f'c)=32 MPa WITH A SLUMP OF 80MM.
F. AGGREGATE MINIMUM SIZE 20MM.
G. ALL BRICKS WALLS TO BE ARTICULATED, EXPANSION JOINT SPACING TO BE 6000mm
H. ALL EXPOSED SLABS TO BE WATERPROOFED WITH APPROVED SYSTEMS.
I. ACOUSTIC ENGINEER TO CHECK AND VERIFY ALL FLOOR SLAB FOR ACOUSTIC REQUIREMENTS IN ACCORDANCE WITH THE BCA REGULATIONS AND ADVISE ON ANY ACOUSTIC TREATMENT NEEDED TO SATISFY THE REGULATION.
J. FOR FOLD REINFORCEMENTS REFER TO TYPICAL SECTION U.N.O.

THIRD FLOOR SLAB: FRL 90/90/90

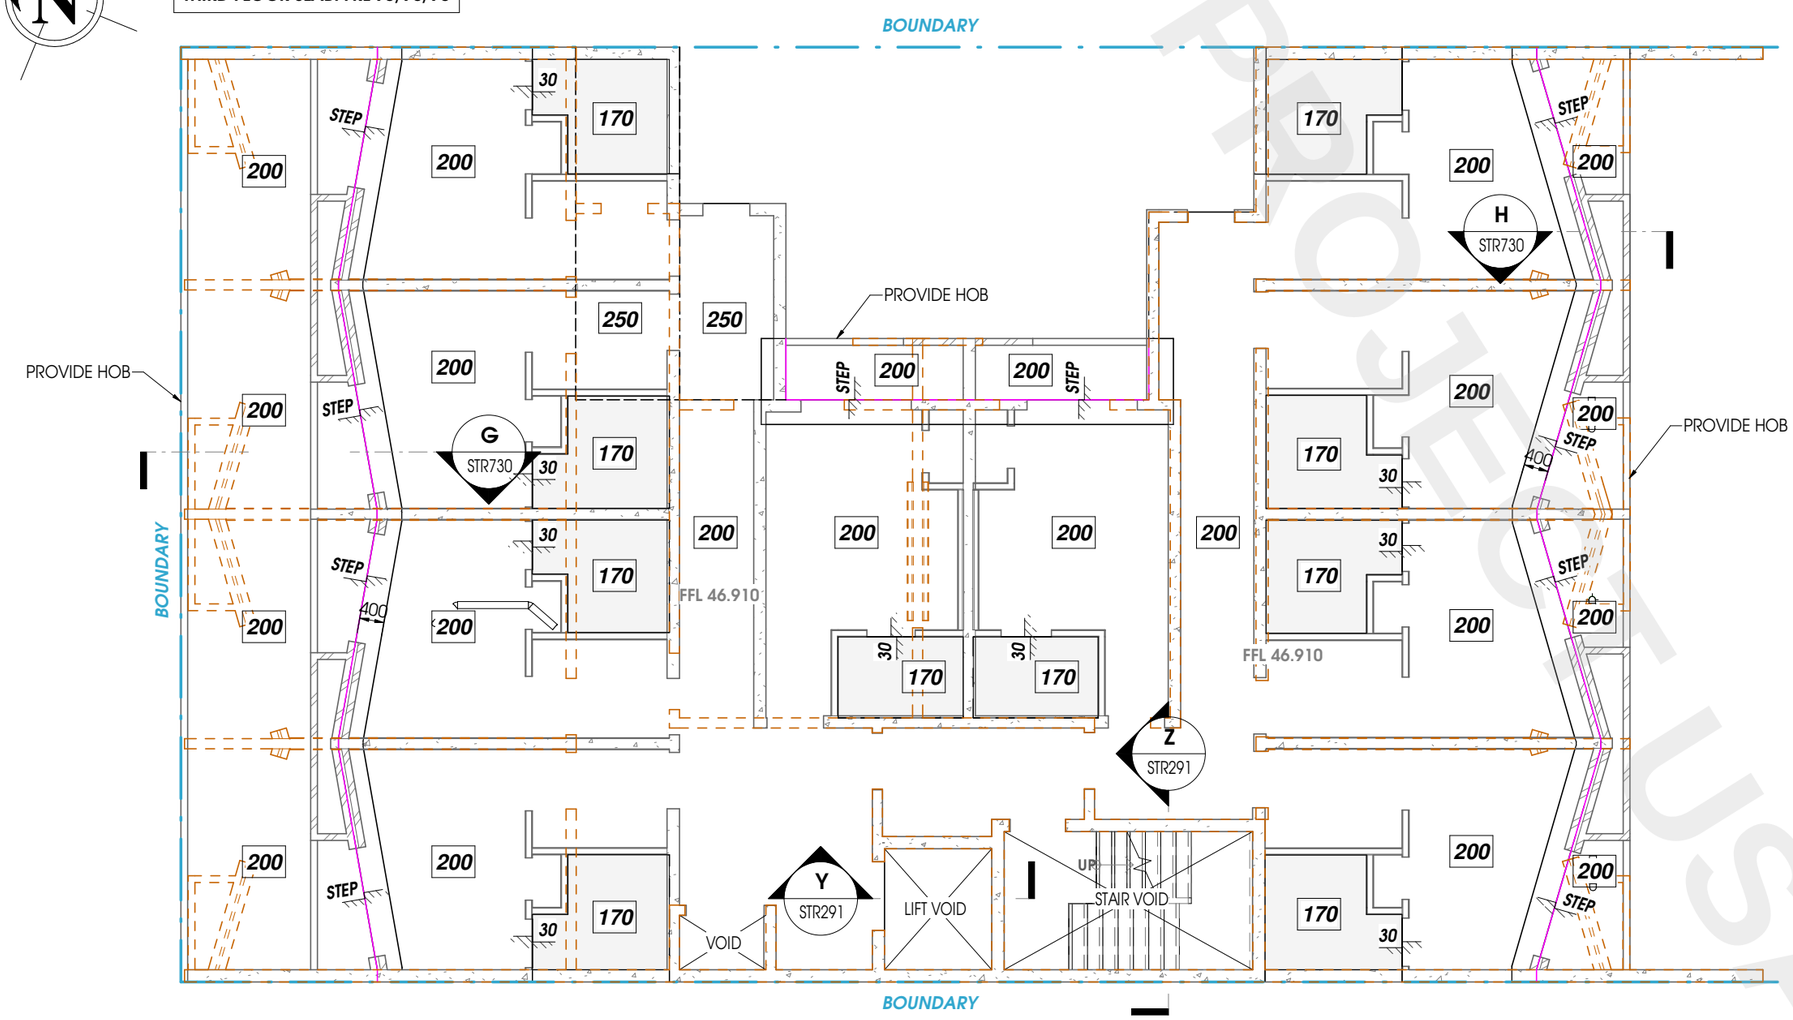

LEVEL 3 SUSPENDED CONCRETE SLAB PLAN

SCALE: 1 : 100

MODULAR ENGINEERS P/L

Structural Engineering | Civil Engineering
Stormwater Engineering | Flood Engineering
Traffic Engineering | Temporary works

ABN : 66 646 960 929
TEL. : 02 873 08473
MOB. : 04 208 98999
EMAIL :
WEBSITE :
ADDRESS :

CLIENT:

PROJECT TITLE:
MULTI DWELLING

SHEET NAME:
LEVEL 3 FLOOR PLAN

PROJECT NUMBER:
175-2026

INTERNAL REVISIONS:

ISSUE	DATE	DESCRIPTION	BY
E	10-09-26	ISSUED FOR CONSTRUCTION	D.A.
D	08-09-26	ISSUED FOR CONSTRUCTION	D.A.
C	24-08-26	ISSUED FOR PRELIMINARY	D.A.
B	21-08-26	ISSUED FOR PRELIMINARY	D.A.

AMENDMENTS

DRAWN : L.M. DATE: 17-07-26
DESIGNED : A.O. REVISION DATE:
QA CHECK : A.O. 10-09-26

APPROVED BY:

RPEQ: 28316
NPER: 5358554
DATE: 10-09-26

ISSUE TYPE:
CONSTRUCTION

SHEET NUMBER:
STR700

SHEET SIZE: **A3** REVISION: **E**

PRINT IN COLOUR

SAMPLE PROJECT A - STRUCTURAL REV E - CURRENT - RECRUITMENT ASSESSMENT ONLY

TEST PROJECT USAGE

NOTE: THE DESIGN AND DETAILS SHOWN ON THESE DRAWINGS ARE APPLICABLE TO THIS PROJECT ONLY AND MAY NOT BE REPRODUCED IN WHOLE OR IN PART OR BE USED FOR ANY OTHER PROJECT OR PURPOSE WITHOUT THE WRITTEN PERMISSION OF WITH WHOM COPYRIGHT RESIDES.

REGULATED DESIGN RECORD

PROJECT ADDRESS:	
PROJECT TITLE:	MULTI DWELLING
CONSENT NO:	STR208 - 2023
BODY CORPORATE REG NO:	DEP0001320
DRAWING TITLE:	LEVEL 3 WALL LAYOUT PLAN
DRAWING NO:	STR701

REV	DATE DD.MM.YY	DESCRIPTION	DP FULL NAME	REG NO
E	10-09-26	ISSUED FOR CONSTRUCTIO		

LEGEND:


- DENOTES CONCRETE COLUMN/ WALL **OVER ONLY**
- DENOTES BRICK WALLS **OVER ONLY**
- DENOTES BLOCK WORK WALLS **OVER ONLY**
- DENOTES RITEK WALLS **OVER ONLY**
- DENOTES CONCRETE WALL/COLUMN **UNDER ONLY**
- DENOTES WET AREA WITH 2mm FALL
- DENOTES SLAB PENETRATION
- DENOTES STEP ON SLAB
- C00 DENOTES COLUMN MARK
- W00 DENOTES WALL MARK
- 000 DENOTES SLAB THICKNESS
- DENOTES EXTENT OF SLAB STEP

FOR STRUCTURAL NOTES REFER TO DRAWING STR00 SERIES

WALL SCHEDULE

FLOOR LEVEL	TYPE	DESCRIPTION	THK (mm)	VERT. REINF.	HORZ. REINF.	f'c
LEVEL 3	3W1	RITEK WALL	200	N12-250 E.F.	N12-250 E.F.	32 MPa
	3W2	RITEK WALL	200	N12-250 E.F.	N12-250 E.F.	32 MPa
	3W3	RITEK WALL	150	N12-250 E.F.	N12-250 E.F.	32 MPa

THIRD FLOOR SLAB: FRL 90/90/90

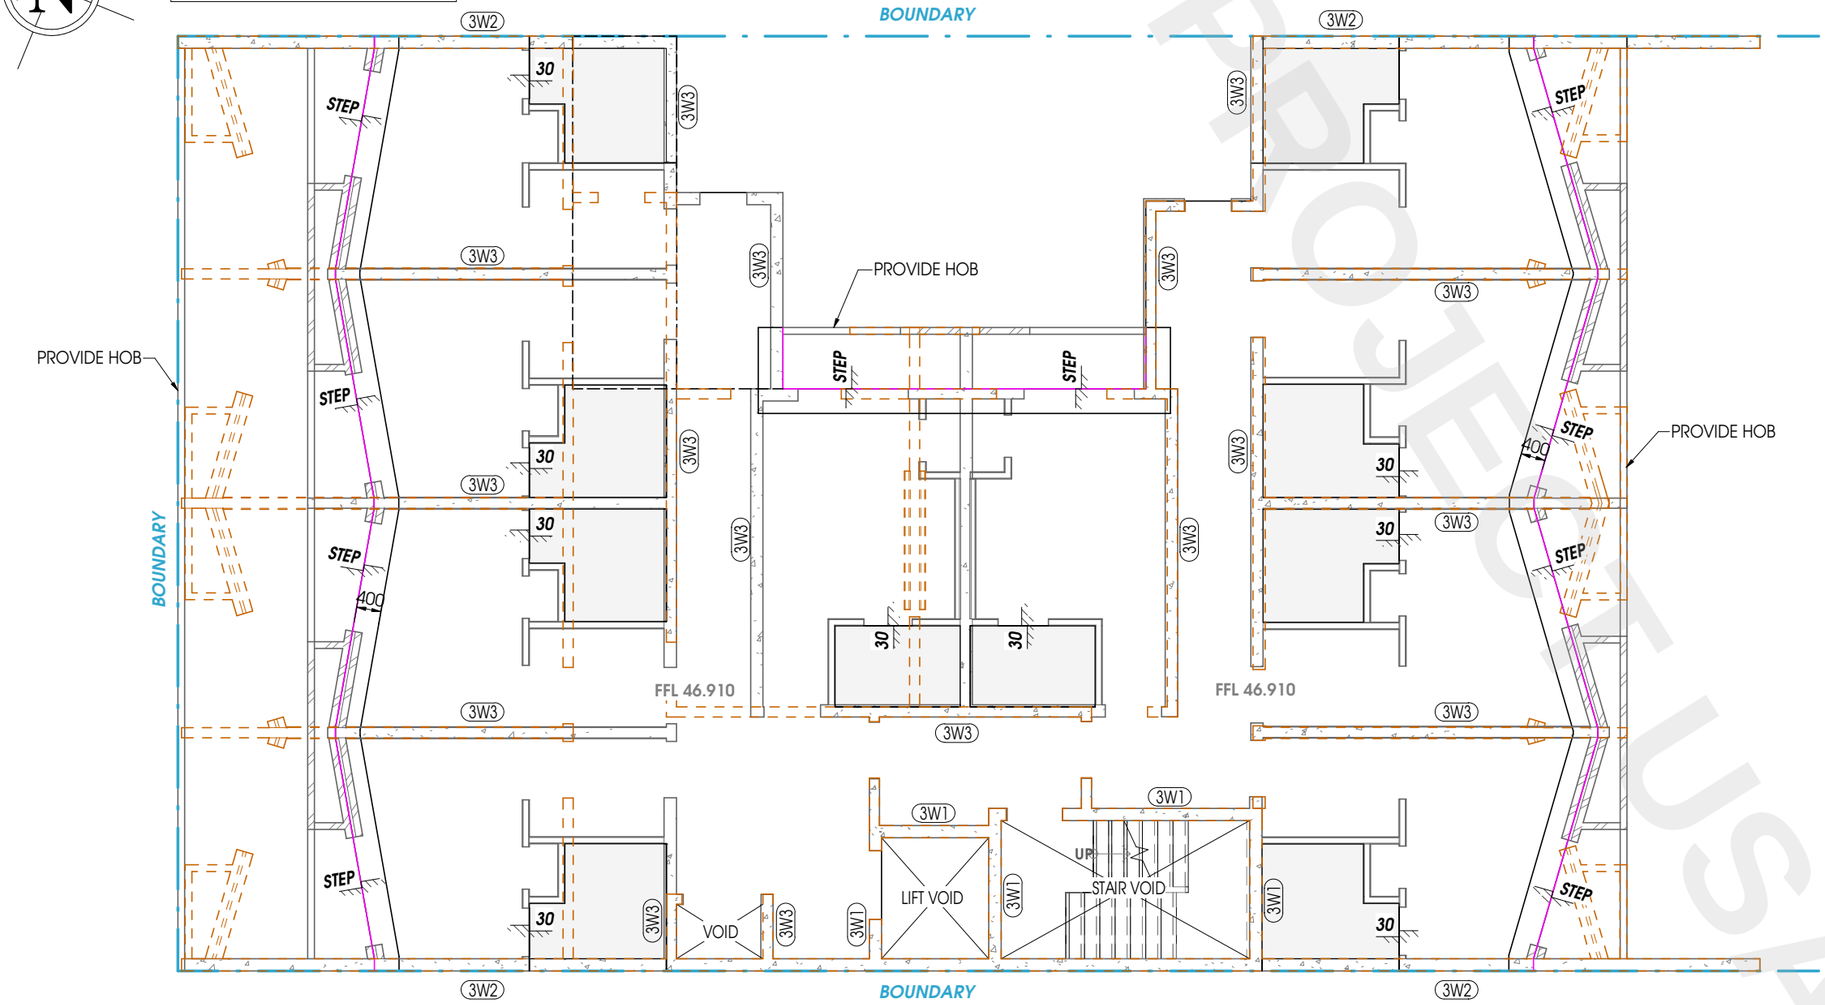

LEVEL 3 WALL LAYOUT PLAN

SCALE: 1 : 100

MODULAR ENGINEERS P/L

Structural Engineering | Civil Engineering
Stormwater Engineering | Flood Engineering
Traffic Engineering | Temporary works

ABN : 66 646 960 929
TEL. : 02 873 08473
MOB. : 04 208 98999
EMAIL :
WEBSITE :
ADDRESS :

CLIENT:

PROJECT TITLE:
MULTI DWELLING

SHEET NAME:
LEVEL 3 WALL LAYOUT PLAN

PROJECT NUMBER:
175-2026

INTERNAL REVISIONS:

ISSUE	DATE	DESCRIPTION	BY
E	10-09-26	ISSUED FOR CONSTRUCTION	D.A.
D	08-09-26	ISSUED FOR CONSTRUCTION	D.A.
C	24-08-26	ISSUED FOR PRELIMINARY	D.A.
B	21-08-26	ISSUED FOR PRELIMINARY	D.A.

AMENDMENTS

DRAWN : L.M. DATE: 17-07-26
DESIGNED : A.O. REVISION DATE:
QA CHECK : A.O. 10-09-26

APPROVED BY:

RPEQ: 28316
NPER: 5358554
DATE: 10-09-26

ISSUE TYPE:
CONSTRUCTION

SHEET NUMBER:
STR701

SHEET SIZE: **A3**
REVISION: **E**

PRINT IN COLOUR

SAMPLE PROJECT A - STRUCTURAL REV E - CURRENT - RECRUITMENT ASSESSMENT ONLY

TEST PROJECT USAGE ONLY

NOTE: THE DESIGN AND DETAILS SHOWN ON THESE DRAWINGS ARE APPLICABLE TO THIS PROJECT ONLY AND MAY NOT BE REPRODUCED IN WHOLE OR IN PART OR BE USED FOR ANY OTHER PROJECT OR PURPOSE WITHOUT THE WRITTEN PERMISSION OF WITH WHOM COPYRIGHT RESIDES.


REGULATED DESIGN RECORD

PROJECT ADDRESS:	
PROJECT TITLE:	MULTI DWELLING
CONSENT NO:	STR208 - 2023
BODY CORPORATE REG NO:	DEP0001320
DRAWING TITLE:	LEVEL 3 BOTTOM REINFORCEMENT PLAN
DRAWING NO:	STR710


REV	DATE DD.MM.YY	DESCRIPTION	DP FULL NAME	REG NO
E	10-09-26	ISSUED FOR CONSTRUCTIO		



BAR LAYING SEQUENCE

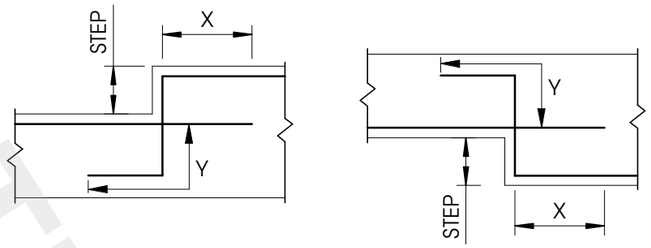

TYPICAL REINFORCEMENT LAPPING

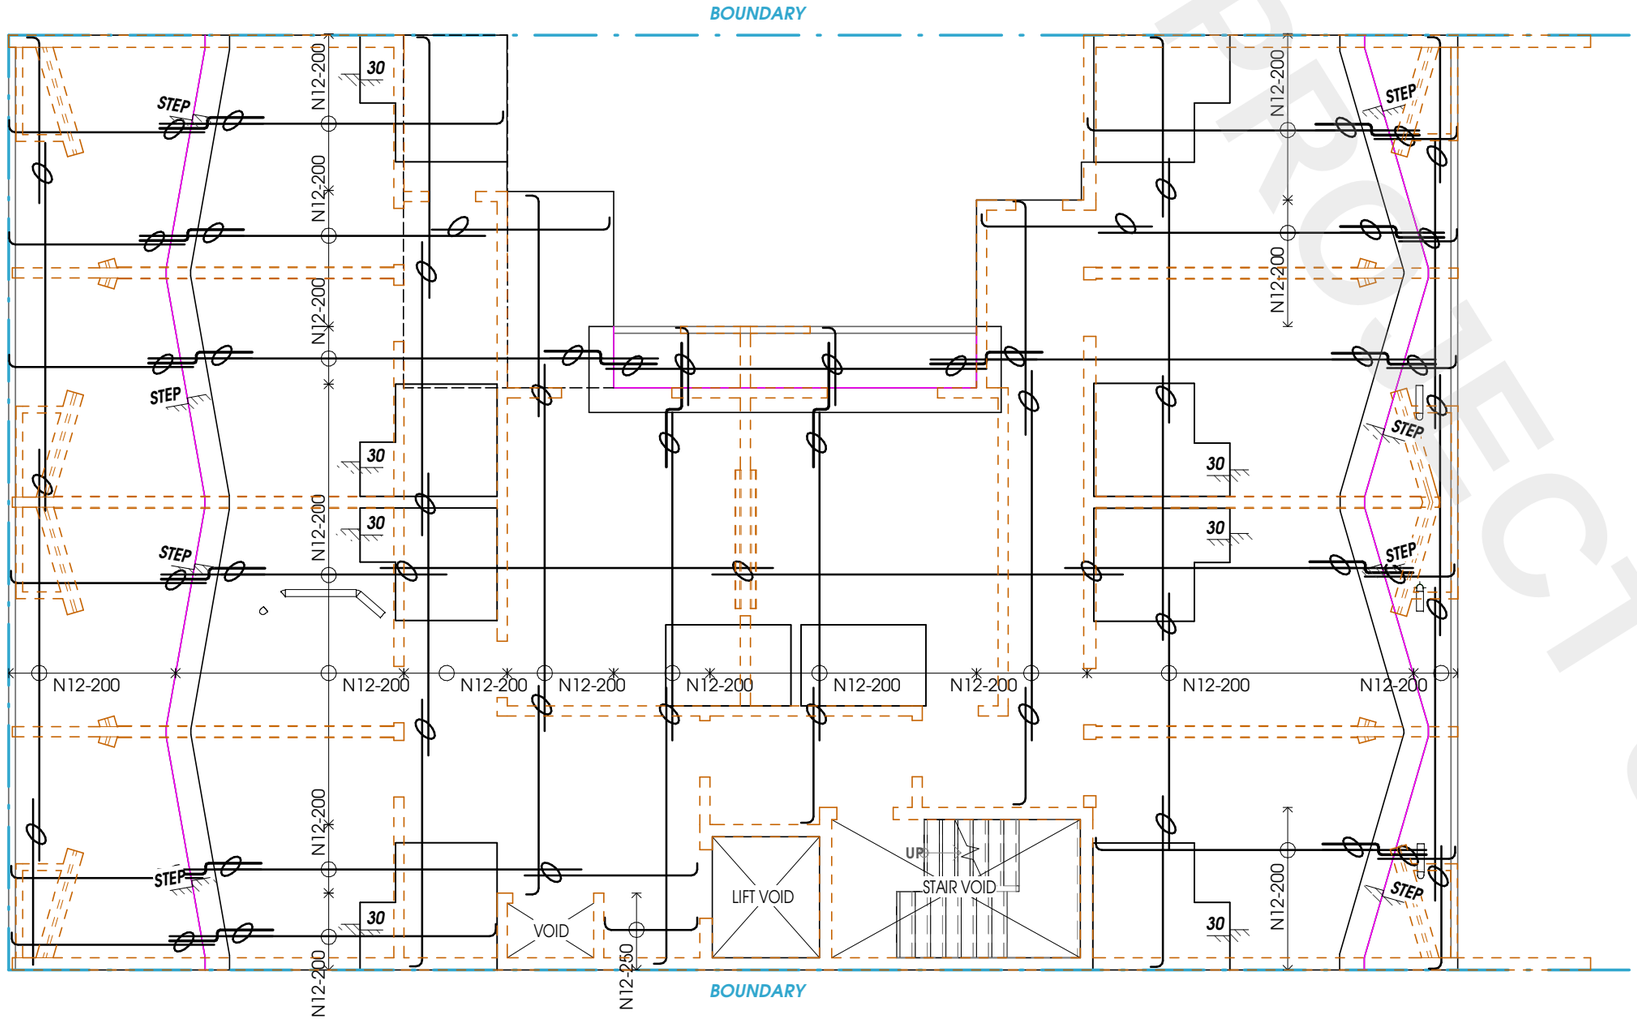
BOUNDARY
STEP
30
N12-200
N12-200
N12-200


REGULATED DESIGN RECORD

PROJECT ADDRESS:	
PROJECT TITLE:	MULTI DWELLING
CONSENT NO:	STR208 - 2023
BODY CORPORATE REG NO:	DEP0001320
DRAWING TITLE:	LEVEL 3 TOP REINFORCEMENT PLAN
DRAWING NO:	STR711


REV	DATE DD.MM.YY	DESCRIPTION	DP FULL NAME	REG NO
E	10-09-26	ISSUED FOR CONSTRUCTIO		



BAR LAYING SEQUENCE

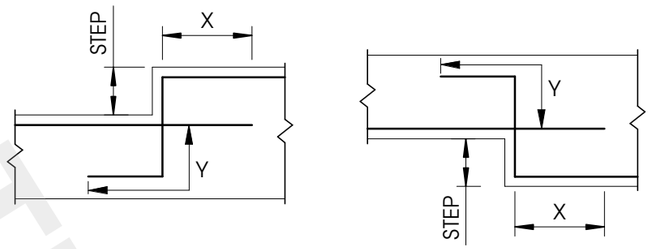

TYPICAL REINFORCEMENT LAPPING

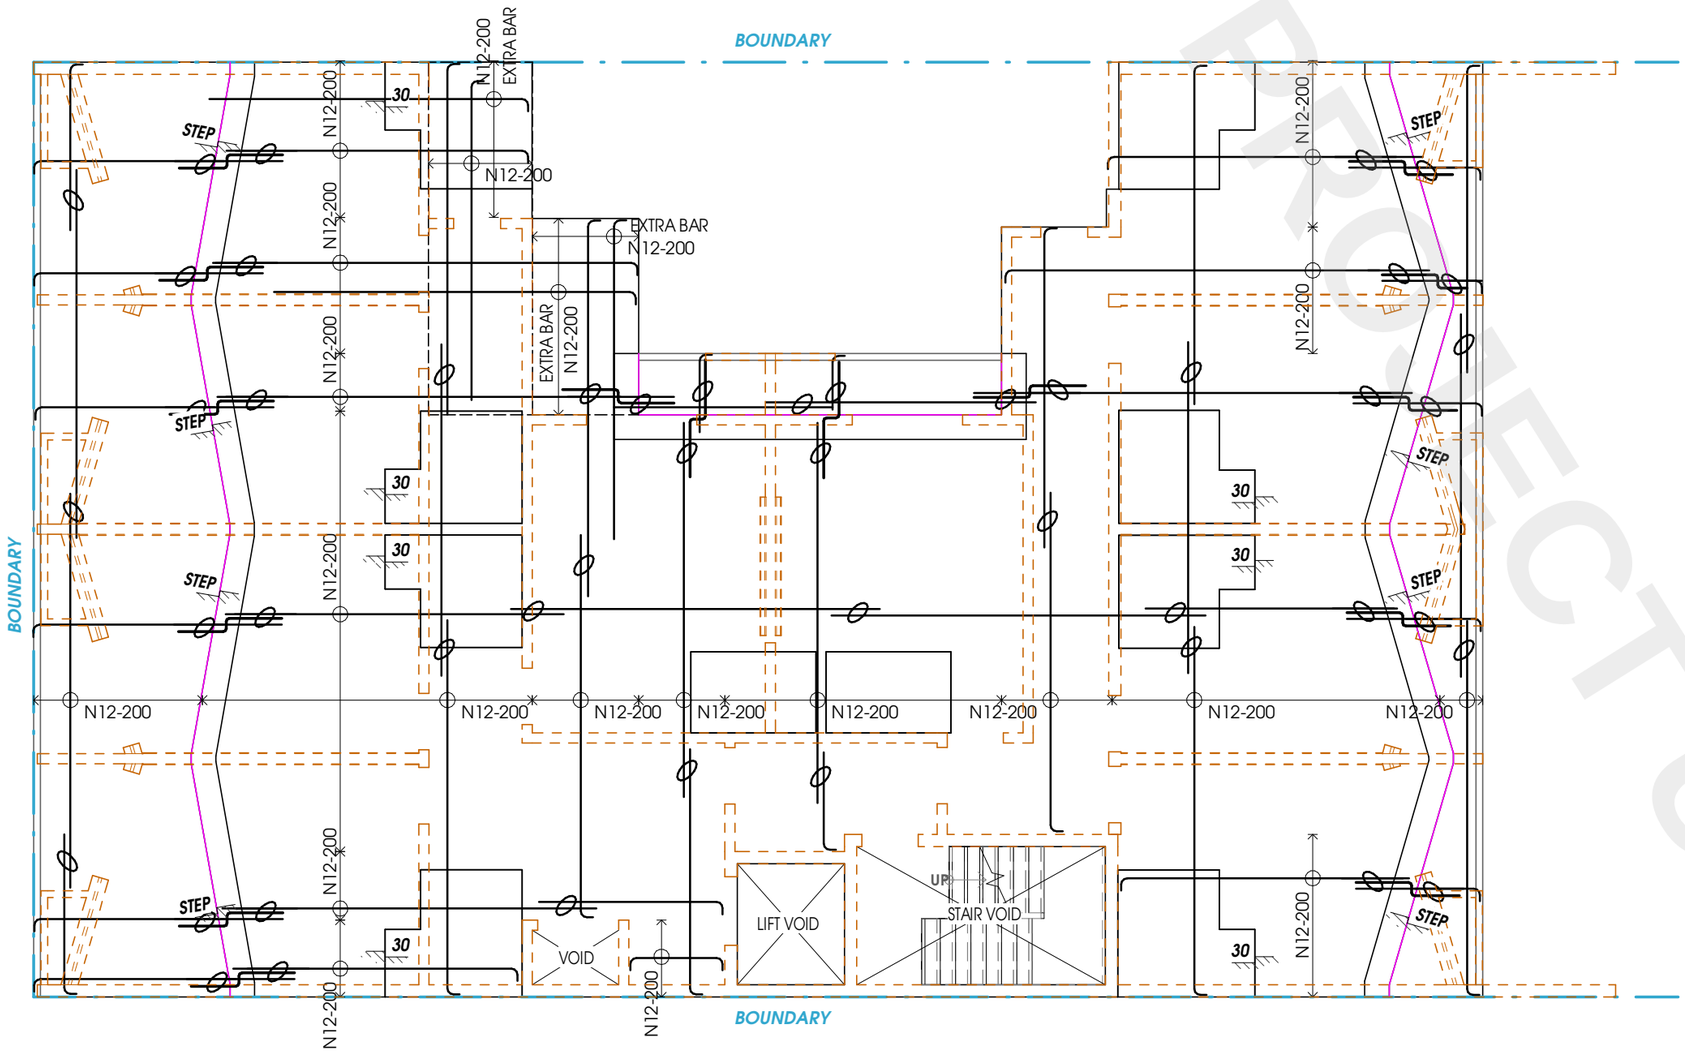


LEVEL 3 TOP REINFORCEMENT PLAN

SCALE: 1 : 100


NOTES:

SUSPENDED SLAB:


A. DRAWING TO BE READ IN CONJUNCTION WITH ARCHITECTURE DRAWINGS .
B. REFER TO ARCHITECTURAL DRAWINGS FOR ALL SETOUT, LEVELS, STEPS, FOLDS & FALLS ETC.
C. REFER TO STORMWATER DRAINAGE DRAWINGS FOR LOCATION OF PUMP WELL AND SUMP PITS.
D. ALL CONCRETE CYLINDERS TO BE STORED AND CURED ON SITE PRIOR TESTING TO AS3600.
E. CONCRETE SLAB (f'c)=32 MPa WITH A SLUMP OF 80MM.
F. AGGREGATE MINIMUM SIZE 20MM.
G. ALL BRICKS WALLS TO BE ARTICULATED, EXPANSION JOINT SPACING TO BE 6000mm
H. ALL EXPOSED SLABS TO BE WATERPROOFED WITH APPROVED SYSTEMS.
I. ACOUSTIC ENGINEER TO CHECK AND VERIFY ALL FLOOR SLAB FOR ACOUSTIC REQUIREMENTS IN ACCORDANCE WITH THE BCA REGULATIONS AND ADVISE ON ANY ACOUSTIC TREATMENT NEEDED TO SATISFY THE REGULATION.
J. FOR FOLD REINFORCEMENTS REFER TO SECTION S4 U.N.O.
K. ENSURE 50mm MINIMUM SPACING BETWEEN BARS.
L. PROVIDE ALL EXTRA REINFORCEMENT AS SHOWN ON PLAN.
M. PROVIDE 3N16 TOP AND BOTTOM AT THE PERIMETER OF THE SLAB.
N. SLAB REINFORCEMENT LAYING SEQUENCE U.N.O.:

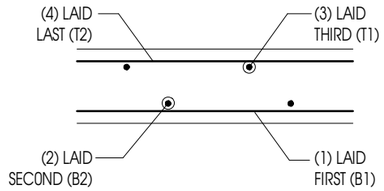

O. TYPICAL TRIMMERS AT PENETRATION/OPENING DETAIL:

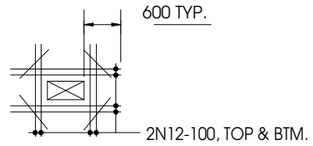

P. TYPICAL TRIMMERS AT RE-ENTRANT CORNERS:

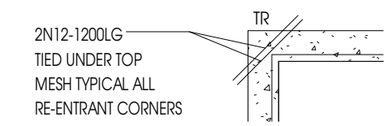

Q. PROVIDE TOP & BOTTOM BARS ON ALL WALL OPENINGS AS PER THE SCHEDULE BELOW:

LENGTH OF OPENING (m)	BOTTOM BAR	TOP BAR
1.0 - 1.8	2N16	2N16
1.8 - 2.5	2N20	2N20
2.5 - 3.5	2N24	2N24

R. PROVIDE ADEQUATE OVERLAP AT MESH JOINTS AS FOLLOWS :
- 400 MIN. LAP FOR SL82 MESH
- 500 MIN. LAP FOR SL92 MESH
- 600 MIN. LAP FOR SL102 MESH

S. PROVIDE ADEQUATE OVERLAP FOR BARS AS FOLLOWS:

BAR(X-Y)	MIN LAPPING REQUIRED
N12	500 mm
N16	800 mm
N20	1000 mm
N24	1200 mm
N28	1400 mm

MODULAR ENGINEERS P/L
Structural Engineering | Civil Engineering
Stormwater Engineering | Flood Engineering
Traffic Engineering | Temporary works
ABN : 66 646 960 929
TEL. : 02 873 08473
MOB. : 04 208 98999
EMAIL :
WEBSITE :
ADDRESS :

CLIENT:

PROJECT TITLE:
MULTI DWELLING

SHEET NAME:
LEVEL 3 TOP REINFORCEMENT PLAN

PROJECT NUMBER:
175-2026

INTERNAL REVISIONS:

ISSUE	DATE	DESCRIPTION	BY
E	10-09-26	ISSUED FOR CONSTRUCTION	D.A.
D	08-09-26	ISSUED FOR CONSTRUCTION	D.A.
C	24-08-26	ISSUED FOR PRELIMINARY	D.A.
B	21-08-26	ISSUED FOR PRELIMINARY	D.A.

AMENDMENTS

DRAWN : L.M. DATE: 17-07-26
DESIGNED : A.O. REVISION DATE:
QA CHECK : A.O. 10-09-26
APPROVED BY:

RPEQ: 28316
NPER: 5358554
DATE: 10-09-26

ISSUE TYPE:
CONSTRUCTION

SHEET NUMBER:
STR711

SHEET SIZE: **A3**
REVISION: **E**

PRINT IN COLOUR

SAMPLE PROJECT A - STRUCTURAL REV E - CURRENT - RECRUITMENT ASSESSMENT ONLY
TEST PROJECT ONLY
NOTE: THE DESIGN AND DETAILS SHOWN ON THESE DRAWINGS ARE APPLICABLE TO THIS PROJECT ONLY AND MAY NOT BE REPRODUCED IN WHOLE OR IN PART OR BE USED FOR ANY OTHER PROJECT OR PURPOSE WITHOUT THE WRITTEN PERMISSION OF WITH WHOM COPYRIGHT RESIDES.

REGULATED DESIGN RECORD

PROJECT ADDRESS:			
PROJECT TITLE:	MULTI DWELLING		
CONSENT NO:	STR208 - 2023	BODY CORPORATE REG NO:	DEP0001320
DRAWING TITLE:	LEVEL 3 LOADING PLAN	DRAWING NO:	STR720

REV	DATE DD.MM.YY	DESCRIPTION	DP FULL NAME	REG NO
E	10-09-26	ISSUED FOR CONSTRUCTIO		




LOADING TABLE
WHERE APPLICABLE

MARK	COLOUR	AREA	SUPERIMPOSED DEAD LOAD	LIVE LOAD
1		RESIDENTIAL	1.5 kPa	1.5 kPa
2		PARKING	0.5 kPa EXC. FALLS AND GRADING	2.5 kPa
3		STORAGE	0.5 kPa	5.0 kPa
4		CORRIDOR / STAIR	1.5 kPa	4.0 kPa
5		LOBBY	1.5 kPa	4.0 kPa
6		BALCONY	1.5 kPa	2.0 kPa
7		MECH ROOM,FAN ROOM	1.5 kPa	5.0 kPa
8		COMMON AREA	1.5 kPa	4.0 kPa
9		LIGHT WEIGHT ROOF	0.5 kPa	0.5 kPa

LOADING TABLE
WHERE APPLICABLE

MARK	COLOUR	AREA	SUPERIMPOSED DEAD LOAD	LIVE LOAD
10		WASTE ROOM	0.5 kPa	5.0 kPa
11		RETAILS	1.5 kPa	4.0 kPa
12		ROOF (NON-TRAFFICABLE)	2.0 kPa	1.5 kPa
13		LANDSCAPE 400mm SOIL MAX.	4.0 kPa	1.5 kPa
14		LANDSCAPE 1000mm SOIL MAX.	10.0 kPa	1.5 kPa
15		SUBSTATION	1.0 kPa	2.0 kPa
16		LOADING DECK	1.0 kPa	10.0 kPa
17		PEBBLES	4.0 kPa	1.5 kPa
18		OSD TANK/ WATER STORAGE TANK	10.0 kPa FOR EVERY METRE HEIGHT OF WATER	

DEFLECTION NOTES (LONG-TERM)
- LONG-TERM DEFLECTION IS BASED ON DL + 0.3LL FOR SUSTAINED LOADS.
- CREEP FACTOR Λ = 2.0 TO 3.0 APPLIED PER AS3600.
- TOTAL DEFLECTION: Δ TOTAL=Δ IMMEDIATE + Λ × Δ SUSTAINED
- IMMEDIATE DEFLECTION: DL + LL
- LONG-TERM DEFLECTION: DL + 0.3LL × Λ

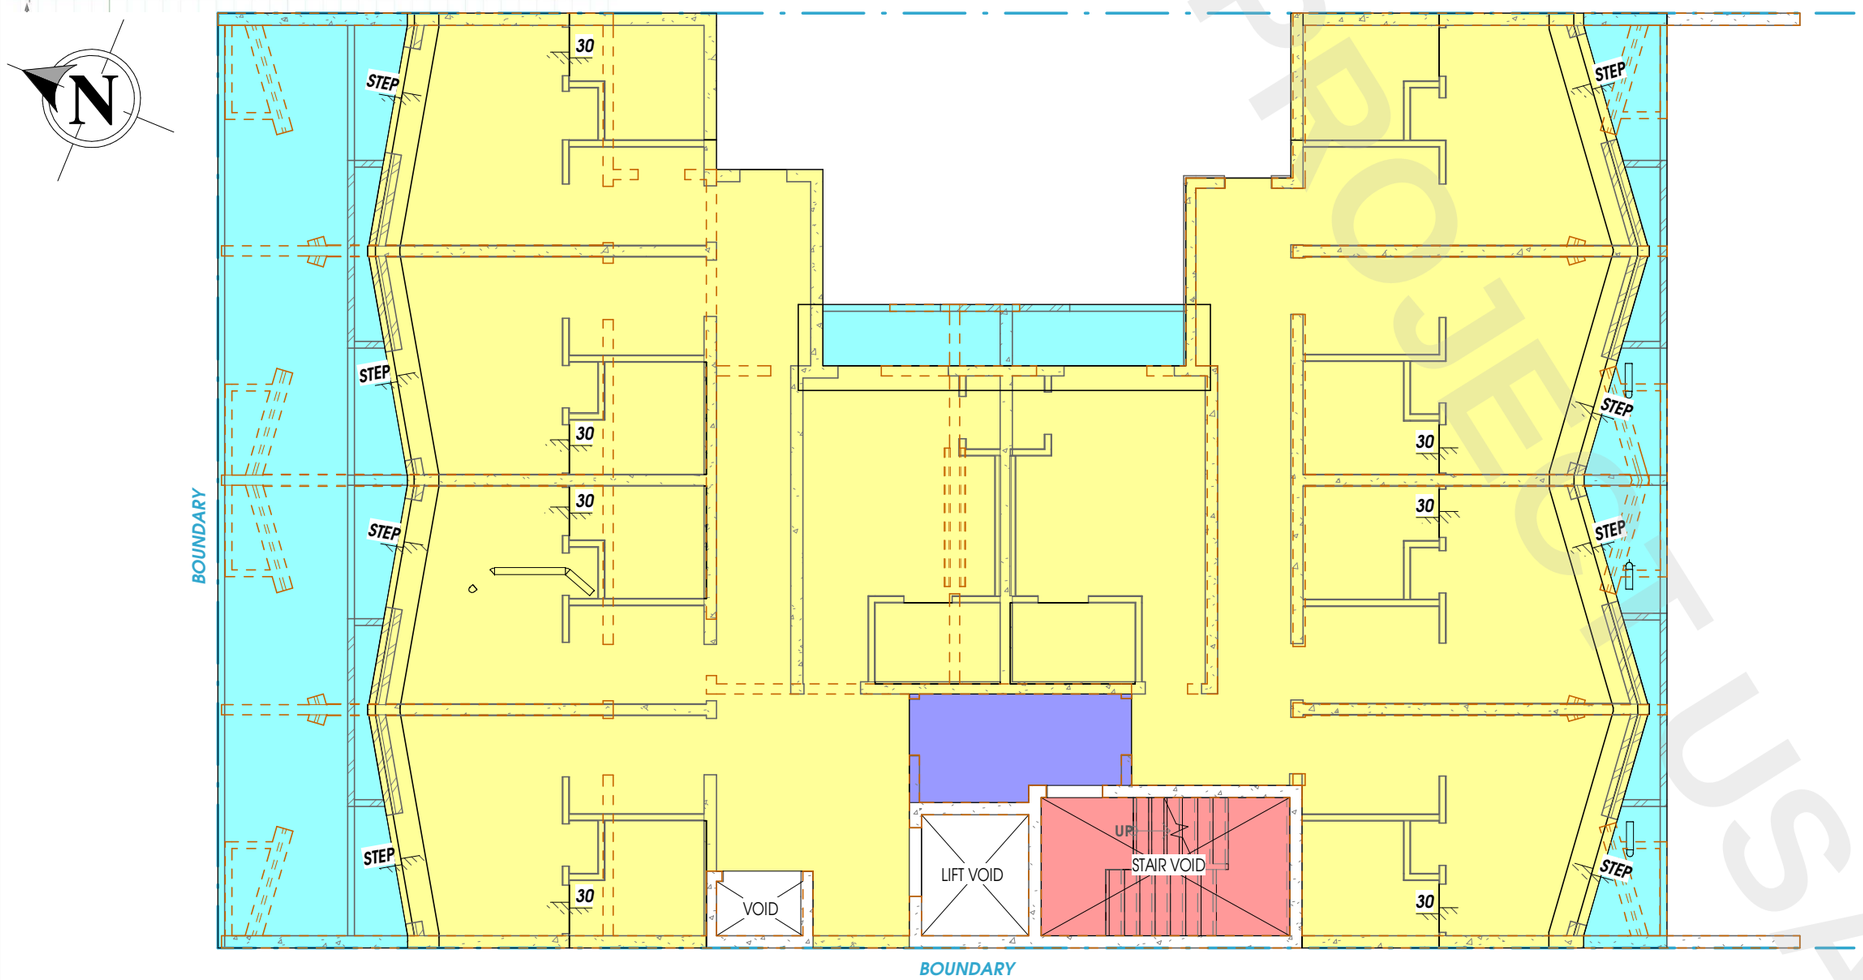

LEVEL 3 LOADING PLAN
SCALE: 1 : 100

PRINT IN COLOUR

MODULAR ENGINEERS P/L
Structural Engineering | Civil Engineering
Stormwater Engineering | Flood Engineering
Traffic Engineering | Temporary works
ABN : 66 646 960 929
TEL. : 02 873 08473
MOB. : 04 208 98999
EMAIL :
WEBSITE :
ADDRESS :

CLIENT:

PROJECT TITLE:
MULTI DWELLING

SHEET NAME:
LEVEL 3 LOADING PLAN

PROJECT NUMBER:
175-2026

INTERNAL REVISIONS:

ISSUE	DATE	DESCRIPTION	BY
E	10-09-26	ISSUED FOR CONSTRUCTION	D.A.
D	08-09-26	ISSUED FOR CONSTRUCTION	D.A.
C	24-08-26	ISSUED FOR PRELIMINARY	D.A.
B	21-08-26	ISSUED FOR PRELIMINARY	D.A.

AMENDMENTS

DRAWN : L.M. DATE: 17-07-26
DESIGNED : A.O. REVISION DATE:
QA CHECK : A.O. 10-09-26
APPROVED BY:

RPEQ: 28316
NPER: 5358554
DATE: 10-09-26

ISSUE TYPE:
CONSTRUCTION

SHEET NUMBER:
STR720

SHEET SIZE: **A3** REVISION: **E**


SAMPLE PROJECT A - STRUCTURAL REVE - CURRENT - RECRUITMENT ASSESSMENT ONLY
TEST PROJECT USAGE ONLY

NOTE: THE DESIGN AND DETAILS SHOWN ON THESE DRAWINGS ARE APPLICABLE TO THIS PROJECT ONLY AND MAY NOT BE REPRODUCED IN WHOLE OR IN PART OR BE USED FOR ANY OTHER PROJECT OR PURPOSE WITHOUT THE WRITTEN PERMISSION OF WITH WHOM COPYRIGHT RESIDES.


REGULATED DESIGN RECORD

PROJECT ADDRESS:	
PROJECT TITLE:	MULTI DWELLING
CONSENT NO:	STR208 - 2023
BODY CORPORATE REG NO:	DEP0001320
DRAWING TITLE:	SECTION AND DETAILS
DRAWING NO:	STR730

REV	DATE DD.MM.YY	DESCRIPTION	DP FULL NAME	REG NO
E	10-09-26	ISSUED FOR CONSTRUCTIO		

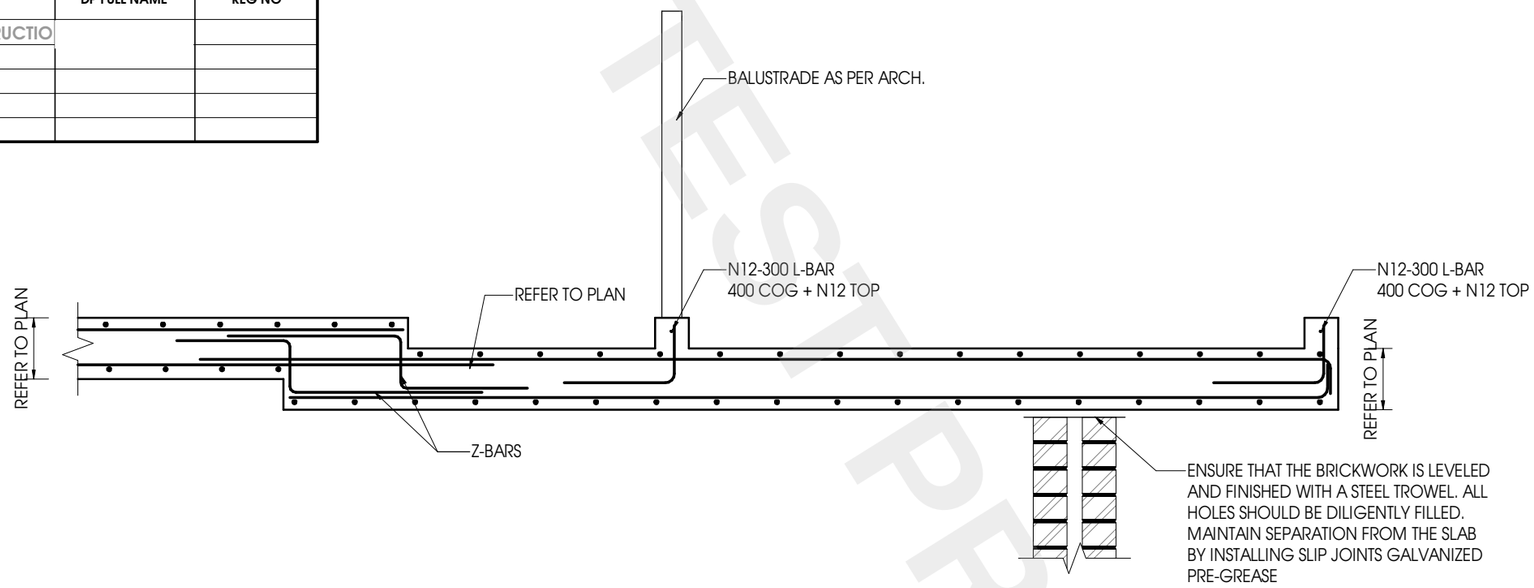

SECTION G
NOT TO SCALE STR700

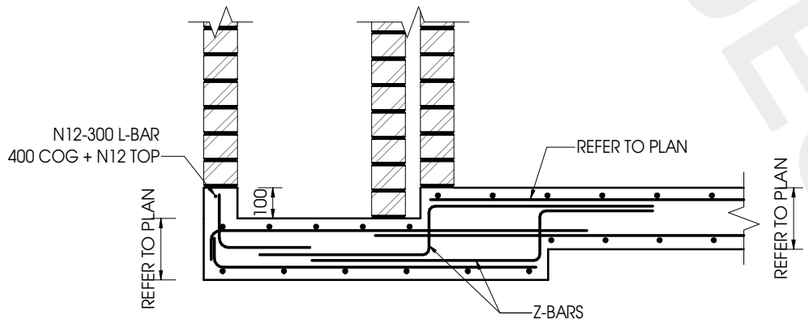

SECTION H
NOT TO SCALE STR700

MODULAR ENGINEERS P/L

Structural Engineering | Civil Engineering
Stormwater Engineering | Flood Engineering
Traffic Engineering | Temporary works

ABN : 66 646 960 929
TEL. : 02 873 08473
MOB. : 04 208 98999
EMAIL :
WEBSITE :
ADDRESS :

CLIENT:

PROJECT TITLE:
MULTI DWELLING

SHEET NAME:
SECTION AND DETAILS

PROJECT NUMBER:
175-2026

INTERNAL REVISIONS:

ISSUE	DATE	DESCRIPTION	BY
E	10-09-26	ISSUED FOR CONSTRUCTION	D.A.
D	08-09-26	ISSUED FOR CONSTRUCTION	D.A.
C	24-08-26	ISSUED FOR PRELIMINARY	D.A.
B	21-08-26	ISSUED FOR PRELIMINARY	D.A.

AMENDMENTS

DRAWN : L.M. DATE: 17-07-26
DESIGNED : A.O. REVISION DATE:
QA CHECK : A.O. 10-09-26

APPROVED BY:

RPEQ: 28316
NPER: 5358554
DATE: 10-09-26

ISSUE TYPE:
CONSTRUCTION

SHEET NUMBER:
STR730

SHEET SIZE: **A3** REVISION: **E**

PRINT IN COLOUR

SAMPLE PROJECT A - STRUCTURAL REV E - CURRENT - RECRUITMENT ASSESSMENT ONLY

TEST PROJECT USAGE ONLY

NOTE: THE DESIGN AND DETAILS SHOWN ON THESE DRAWINGS ARE APPLICABLE TO THIS PROJECT ONLY AND MAY NOT BE REPRODUCED IN WHOLE OR IN PART OR BE USED FOR ANY OTHER PROJECT OR PURPOSE WITHOUT THE WRITTEN PERMISSION OF WITH WHOM COPYRIGHT RESIDES.

REGULATED DESIGN RECORD


PROJECT ADDRESS:			
PROJECT TITLE:	MULTI DWELLING		
CONSENT NO:	STR208 - 2023	BODY CORPORATE REG NO:	DEP0001320
DRAWING TITLE:	LEVEL 4 FLOOR PLAN	DRAWING NO:	STR800

REV	DATE DD.MM.YY	DESCRIPTION	DP FULL NAME	REG NO
E	10-09-26	ISSUED FOR CONSTRUCTIO		

LEGEND:

- DENOTES CONCRETE COLUMN/ WALL **OVER ONLY**
- DENOTES BRICK WALLS **OVER ONLY**
- DENOTES BLOCK WORK WALLS **OVER ONLY**
- DENOTES RITEK WALLS **OVER ONLY**
- DENOTES CONCRETE WALL/COLUMN **UNDER ONLY**
- DENOTES WET AREA WITH 2mm FALL
- DENOTES SLAB PENETRATION
- DENOTES STEP ON SLAB
- C00 DENOTES COLUMN MARK
- W00 DENOTES WALL MARK
- 000 DENOTES SLAB THICKNESS
- DENOTES EXTENT OF SLAB STEP

FOR STRUCTURAL NOTES REFER TO DRAWING STR00 SERIES

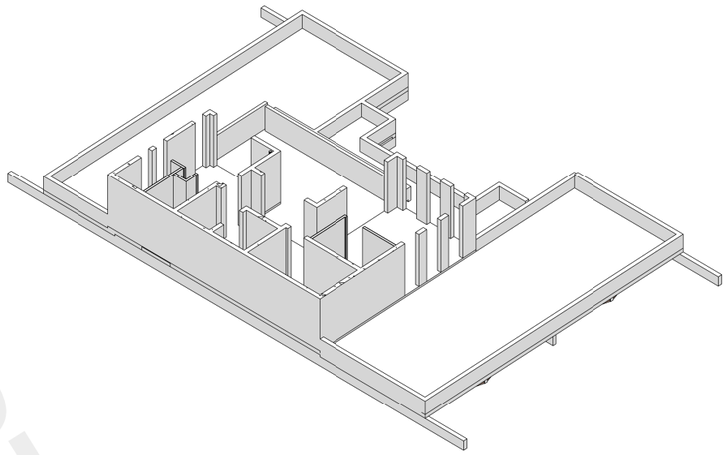


NOTES:

SUSPENDED SLAB:

A. DRAWING TO BE READ IN CONJUNCTION WITH ARCHITECTURE DRAWINGS .
B. REFER TO ARCHITECTURAL DRAWINGS FOR ALL SETOUT, LEVELS, STEPS, FOLDS & FALLS ETC.
C. REFER TO STORMWATER DRAINAGE DRAWINGS FOR LOCATION OF PUMP WELL AND SUMP PITS.
D. ALL CONCRETE CYLINDERS TO BE STORED AND CURED ON SITE PRIOR TESTING TO AS3600.
E. CONCRETE SLAB (f'c)=32 MPa WITH A SLUMP OF 80MM.
F. AGGREGATE MINIMUM SIZE 20MM.
G. ALL BRICKS WALLS TO BE ARTICULATED, EXPANSION JOINT SPACING TO BE 6000mm
H. ALL EXPOSED SLABS TO BE WATERPROOFED WITH APPROVED SYSTEMS.
I. ACOUSTIC ENGINEER TO CHECK AND VERIFY ALL FLOOR SLAB FOR ACOUSTIC REQUIREMENTS IN ACCORDANCE WITH THE BCA REGULATIONS AND ADVISE ON ANY ACOUSTIC TREATMENT NEEDED TO SATISFY THE REGULATION.
J. FOR FOLD REINFORCEMENTS REFER TO TYPICAL SECTION U.N.O.

FOURTH FLOOR SLAB: FRL 90/90/90

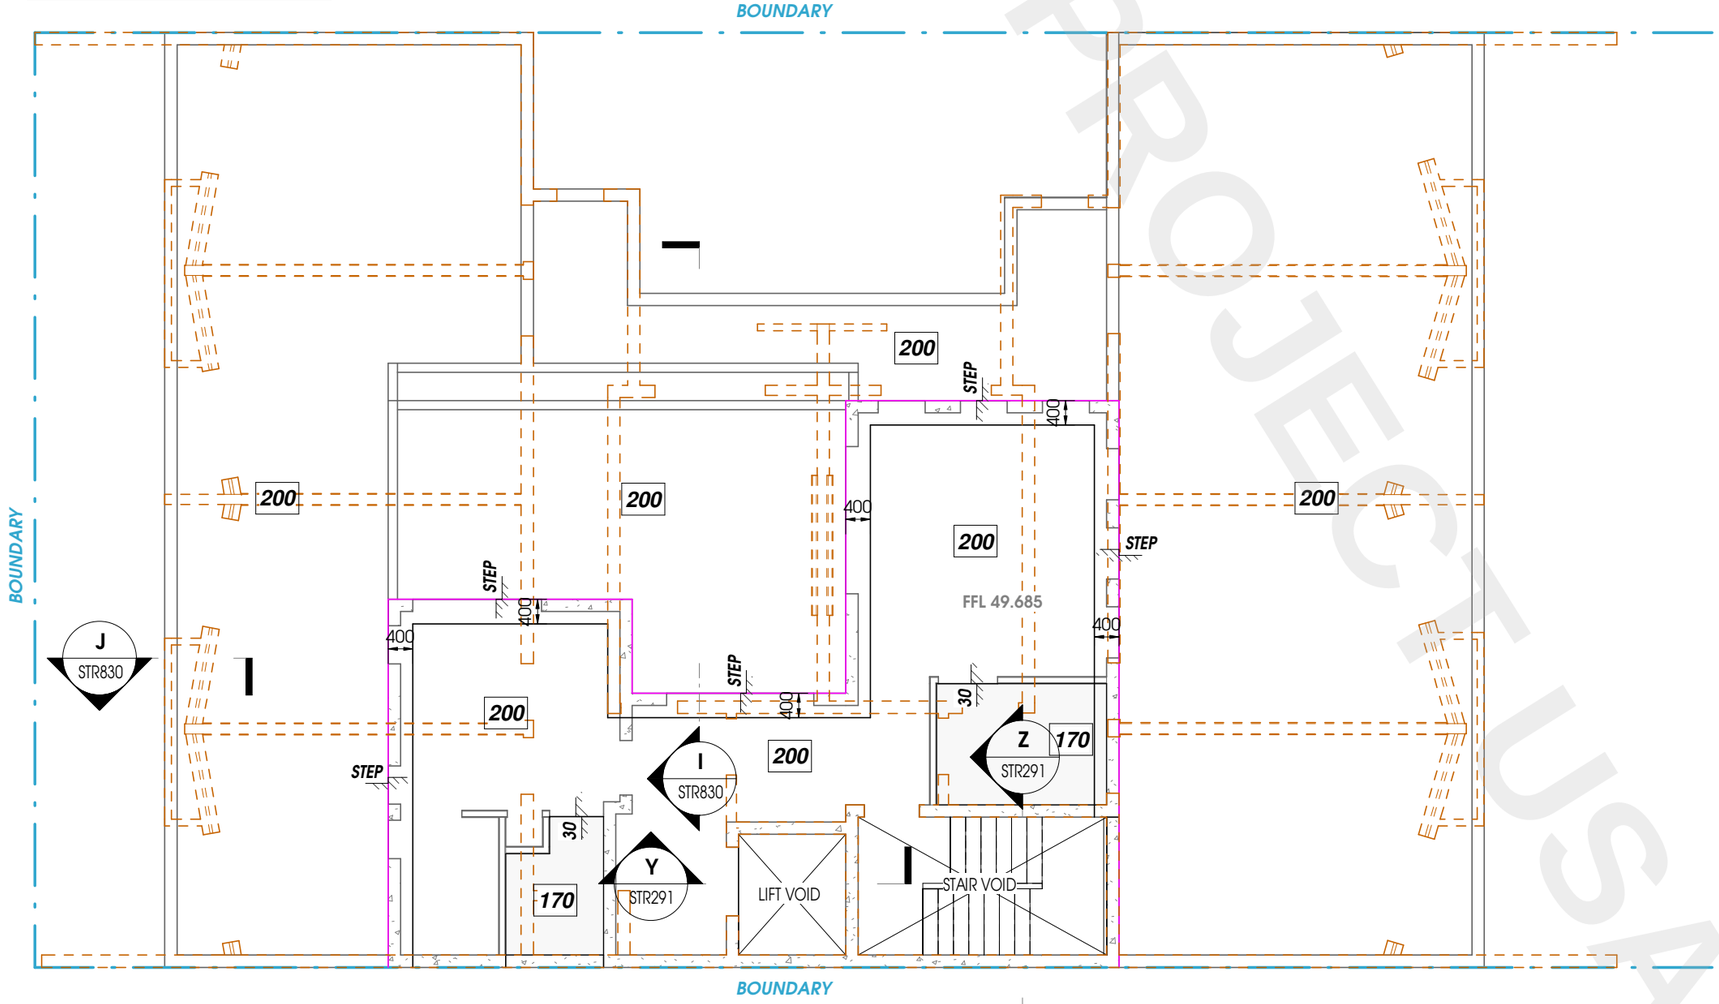

LEVEL 4 SUSPENDED CONCRETE SLAB PLAN

SCALE: 1 : 100

MODULAR ENGINEERS P/L

Structural Engineering | Civil Engineering
Stormwater Engineering | Flood Engineering
Traffic Engineering | Temporary works

ABN : 66 646 960 929
TEL. : 02 873 08473
MOB. : 04 208 98999
EMAIL :
WEBSITE :
ADDRESS :

CLIENT:

PROJECT TITLE:
MULTI DWELLING

SHEET NAME:
LEVEL 4 FLOOR PLAN

PROJECT NUMBER:
175-2026

INTERNAL REVISIONS:

ISSUE	DATE	DESCRIPTION	BY
E	10-09-26	ISSUED FOR CONSTRUCTION	D.A.
D	08-09-26	ISSUED FOR CONSTRUCTION	D.A.
C	24-08-26	ISSUED FOR PRELIMINARY	D.A.
B	21-08-26	ISSUED FOR PRELIMINARY	D.A.

AMENDMENTS

DRAWN : L.M. DATE: 17-07-26
DESIGNED : A.O. REVISION DATE:
QA CHECK : A.O. 10-09-26

APPROVED BY:

RPEQ: 28316
NPER: 5358554
DATE: 10-09-26

ISSUE TYPE:
CONSTRUCTION

SHEET NUMBER:
STR800

SHEET SIZE: **A3** REVISION: **E**

PRINT IN COLOUR

SAMPLE PROJECT A - STRUCTURAL REV E - CURRENT - RECRUITMENT ASSESSMENT ONLY

TEST PROJECT USAGE

NOTE: THE DESIGN AND DETAILS SHOWN ON THESE DRAWINGS ARE APPLICABLE TO THIS PROJECT ONLY AND MAY NOT BE REPRODUCED IN WHOLE OR IN PART OR BE USED FOR ANY OTHER PROJECT OR PURPOSE WITHOUT THE WRITTEN PERMISSION OF WITH WHOM COPYRIGHT RESIDES.

REGULATED DESIGN RECORD

PROJECT ADDRESS:	
PROJECT TITLE:	MULTI DWELLING
CONSENT NO:	STR208 - 2023
BODY CORPORATE REG NO:	DEP0001320
DRAWING TITLE:	LEVEL 4 WALL LAYOUT PLAN
DRAWING NO:	STR801

REV	DATE DD.MM.YY	DESCRIPTION	DP FULL NAME	REG NO
E	10-09-26	ISSUED FOR CONSTRUCTIO		

LEGEND:


- DENOTES CONCRETE COLUMN/ WALL **OVER ONLY**
- DENOTES BRICK WALLS **OVER ONLY**
- DENOTES BLOCK WORK WALLS **OVER ONLY**
- DENOTES RITEK WALLS **OVER ONLY**
- DENOTES CONCRETE WALL/COLUMN **UNDER ONLY**
- DENOTES WET AREA WITH 2mm FALL
- DENOTES SLAB PENETRATION
- DENOTES STEP ON SLAB
- C00 DENOTES COLUMN MARK
- W00 DENOTES WALL MARK
- 000 DENOTES SLAB THICKNESS
- DENOTES EXTENT OF SLAB STEP

FOR STRUCTURAL NOTES REFER TO DRAWING STR00 SERIES

WALL SCHEDULE

FLOOR LEVEL	TYPE	DESCRIPTION	THK (mm)	VERT. REINF.	HORZ. REINF.	f'c
LEVEL 4	4W1	RITEK WALL	200	N12-300 E.F.	N12-300 E.F.	32 MPa

FOURTH FLOOR SLAB: FRL 90/90/90

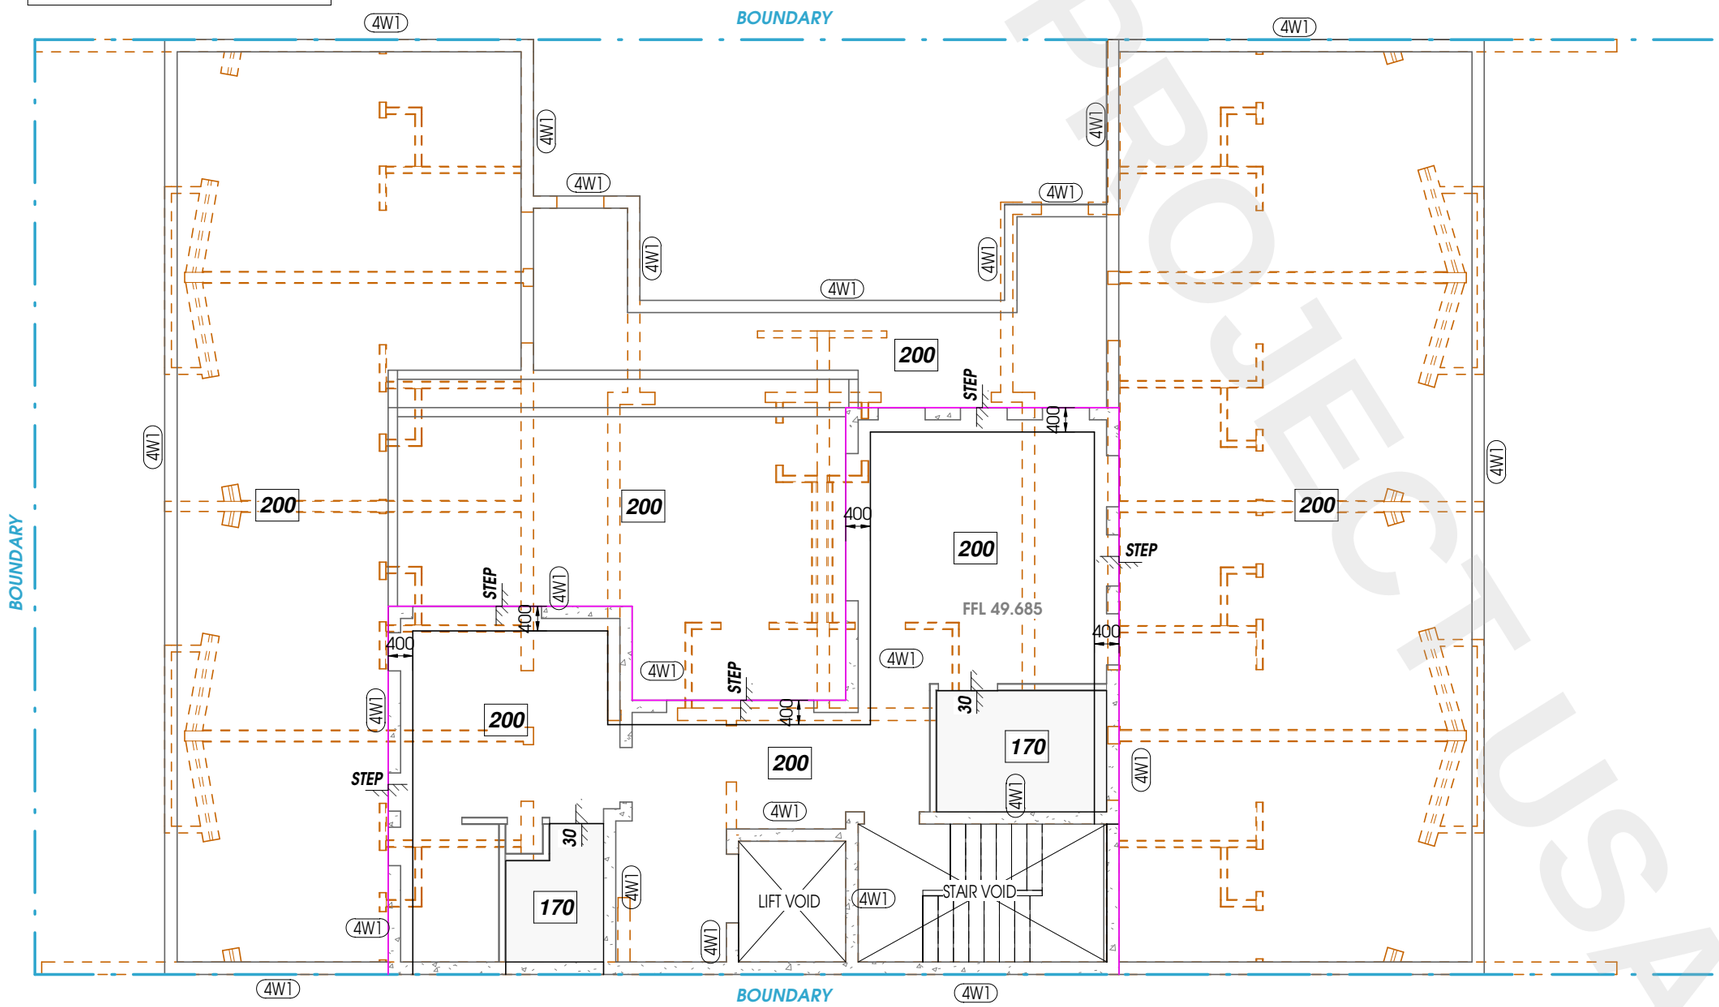

LEVEL 4 WALL LAYOUT PLAN

SCALE: 1 : 100

MODULAR ENGINEERS P/L

Structural Engineering | Civil Engineering
Stormwater Engineering | Flood Engineering
Traffic Engineering | Temporary works

ABN : 66 646 960 929
TEL. : 02 873 08473
MOB. : 04 208 98999
EMAIL :
WEBSITE :
ADDRESS :

CLIENT:

PROJECT TITLE:
MULTI DWELLING

SHEET NAME:
LEVEL 4 WALL LAYOUT PLAN

PROJECT NUMBER:
175-2026

INTERNAL REVISIONS:

ISSUE	DATE	DESCRIPTION	BY
E	10-09-26	ISSUED FOR CONSTRUCTION	D.A.
D	08-09-26	ISSUED FOR CONSTRUCTION	D.A.
C	24-08-26	ISSUED FOR PRELIMINARY	D.A.
B	21-08-26	ISSUED FOR PRELIMINARY	D.A.

AMENDMENTS

DRAWN : L.M. DATE: 17-07-26
DESIGNED : A.O. REVISION DATE:
QA CHECK : A.O. 10-09-26

APPROVED BY:

RPEQ: 28316
NPER: 5358554
DATE: 10-09-26

ISSUE TYPE:
CONSTRUCTION

SHEET NUMBER:
STR801

SHEET SIZE: **A3** REVISION: **E**

PRINT IN COLOUR

SAMPLE PROJECT A - STRUCTURAL REV E - CURRENT - RECRUITMENT ASSESSMENT ONLY

TEST PROJECT USAGE

NOTE: THE DESIGN AND DETAILS SHOWN ON THESE DRAWINGS ARE APPLICABLE TO THIS PROJECT ONLY AND MAY NOT BE REPRODUCED IN WHOLE OR IN PART OR BE USED FOR ANY OTHER PROJECT OR PURPOSE WITHOUT THE WRITTEN PERMISSION OF WITH WHOM COPYRIGHT RESIDES.


REGULATED DESIGN RECORD

PROJECT ADDRESS:	
PROJECT TITLE:	MULTI DWELLING
CONSENT NO:	STR208 - 2023
BODY CORPORATE REG NO:	DEP0001320
DRAWING TITLE:	LEVEL 4 BOTTOM REINFORCEMENT PLAN
DRAWING NO:	STR810


REV	DATE DD.MM.YY	DESCRIPTION	DP FULL NAME	REG NO
E	10-09-26	ISSUED FOR CONSTRUCTIO		



BAR LAYING SEQUENCE

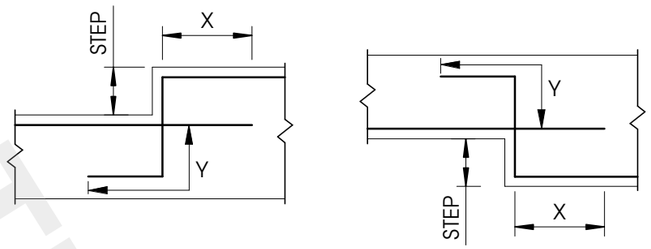

TYPICAL REINFORCEMENT LAPPING

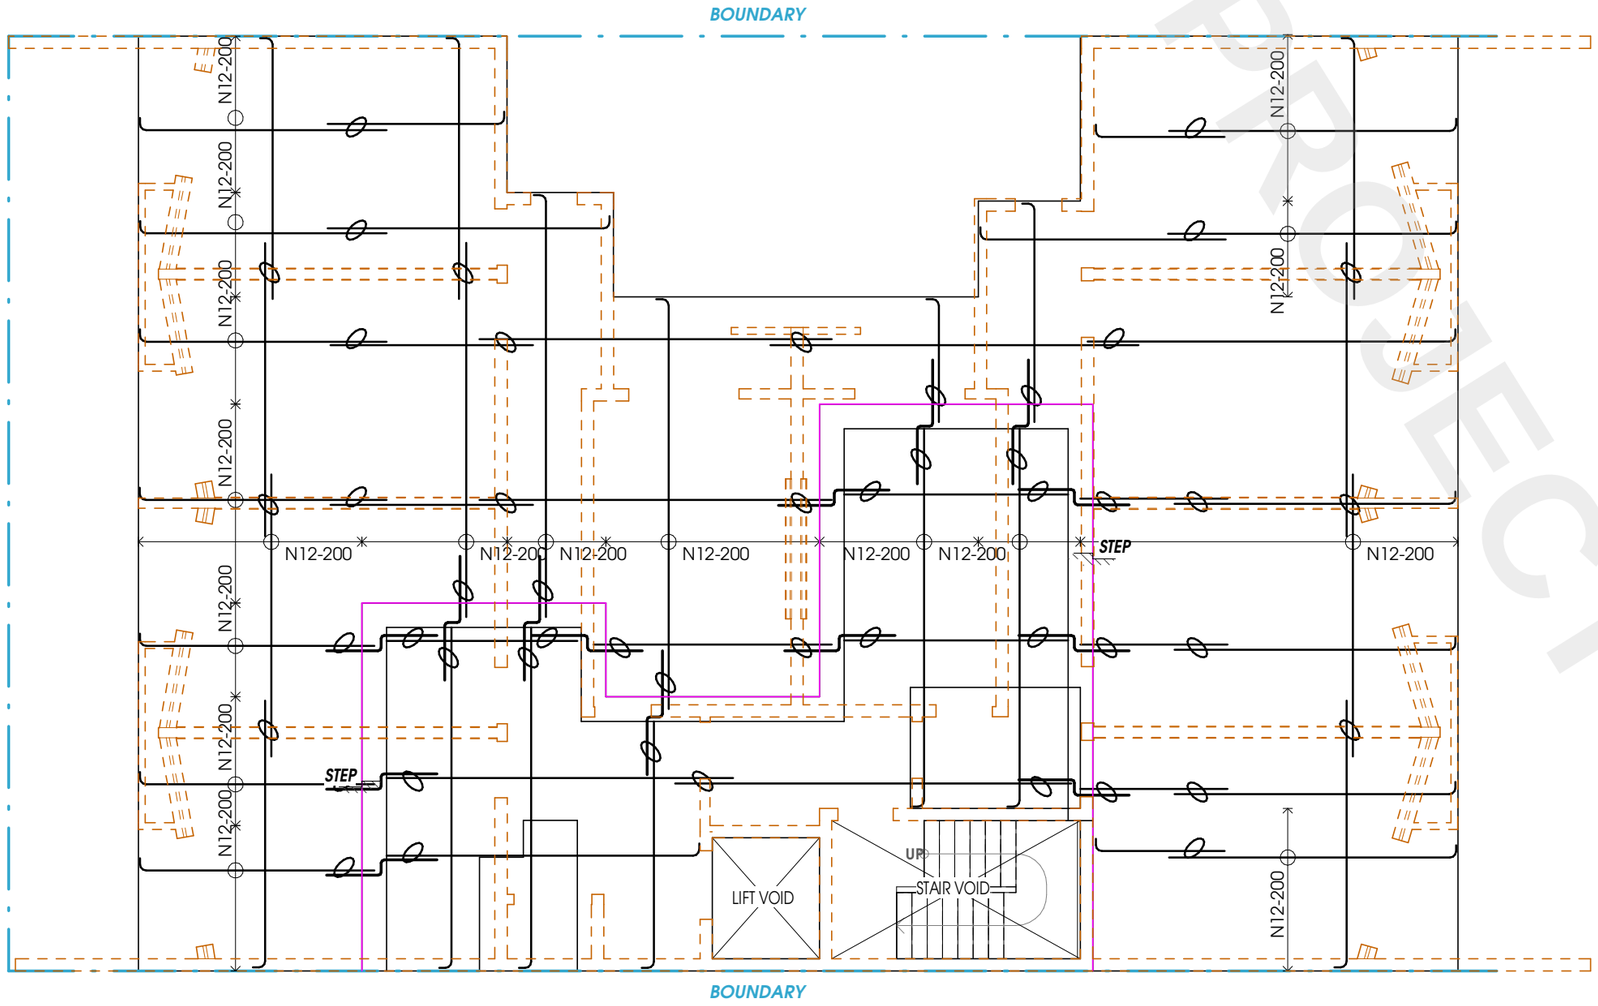


LEVEL 4 BOTTOM REINFORCEMENT PLAN

SCALE: 1 : 100


NOTES:

SUSPENDED SLAB:


A. DRAWING TO BE READ IN CONJUNCTION WITH ARCHITECTURE DRAWINGS .
B. REFER TO ARCHITECTURAL DRAWINGS FOR ALL SETOUT, LEVELS, STEPS, FOLDS & FALLS ETC.
C. REFER TO STORMWATER DRAINAGE DRAWINGS FOR LOCATION OF PUMP WELL AND SUMP PITS.
D. ALL CONCRETE CYLINDERS TO BE STORED AND CURED ON SITE PRIOR TESTING TO AS3600.
E. CONCRETE SLAB (f'c)=32 MPa WITH A SLUMP OF 80MM.
F. AGGREGATE MINIMUM SIZE 20MM.
G. ALL BRICKS WALLS TO BE ARTICULATED, EXPANSION JOINT SPACING TO BE 6000mm
H. ALL EXPOSED SLABS TO BE WATERPROOFED WITH APPROVED SYSTEMS.
I. ACOUSTIC ENGINEER TO CHECK AND VERIFY ALL FLOOR SLAB FOR ACOUSTIC REQUIREMENTS IN ACCORDANCE WITH THE BCA REGULATIONS AND ADVISE ON ANY ACOUSTIC TREATMENT NEEDED TO SATISFY THE REGULATION.
J. FOR FOLD REINFORCEMENTS REFER TO SECTION S4 U.N.O.
K. ENSURE 50mm MINIMUM SPACING BETWEEN BARS.
L. PROVIDE ALL EXTRA REINFORCEMENT AS SHOWN ON PLAN.
M. PROVIDE 3N16 TOP AND BOTTOM AT THE PERIMETER OF THE SLAB.
N. SLAB REINFORCEMENT LAYING SEQUENCE U.N.O.:

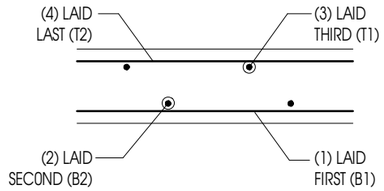

O. TYPICAL TRIMMERS AT PENETRATION/OPENING DETAIL:

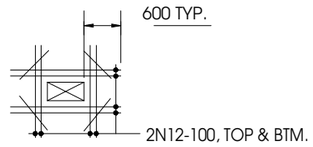

P. TYPICAL TRIMMERS AT RE-ENTRANT CORNERS:

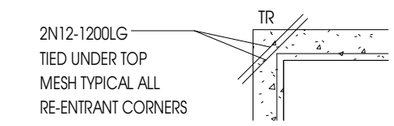

Q. PROVIDE TOP & BOTTOM BARS ON ALL WALL OPENINGS AS PER THE SCHEDULE BELOW:

LENGTH OF OPENING (m)	BOTTOM BAR	TOP BAR
1.0 - 1.8	2N16	2N16
1.8 - 2.5	2N20	2N20
2.5 - 3.5	2N24	2N24

R. PROVIDE ADEQUATE OVERLAP AT MESH JOINTS AS FOLLOWS :
- 400 MIN. LAP FOR SL82 MESH
- 500 MIN. LAP FOR SL92 MESH
- 600 MIN. LAP FOR SL102 MESH

S. PROVIDE ADEQUATE OVERLAP FOR BARS AS FOLLOWS:

BAR(X-Y)	MIN LAPPING REQUIRED
N12	500 mm
N16	800 mm
N20	1000 mm
N24	1200 mm
N28	1400 mm

PRINT IN COLOUR

MODULAR ENGINEERS P/L
Structural Engineering | Civil Engineering
Stormwater Engineering | Flood Engineering
Traffic Engineering | Temporary works
ABN : 66 646 960 929
TEL. : 02 873 08473
MOB. : 04 208 98999
EMAIL :
WEBSITE :
ADDRESS :

CLIENT:

PROJECT TITLE:
MULTI DWELLING

SHEET NAME:
LEVEL 4 BOTTOM REINFORCEMENT PLAN

PROJECT NUMBER:
175-2026

INTERNAL REVISIONS:

ISSUE	DATE	DESCRIPTION	BY
E	10-09-26	ISSUED FOR CONSTRUCTION	D.A.
D	08-09-26	ISSUED FOR CONSTRUCTION	D.A.
C	24-08-26	ISSUED FOR PRELIMINARY	D.A.
B	21-08-26	ISSUED FOR PRELIMINARY	D.A.

AMENDMENTS

DRAWN : L.M. DATE: 17-07-26
DESIGNED : A.O. REVISION DATE:
QA CHECK : A.O. 10-09-26
APPROVED BY:

RPEQ: 28316
NPER: 5358554
DATE: 10-09-26

ISSUE TYPE:
CONSTRUCTION

SHEET NUMBER:
STR810

SHEET SIZE: **A3**
REVISION: **E**

SAMPLE PROJECT A - STRUCTURAL REV E - CURRENT - RECRUITMENT ASSESSMENT ONLY
TEST PROJECT ONLY
NOT FOR CONSTRUCTION
NOTE: THE DESIGN AND DETAILS SHOWN ON THESE DRAWINGS ARE APPLICABLE TO THIS PROJECT ONLY AND MAY NOT BE REPRODUCED IN WHOLE OR IN PART OR BE USED FOR ANY OTHER PROJECT OR PURPOSE WITHOUT THE WRITTEN PERMISSION OF WITH WHOM COPYRIGHT RESIDES.


REGULATED DESIGN RECORD

PROJECT ADDRESS:	
PROJECT TITLE:	MULTI DWELLING
CONSENT NO:	STR208 - 2023
BODY CORPORATE REG NO:	DEP0001320
DRAWING TITLE:	LEVEL 4 TOP REINFORCEMENT PLAN
DRAWING NO:	STR811


REV	DATE DD.MM.YY	DESCRIPTION	DP FULL NAME	REG NO
E	10-09-26	ISSUED FOR CONSTRUCTIO		



BAR LAYING SEQUENCE

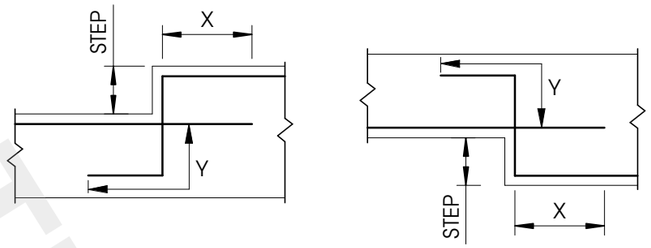

TYPICAL REINFORCEMENT LAPPING

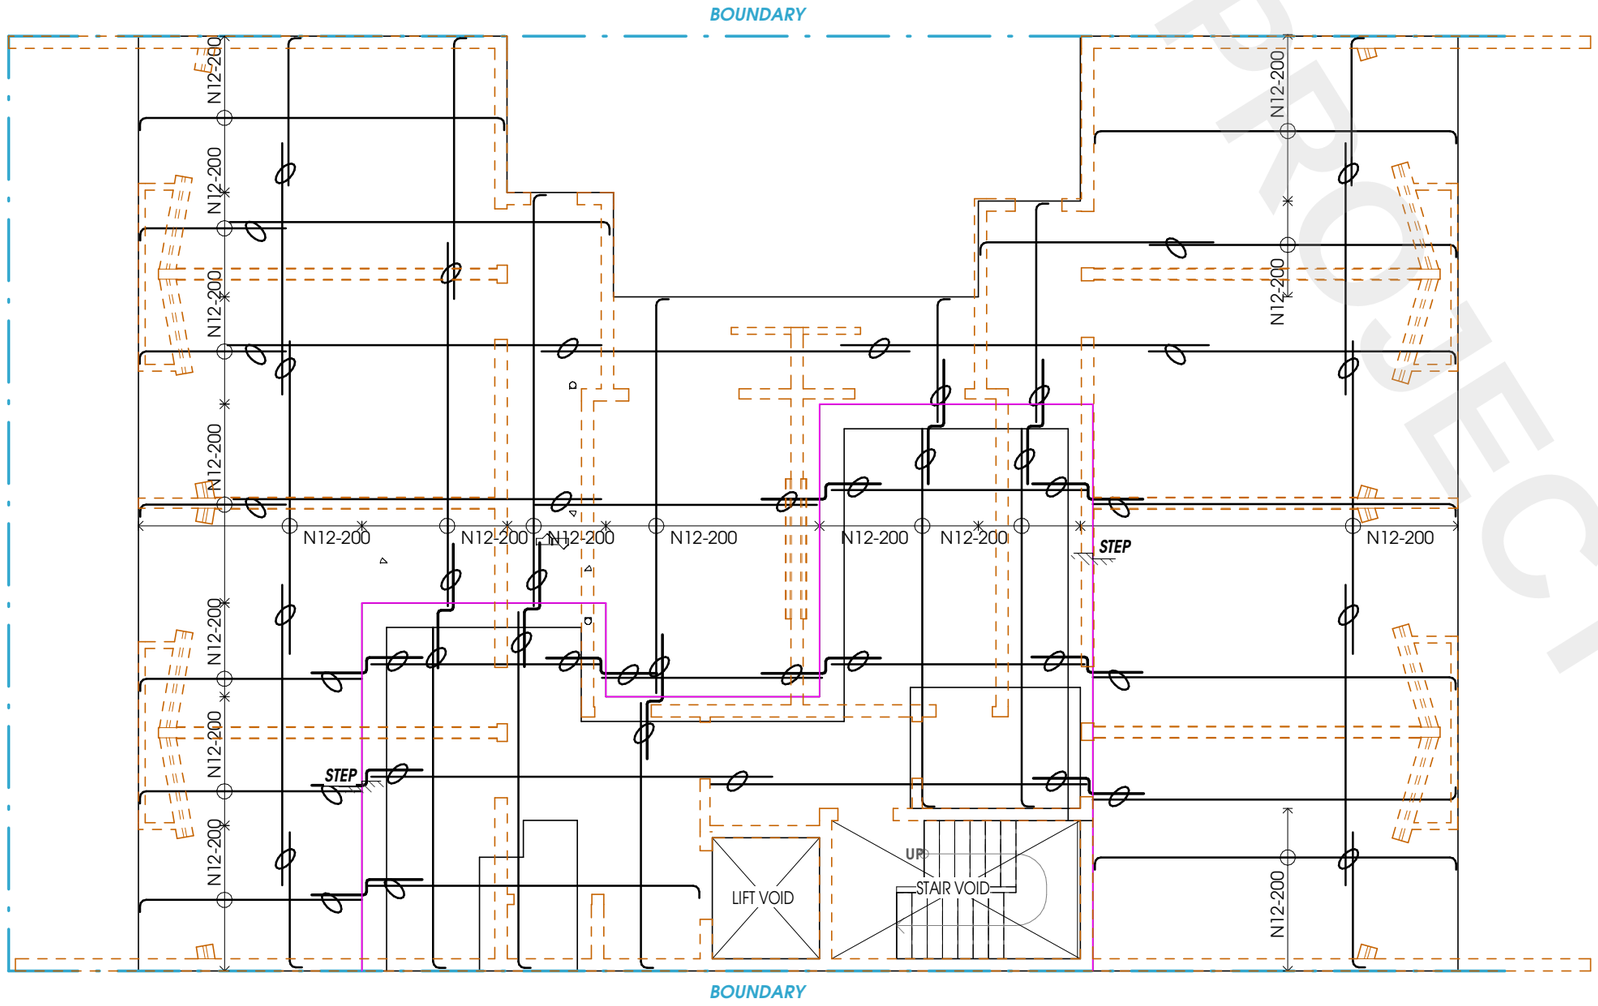


LEVEL 4 TOP REINFORCEMENT PLAN

SCALE: 1 : 100


NOTES:

SUSPENDED SLAB:


A. DRAWING TO BE READ IN CONJUNCTION WITH ARCHITECTURE DRAWINGS .
B. REFER TO ARCHITECTURAL DRAWINGS FOR ALL SETOUT, LEVELS, STEPS, FOLDS & FALLS ETC.
C. REFER TO STORMWATER DRAINAGE DRAWINGS FOR LOCATION OF PUMP WELL AND SUMP PITS.
D. ALL CONCRETE CYLINDERS TO BE STORED AND CURED ON SITE PRIOR TESTING TO AS3600.
E. CONCRETE SLAB (f'c)=32 MPa WITH A SLUMP OF 80MM.
F. AGGREGATE MINIMUM SIZE 20MM.
G. ALL BRICKS WALLS TO BE ARTICULATED, EXPANSION JOINT SPACING TO BE 6000mm
H. ALL EXPOSED SLABS TO BE WATERPROOFED WITH APPROVED SYSTEMS.
I. ACOUSTIC ENGINEER TO CHECK AND VERIFY ALL FLOOR SLAB FOR ACOUSTIC REQUIREMENTS IN ACCORDANCE WITH THE BCA REGULATIONS AND ADVISE ON ANY ACOUSTIC TREATMENT NEEDED TO SATISFY THE REGULATION.
J. FOR FOLD REINFORCEMENTS REFER TO SECTION S4 U.N.O.
K. ENSURE 50mm MINIMUM SPACING BETWEEN BARS.
L. PROVIDE ALL EXTRA REINFORCEMENT AS SHOWN ON PLAN.
M. PROVIDE 3N16 TOP AND BOTTOM AT THE PERIMETER OF THE SLAB.
N. SLAB REINFORCEMENT LAYING SEQUENCE U.N.O.:

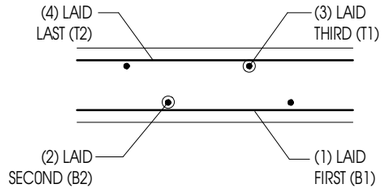

O. TYPICAL TRIMMERS AT PENETRATION/OPENING DETAIL:

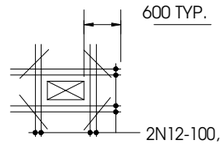

P. TYPICAL TRIMMERS AT RE-ENTRANT CORNERS:

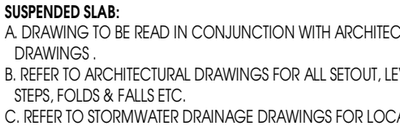

Q. PROVIDE TOP & BOTTOM BARS ON ALL WALL OPENINGS AS PER THE SCHEDULE BELOW:

LENGTH OF OPENING (m)	BOTTOM BAR	TOP BAR
1.0 - 1.8	2N16	2N16
1.8 - 2.5	2N20	2N20
2.5 - 3.5	2N24	2N24

R. PROVIDE ADEQUATE OVERLAP AT MESH JOINTS AS FOLLOWS :
- 400 MIN. LAP FOR SL82 MESH
- 500 MIN. LAP FOR SL92 MESH
- 600 MIN. LAP FOR SL102 MESH

S. PROVIDE ADEQUATE OVERLAP FOR BARS AS FOLLOWS:

BAR(X-Y)	MIN LAPPING REQUIRED
N12	500 mm
N16	800 mm
N20	1000 mm
N24	1200 mm
N28	1400 mm

MODULAR ENGINEERS P/L

Structural Engineering | Civil Engineering
Stormwater Engineering | Flood Engineering
Traffic Engineering | Temporary works

ABN : 66 646 960 929
TEL. : 02 873 08473
MOB. : 04 208 98999
EMAIL :
WEBSITE :
ADDRESS :

CLIENT:

PROJECT TITLE:
MULTI DWELLING

SHEET NAME:
LEVEL 4 TOP REINFORCEMENT PLAN

PROJECT NUMBER:
175-2026

INTERNAL REVISIONS:

ISSUE	DATE	DESCRIPTION	BY
E	10-09-26	ISSUED FOR CONSTRUCTION	D.A.
D	08-09-26	ISSUED FOR CONSTRUCTION	D.A.
C	24-08-26	ISSUED FOR PRELIMINARY	D.A.
B	21-08-26	ISSUED FOR PRELIMINARY	D.A.

AMENDMENTS

DRAWN : L.M. DATE: 17-07-26
DESIGNED : A.O. REVISION DATE:
QA CHECK : A.O. 10-09-26
APPROVED BY:

RPEQ: 28316
NPER: 5358554
DATE: 10-09-26

ISSUE TYPE:
CONSTRUCTION

SHEET NUMBER:
STR811

SHEET SIZE: **A3**
REVISION: **E**

PRINT IN COLOUR

SAMPLE PROJECT A - STRUCTURAL REVIEW - CURRENT - RECRUITMENT ASSESSMENT ONLY


TEST PROJECT ONLY

NOTE: THE DESIGN AND DETAILS SHOWN ON THESE DRAWINGS ARE APPLICABLE TO THIS PROJECT ONLY AND MAY NOT BE REPRODUCED IN WHOLE OR IN PART OR BE USED FOR ANY OTHER PROJECT OR PURPOSE WITHOUT THE WRITTEN PERMISSION OF WITH WHOM COPYRIGHT RESIDES.

REGULATED DESIGN RECORD

PROJECT ADDRESS:			
PROJECT TITLE:	MULTI DWELLING		
CONSENT NO:	STR208 - 2023	**BODY CORPORATE REG NO:**	DEP0001320
DRAWING TITLE:	LEVEL 4 LOADING PLAN	**DRAWING NO:**	STR820

REV	DATE DD.MM.YY	DESCRIPTION	DP FULL NAME	REG NO
E	10-09-26	ISSUED FOR CONSTRUCTIO		

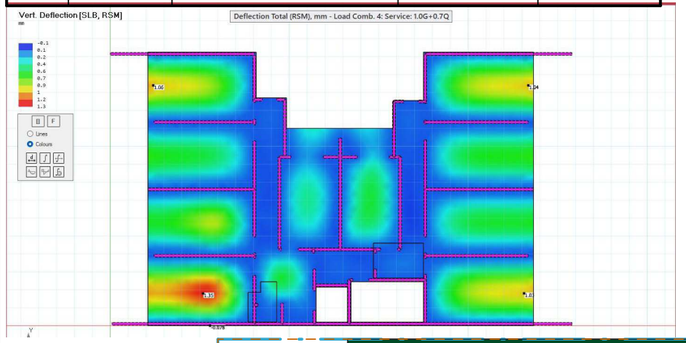


LOADING TABLE
WHERE APPLICABLE

MARK	COLOUR	AREA	SUPERIMPOSED DEAD LOAD	LIVE LOAD
1		RESIDENTIAL	1.5 kPa	1.5 kPa
2		PARKING	0.5 kPa EXC. FALLS AND GRADING	2.5 kPa
3		STORAGE	0.5 kPa	5.0 kPa
4		CORRIDOR / STAIR	1.5 kPa	4.0 kPa
5		LOBBY	1.5 kPa	4.0 kPa
6		BALCONY	1.5 kPa	2.0 kPa
7		MECH ROOM,FAN ROOM	1.5 kPa	5.0 kPa
8		COMMON AREA	1.5 kPa	4.0 kPa
9		LIGHT WEIGHT ROOF	0.5 kPa	0.5 kPa

LOADING TABLE
WHERE APPLICABLE

MARK	COLOUR	AREA	SUPERIMPOSED DEAD LOAD	LIVE LOAD
10		WASTE ROOM	0.5 kPa	5.0 kPa
11		RETAILS	1.5 kPa	4.0 kPa
12		ROOF (NON-TRAFFICABLE)	2.0 kPa	1.5 kPa
13		LANDSCAPE 400mm SOIL MAX.	4.0 kPa	1.5 kPa
14		LANDSCAPE 1000mm SOIL MAX.	10.0 kPa	1.5 kPa
15		SUBSTATION	1.0 kPa	2.0 kPa
16		LOADING DECK	1.0 kPa	10.0 kPa
17		PEBBLES	4.0 kPa	1.5 kPa
18		OSD TANK/ WATER STORAGE TANK	10.0 kPa FOR EVERY METRE HEIGHT OF WATER	

DEFLECTION NOTES (LONG-TERM)
- LONG-TERM DEFLECTION IS BASED ON DL + 0.3LL FOR SUSTAINED LOADS.
- CREEP FACTOR Λ = 2.0 TO 3.0 APPLIED PER AS3600.
- TOTAL DEFLECTION: Δ TOTAL=Δ IMMEDIATE + Λ × Δ SUSTAINED
- IMMEDIATE DEFLECTION: DL + LL
- LONG-TERM DEFLECTION: DL + 0.3LL × Λ

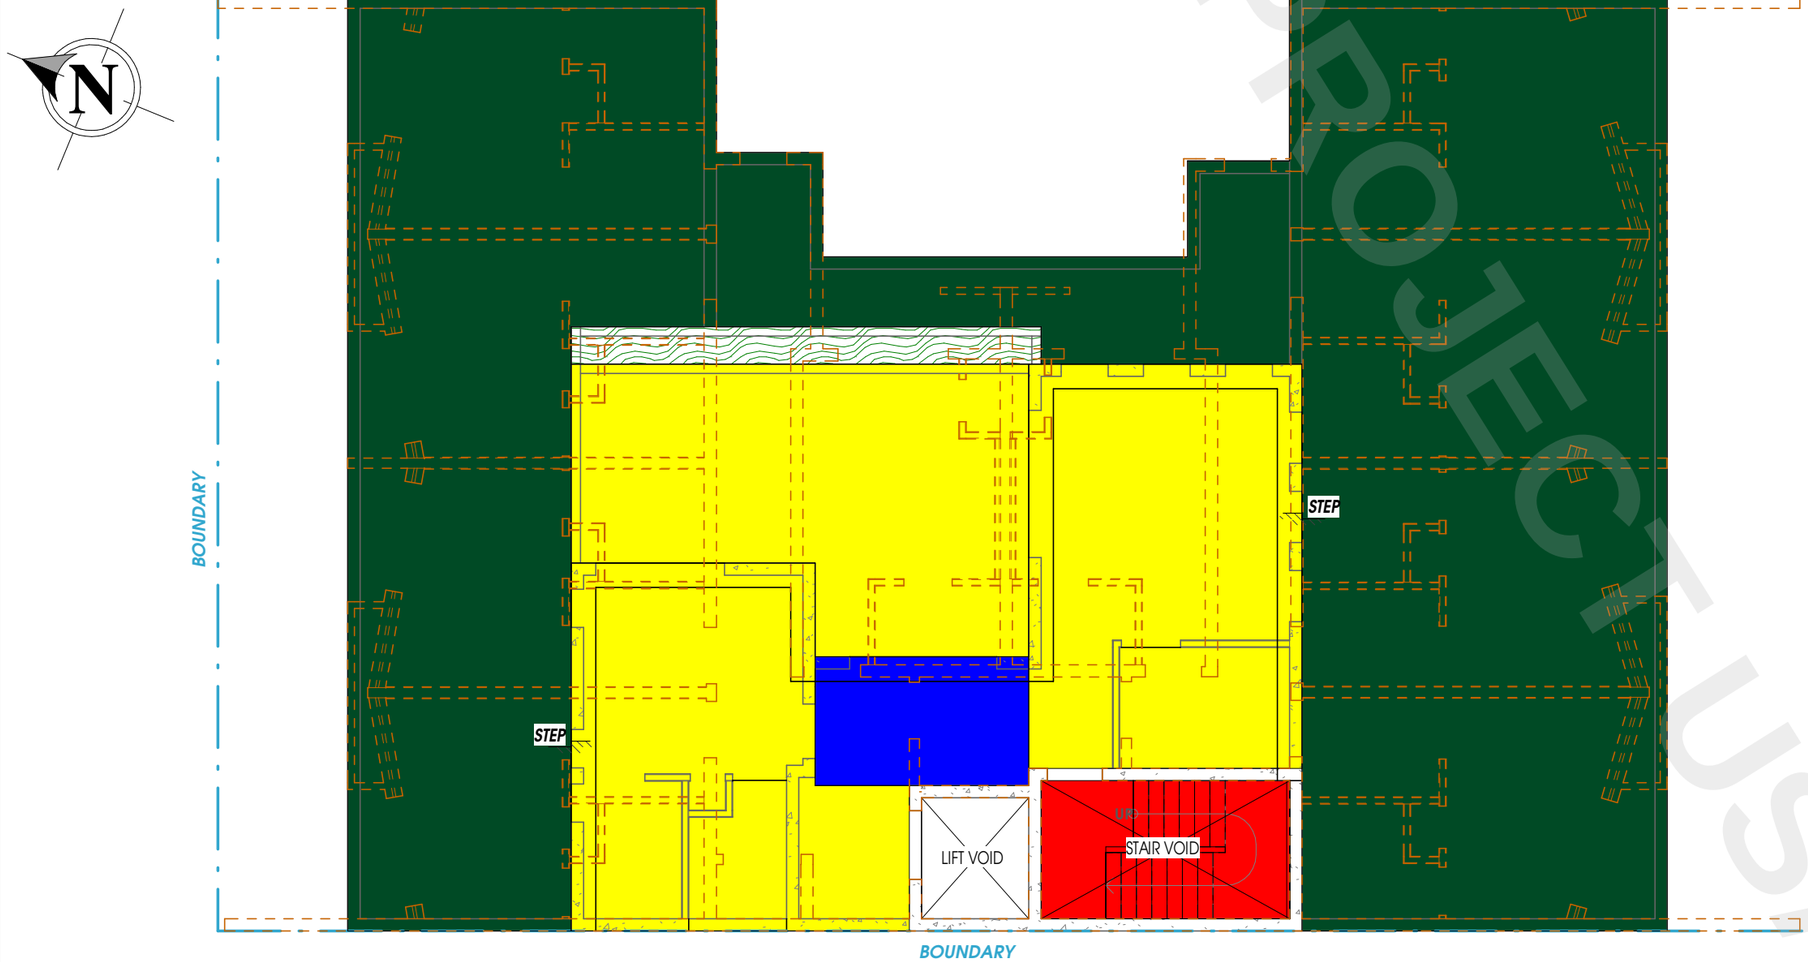

LEVEL 4 LOADING PLAN
SCALE: 1 : 100

MODULAR ENGINEERS P/L

Structural Engineering | Civil Engineering
Stormwater Engineering | Flood Engineering
Traffic Engineering | Temporary works

ABN : 66 646 960 929
TEL. : 02 873 08473
MOB. : 04 208 98999
EMAIL :
WEBSITE :
ADDRESS :

CLIENT:

PROJECT TITLE:
MULTI DWELLING

SHEET NAME:
LEVEL 4 LOADING PLAN

PROJECT NUMBER:
175-2026

INTERNAL REVISIONS:

ISSUE	DATE	DESCRIPTION	BY
E	10-09-26	ISSUED FOR CONSTRUCTION	D.A.
D	08-09-26	ISSUED FOR CONSTRUCTION	D.A.
C	24-08-26	ISSUED FOR PRELIMINARY	D.A.
B	21-08-26	ISSUED FOR PRELIMINARY	D.A.

AMENDMENTS

DRAWN : L.M. DATE: 17-07-26
DESIGNED : A.O. REVISION DATE:
QA CHECK : A.O. 10-09-26

APPROVED BY:

RPEQ: 28316
NPER: 5358554
DATE: 10-09-26

ISSUE TYPE:
CONSTRUCTION

SHEET NUMBER:
STR820

SHEET SIZE: **A3** REVISION: **E**

PRINT IN COLOUR

SAMPLE PROJECT A - STRUCTURAL REVIEW - CURRENT - RECRUITMENT ASSESSMENT ONLY


TEST PROJECT USAGE ONLY


NOTE: THE DESIGN AND DETAILS SHOWN ON THESE DRAWINGS ARE APPLICABLE TO THIS PROJECT ONLY AND MAY NOT BE REPRODUCED IN WHOLE OR IN PART OR BE USED FOR ANY OTHER PROJECT OR PURPOSE WITHOUT THE WRITTEN PERMISSION OF WITH WHOM COPYRIGHT RESIDES.

REGULATED DESIGN RECORD


PROJECT ADDRESS:			
PROJECT TITLE:	MULTI DWELLING		
CONSENT NO:	STR208 - 2023	BODY CORPORATE REG NO:	DEP0001320
DRAWING TITLE:	SECTION AND DETAILS	DRAWING NO:	STR830

REV	DATE DD.MM.YY	DESCRIPTION	DP FULL NAME	REG NO
E	10-09-26	ISSUED FOR CONSTRUCTIO		

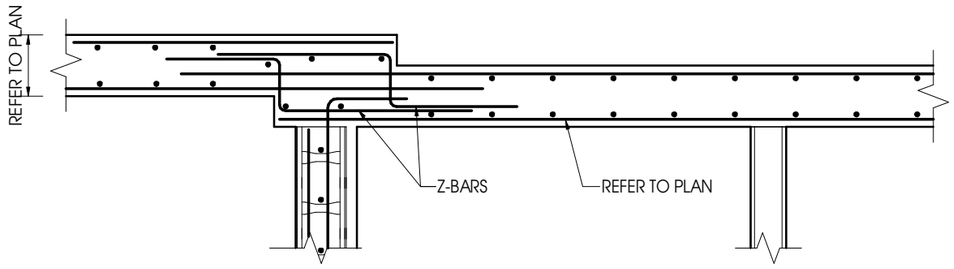

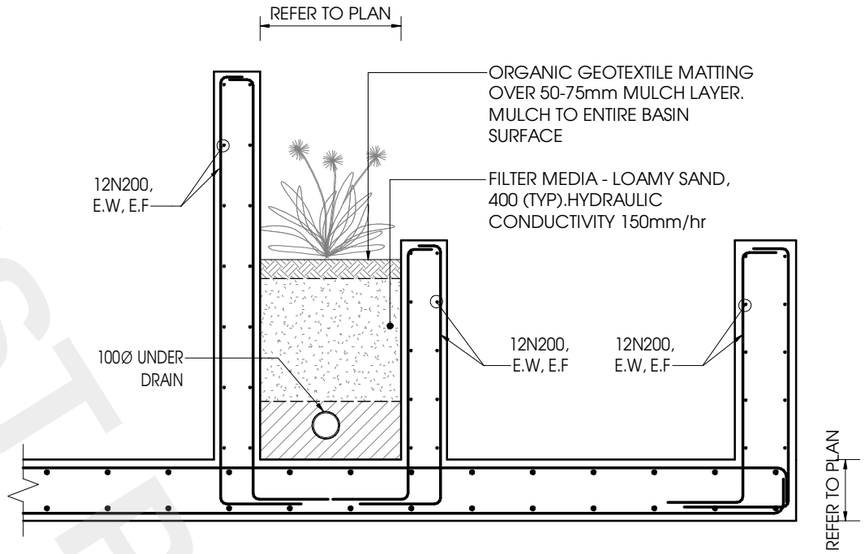

SECTION I
NOT TO SCALE STR800

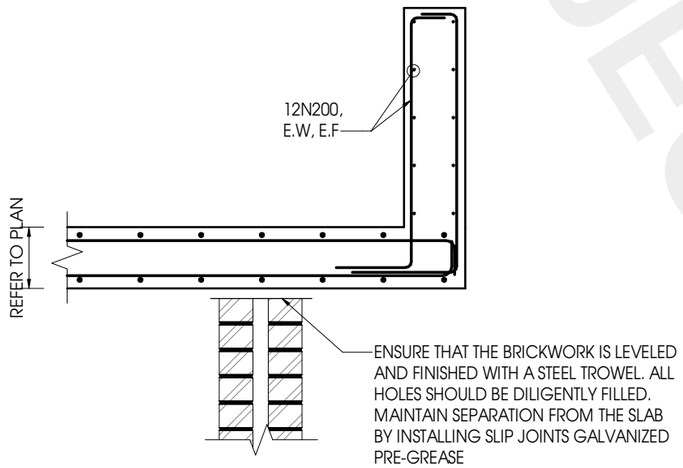

SECTION J
NOT TO SCALE STR800

MODULAR ENGINEERS P/L
Structural Engineering | Civil Engineering
Stormwater Engineering | Flood Engineering
Traffic Engineering | Temporary works
ABN : 66 646 960 929
TEL. : 02 873 08473
MOB. : 04 208 98999
EMAIL :
WEBSITE :
ADDRESS :

CLIENT:

PROJECT TITLE:
MULTI DWELLING

SHEET NAME:
SECTION AND DETAILS

PROJECT NUMBER:
175-2026

INTERNAL REVISIONS:

ISSUE	DATE	DESCRIPTION	BY
E	10-09-26	ISSUED FOR CONSTRUCTION	D.A.
D	08-09-26	ISSUED FOR CONSTRUCTION	D.A.
C	24-08-26	ISSUED FOR PRELIMINARY	D.A.
B	21-08-26	ISSUED FOR PRELIMINARY	D.A.

AMENDMENTS

DRAWN : L.M. DATE: 17-07-26
DESIGNED : A.O. REVISION DATE:
QA CHECK : A.O. 10-09-26

APPROVED BY:

RPEQ: 28316
NPER: 5358554
DATE: 10-09-26

ISSUE TYPE:
CONSTRUCTION

SHEET NUMBER:
STR830

SHEET SIZE: **A3** REVISION: **E**

PRINT IN COLOUR

SAMPLE PROJECT A - STRUCTURAL REV E - CURRENT - RECRUITMENT ASSESSMENT ONLY

TEST PROJECT USAGE ONLY

NOTE: THE DESIGN AND DETAILS SHOWN ON THESE DRAWINGS ARE APPLICABLE TO THIS PROJECT ONLY AND MAY NOT BE REPRODUCED IN WHOLE OR IN PART OR BE USED FOR ANY OTHER PROJECT OR PURPOSE WITHOUT THE WRITTEN PERMISSION OF WITH WHOM COPYRIGHT RESIDES.

REGULATED DESIGN RECORD


PROJECT ADDRESS:			
PROJECT TITLE:	MULTI DWELLING		
CONSENT NO:	STR208 - 2023	BODY CORPORATE REG NO:	DEP0001320
DRAWING TITLE:	ROOF PLAN	DRAWING NO:	STR900

REV	DATE DD.MM.YY	DESCRIPTION	DP FULL NAME	REG NO
E	10-09-26	ISSUED FOR CONSTRUCTIO		

LEGEND:

- DENOTES CONCRETE COLUMN/ WALL **OVER ONLY**
- DENOTES BRICK WALLS **OVER ONLY**
- DENOTES BLOCK WORK WALLS **OVER ONLY**
- DENOTES RITEK WALLS **OVER ONLY**
- DENOTES CONCRETE WALL/COLUMN **UNDER ONLY**
- DENOTES WET AREA WITH 2mm FALL
- DENOTES SLAB PENETRATION
- DENOTES STEP ON SLAB
- C00 DENOTES COLUMN MARK
- W00 DENOTES WALL MARK
- 000 DENOTES SLAB THICKNESS
- DENOTES EXTENT OF SLAB STEP


FOR STRUCTURAL NOTES REFER TO DRAWING STR00 SERIES

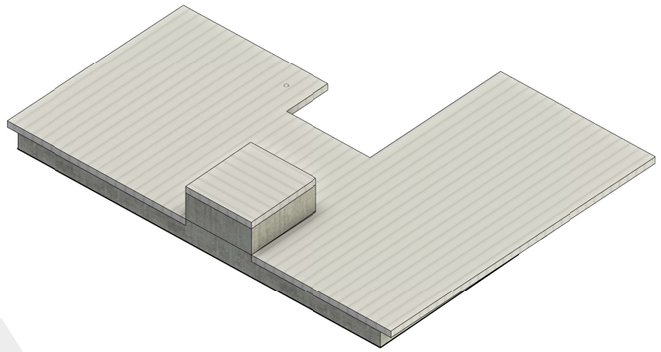


NOTES:

SUSPENDED SLAB:

A. DRAWING TO BE READ IN CONJUNCTION WITH ARCHITECTURE DRAWINGS .
B. REFER TO ARCHITECTURAL DRAWINGS FOR ALL SETOUT, LEVELS, STEPS, FOLDS & FALLS ETC.
C. REFER TO STORMWATER DRAINAGE DRAWINGS FOR LOCATION OF PUMP WELL AND SUMP PITS.
D. ALL CONCRETE CYLINDERS TO BE STORED AND CURED ON SITE PRIOR TESTING TO AS3600.
E. CONCRETE SLAB (f'c)=32 MPa WITH A SLUMP OF 80MM.
F. AGGREGATE MINIMUM SIZE 20MM.
G. ALL BRICKS WALLS TO BE ARTICULATED, EXPANSION JOINT SPACING TO BE 6000mm
H. ALL EXPOSED SLABS TO BE WATERPROOFED WITH APPROVED SYSTEMS.
I. ACOUSTIC ENGINEER TO CHECK AND VERIFY ALL FLOOR SLAB FOR ACOUSTIC REQUIREMENTS IN ACCORDANCE WITH THE BCA REGULATIONS AND ADVISE ON ANY ACOUSTIC TREATMENT NEEDED TO SATISFY THE REGULATION.
J. FOR FOLD REINFORCEMENTS REFER TO TYPICAL SECTION U.N.O.

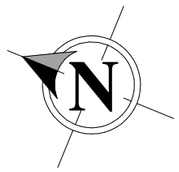

ROOF FLOOR SLAB: FRL 90/90/90

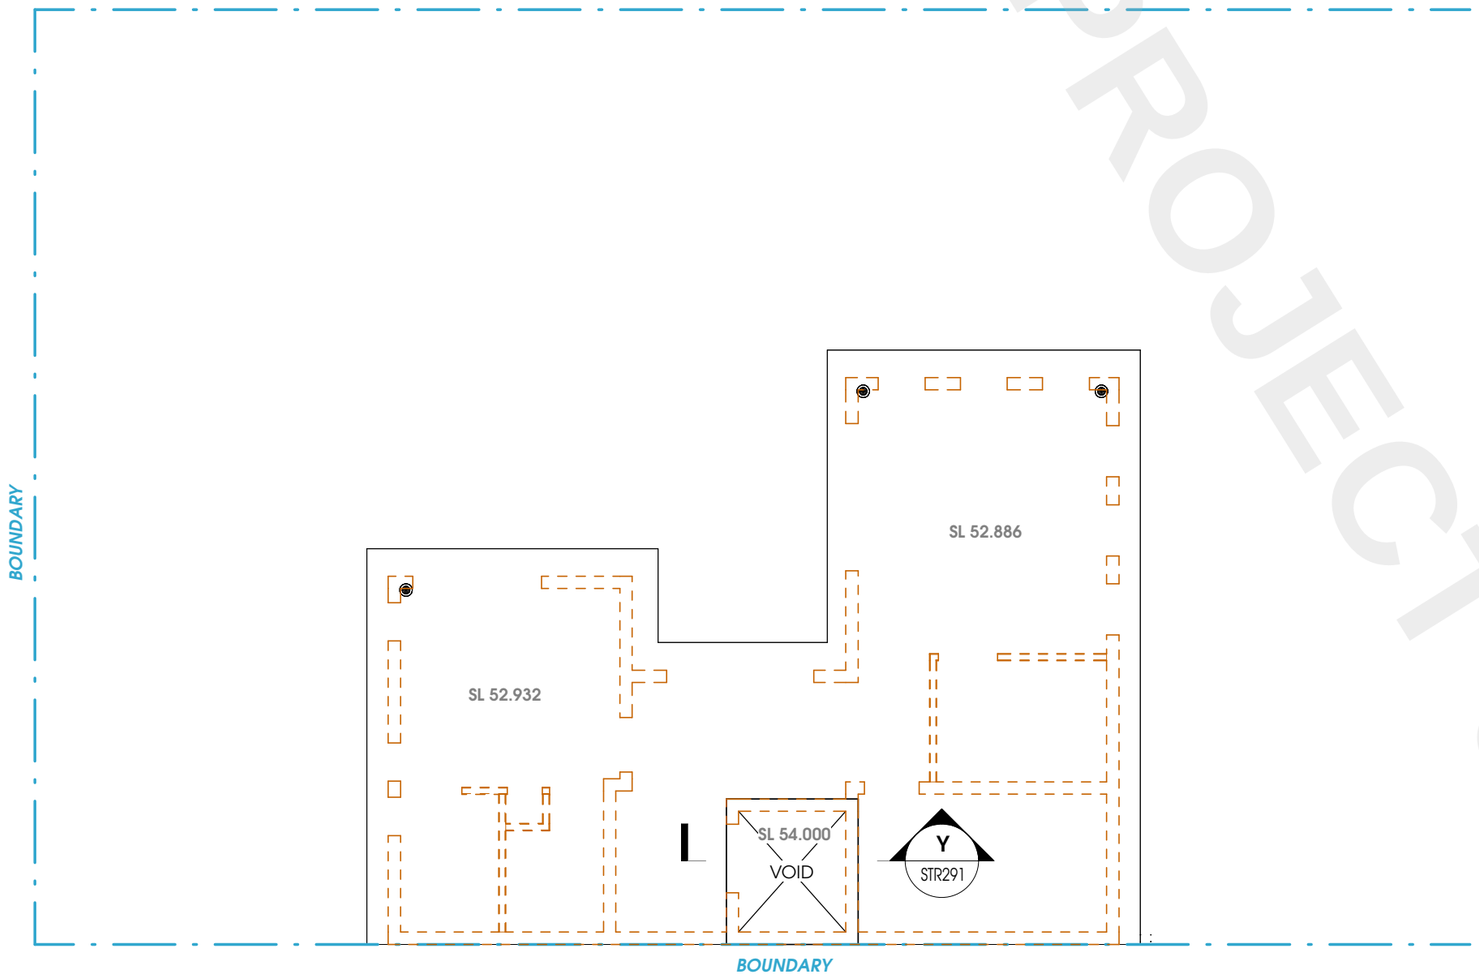

LEVEL 5 ROOF PLAN

SCALE: 1 : 100

MODULAR ENGINEERS P/L

Structural Engineering | Civil Engineering
Stormwater Engineering | Flood Engineering
Traffic Engineering | Temporary works

ABN : 66 646 960 929
TEL. : 02 873 08473
MOB. : 04 208 98999
EMAIL :
WEBSITE :
ADDRESS :

CLIENT:

PROJECT TITLE:
MULTI DWELLING

SHEET NAME:
ROOF PLAN

PROJECT NUMBER:
175-2026

INTERNAL REVISIONS:

ISSUE	DATE	DESCRIPTION	BY
E	10-09-26	ISSUED FOR CONSTRUCTION	D.A.
D	08-09-26	ISSUED FOR CONSTRUCTION	D.A.
C	24-08-26	ISSUED FOR PRELIMINARY	D.A.
B	21-08-26	ISSUED FOR PRELIMINARY	D.A.

AMENDMENTS

DRAWN : L.M. DATE: 17-07-26
DESIGNED : A.O. REVISION DATE:
QA CHECK : A.O. 10-09-26

APPROVED BY:

RPEQ: 28316
NPER: 5358554
DATE: 10-09-26

ISSUE TYPE:
CONSTRUCTION

SHEET NUMBER:
STR900

SHEET SIZE: **A3**
REVISION: **E**

PRINT IN COLOUR

SAMPLE PROJECT A - STRUCTURAL REV E - CURRENT - RECRUITMENT ASSESSMENT ONLY

TEST PROJECT USAGE

NOTE: THE DESIGN AND DETAILS SHOWN ON THESE DRAWINGS ARE APPLICABLE TO THIS PROJECT ONLY AND MAY NOT BE REPRODUCED IN WHOLE OR IN PART OR BE USED FOR ANY OTHER PROJECT OR PURPOSE WITHOUT THE WRITTEN PERMISSION OF WITH WHOM COPYRIGHT RESIDES.


REGULATED DESIGN RECORD

PROJECT ADDRESS:			
PROJECT TITLE:	MULTI DWELLING		
CONSENT NO:	STR208 - 2023	BODY CORPORATE REG NO:	DEP0001320
DRAWING TITLE:	ROOF BOTTOM REINFORCEMENT PLAN	DRAWING NO:	STR901


REV	DATE DD.MM.YY	DESCRIPTION	DP FULL NAME	REG NO
E	10-09-26	ISSUED FOR CONSTRUCTIO		




BAR LAYING SEQUENCE

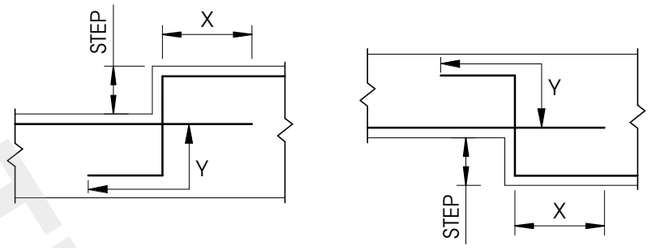

TYPICAL REINFORCEMENT LAPPING

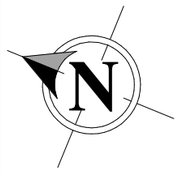

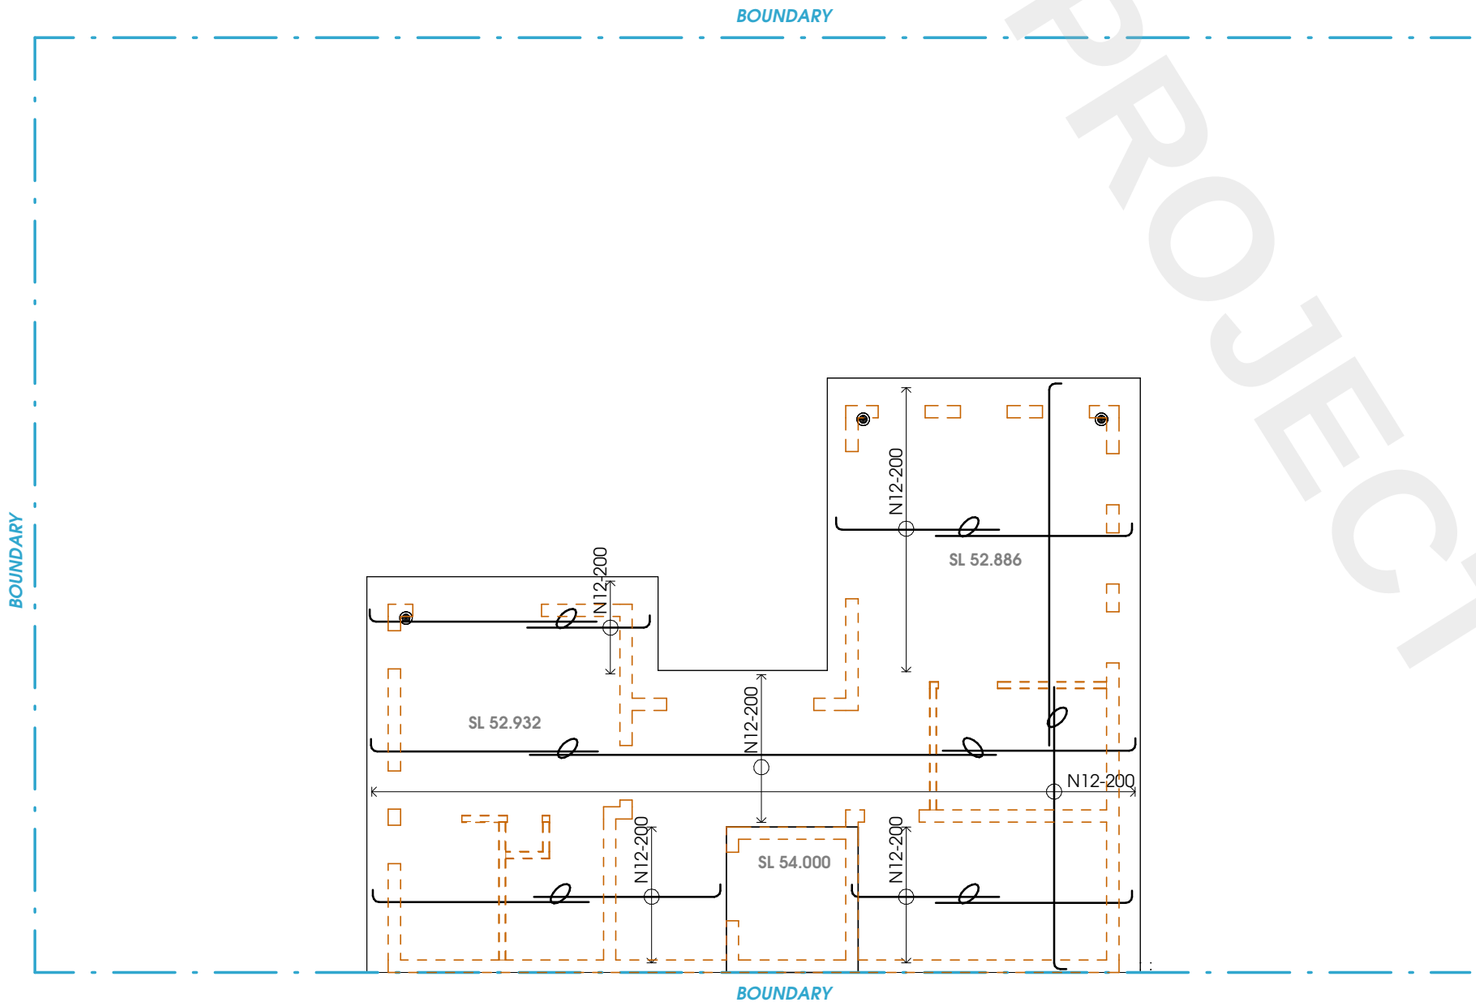


ROOF BOTTOM REINFORCEMENT PLAN

SCALE: 1 : 100


NOTES:

SUSPENDED SLAB:


A. DRAWING TO BE READ IN CONJUNCTION WITH ARCHITECTURE DRAWINGS .
B. REFER TO ARCHITECTURAL DRAWINGS FOR ALL SETOUT, LEVELS, STEPS, FOLDS & FALLS ETC.
C. REFER TO STORMWATER DRAINAGE DRAWINGS FOR LOCATION OF PUMP WELL AND SUMP PITS.
D. ALL CONCRETE CYLINDERS TO BE STORED AND CURED ON SITE PRIOR TESTING TO AS3600.
E. CONCRETE SLAB (f'c)=32 MPa WITH A SLUMP OF 80MM.
F. AGGREGATE MINIMUM SIZE 20MM.
G. ALL BRICKS WALLS TO BE ARTICULATED, EXPANSION JOINT SPACING TO BE 6000mm
H. ALL EXPOSED SLABS TO BE WATERPROOFED WITH APPROVED SYSTEMS.
I. ACOUSTIC ENGINEER TO CHECK AND VERIFY ALL FLOOR SLAB FOR ACOUSTIC REQUIREMENTS IN ACCORDANCE WITH THE BCA REGULATIONS AND ADVISE ON ANY ACOUSTIC TREATMENT NEEDED TO SATISFY THE REGULATION.
J. FOR FOLD REINFORCEMENTS REFER TO SECTION S4 U.N.O.
K. ENSURE 50mm MINIMUM SPACING BETWEEN BARS.
L. PROVIDE ALL EXTRA REINFORCEMENT AS SHOWN ON PLAN.
M. PROVIDE 3N16 TOP AND BOTTOM AT THE PERIMETER OF THE SLAB.
N. SLAB REINFORCEMENT LAYING SEQUENCE U.N.O.:

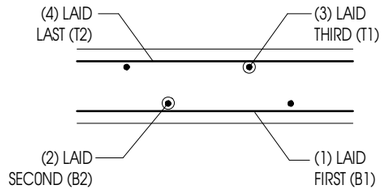

O. TYPICAL TRIMMERS AT PENETRATION/OPENING DETAIL:

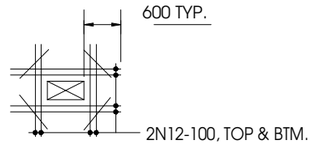

P. TYPICAL TRIMMERS AT RE-ENTRANT CORNERS:

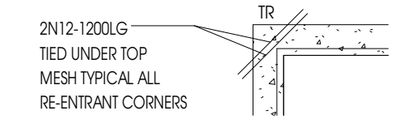

Q. PROVIDE TOP & BOTTOM BARS ON ALL WALL OPENINGS AS PER THE SCHEDULE BELOW:

LENGTH OF OPENING (m)	BOTTOM BAR	TOP BAR
1.0 - 1.8	2N16	2N16
1.8 - 2.5	2N20	2N20
2.5 - 3.5	2N24	2N24

R. PROVIDE ADEQUATE OVERLAP AT MESH JOINTS AS FOLLOWS :
- 400 MIN. LAP FOR SL82 MESH
- 500 MIN. LAP FOR SL92 MESH
- 600 MIN. LAP FOR SL102 MESH

S. PROVIDE ADEQUATE OVERLAP FOR BARS AS FOLLOWS:

BAR(X-Y)	MIN LAPPING REQUIRED
N12	500 mm
N16	800 mm
N20	1000 mm
N24	1200 mm
N28	1400 mm

MODULAR ENGINEERS P/L

Structural Engineering | Civil Engineering
Stormwater Engineering | Flood Engineering
Traffic Engineering | Temporary works

ABN : 66 646 960 929
TEL. : 02 873 08473
MOB. : 04 208 98999
EMAIL :
WEBSITE :
ADDRESS :

CLIENT:

PROJECT TITLE:
MULTI DWELLING

SHEET NAME:
ROOF BOTTOM REINFORCEMENT PLAN

PROJECT NUMBER:
175-2026

INTERNAL REVISIONS:

ISSUE	DATE	DESCRIPTION	BY
E	10-09-26	ISSUED FOR CONSTRUCTION	D.A.
D	08-09-26	ISSUED FOR CONSTRUCTION	D.A.
C	24-08-26	ISSUED FOR PRELIMINARY	D.A.
B	21-08-26	ISSUED FOR PRELIMINARY	D.A.

AMENDMENTS

DRAWN : L.M. DATE: 17-07-26
DESIGNED : A.O. REVISION DATE:
QA CHECK : A.O. 10-09-26

APPROVED BY:

RPEQ: 28316
NPER: 5358554
DATE: 10-09-26

ISSUE TYPE:
CONSTRUCTION

SHEET NUMBER:
STR901

SHEET SIZE: **A3**
REVISION: **E**

PRINT IN COLOUR

SAMPLE PROJECT A - STRUCTURAL REV E - CURRENT - RECRUITMENT ASSESSMENT ONLY


TEST PROJECT ONLY

NOTE: THE DESIGN AND DETAILS SHOWN ON THESE DRAWINGS ARE APPLICABLE TO THIS PROJECT ONLY AND MAY NOT BE REPRODUCED IN WHOLE OR IN PART OR BE USED FOR ANY OTHER PROJECT OR PURPOSE WITHOUT THE WRITTEN PERMISSION OF WITH WHOM COPYRIGHT RESIDES.


REGULATED DESIGN RECORD

PROJECT ADDRESS:			
PROJECT TITLE:	MULTI DWELLING		
CONSENT NO:	STR208 - 2023	BODY CORPORATE REG NO:	DEP0001320
DRAWING TITLE:	ROOF TOP REINFORCEMENT PLAN	DRAWING NO:	STR902


REV	DATE DD.MM.YY	DESCRIPTION	DP FULL NAME	REG NO
E	10-09-26	ISSUED FOR CONSTRUCTIO		

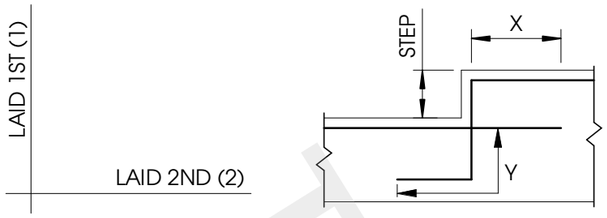


BAR LAYING SEQUENCE

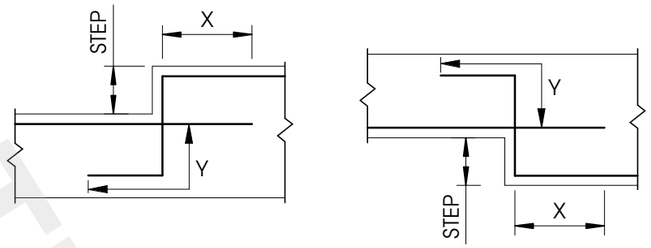

TYPICAL REINFORCEMENT LAPPING

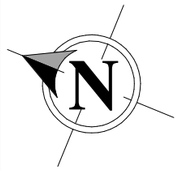

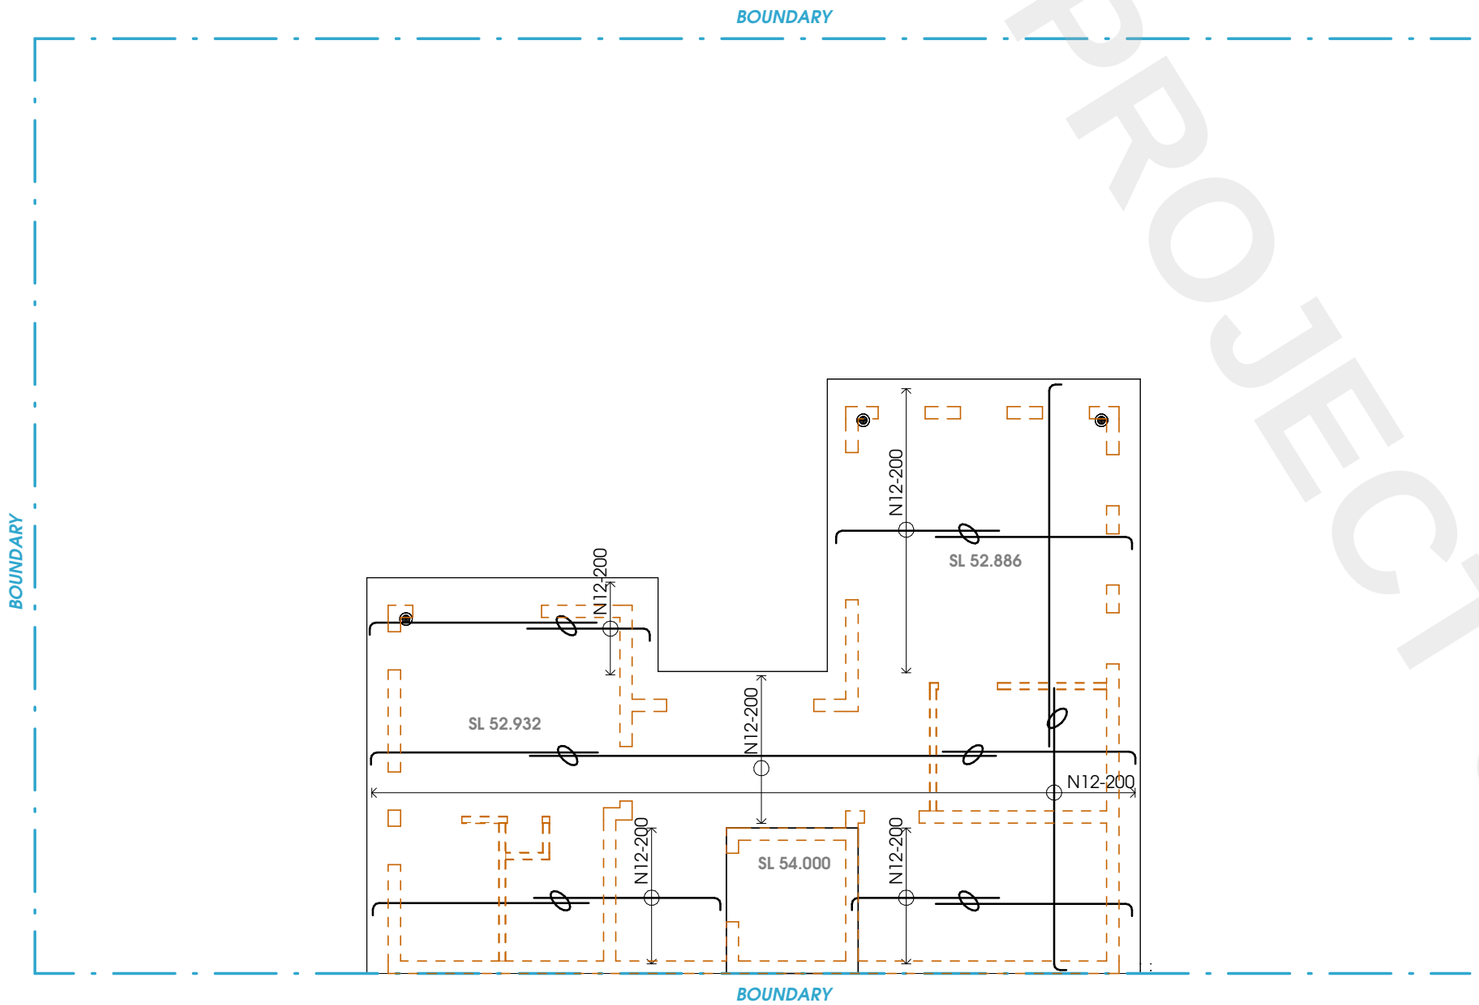


ROOF TOP REINFORCEMENT PLAN

SCALE: 1 : 100


NOTES:

SUSPENDED SLAB:


A. DRAWING TO BE READ IN CONJUNCTION WITH ARCHITECTURE DRAWINGS .
B. REFER TO ARCHITECTURAL DRAWINGS FOR ALL SETOUT, LEVELS, STEPS, FOLDS & FALLS ETC.
C. REFER TO STORMWATER DRAINAGE DRAWINGS FOR LOCATION OF PUMP WELL AND SUMP PITS.
D. ALL CONCRETE CYLINDERS TO BE STORED AND CURED ON SITE PRIOR TESTING TO AS3600.
E. CONCRETE SLAB (f'c)=32 MPa WITH A SLUMP OF 80MM.
F. AGGREGATE MINIMUM SIZE 20MM.
G. ALL BRICKS WALLS TO BE ARTICULATED, EXPANSION JOINT SPACING TO BE 6000mm
H. ALL EXPOSED SLABS TO BE WATERPROOFED WITH APPROVED SYSTEMS.
I. ACOUSTIC ENGINEER TO CHECK AND VERIFY ALL FLOOR SLAB FOR ACOUSTIC REQUIREMENTS IN ACCORDANCE WITH THE BCA REGULATIONS AND ADVISE ON ANY ACOUSTIC TREATMENT NEEDED TO SATISFY THE REGULATION.
J. FOR FOLD REINFORCEMENTS REFER TO SECTION S4 U.N.O.
K. ENSURE 50mm MINIMUM SPACING BETWEEN BARS.
L. PROVIDE ALL EXTRA REINFORCEMENT AS SHOWN ON PLAN.
M. PROVIDE 3N16 TOP AND BOTTOM AT THE PERIMETER OF THE SLAB.
N. SLAB REINFORCEMENT LAYING SEQUENCE U.N.O.:

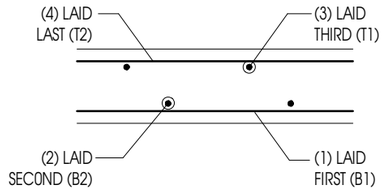

O. TYPICAL TRIMMERS AT PENETRATION/OPENING DETAIL:

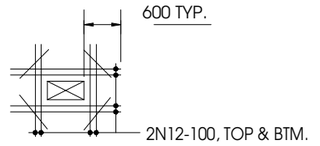

P. TYPICAL TRIMMERS AT RE-ENTRANT CORNERS:

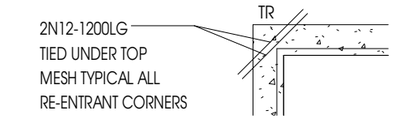

Q. PROVIDE TOP & BOTTOM BARS ON ALL WALL OPENINGS AS PER THE SCHEDULE BELOW:

LENGTH OF OPENING (m)	BOTTOM BAR	TOP BAR
1.0 - 1.8	2N16	2N16
1.8 - 2.5	2N20	2N20
2.5 - 3.5	2N24	2N24

R. PROVIDE ADEQUATE OVERLAP AT MESH JOINTS AS FOLLOWS :
- 400 MIN. LAP FOR SL82 MESH
- 500 MIN. LAP FOR SL92 MESH
- 600 MIN. LAP FOR SL102 MESH

S. PROVIDE ADEQUATE OVERLAP FOR BARS AS FOLLOWS:

BAR(X-Y)	MIN LAPPING REQUIRED
N12	500 mm
N16	800 mm
N20	1000 mm
N24	1200 mm
N28	1400 mm

MODULAR ENGINEERS P/L

Structural Engineering | Civil Engineering
Stormwater Engineering | Flood Engineering
Traffic Engineering | Temporary works

ABN : 66 646 960 929
TEL. : 02 873 08473
MOB. : 04 208 98999
EMAIL :
WEBSITE :
ADDRESS :

CLIENT:

PROJECT TITLE:
MULTI DWELLING

SHEET NAME:
ROOF TOP REINFORCEMENT PLAN

PROJECT NUMBER:
175-2026

INTERNAL REVISIONS:

ISSUE	DATE	DESCRIPTION	BY
E	10-09-26	ISSUED FOR CONSTRUCTION	D.A.
D	08-09-26	ISSUED FOR CONSTRUCTION	D.A.
C	24-08-26	ISSUED FOR PRELIMINARY	D.A.
B	21-08-26	ISSUED FOR PRELIMINARY	D.A.

AMENDMENTS

DRAWN : L.M. DATE: 17-07-26
DESIGNED : A.O. REVISION DATE:
QA CHECK : A.O. 10-09-26

APPROVED BY:

RPEQ: 28316
NPER: 5358554
DATE: 10-09-26

ISSUE TYPE:
CONSTRUCTION

SHEET NUMBER:
STR902

SHEET SIZE: **A3**
REVISION: **E**

PRINT IN COLOUR

SAMPLE PROJECT A - STRUCTURAL REV E - CURRENT - RECRUITMENT ASSESSMENT ONLY

TEST PROJECT ONLY

NOTE: THE DESIGN AND DETAILS SHOWN ON THESE DRAWINGS ARE APPLICABLE TO THIS PROJECT ONLY AND MAY NOT BE REPRODUCED IN WHOLE OR IN PART OR BE USED FOR ANY OTHER PROJECT OR PURPOSE WITHOUT THE WRITTEN PERMISSION OF WITH WHOM COPYRIGHT RESIDES.

REGULATED DESIGN RECORD

PROJECT ADDRESS:	
PROJECT TITLE:	MULTI DWELLING
CONSENT NO:	STR208 - 2023
BODY CORPORATE REG NO:	DEP0001320
DRAWING TITLE:	ROOF LOADING PLAN
DRAWING NO:	STR903

REV	DATE DD.MM.YY	DESCRIPTION	DP FULL NAME	REG NO
E	10-09-26	ISSUED FOR CONSTRUCTIO		




LOADING TABLE
WHERE APPLICABLE

MARK	COLOUR	AREA	SUPERIMPOSED DEAD LOAD	LIVE LOAD
1		RESIDENTIAL	1.5 kPa	1.5 kPa
2		PARKING	0.5 kPa EXC. FALLS AND GRADING	2.5 kPa
3		STORAGE	0.5 kPa	5.0 kPa
4		CORRIDOR / STAIR	1.5 kPa	4.0 kPa
5		LOBBY	1.5 kPa	4.0 kPa
6		BALCONY	1.5 kPa	2.0 kPa
7		MECH ROOM,FAN ROOM	1.5 kPa	5.0 kPa
8		COMMON AREA	1.5 kPa	4.0 kPa
9		LIGHT WEIGHT ROOF	0.5 kPa	0.5 kPa

LOADING TABLE
WHERE APPLICABLE

MARK	COLOUR	AREA	SUPERIMPOSED DEAD LOAD	LIVE LOAD
10		WASTE ROOM	0.5 kPa	5.0 kPa
11		RETAILS	1.5 kPa	4.0 kPa
12		ROOF (NON-TRAFFICABLE)	2.0 kPa	1.5 kPa
13		LANDSCAPE 400mm SOIL MAX.	4.0 kPa	1.5 kPa
14		LANDSCAPE 1000mm SOIL MAX.	10.0 kPa	1.5 kPa
15		SUBSTATION	1.0 kPa	2.0 kPa
16		LOADING DECK	1.0 kPa	10.0 kPa
17		PEBBLES	4.0 kPa	1.5 kPa
18		OSD TANK/ WATER STORAGE TANK	10.0 kPa FOR EVERY METRE HEIGHT OF WATER	

DEFLECTION NOTES (LONG-TERM)
- LONG-TERM DEFLECTION IS BASED ON DL + 0.3LL FOR SUSTAINED LOADS.
- CREEP FACTOR Λ = 2.0 TO 3.0 APPLIED PER AS3600.
- TOTAL DEFLECTION: Δ TOTAL=Δ IMMEDIATE + $\Lambda \times \Delta$ SUSTAINED
- IMMEDIATE DEFLECTION: DL + LL
- LONG-TERM DEFLECTION: DL + 0.3LL $\times \Lambda$

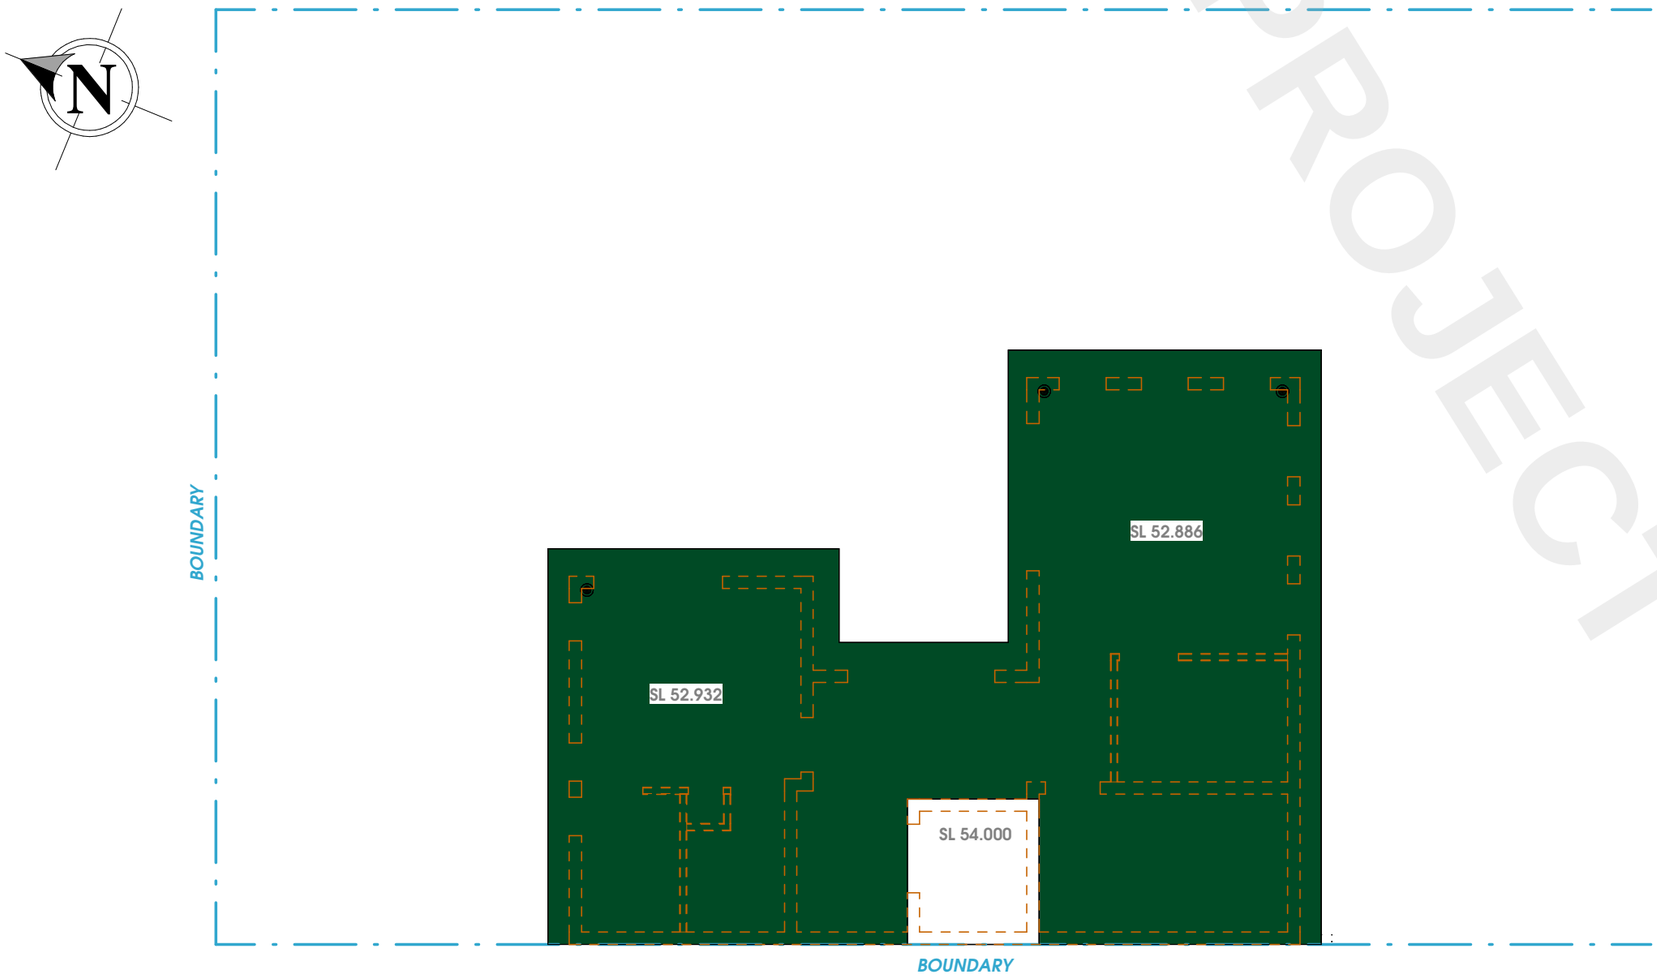

ROOF LOADING PLAN
SCALE: 1 : 100

PRINT IN COLOUR

MODULAR ENGINEERS P/L
Structural Engineering | Civil Engineering
Stormwater Engineering | Flood Engineering
Traffic Engineering | Temporary works
ABN : 66 646 960 929
TEL. : 02 873 08473
MOB. : 04 208 98999
EMAIL :
WEBSITE :
ADDRESS :

CLIENT:

PROJECT TITLE:
MULTI DWELLING

SHEET NAME:
ROOF LOADING PLAN

PROJECT NUMBER:
175-2026

INTERNAL REVISIONS:

ISSUE	DATE	DESCRIPTION	BY
E	10-09-26	ISSUED FOR CONSTRUCTION	D.A.
D	08-09-26	ISSUED FOR CONSTRUCTION	D.A.
C	24-08-26	ISSUED FOR PRELIMINARY	D.A.
B	21-08-26	ISSUED FOR PRELIMINARY	D.A.

AMENDMENTS

DRAWN : L.M. DATE: 17-07-26
DESIGNED : A.O. REVISION DATE:
QA CHECK : A.O. 10-09-26

APPROVED BY:

RPEQ: 28316
NPER: 5358554
DATE: 10-09-26

ISSUE TYPE:
CONSTRUCTION

SHEET NUMBER:
STR903

SHEET SIZE: **A3**
REVISION: **E**


SAMPLE PROJECT A - STRUCTURAL REV E - CURRENT - RECRUITMENT ASSESSMENT ONLY
TEST PROJECT USAGE

NOTE: THE DESIGN AND DETAILS SHOWN ON THESE DRAWINGS ARE APPLICABLE TO THIS PROJECT ONLY AND MAY NOT BE REPRODUCED IN WHOLE OR IN PART OR BE USED FOR ANY OTHER PROJECT OR PURPOSE WITHOUT THE WRITTEN PERMISSION OF WITH WHOM COPYRIGHT RESIDES.


REGULATED DESIGN RECORD

PROJECT ADDRESS:			
PROJECT TITLE:	MULTI DWELLING		
CONSENT NO:	STR208 - 2023	BODY CORPORATE REG NO:	DEP0001320
DRAWING TITLE:	SECTION AND DETAILS	DRAWING NO:	STR904

REV	DATE DD.MM.YY	DESCRIPTION	DP FULL NAME	REG NO
E	10-09-26	ISSUED FOR CONSTRUCTIO		

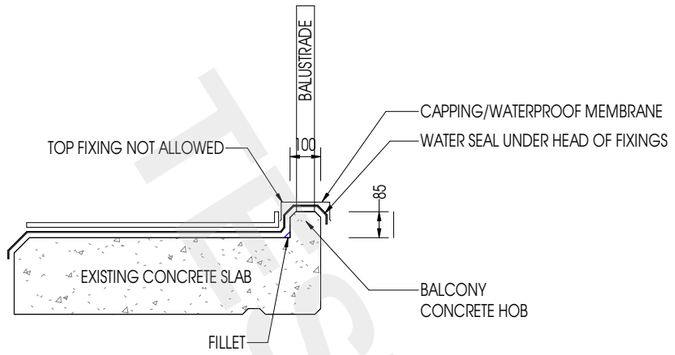


OPTION A

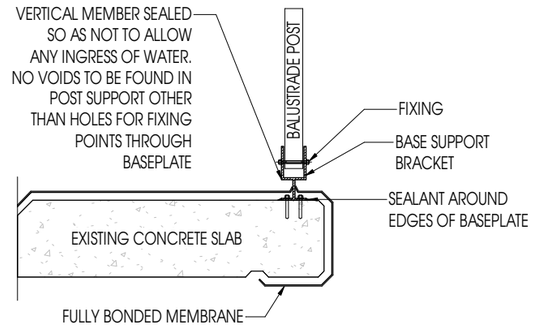


OPTION B

TYPICAL BALCONY EDGE DETAILS

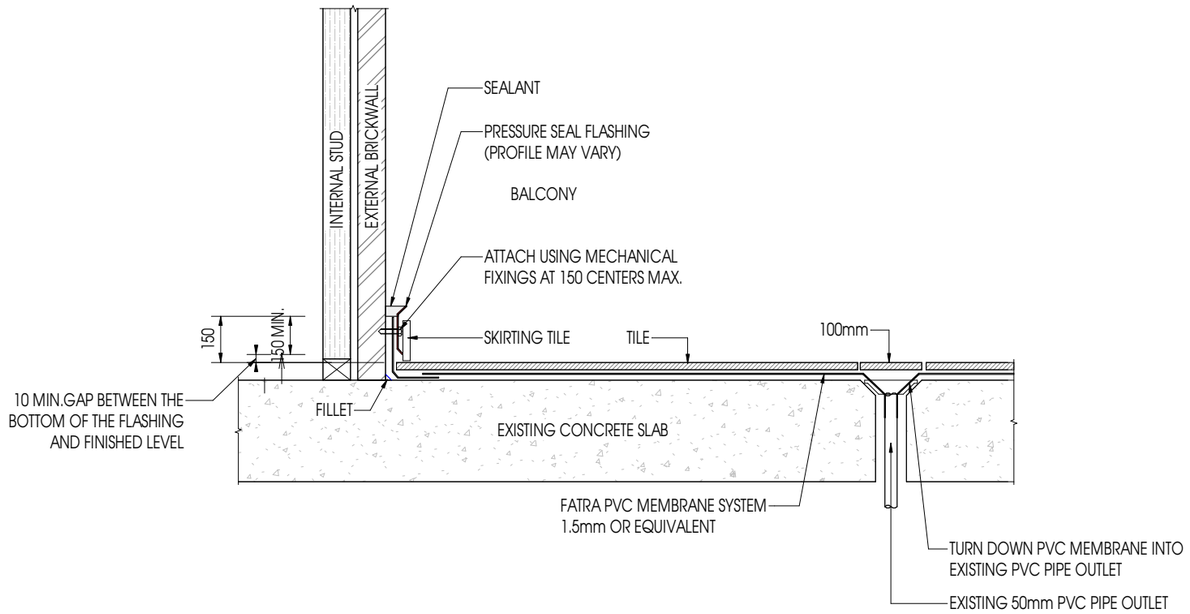

TYPICAL EXTERNAL BALCONY WATERPROOF DETAIL

PROCEDURE WORK:
- DEMOLISH AND REMOVE EXISTING TILES AND BED.
- RECTIFY THE GRADIENTS.
- REMOVE CAVITY BLOCKWORK.
- INSTALL CAVITY FLASHING.
- INSTALL BALCONY PVC MEMBRANE(DETAILS AS ABOVE).
- RE-TILE TO CORRECT GRADIENT.
- CARRY CAVITY FLASHING BETWEEN DOORS.

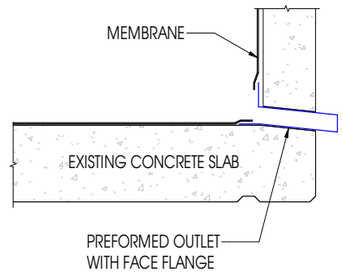

OUTLET SPITTER PIPE

EXTERNAL WATERPROOFING MEMBRANES - NCC:
EXTERNAL WATERPROOFING MEMBRANES TO BALCONIES, EXPOSED SLABS, SLAB EDGES, RAINWATER OUTLETS, POST PENETRATIONS AND SIMILAR EXTERNAL WATERPROOFED AREAS SHALL BE FATRA PVC MEMBRANE SYSTEM 1.5 MM, FATRA 810V, OR APPROVED EQUIVALENT PROPRIETARY WATERPROOFING MEMBRANE SYSTEM, INSTALLED STRICTLY IN ACCORDANCE WITH THE MANUFACTURER'S REQUIREMENTS AND AS 4654.2.
MEMBRANES SHALL BE TURNED UP AT WALLS/HOBS, DRESSED INTO OUTLETS, SEALED AROUND PENETRATIONS, AND TURNED OVER SLAB EDGES. AT EXPOSED SLAB EDGES, MEMBRANE SHALL BE TERMINATED WITH A DRIP GROOVE OR APPROVED EQUIVALENT EDGE TERMINATION DETAIL TO PREVENT WATER TRACKING BACK UNDER THE SLAB EDGE. ALL OUTLETS, POSTS, COLLARS, FLANGES, WELDS, SEALANTS, TERMINATIONS AND PENETRATIONS SHALL BE COMPATIBLE WITH THE SELECTED WATERPROOFING SYSTEM AND INSTALLED BY AN APPROVED WATERPROOFING CONTRACTOR.
REFER TO TYPICAL BALCONY WATERPROOFING, RAINWATER OUTLET, POST PENETRATION AND MEMBRANE TERMINATION DETAILS ON THIS DRAWING.

PRINT IN COLOUR

NOTE: THE DESIGN AND DETAILS SHOWN ON THESE DRAWINGS ARE APPLICABLE TO THIS PROJECT ONLY AND MAY NOT BE REPRODUCED IN WHOLE OR IN PART OR BE USED FOR ANY OTHER PROJECT OR PURPOSE WITHOUT THE WRITTEN PERMISSION OF WITH WHOM COPYRIGHT RESIDES.

MODULAR ENGINEERS P/L
Structural Engineering | Civil Engineering
Stormwater Engineering | Flood Engineering
Traffic Engineering | Temporary works
ABN : 66 646 960 929
TEL. : 02 873 08473
MOB. : 04 208 98999
EMAIL :
WEBSITE :
ADDRESS :

CLIENT:

PROJECT TITLE:
MULTI DWELLING

SHEET NAME:
SECTION AND DETAILS

PROJECT NUMBER:
175-2026

INTERNAL REVISIONS:

ISSUE	DATE	DESCRIPTION	BY
E	10-09-26	ISSUED FOR CONSTRUCTION	D.A.
D	08-09-26	ISSUED FOR CONSTRUCTION	D.A.
C	24-08-26	ISSUED FOR PRELIMINARY	D.A.
B	21-08-26	ISSUED FOR PRELIMINARY	D.A.

AMENDMENTS

DRAWN : L.M. DATE: 17-07-26
DESIGNED : A.O. REVISION DATE:
QA CHECK : A.O. 10-09-26

APPROVED BY:

RPEQ: 28316
NPER: 5358554
DATE: 10-09-26

ISSUE TYPE:
CONSTRUCTION

SHEET NUMBER:
STR904

SHEET SIZE: A3
REVISION: E

SAMPLE PROJECT A - STRUCTURAL REVE - CURRENT - RECRUITMENT ASSESSMENT ONLY
TESTPROJECT


TYPICAL WATERPROOFING DETAILS

REGULATED DESIGN RECORD

PROJECT ADDRESS:			
PROJECT TITLE:	MULTI DWELLING		
CONSENT NO:	STR208 - 2023	BODY CORPORATE REG NO:	DEP0001320
DRAWING TITLE:	SECTION AND DETAILS	DRAWING NO:	STR905

REV	DATE DD.MM.YY	DESCRIPTION	DP FULL NAME	REG NO
E	10-09-26	ISSUED FOR CONSTRUCTIO		

FALLS:
THE FALL CAN BE FORMED IN THE STRUCTURAL SUBSTRATE OR FORMED BY A SCREED OVER THE STRUCTURAL SUBSTRATE, WHICH MUST NOT BE LESS THAN 1 IN 100 (10MM PER 1M). FALLS IN FINISHES MUST ENSURE WATER DRAINS TO THE DRAINAGE OUTLET, WITH NO WATER RETENTION ON THE FINISHED SURFACE.

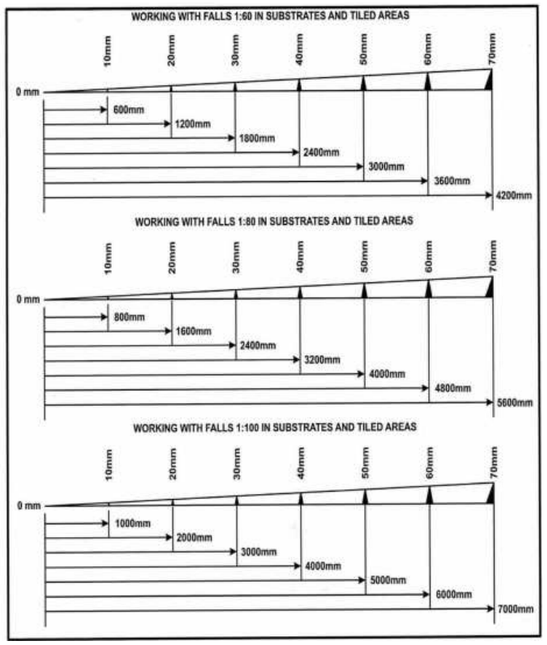

NOT TO SCALE

LAYING MEMBRANES
JUNCTIONS, LAP JOINTS, SEAMS AND COLD JOINTS:
LIQUID APPLIED MEMBRANES USUALLY DON'T HAVE A MANUFACTURER'S DESCRIPTION COVERING THESE ISSUES RELATING TO THE WEAK POINTS IN 'SHEET' SYSTEMS. HOWEVER, SHOULD THE LIQUID APPLIED SYSTEM INCORPORATE REINFORCING FABRIC A LAP JOINT, USUALLY A MIN OF 40MM IS APPLICABLE.
CURING:
ALL COMPONENTS OF THE MEMBRANE SYSTEM MUST BE CURED BEFORE CONSIDERED 'FIT FOR PURPOSE'.
CONSIDERATIONS FOR LIQUID APPLIED MEMBRANE SYSTEMS ARE:
· LOW TEMPERATURES, WET FILM THICKNESS, RELATIVE HUMIDITY, SOLIDS CONTENT AND AIR MOVEMENT CAN DELAY CURING.
· NO FURTHER WORK SHOULD BE COMMENCED UNTIL THE MEMBRANE IS CURED
· PREMATURE COVERING OF THE MEMBRANE MAY PREVENT CURING AND LEAD TO DEGRADATION.
· INTERVALS BETWEEN APPLIED MEMBRANE COATINGS SHOULD TAKE INTO ACCOUNT THE NECESSARY CURING TIMES.
FILLETS
WHEN A MEMBRANE CHANGES FROM HORIZONTAL TO VERTICAL PLANE IT REQUIRES A 'BOND BREAKER' APPLICATION.


MEMBRANE CLASS	ELONGATION AT BREAK	MIN. BOND BREAKER/TAPE WIDTH TO BRIDGE JOINTS OPENING UP BY 5mm
II	60% TO 300%	35 mm
III	>300%	12 mm

TERMINATION OF MEMBRANES
UPWARD TERMINATIONS:
HEIGHT:
THE MEMBRANE TERMINATION IS CREATED TO PREVENT WATER ENTRY, THE FINISHED HEIGHT OF THE MEMBRANE SHOULD CATER FOR THE SURFACE COVERAGE HEIGHT TO PREVENT WATER, INCLUDING WIND DRIVEN, FROM FLOWING OVER THE TOP OF THE MEMBRANE. IN WIND CLASS N1 THE TERMINATION HEIGHT MUST BE NOT LESS THAN 40MM.


MEMBRANE TERMINATION FINISHING:
THE STANDARD IS MOSTLY CONCERNED WITH SHEET MEMBRANES RELATING TO OVER-FLASHING OR COVERFLASHING, HOWEVER SOME POINTS RELATE TO LIQUID APPLIED:-

TERMINATION OF A PRESSURE SEAL FLASHING:
· PRESSURE SEAL FLASHING TO BE ATTACHED USING MECHANICAL FIXINGS AT A MAXIMUM OF 150MM CENTERS. THE LAP FROM THE BOTTOM EDGE OF THE MECHANICAL FIXING, TO THE BOTTOM EDGE OF THE PRESSURE SEAL FLASHING SHALL BE A MINIMUM OF 15MM.
· SEALANT TO ENCAPSULATE THE PRESSURE SEAL FLASHING TO THE WEATHERPROOF WALL
· THERE IS TO BE A MINIMUM OF 10MM GAP BETWEEN THE BOTTOM OF THE FLASHING AND THE FINISHED LEVEL.

TERMINATION OF OVERFLASHING:
· THE OVERFLASHING IS TO BE ATTACHED INTO THE WATERPROOF WALL VIA A RIGULET OF MINIMUM 15MM AND FIXED IN PLACE, INCLUSIVE OF SEALANT
· THE LAP FROM THE TOP EDGE OF THE SEALED RIGULET TO THE BOTTOM OF THE MEMBRANE IS A MINIMUM OF 75MM
· THE GAP BETWEEN THE BOTTOM OF THE FLASHING AND THE FINISHED LEVEL MUST BE A MINIMUM OF 10MM

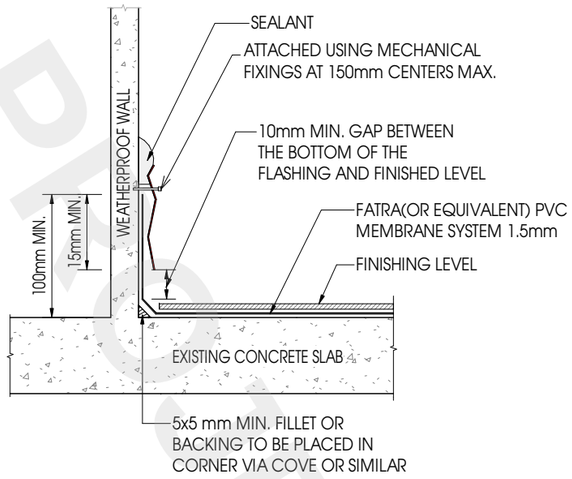

TYPICAL VERTICAL UPWARD TERMINATION- DETAIL OF PRESSURE SEAL

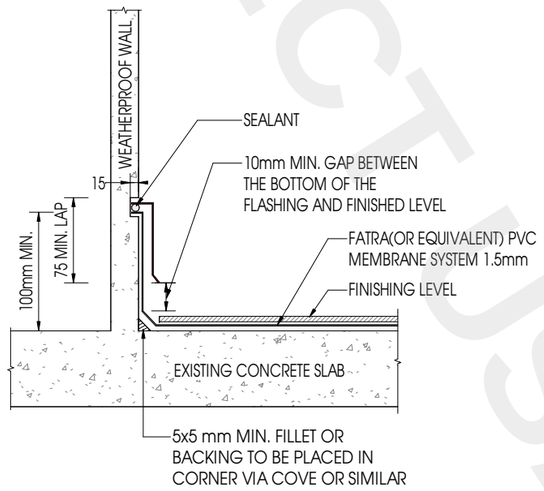

TYPICAL VERTICAL UPWARD TERMINATION- DETAIL OF OVERFLASHING

TO COMPLY WITH AS 4654.2 AND MANUFACTURER'S REQUIREMENTS.

PRINT IN COLOUR

MODULAR ENGINEERS P/L
Structural Engineering | Civil Engineering
Stormwater Engineering | Flood Engineering
Traffic Engineering | Temporary works
ABN : 66 646 960 929
TEL. : 02 873 08473
MOB. : 04 208 98999
EMAIL :
WEBSITE :
ADDRESS :

CLIENT:

PROJECT TITLE:
MULTI DWELLING

SHEET NAME:
SECTION AND DETAILS

PROJECT NUMBER:
175-2026

INTERNAL REVISIONS:

ISSUE	DATE	DESCRIPTION	BY
E	10-09-26	ISSUED FOR CONSTRUCTION	D.A.
D	08-09-26	ISSUED FOR CONSTRUCTION	D.A.
C	24-08-26	ISSUED FOR PRELIMINARY	D.A.
B	21-08-26	ISSUED FOR PRELIMINARY	D.A.

AMENDMENTS

DRAWN : L.M. DATE: 17-07-26
DESIGNED : A.O. REVISION DATE:
QA CHECK : A.O. 10-09-26
APPROVED BY:

RPEQ: 28316
NPER: 5358554
DATE: 10-09-26

ISSUE TYPE:
CONSTRUCTION

SHEET NUMBER:
STR905

SHEET SIZE: **A3** REVISION: **E**

SAMPLE PROJECT A - STRUCTURAL REV E - CURRENT - RECRUITMENT ASSESSMENT ONLY
TEST PROJECT NOT FOR USE

NOTE: THE DESIGN AND DETAILS SHOWN ON THESE DRAWINGS ARE APPLICABLE TO THIS PROJECT ONLY AND MAY NOT BE REPRODUCED IN WHOLE OR IN PART OR BE USED FOR ANY OTHER PROJECT OR PURPOSE WITHOUT THE WRITTEN PERMISSION OF WITH WHOM COPYRIGHT RESIDES.